

Прихожая. Коллаж-концепция



Плинтус скрытый из напольного керамогранита



Холл. Коллаж-концепция

св-ники Китай
или
световой
натяжной потолок

Двери межкомнатные
ACADEMY
Slim Soft Touch
высота полотна - 2200

кварцвинил
или
инженерная доска

панели полистирол
Decor Dizayn DD901
150x10x2000

поручень настенный
из дерева
с подсветкой

стекло



Плинтус скрытый из
напольного керамогранита

дверь скрытая
ABS кромка

потолок ГКЛ,
св-ник гипсовый
встраиваемый
ARTPOLE SGS26

встраиваемый
гипсовый св-ник
Stellanova SUBRA-E



светильник
подвесной
Китай

подсветка
по
периметру

потолок ГКЛ
в цвет стен

покраска

ВОДОПАД ПО СТЕКЛУ

Снизу - база
под насос,
камни и искусств.
растения

Сверху
(за рельефным
карнизом)
выпуск воды



мебельная
конструкция
с дверью
в тех. помещение

отверстие
для кошки

первая ступень
- подиум,
покрытие -
микроцемент

керамогранит ИТАЛОН
Сильвер Натуральный
900x1800

Кухня-гостиная. Коллаж-концепция



накладной светильник
в стиле трековых
Maytoni Basis Rot

шкаф-витрина
для Lego

декорат.краска
ASTI velato

подсветка
закарнизная
вдоль ступени

панели под камень
из полиуретана, Китай,

встраиваемый
магнитный
шинопровод
MAYTONI

опуск потолка
ГКЛ
цвет белый

потолок-
штукатурка,
декорат.краска
ASTI velato

декорат.краска
ASTI velato

потолок ГКЛ,
св-ники гипсовые встраиваемые
ARTPOLE SGS37



св-ник подвесной
Китай

св-ник - бра Затмение

св-ник подвесной
Китай



декорат.краска
ASTI velato

покраска - белый

мебельная конструкция
стеллажей


тумба, встроенная
в нишу в подиуме

керамогранит ИТАЛОН
Сильвер Натуральный
900x1800

декорат.краска
ASTI velato

керамогранит 120x60
Zodiac Civic Lm

Плинтус скрытый
из напольного керамогранита

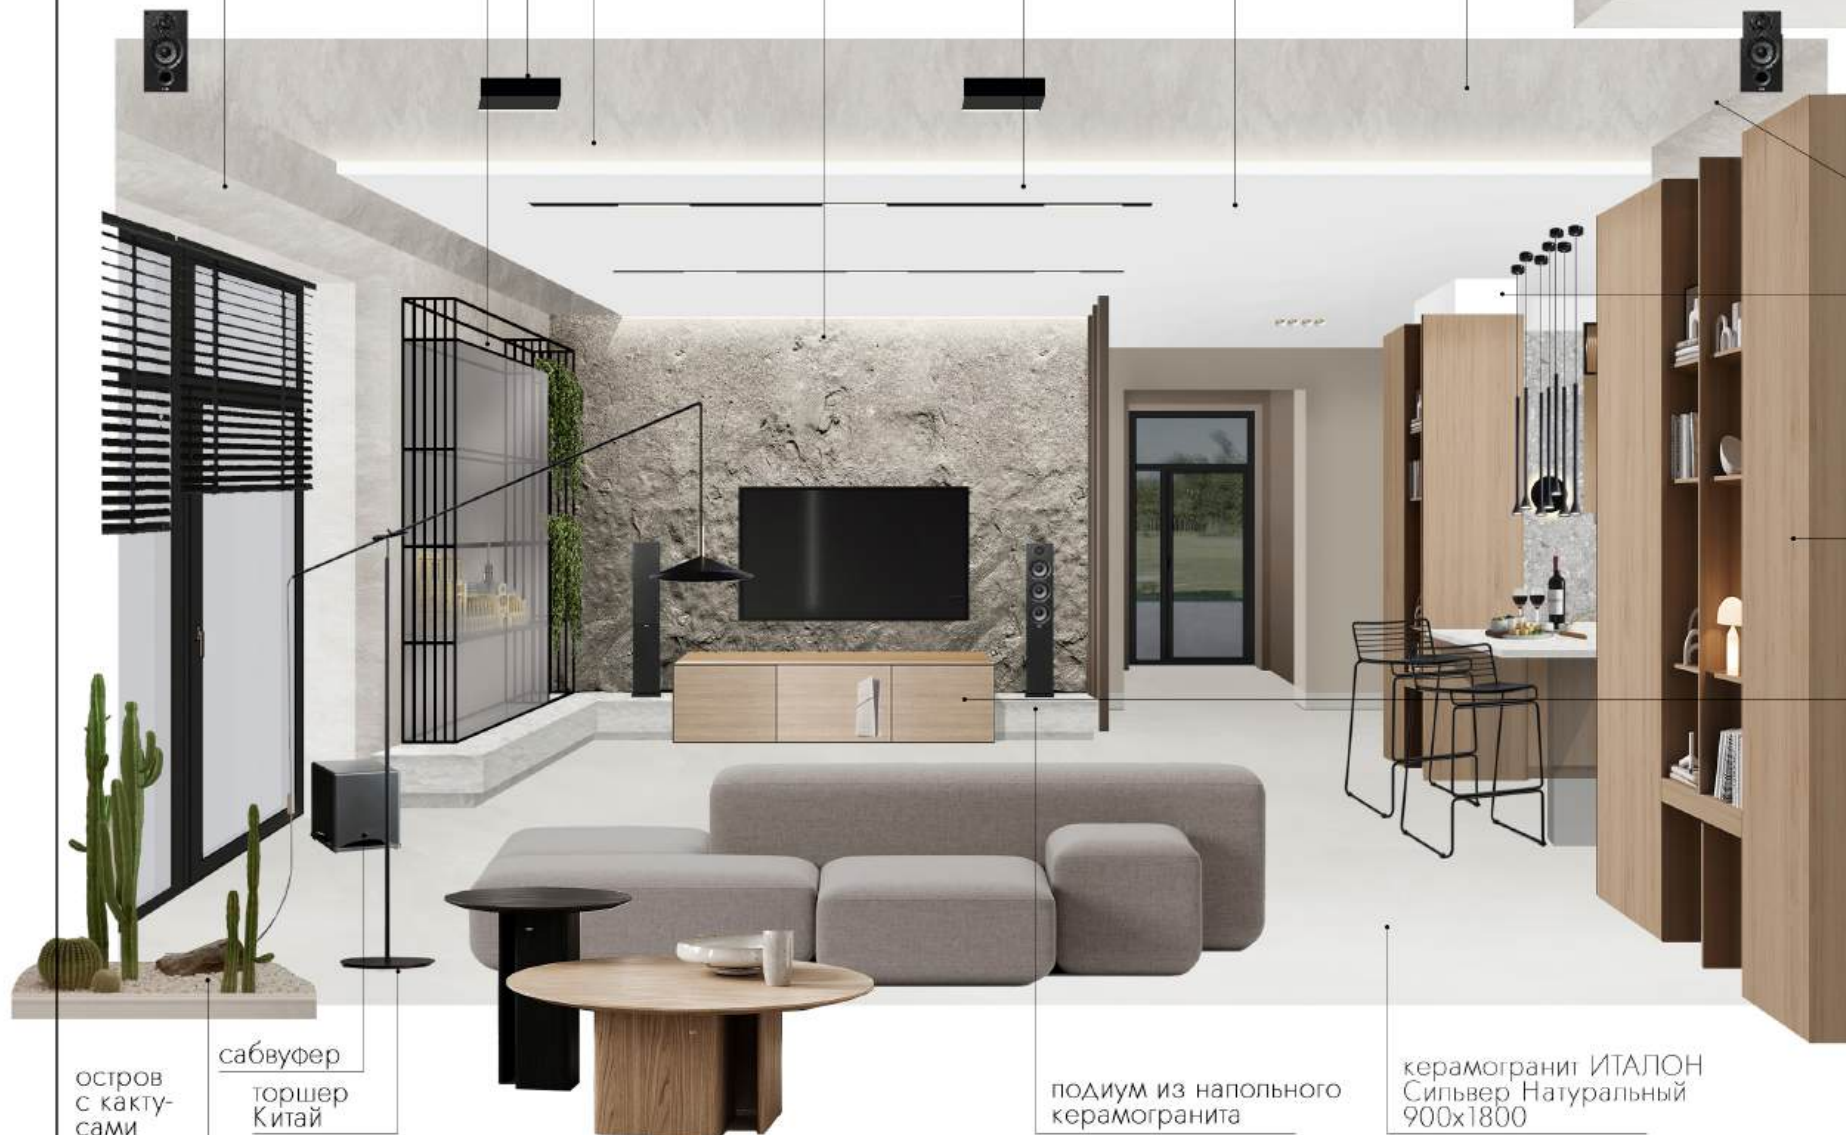


остров
с какту-
сами

сабвуфер
торшер
Китай

подиум из напольного
керамогранита

керамогранит ИТАЛОН
Сильвер Натуральный
900x1800

Гостевая 1 эт. Коллаж-концепция

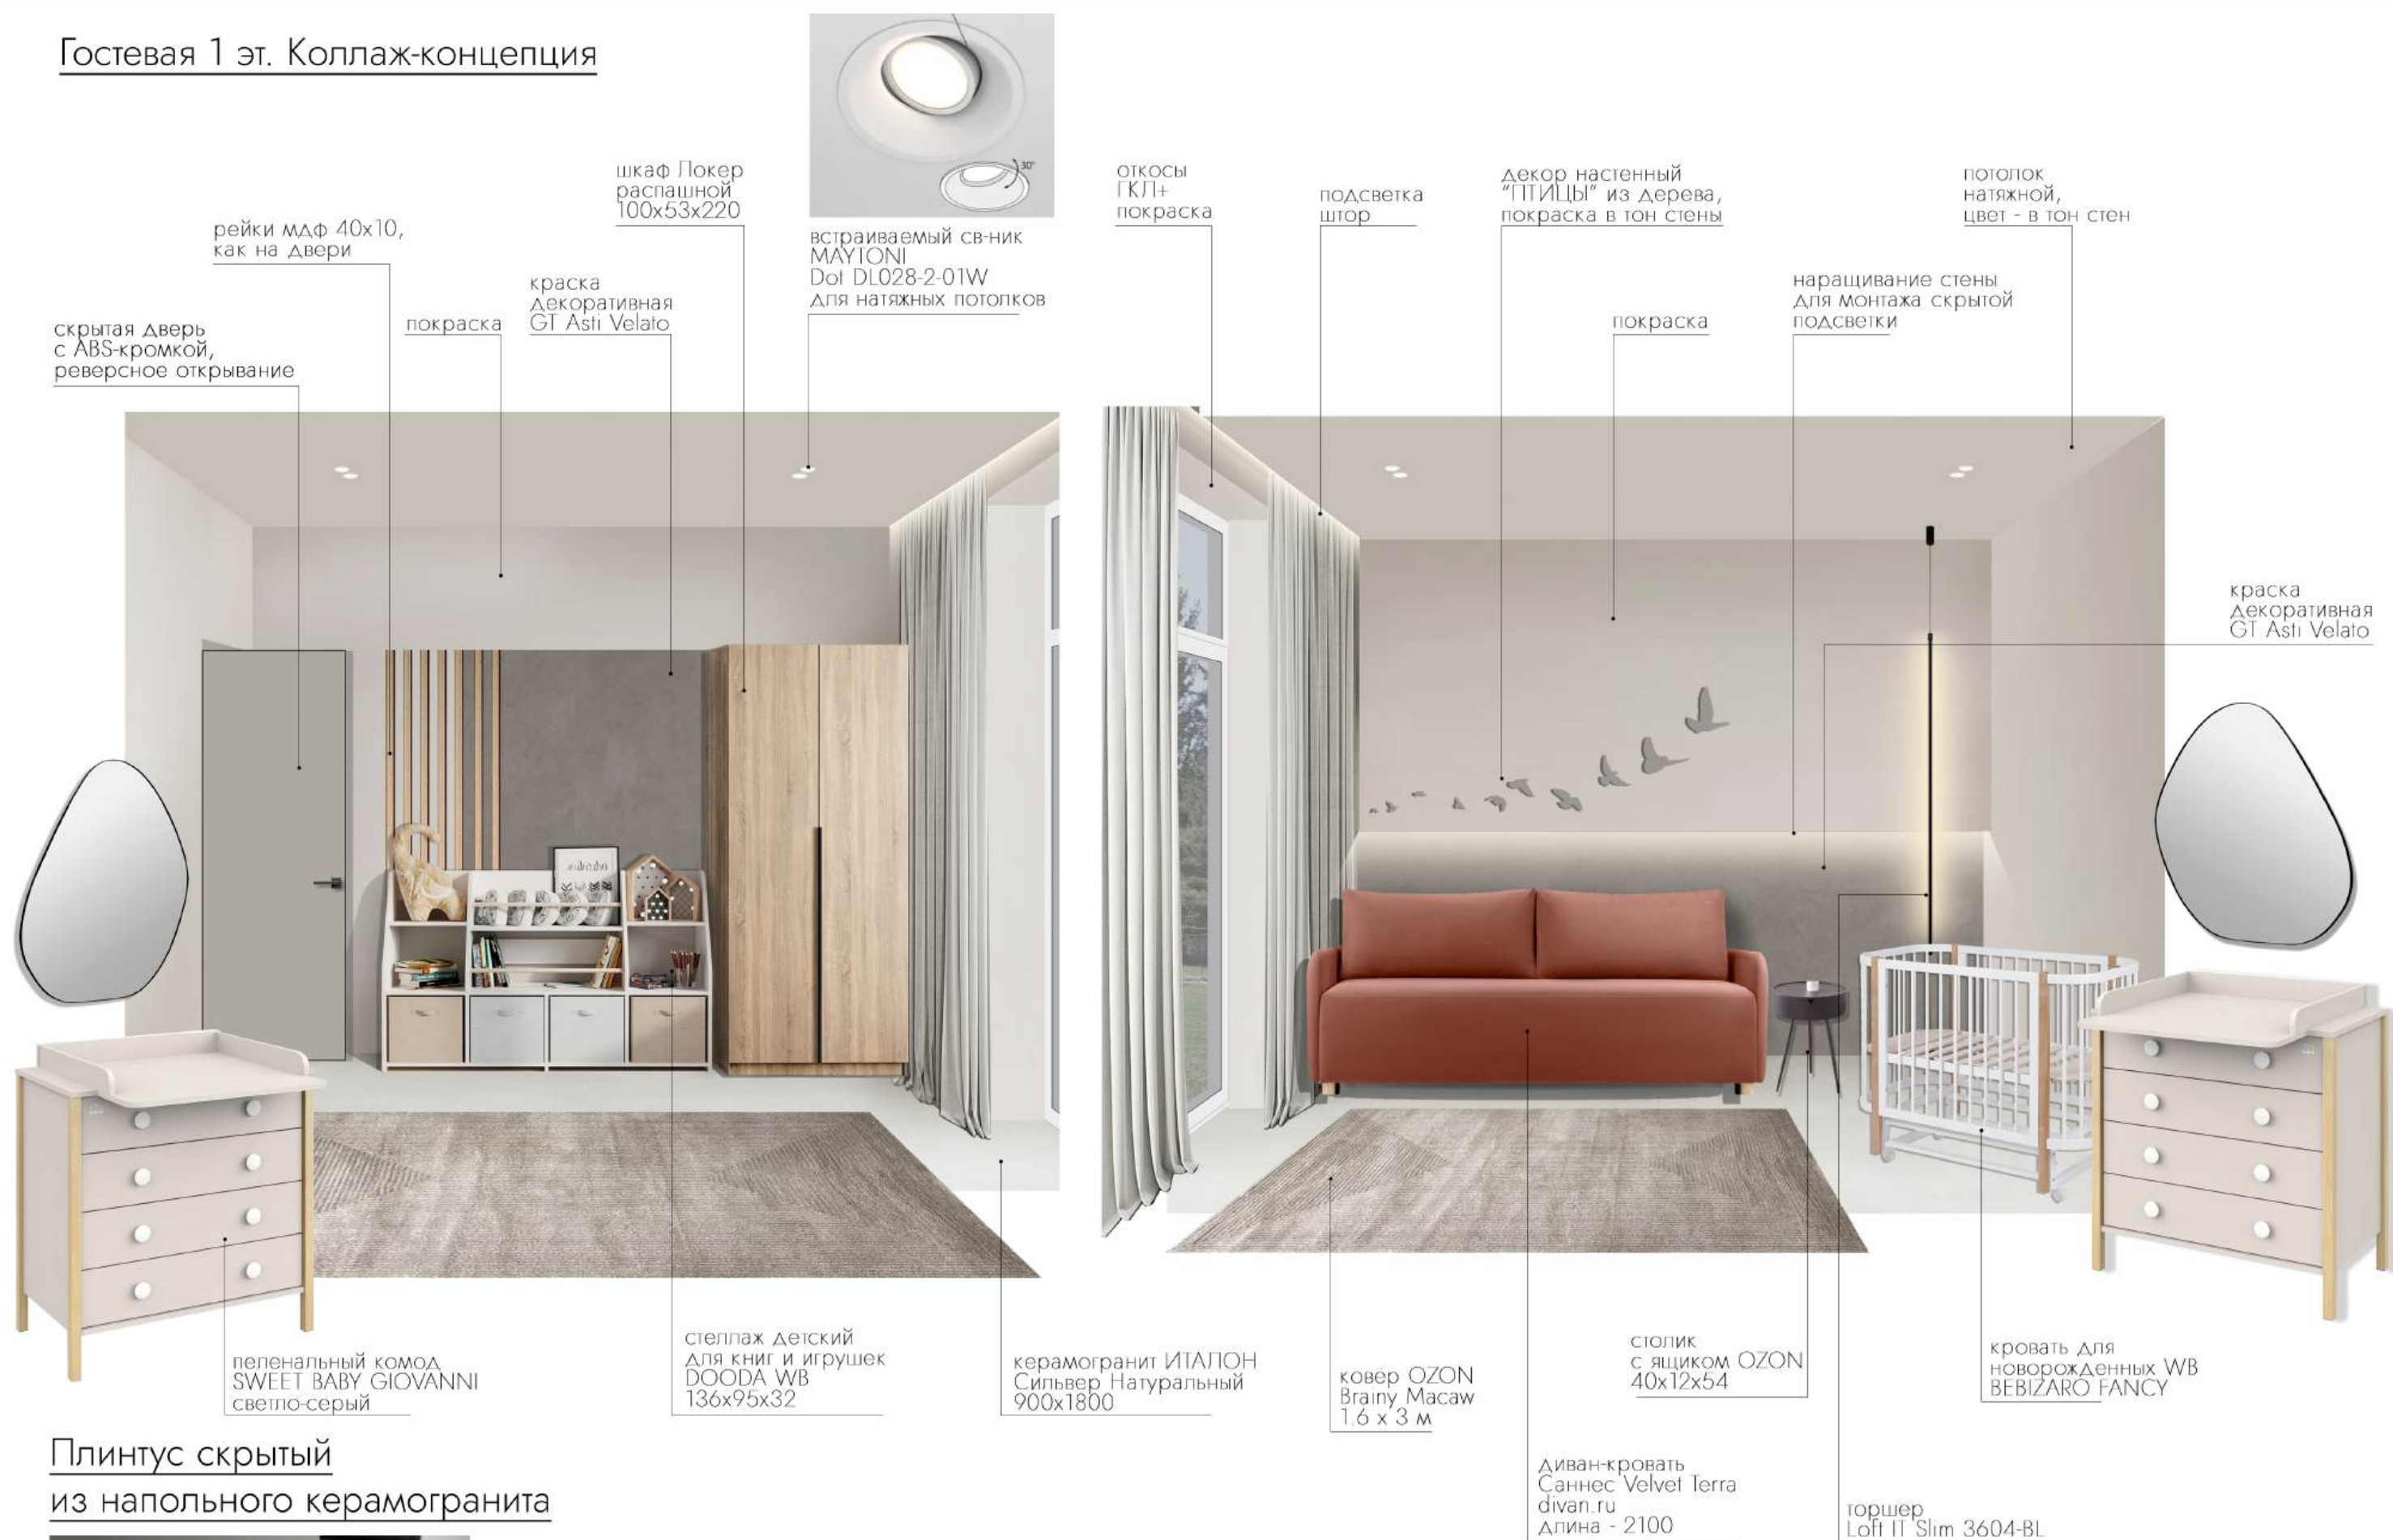

Санузел 1 эт. Коллаж-концепция

потолок натяжной
в тон плитке

закарнизная подсветка
по периметру

керамогранит 600x1200
Simpolo гладкий

полотенцесушитель
(электрический?)

зеркало с подсветкой

встраиваемый смеситель
для раковины

подвесная тумба

подвесной унитаз
с инсталляцией,
гигиенический душ

керамогранит ИТАЛОН
Сильвер Натуральный
900x1800

встраиваемый св-ник
MAYTONI
Dot DL028-2-01W
Для натяжных потолков



керамогранит 600x1200
Simpolo рельеф

душевая система никель
накладная

полка навесная металл
OZON

керамогранит 600x1200
Simpolo рельеф

керамогранит 600x1200
Simpolo гладкий

керамогранит ИТАЛОН
Сильвер Натуральный
900x1800



Гостевая 2 эт. Коллаж-концепция



встраиваемый св-ник
MAYTONI
Dot DL028-2-01W
Для натяжных потолков

зеркало на заказ
с подсветкой снизу

покраска в цвет шкафа

покраска

откосы
ГКЛ+
покраска

подсветка
штор

покраска
в цвет
шкафа

наращивание стены
для монтажа скрытой
подсветки

подвесные
св-ники
Китай

потолок
натяжной,
цвет - белый

покраска

декор.
краска
Asti Velato

бра Китай

Прикроватная
тумба консоль
"Пестер"
543x407x216

кварцвинил
или инженерная доска

МФ Агат двухспальная кровать,
с подъемным механизмом RIMINI,
180x200 см

Стул REYNAUX 1

Двери межкомнатные
ACADEMY
Slim Soft Touch
высота полотна - 2200


Плинтус скрытый




шкаф распашной
Квелен-2 Terra
96x55x220



Санузел 3 эт. Коллаж-концепция

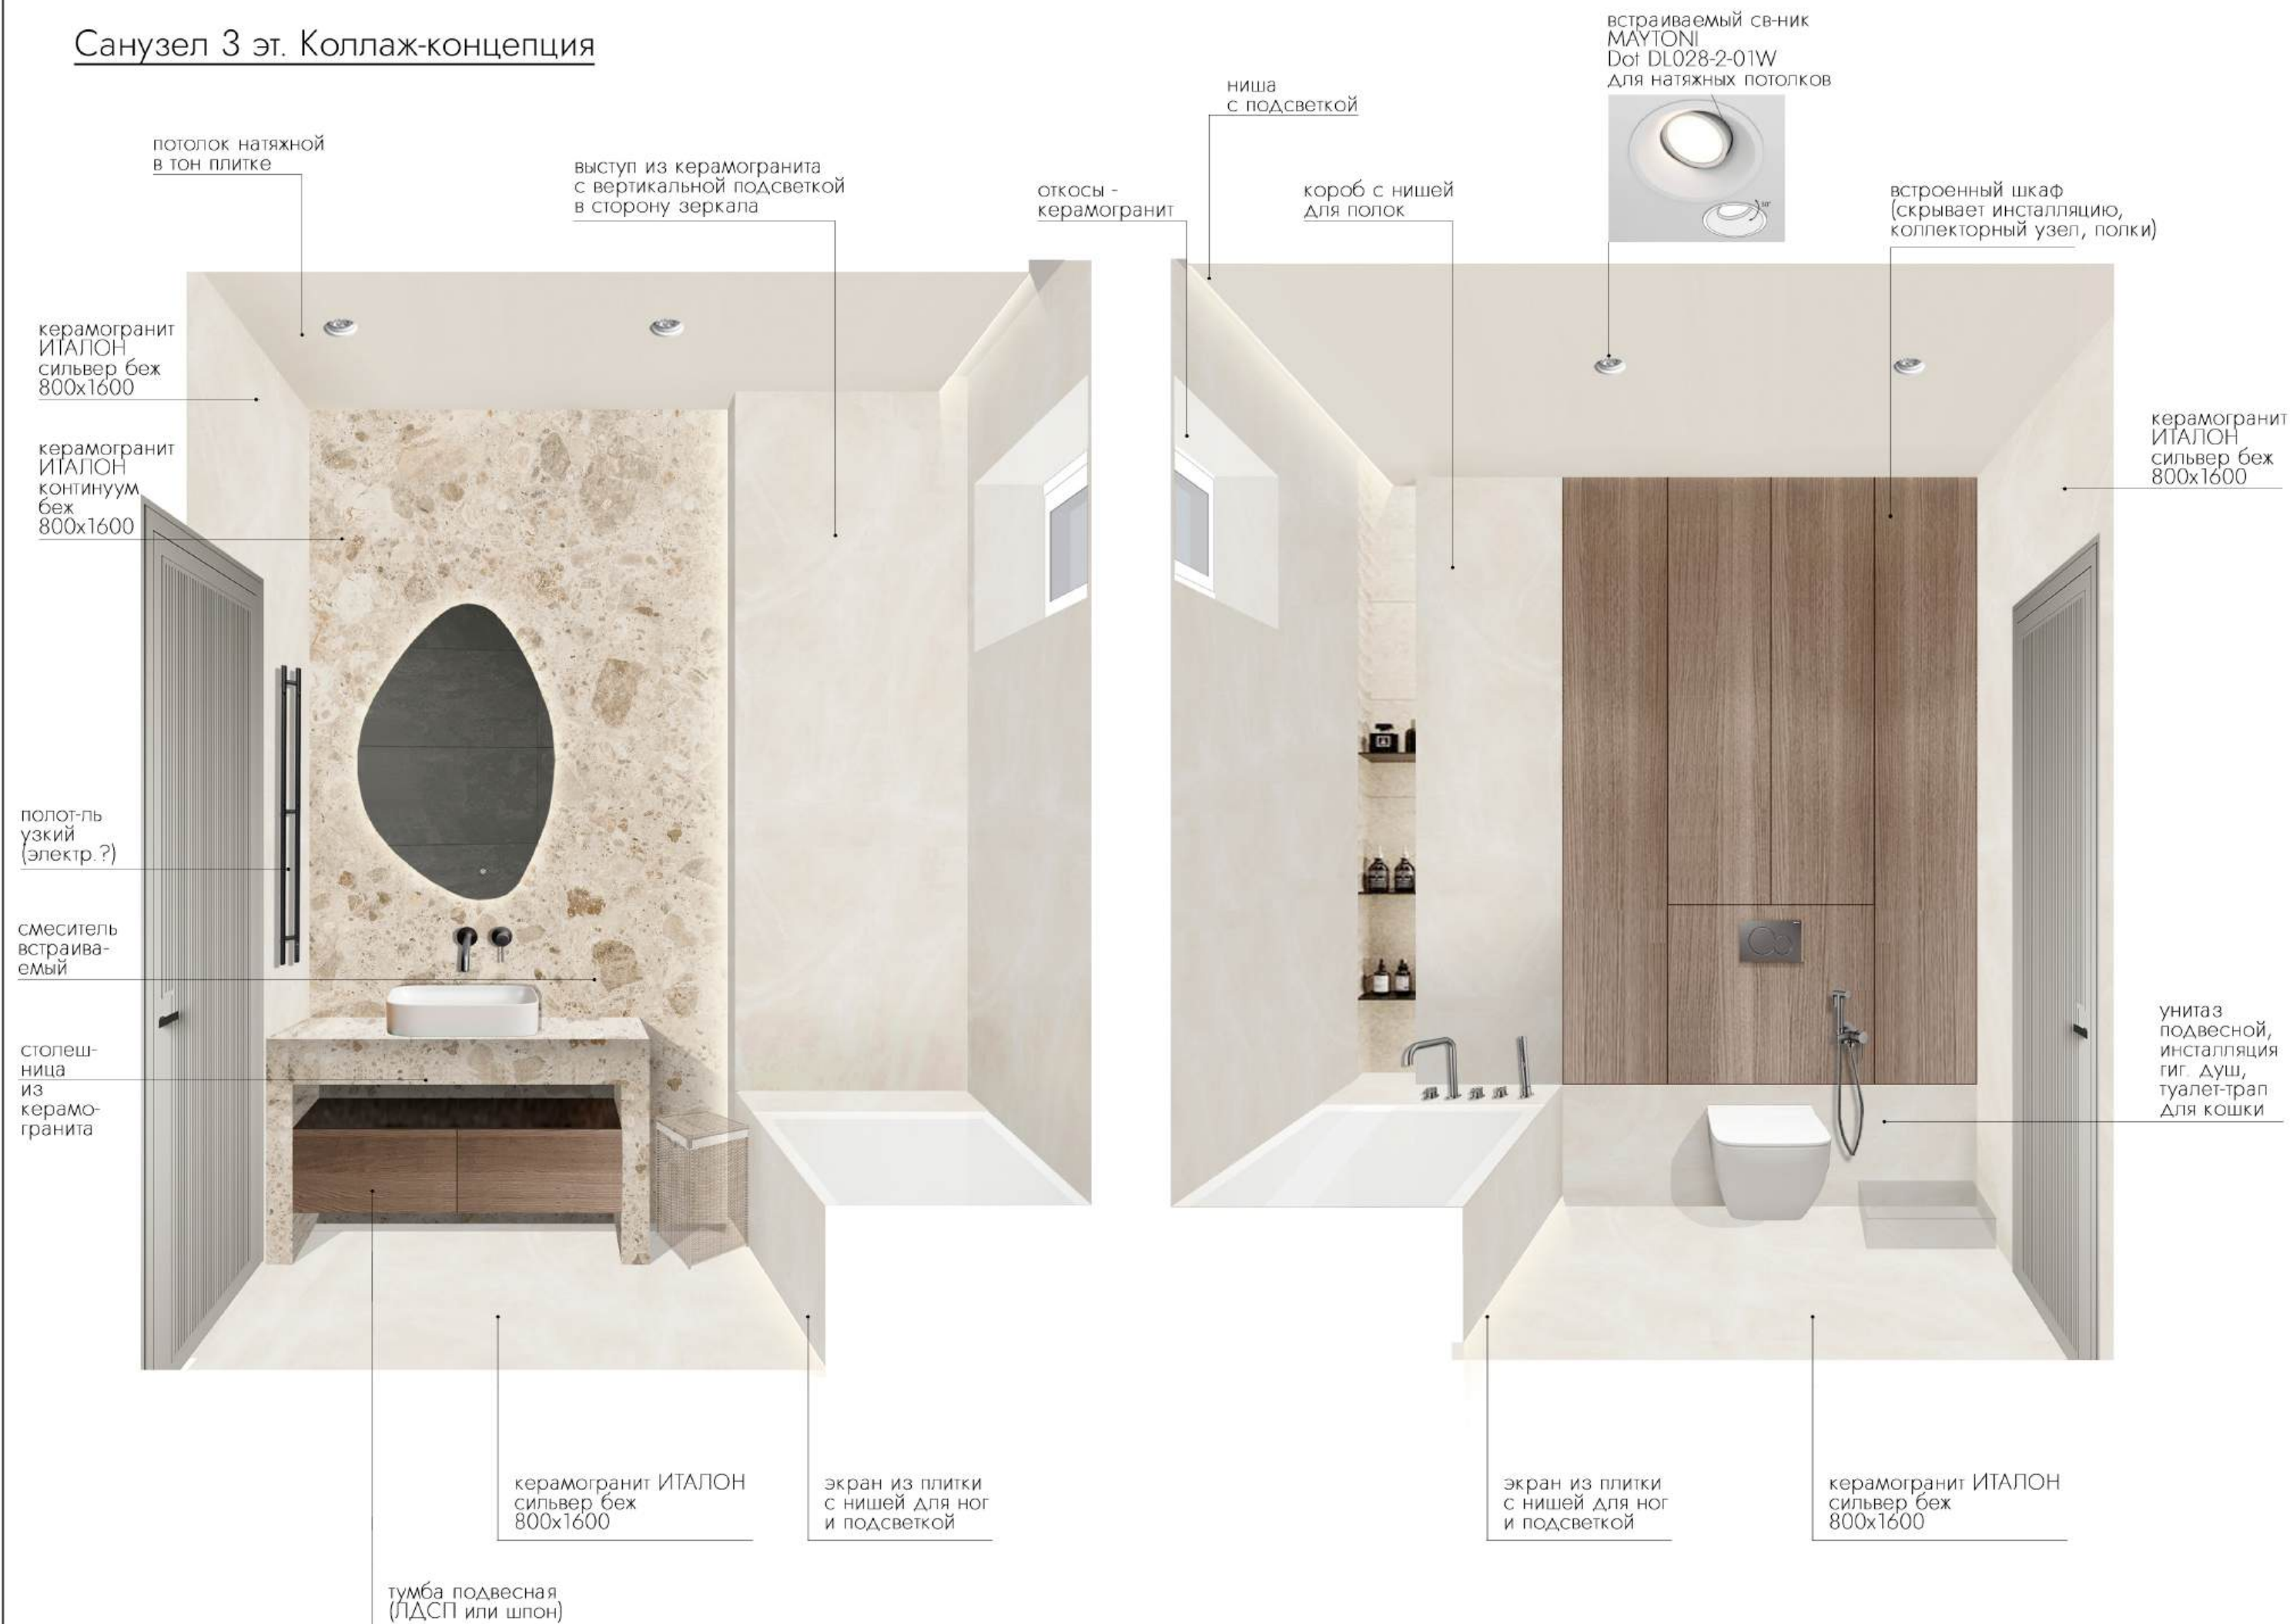

Кабинет. Коллаж-концепция

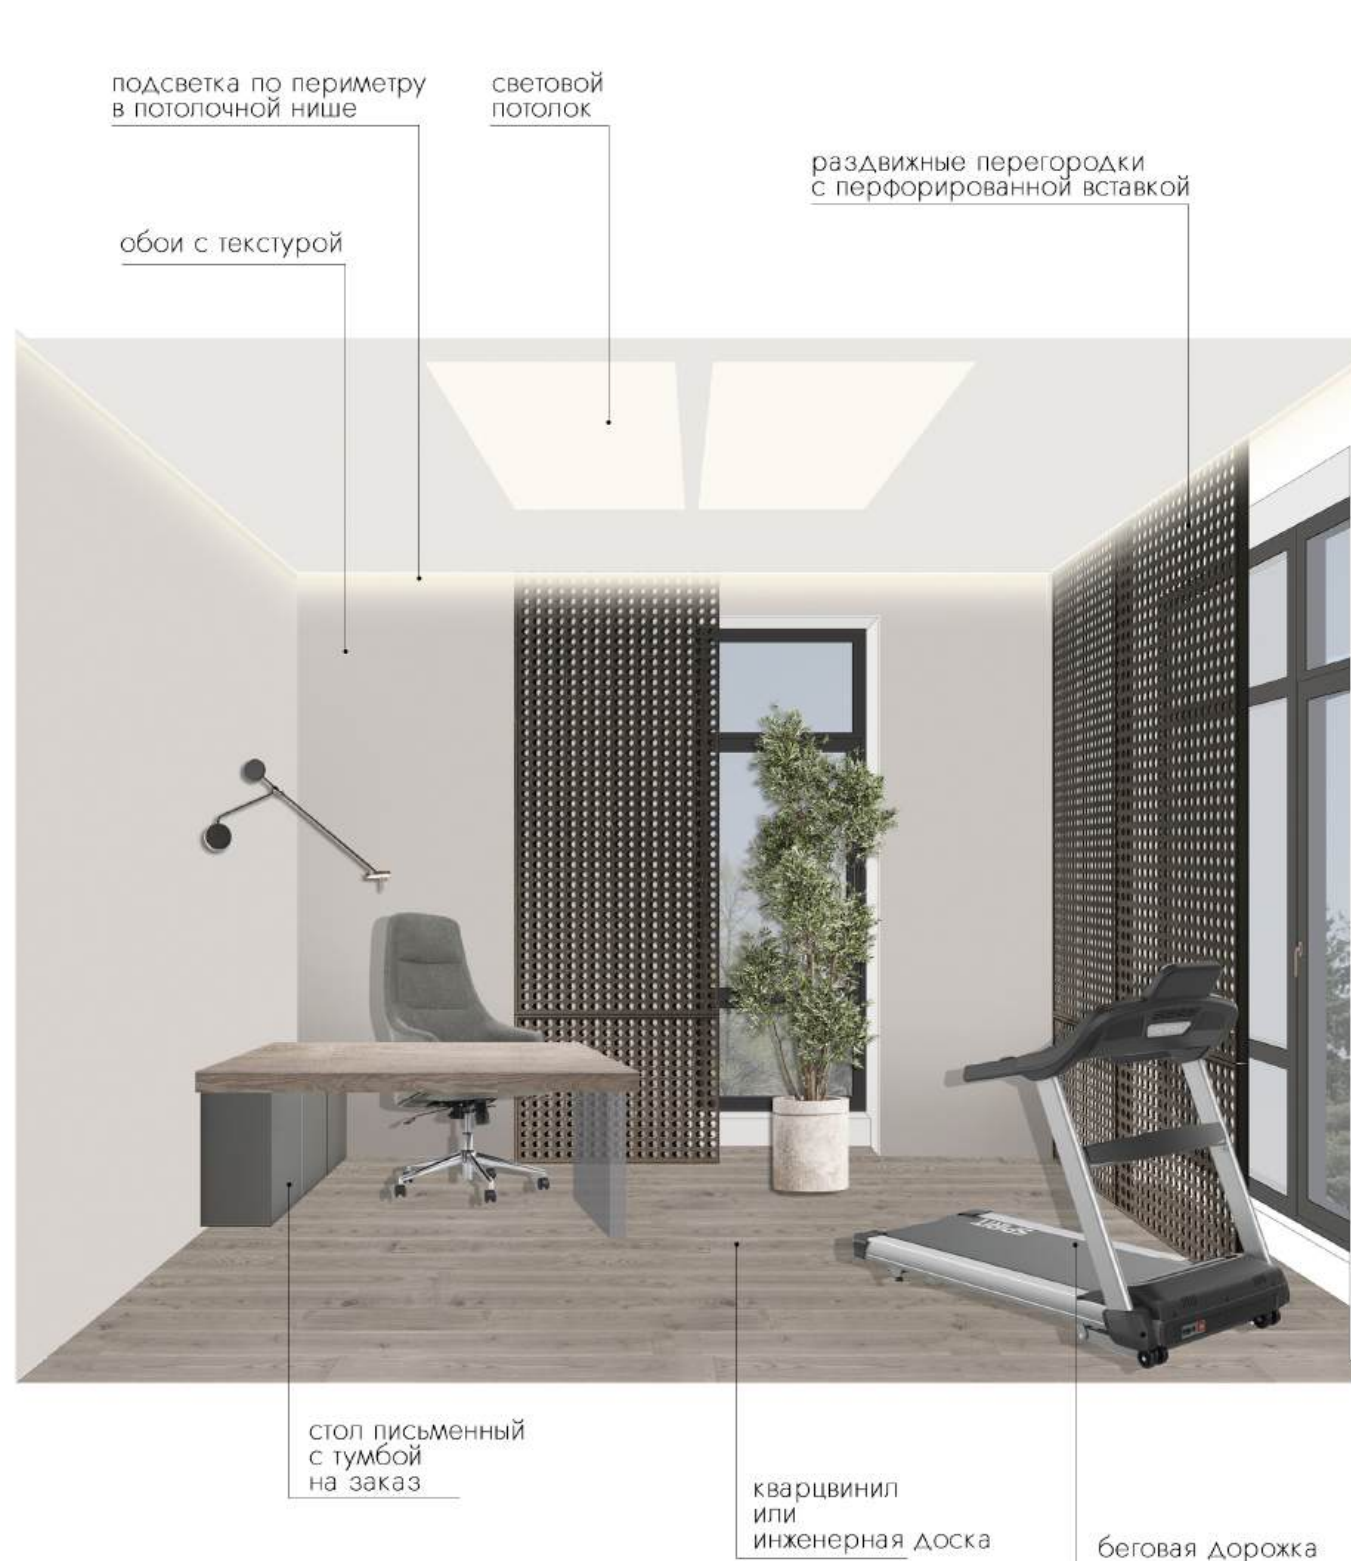

Плинтус скрытый



Детская. Коллаж-концепция

потолок ГКЛ,
св-ники гипсовые
встраиваемые
ARTPOLE SGS37



покраска

Двери межкомнатные
ACADEMY
Slim Soft Touch
высота полотна - 2200

пробковые панели
на клей

игровая
на втором ярусе:
сетка по деревянному
каркасу

стеллаж Лесли
Plywood White
91x41x202

покраска

закарнизная
подсветка

светильники
Китай



флизелиновые фотообои
на стену Dekor Vinyl
"Таинственный лес в тумане"
400x270 см. OZON

Кровать двухъярусная
CARVER 1 733263

бра
на каждом уровне

тумба прикроватная
Вита

панели мебельные
с перфорацией
для полок

Письменный стол
Лесли Plywood White

стул Слинг
вращающийся

шкаф трехсекционный HOFF
Fun 134.4x190x51.6 см

кварцвинил
или
инженерная доска



Плинтус скрытый



Спальня. Коллаж-концепция

отделка стены
тонируемыми
досками и рейками



потолок ГКЛ,
св-ники гипсовые
встраиваемые
ARTPOLE SGS37



покраска

потолок
декоративная
краска (или шт-ка)

декоративная
краска (или шт-ка)

подвесная конструкция
металлокаркас, ГКЛ,
отделка панелями
из полиуретана под камень

отделка откоса
досками со стены

покраска откоса

потолок ГКЛ
в цвет стен

покраска

навесные кашпо
с растениями

зеркало
тонируемое

бра

закарнизная
подсветка



Электрокамин паровой.
Тумба из ЛДСП

Двери межкомнатные
ACADEMY
Slim Soft Touch
высота полотна - 2200

торшер Китай

встраиваемый
гипсовый
светильник
SUBRA-M 60

тумба
подиум с нишей для тумб
ЛДСП под дерево

столик туалетный с зеркалом и
ящиком, WB, 1100x400

стул OZON

кварцвинил
или инженерная
доска

Плинтус скрытый



Санузел 2 эт. Коллаж-концепция

потолок
натяжной

покраска

короб под
инсталляцию
Панели полиуретан
под травертин, на клей
(или керамогранит
600x1200)

дверь скрытая,
реверсное открывание

полка из плитки

душ. система
встраиваемая

подвесной унитаз
с инсталляцией,
гигиенический душ

экран ванны
с нишей для ног
и подсветкой

подсветка закарнизная
и вертикальная
(до борта ванны или до полки)

короб с нишей

полки в нише

встраиваемый св-ник
MAYTONI
Dot DL028-2-01W
для натяжных потолков



композиция из сухой травы
с подсветкой
за стеклянной
перегородкой
(доступ из гардеробной)

встроенный шкаф
с открытой нишей
и ящиками

панели полиуретан
под травертин, на клей
(или керамогранит
600x1200)

покраска

зеркало органической
формы Continent

встраиваемый смеситель


раковина из бетона,
тумбы по бокам

керамогранит 600x1200
ИТАЛОН СНОУ
натуральный

керамогранит 600x1200
ИТАЛОН СНОУ
натуральный



План опорный, 1 этаж

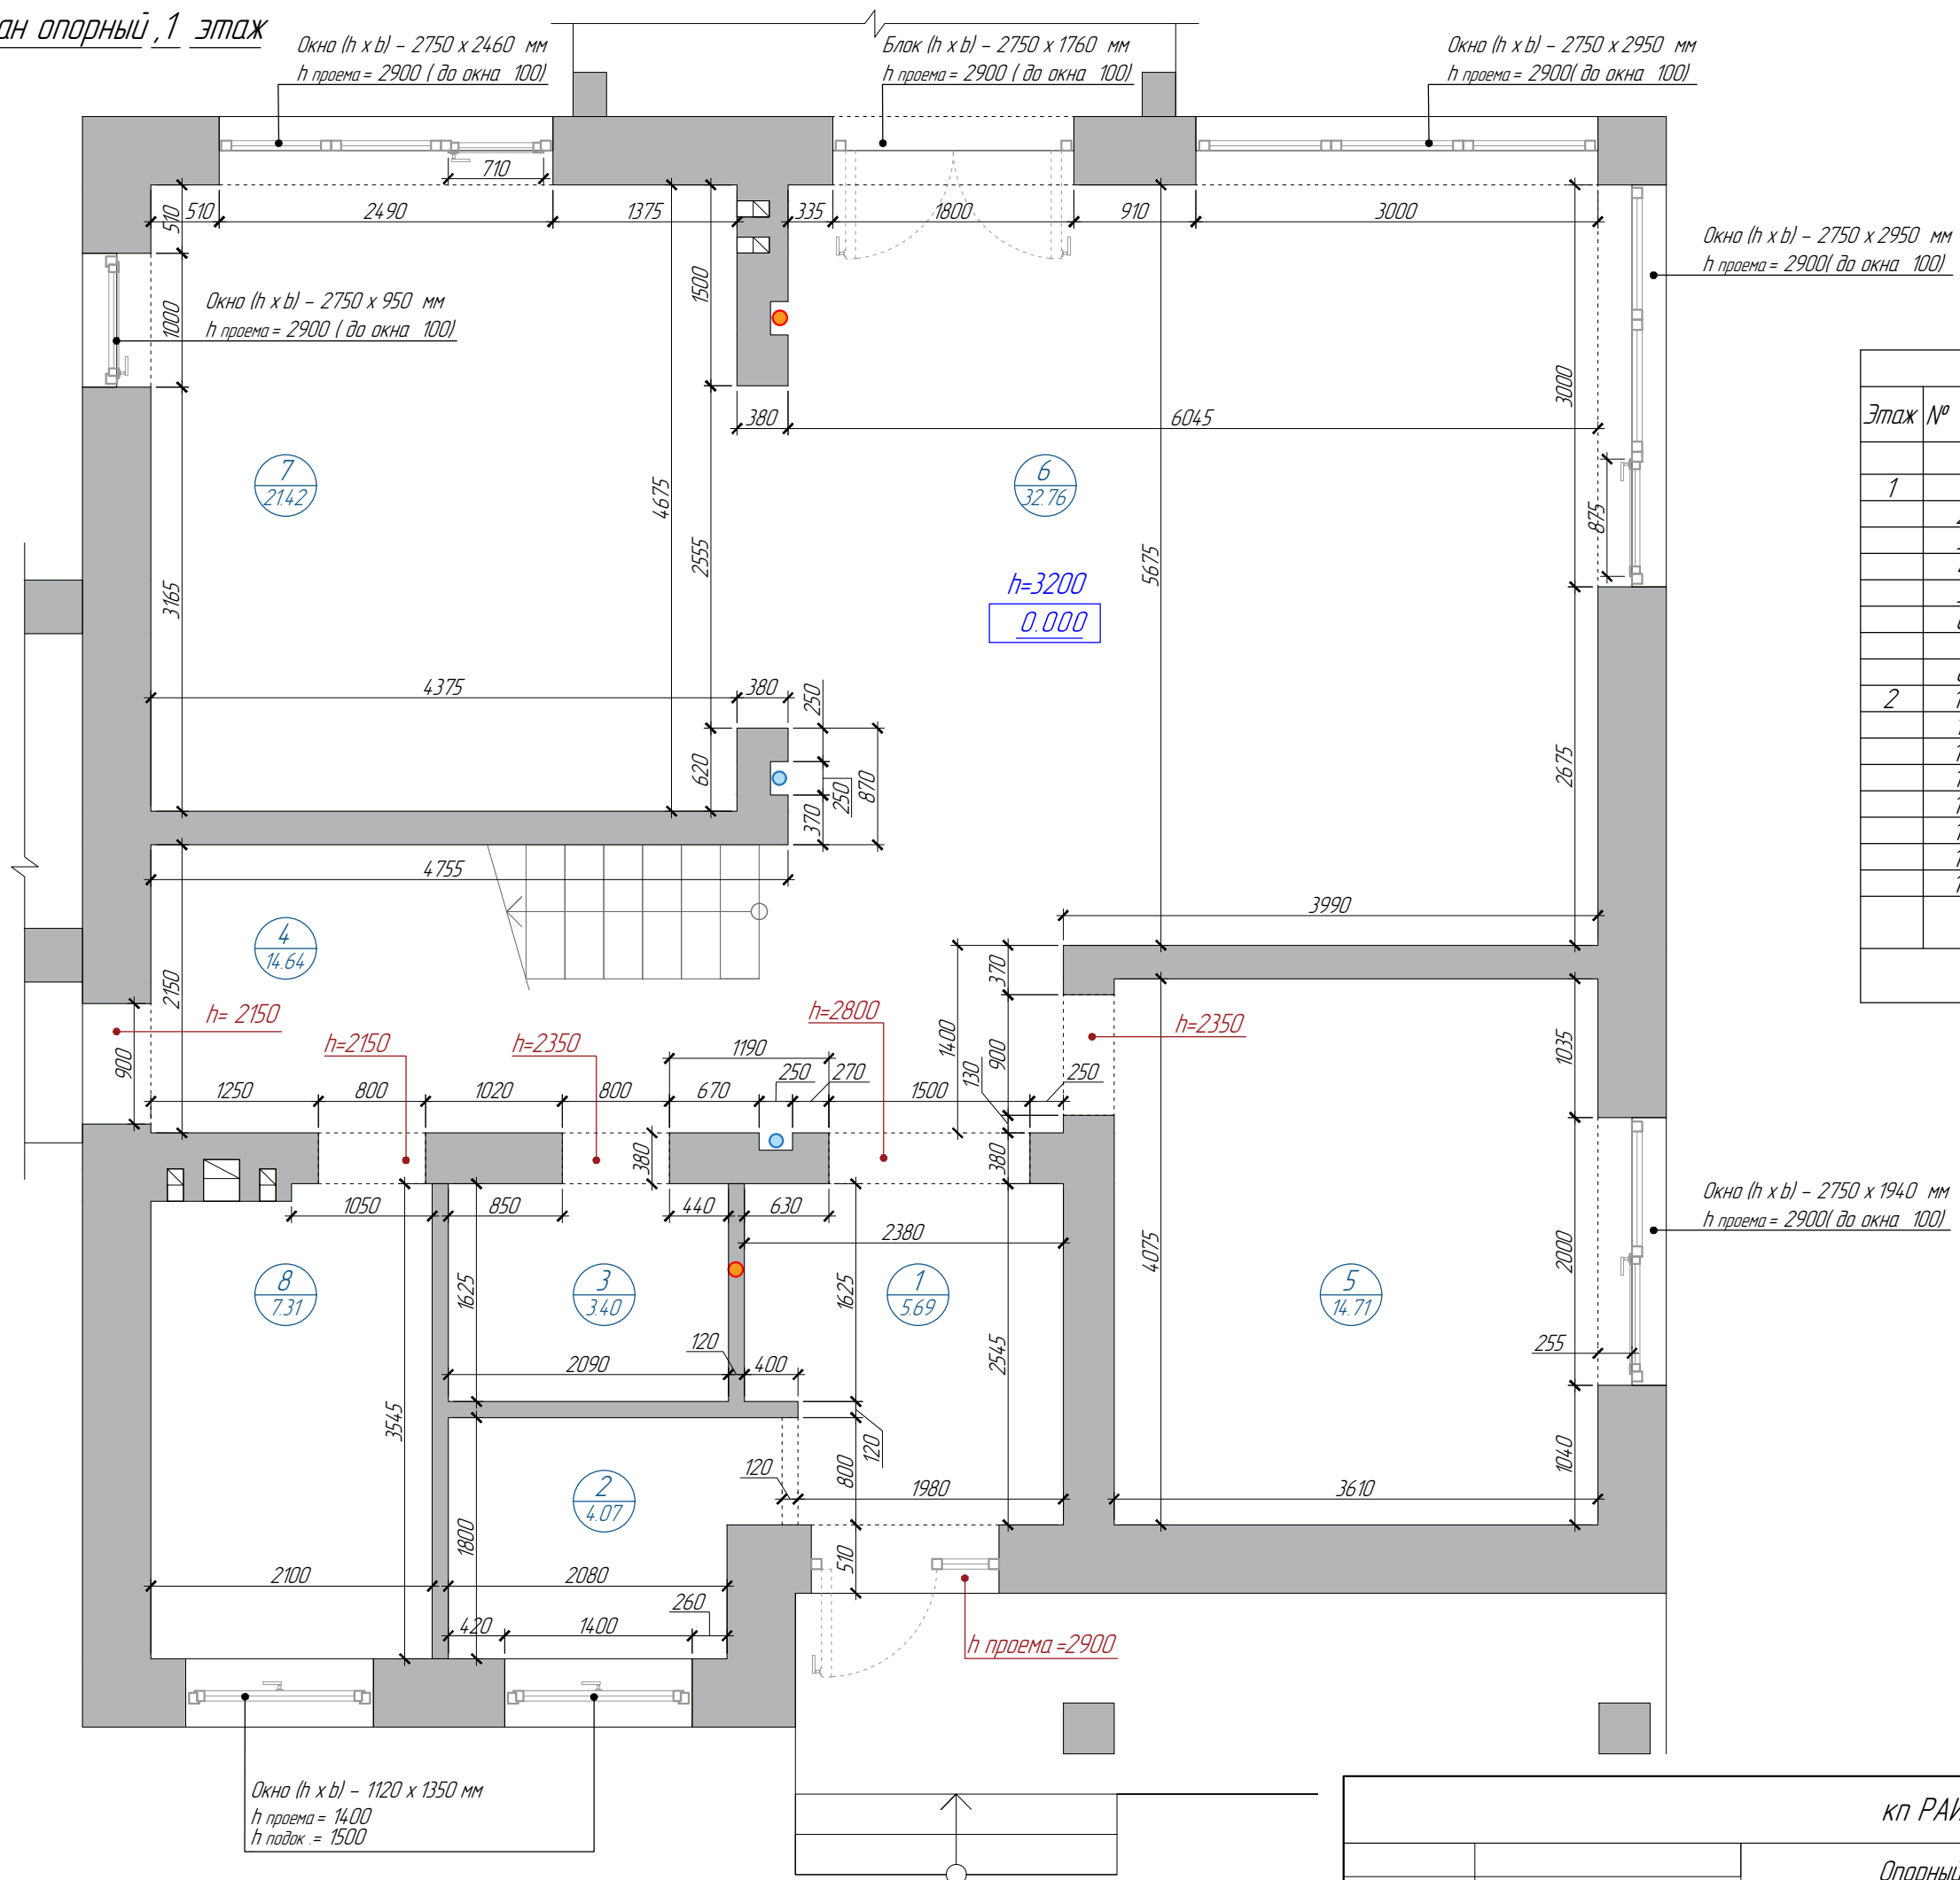

Экспликация помещений					
Этаж	№ пом.	Наименование помещения	Площадь, м ²		Примечание
			осн.	вспом.	
1	1	Прихожая		5.69	
	2	Гардеробная		4.07	
	3	Санузел гостевой		3.40	
	4	Лестничный холл		14.64	
	5	Комната няни	14.71		
	6	Гостиная	32.76		
	7	Кухня –столовая	21.42		
	8	Котельная		7.31	
2	10	Лестничный холл		8.54	
	11	Мастер –спальня	20.45		
	12	Ванная комната		6.33	
	13	Гардеробная		4.25	
	14	Детская комната	20.49		
	15	Кабинет	14.71		
	16	Санузел		6.08	
	17	Гостевая комната	15.11		
			Итого по помещениям	139.65	60.31
Общая площадь помещений дома			199.96		

УСЛОВНЫЕ ОБОЗНАЧЕНИЯ

-  стены и перегородки из керамоблока
 стояк канализации
 стояк лифтовой канализации


кп РАЙТ ЭКО

Опорный план. 1 этаж

Архитектор	Обчарова Ольга
------------	----------------

ΟΔΥΣΣΕΥΣ
PROJECT

План опорный, 2 этаж

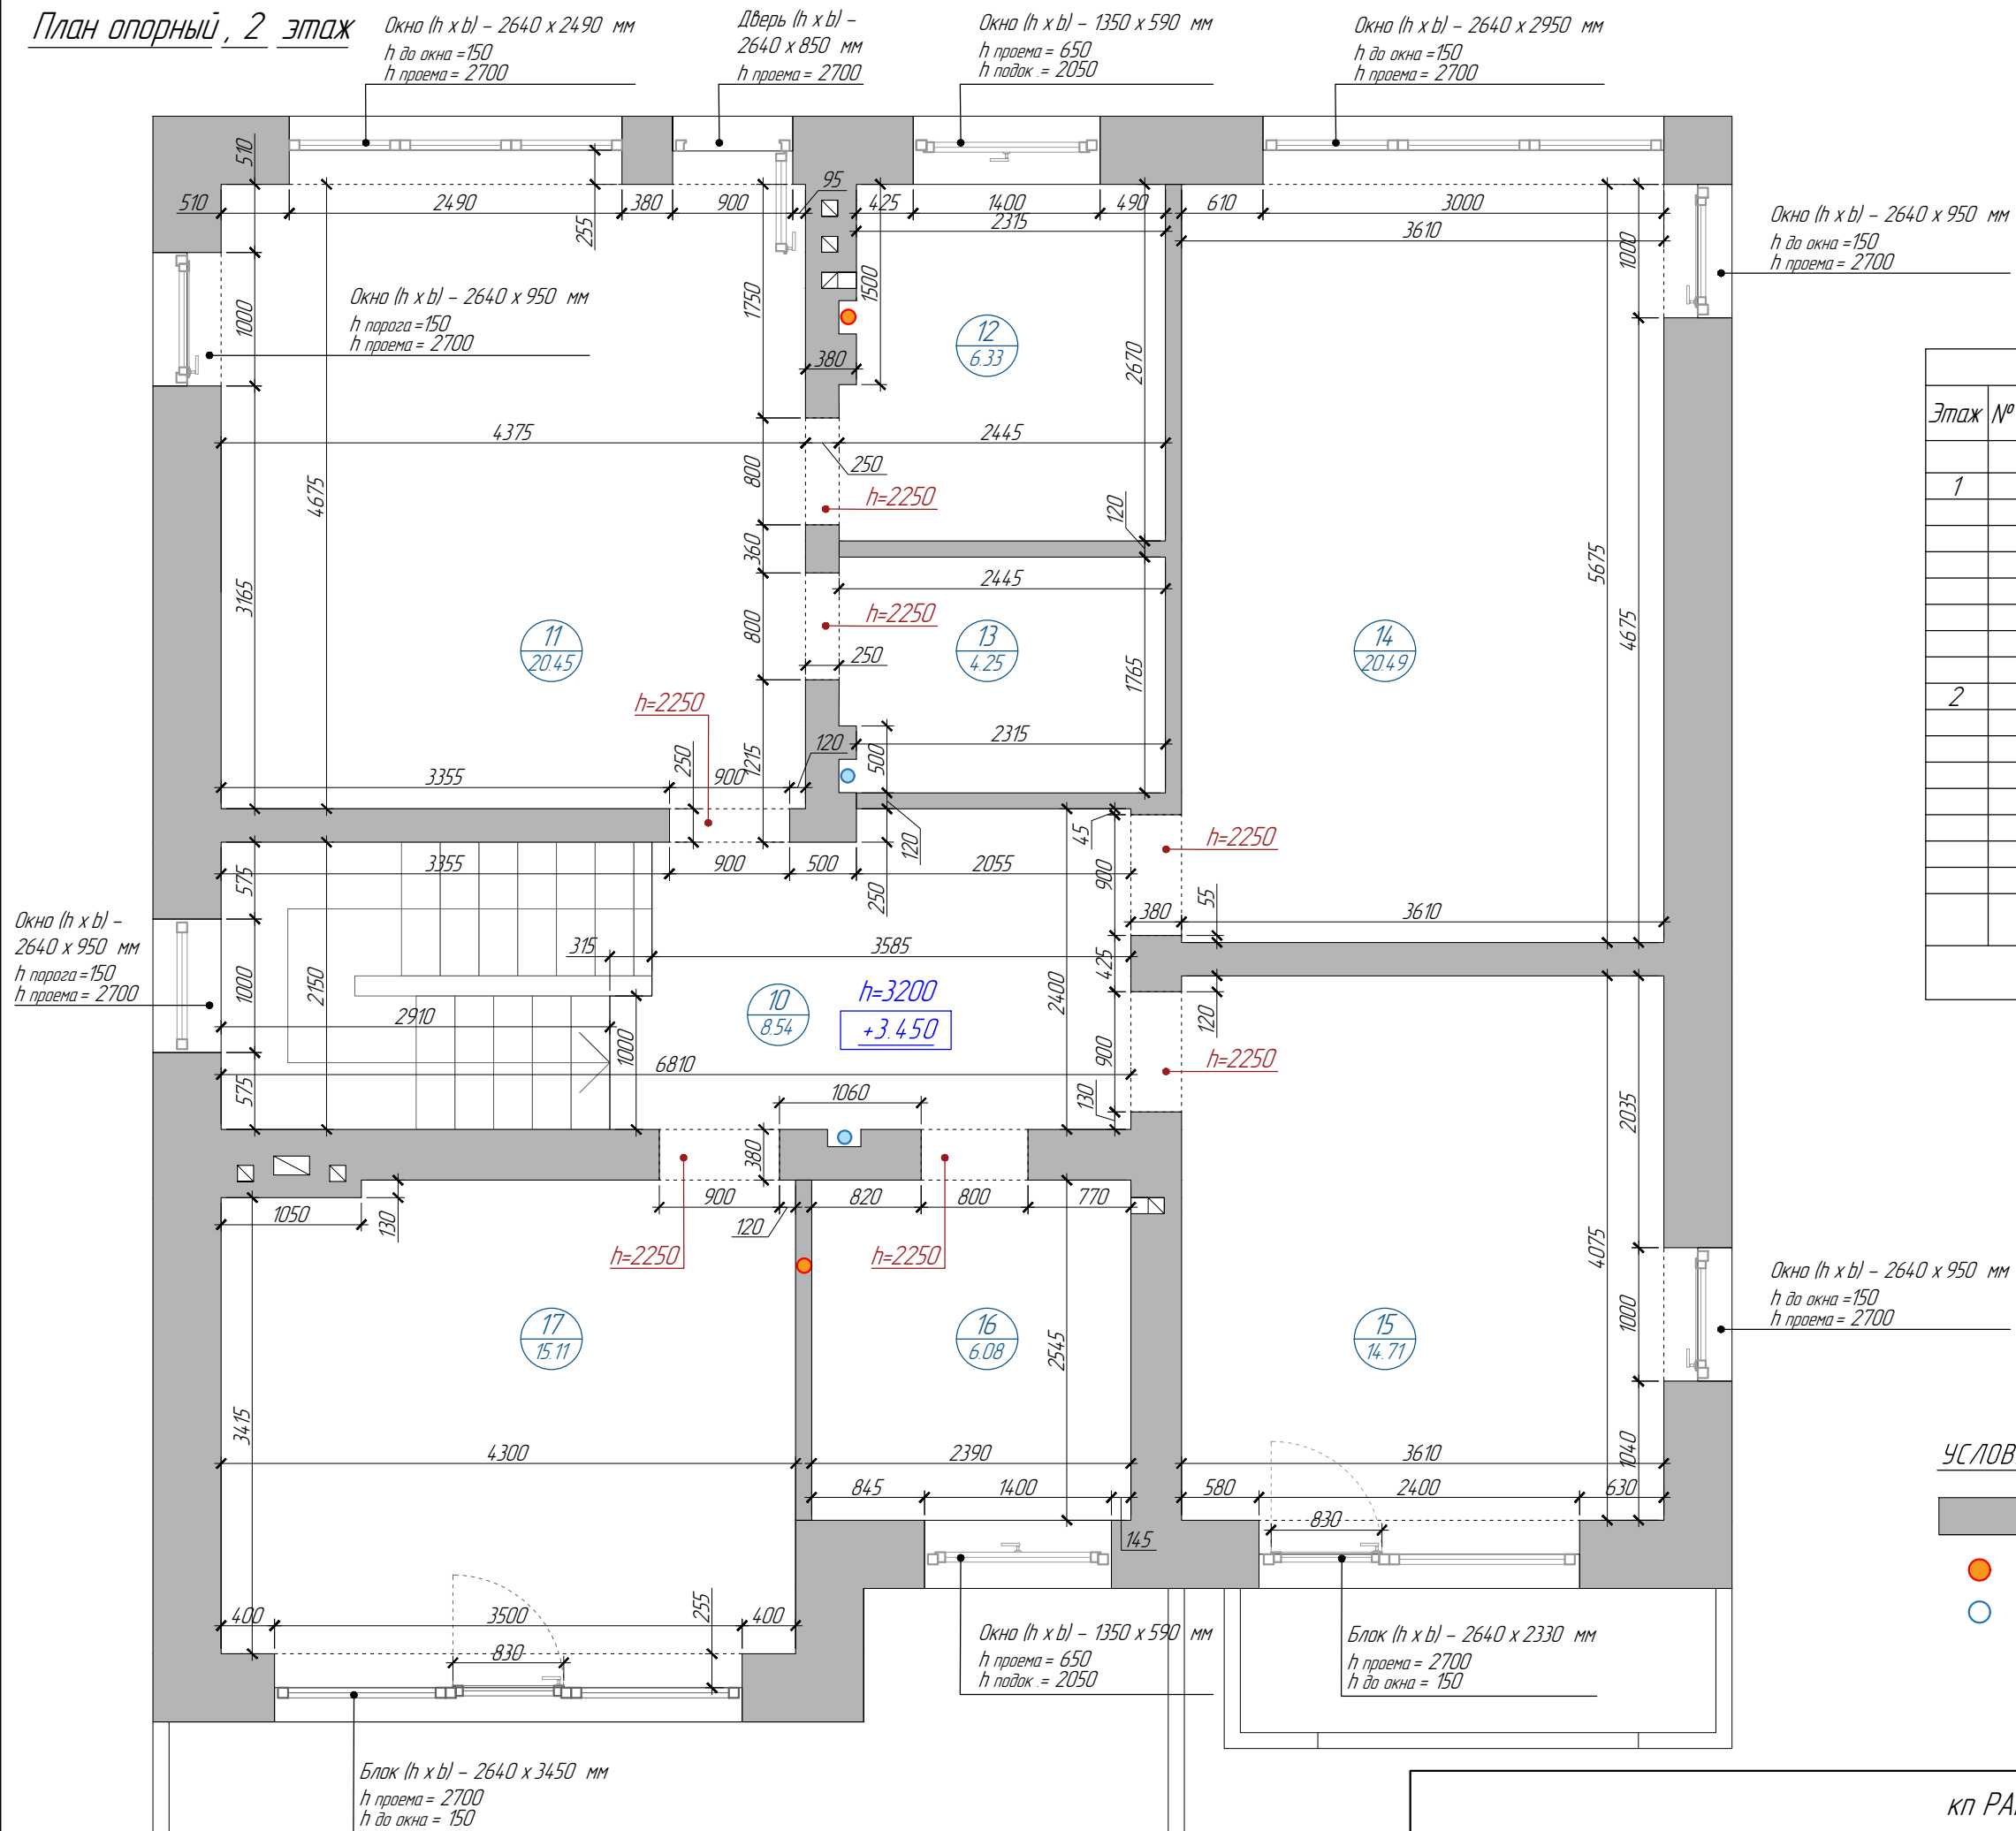

Экспликация помещений					
Этаж	№ пом.	Наименование помещения	Площадь, м ²		Примечание
			осн.	вспом.	
1	1	Прихожая		5.69	
	2	Гардеробная		4.07	
	3	Санузел гостевой		3.40	
	4	Лестничный холл		14.64	
	5	Комната няни	14.71		
	6	Гостиная	32.76		
	7	Кухня -столовая	214.2		
	8	Котельная		7.31	
2	10	Лестничный холл		8.54	
	11	Мастер -спальня	20.45		
	12	Ванная комната		6.33	
	13	Гардеробная		4.25	
	14	Детская комната	20.49		
	15	Кабинет	14.71		
	16	Санузел		6.08	
	17	Гостевая комната	15.11		
		Итого по помещениям	139.65	60.31	
Общая площадь помещений дома			199.96		


УСЛОВНЫЕ ОБОЗНАЧЕНИЯ

-  стены и перегородки из керамблока
 стояк канализации
 стояк ливневой канализации

кп РАЙТ ЭКО

Опорный план. 2 этаж

ΟΙΚΟΧΑΡΩΝ
PROJECT

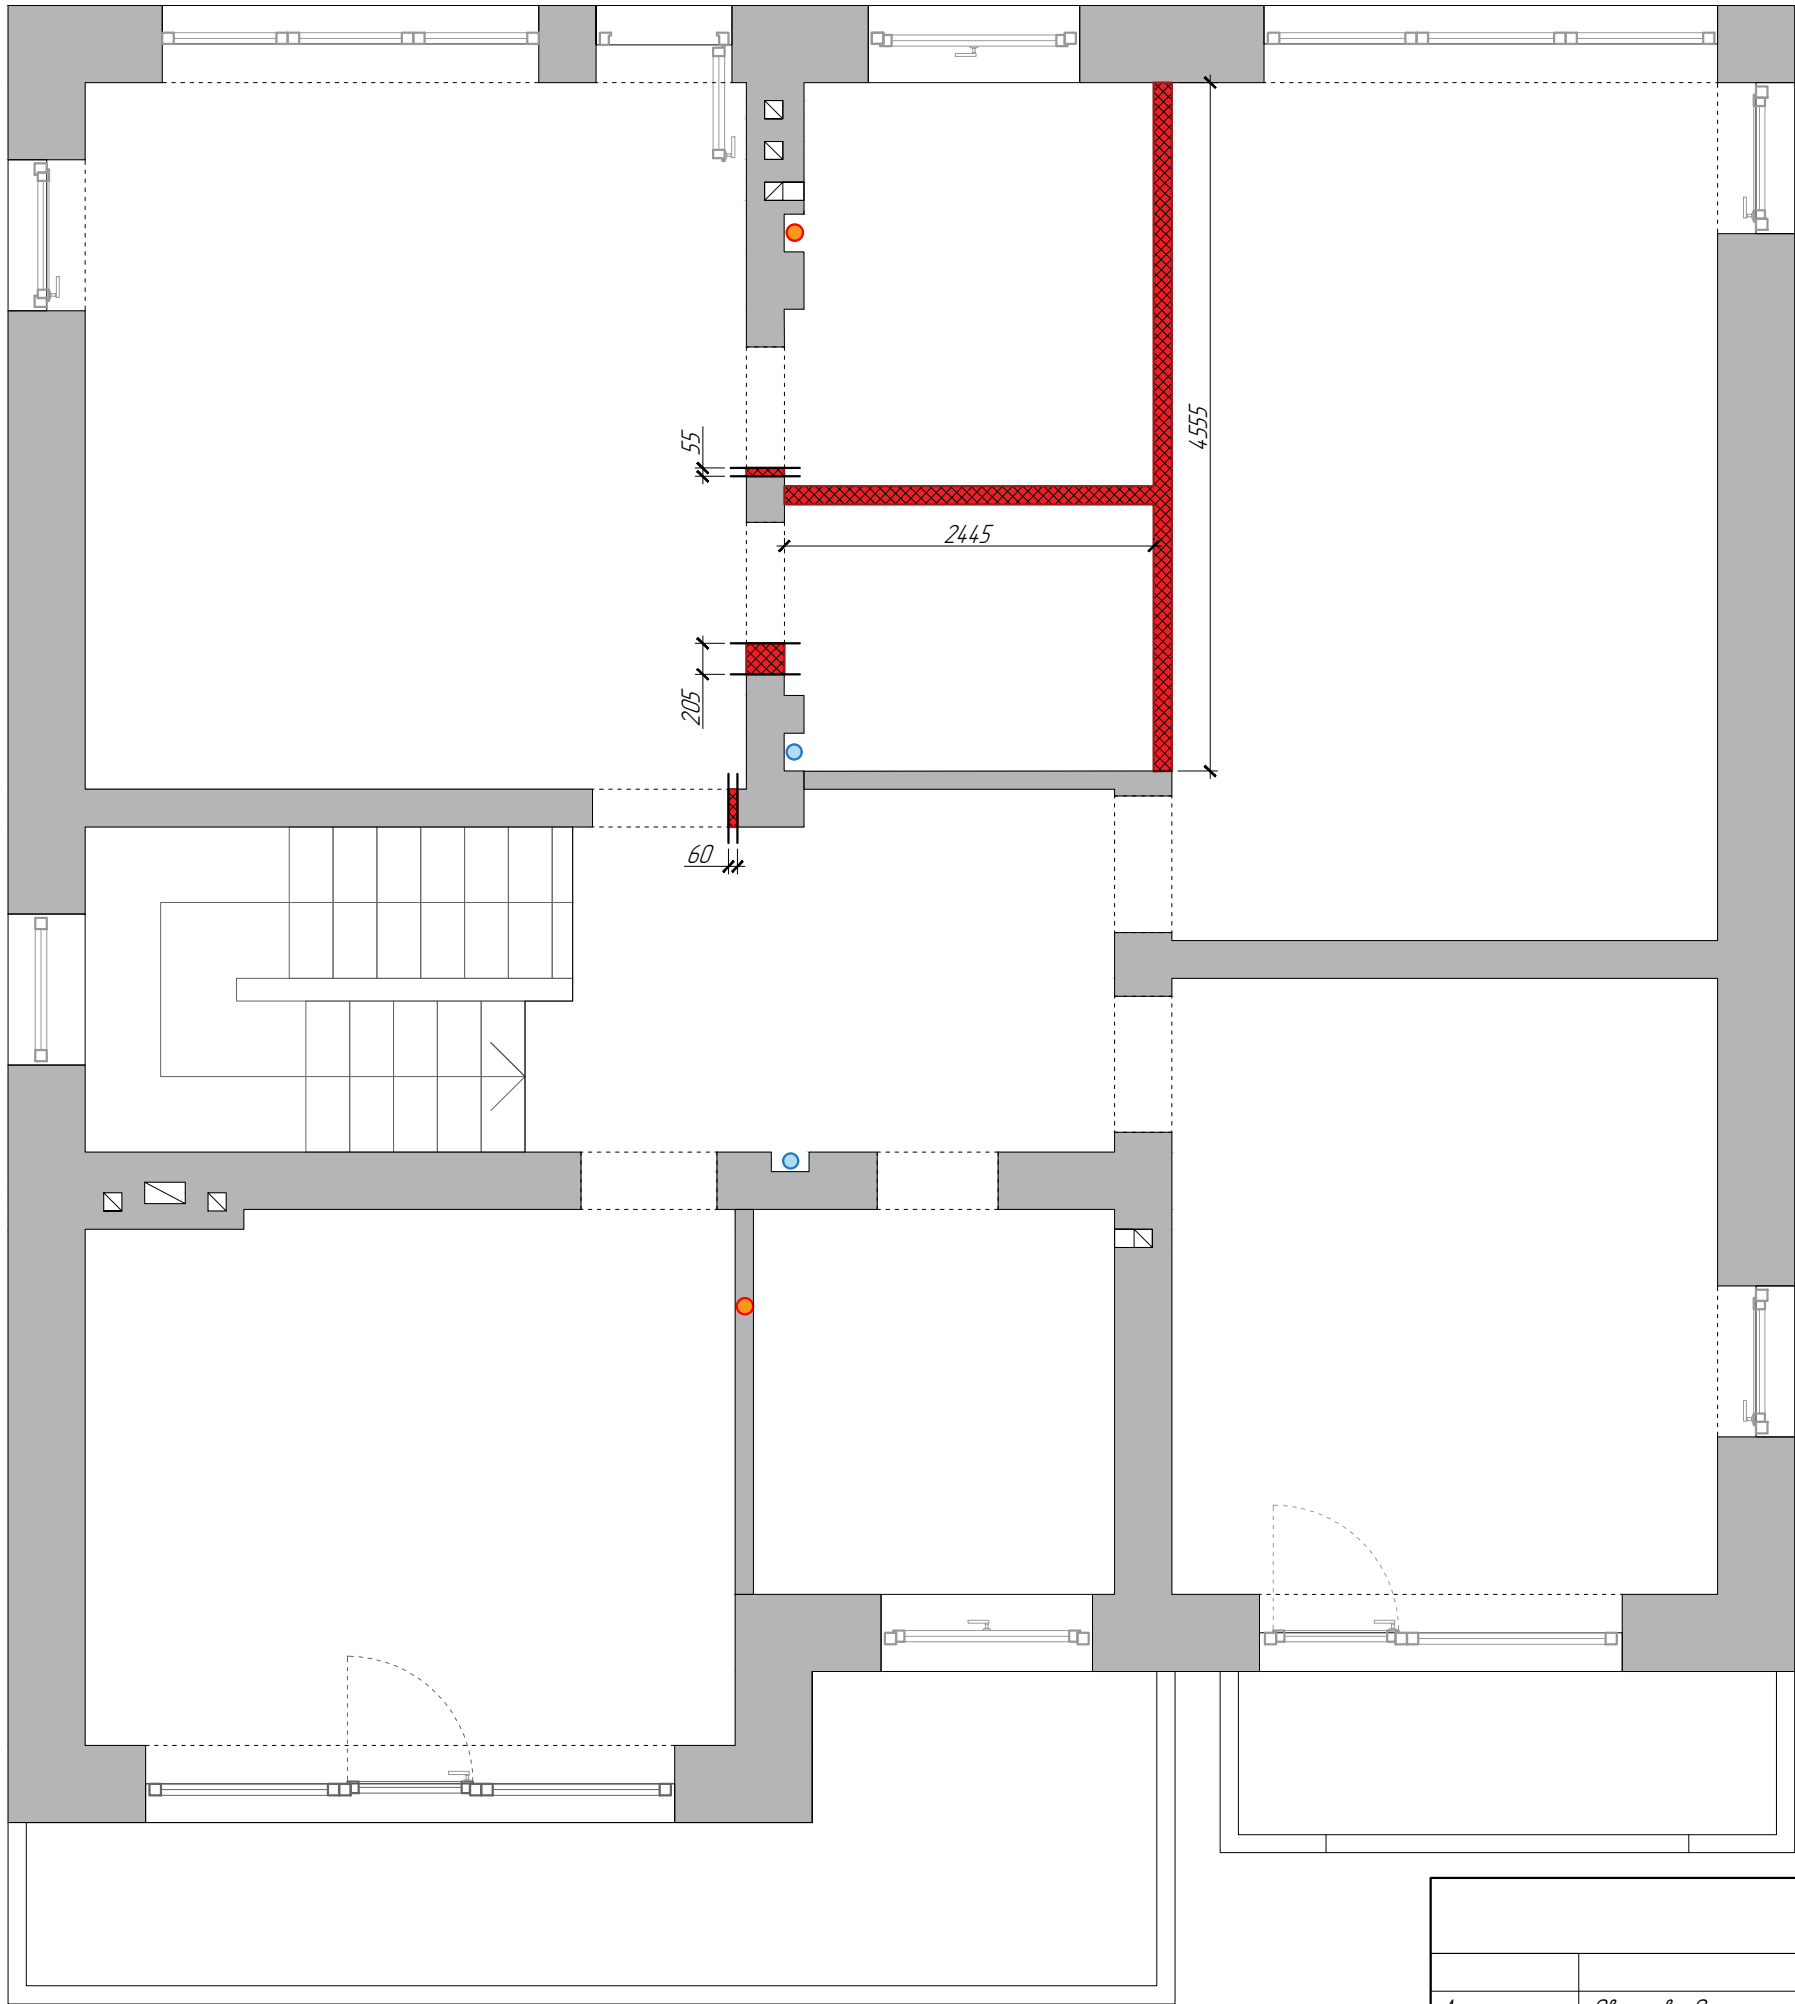

УСЛОВНЫЕ ОБОЗНАЧЕНИЯ

- стены и перегородки из керамоблока
- стояк канализации
- стояк ливневой канализации
- демонтируемые перегородки и их фрагменты


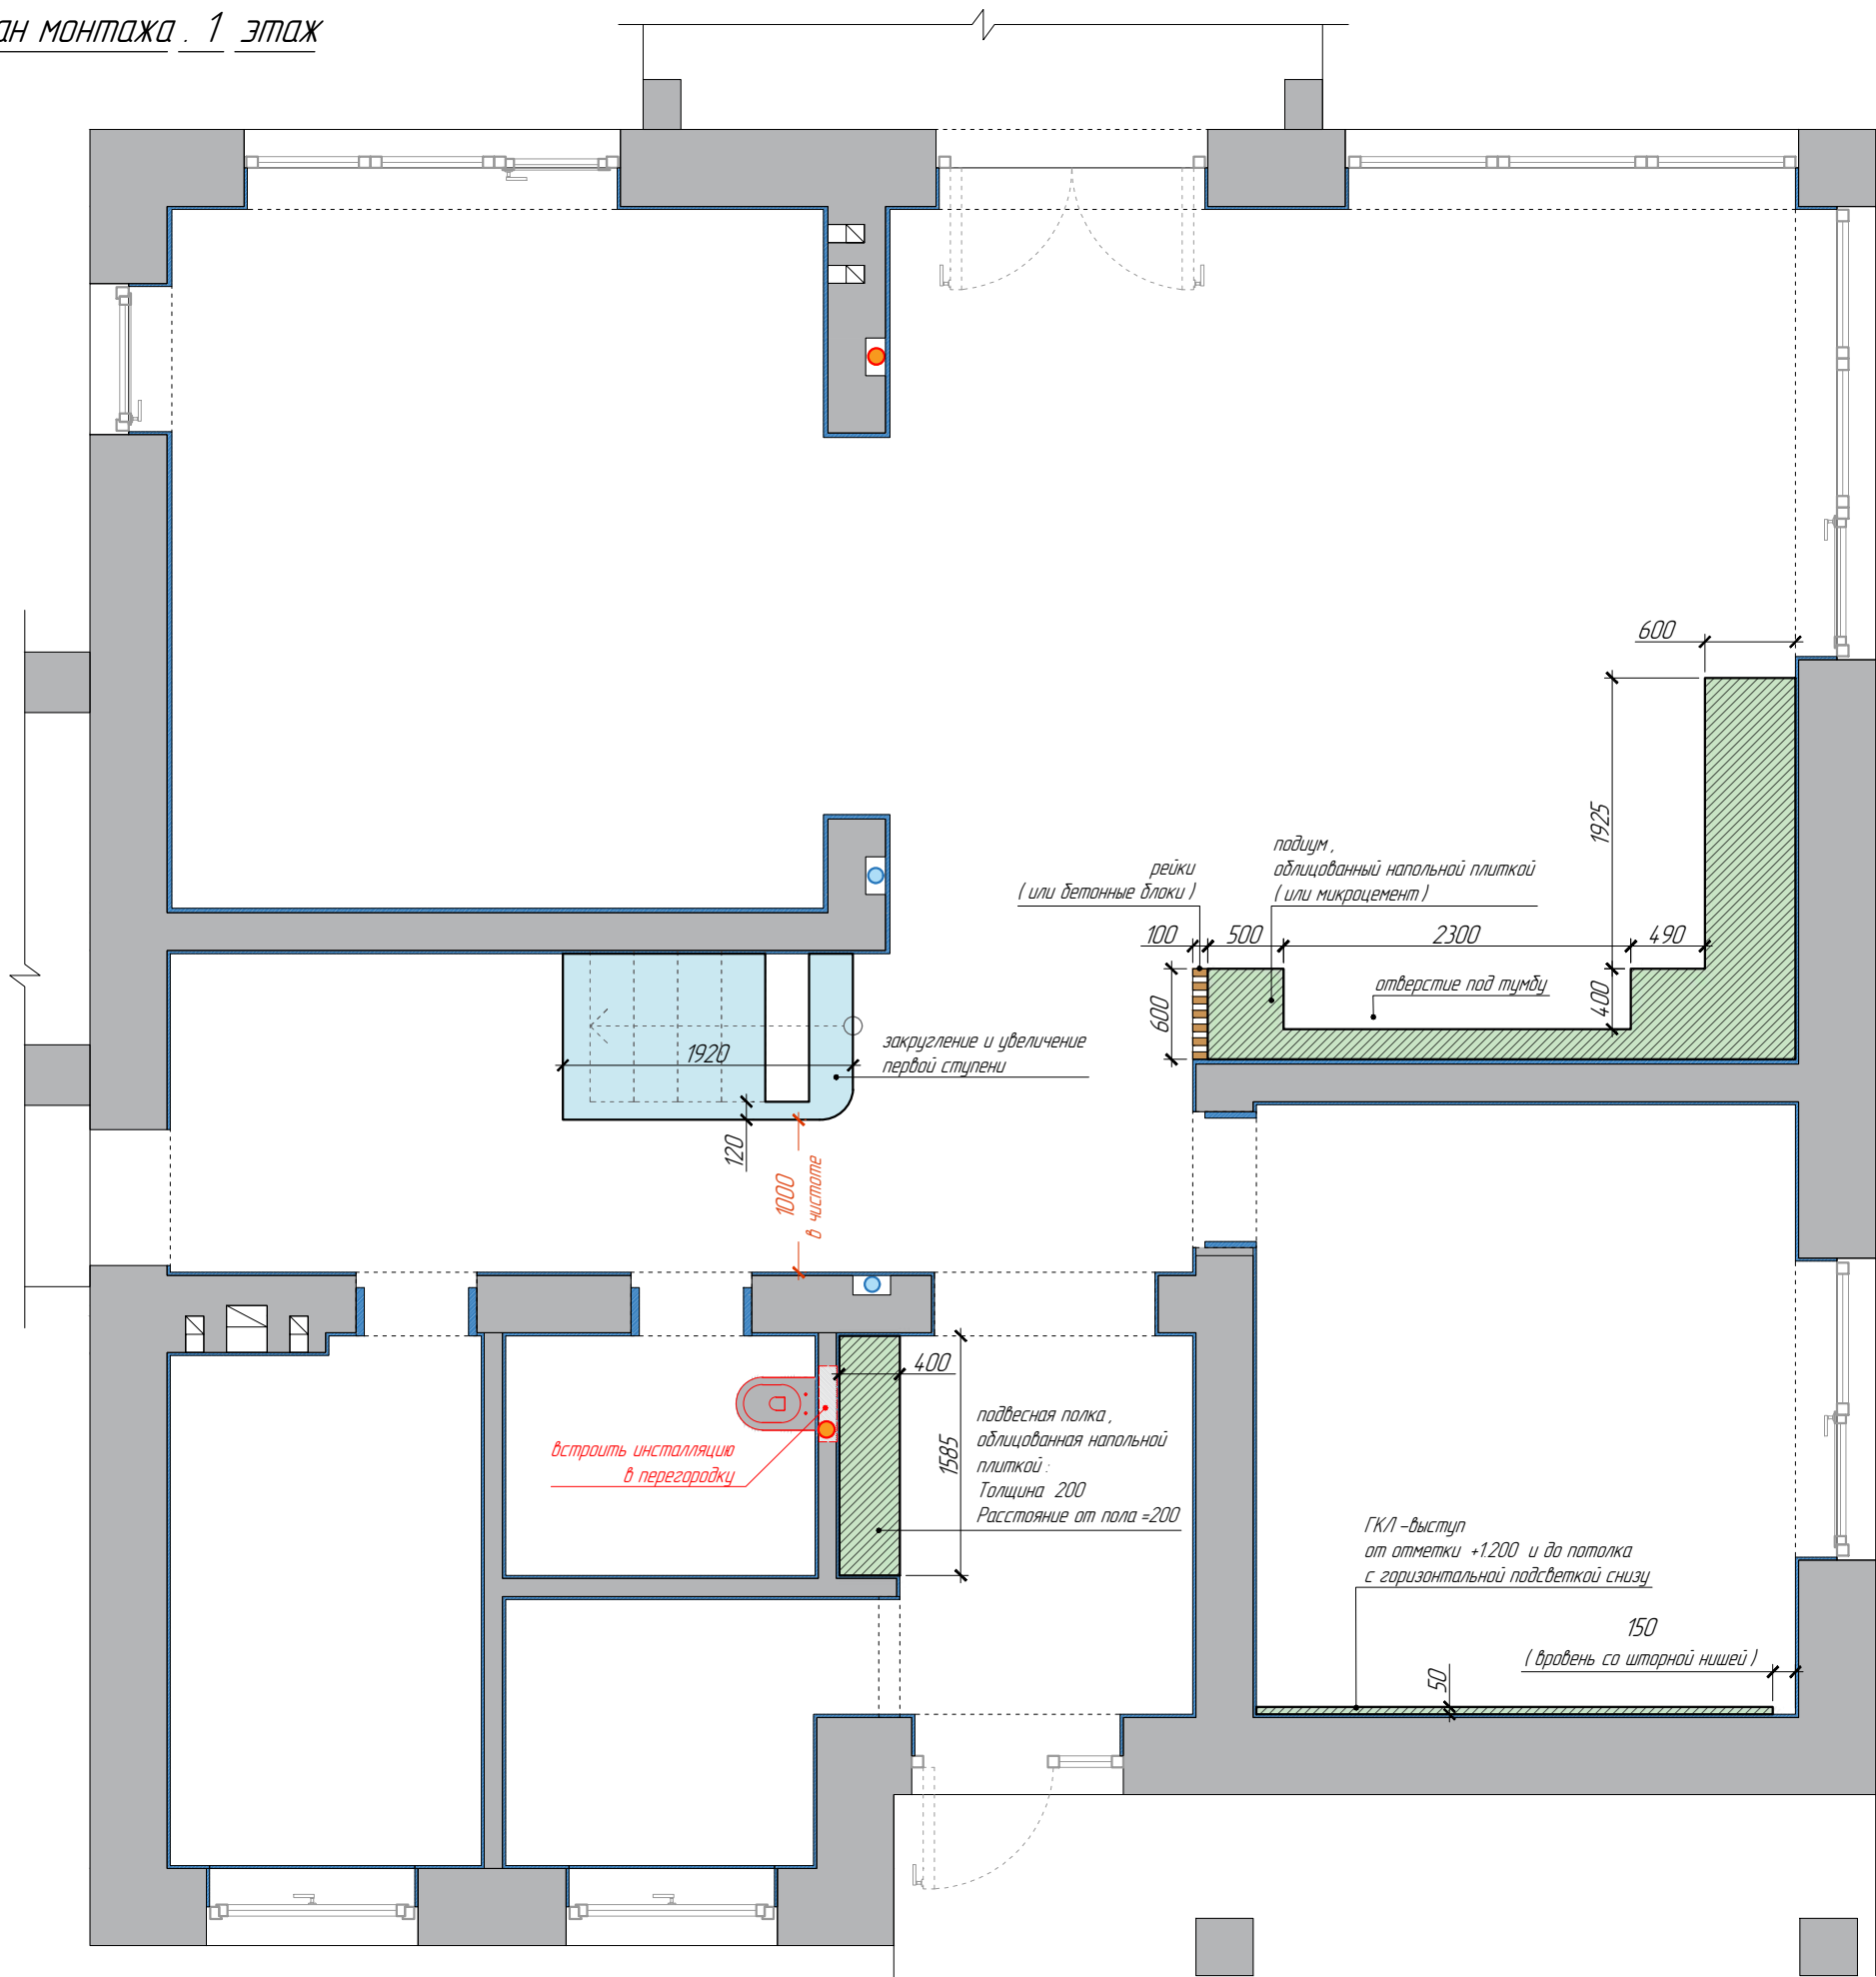


Схема подиума в гостиной

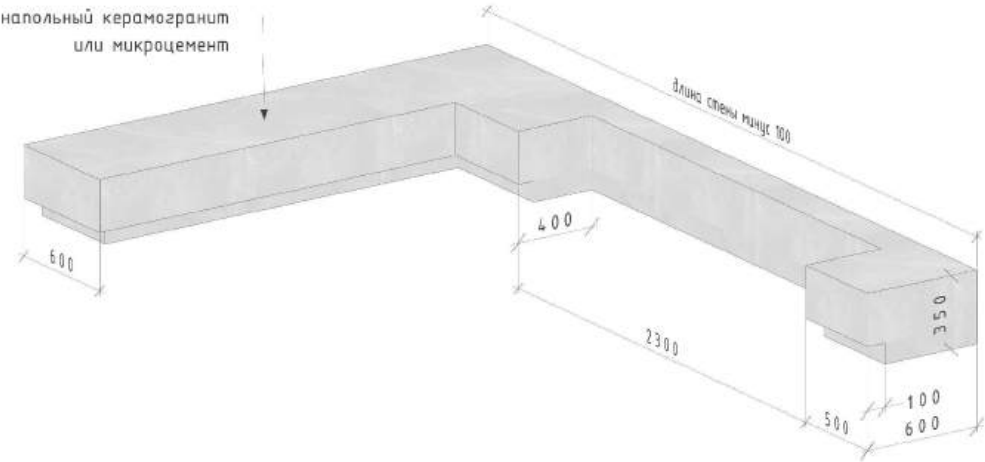

УСЛОВНЫЕ ОБОЗНАЧЕНИЯ

- стены и перегородки из керамоблока
- стояк канализации
- стоякливневой канализации
- возводимые перегородки из пазогребневых блоков
- возводимые перегородки из керамоблоков
- возводимые конструкции из ГКЛВ
- важные размеры
- штукатурный слой

ПРИМЕЧАНИЯ

- Все конструкции возводятся с отм. 0.000 до отметки потолка, если не указано иное
- Внутренние и внешние углы, к которым будет примыкать встроенная мебель, вывести 90° как на плане, так и по вертикали.


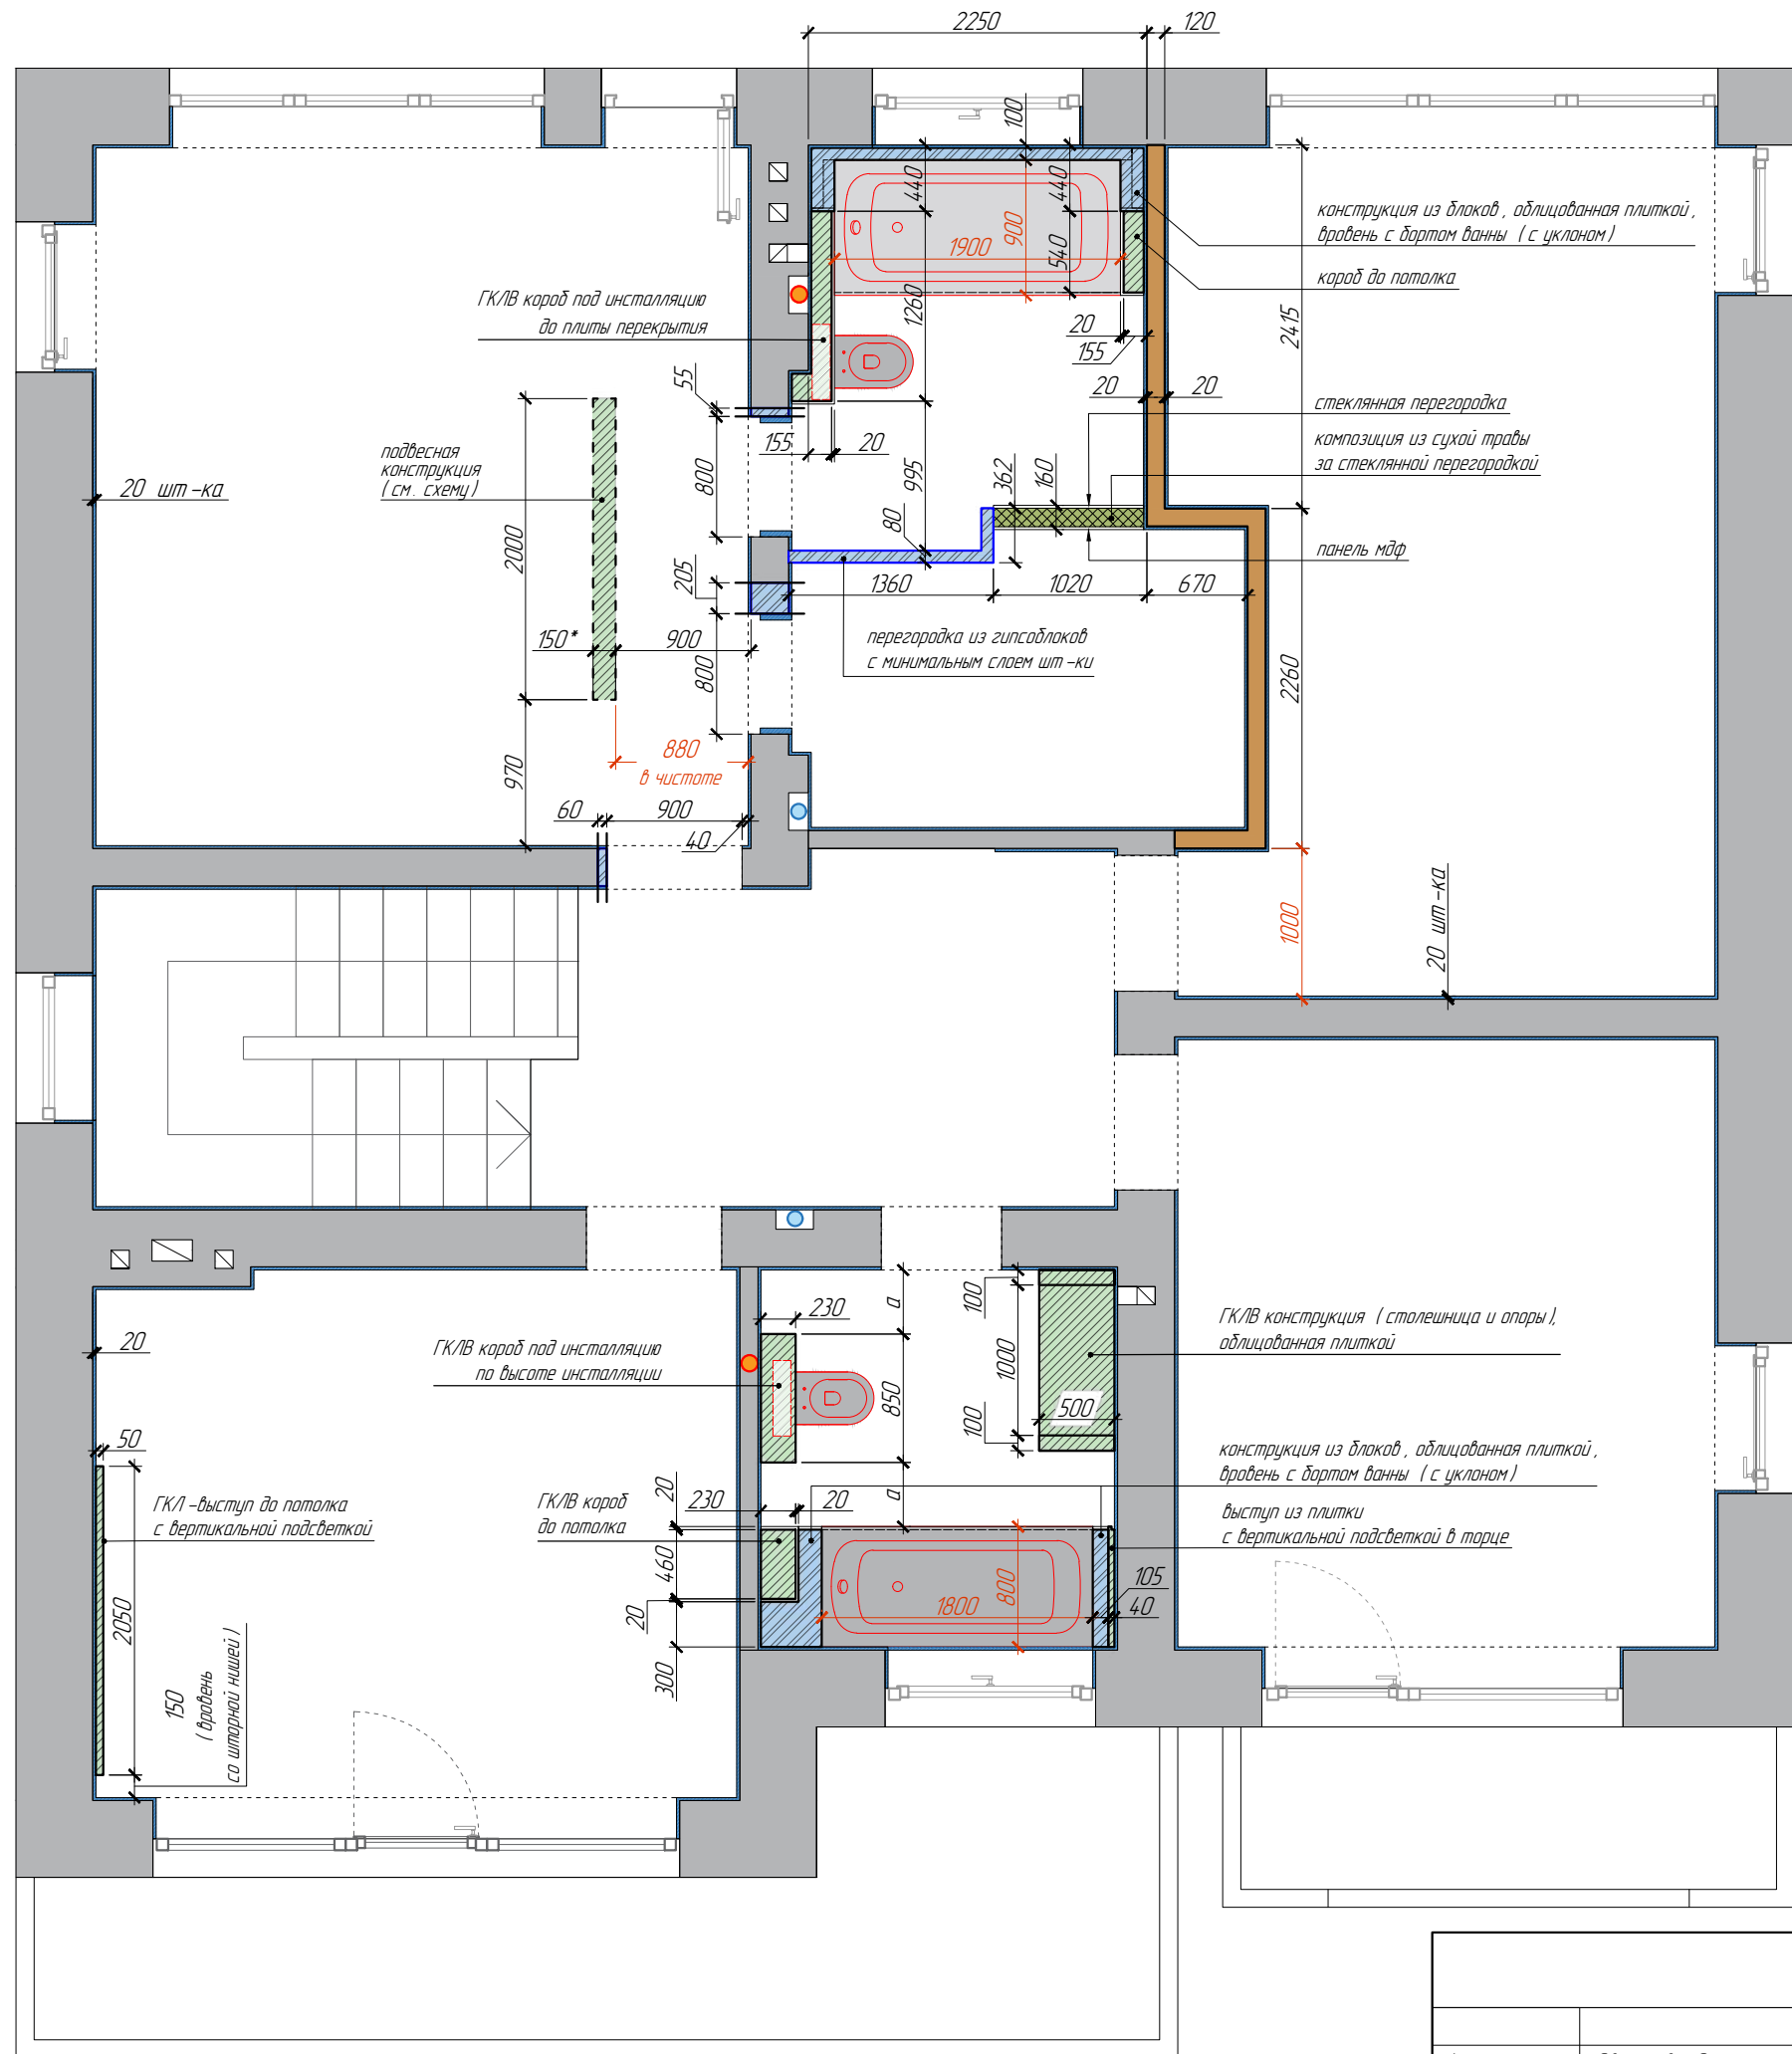


Схема подвесной конструкции под ТВ в спальне

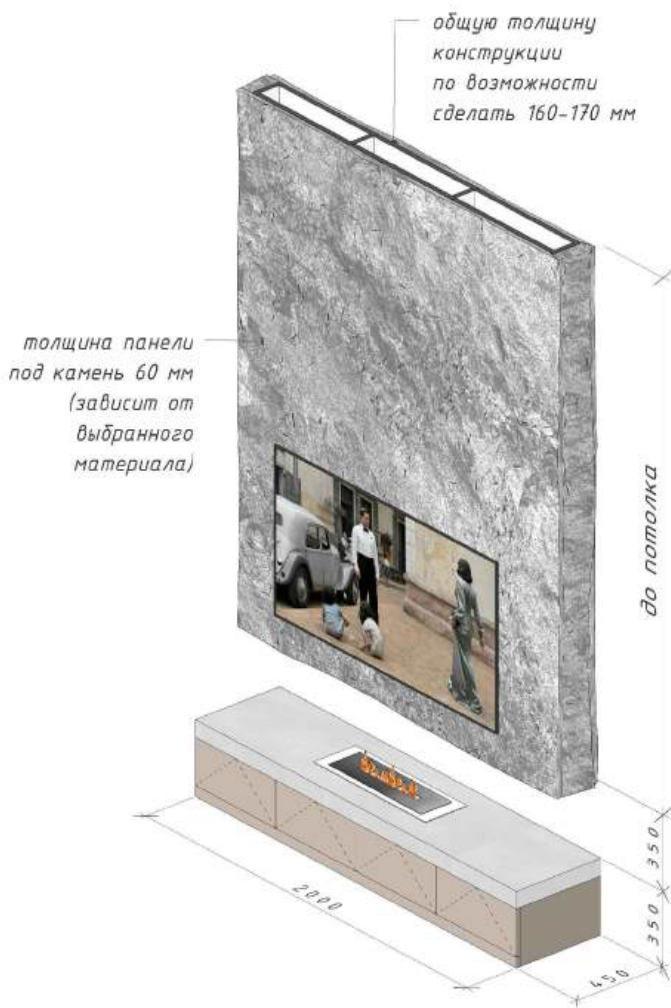

УСЛОВНЫЕ ОБОЗНАЧЕНИЯ

- стены и перегородки из керамблока
- стояк канализации
- стоякливневой канализации
- возводимые перегородки из пазогребневыхблоков
- возводимые перегородки из керамблоков
- возводимые конструкции из ГКЛ/В
- важные размеры
- штукатурный слой

ПРИМЕЧАНИЯ

- Все конструкции возводятся с отм. 0.000 до отметки потолка, если не указано иное
- Внутренние и внешние углы, к которым будет примыкать встраиваемая мебель, вывести 90° как на плане, так и по вертикали.


кп РАЙТ ЭКО

План монтажа 2 этаж

ООО ЧАРОВА
PROJECT

Архитектор Овчарова Ольга

План 1 этажа

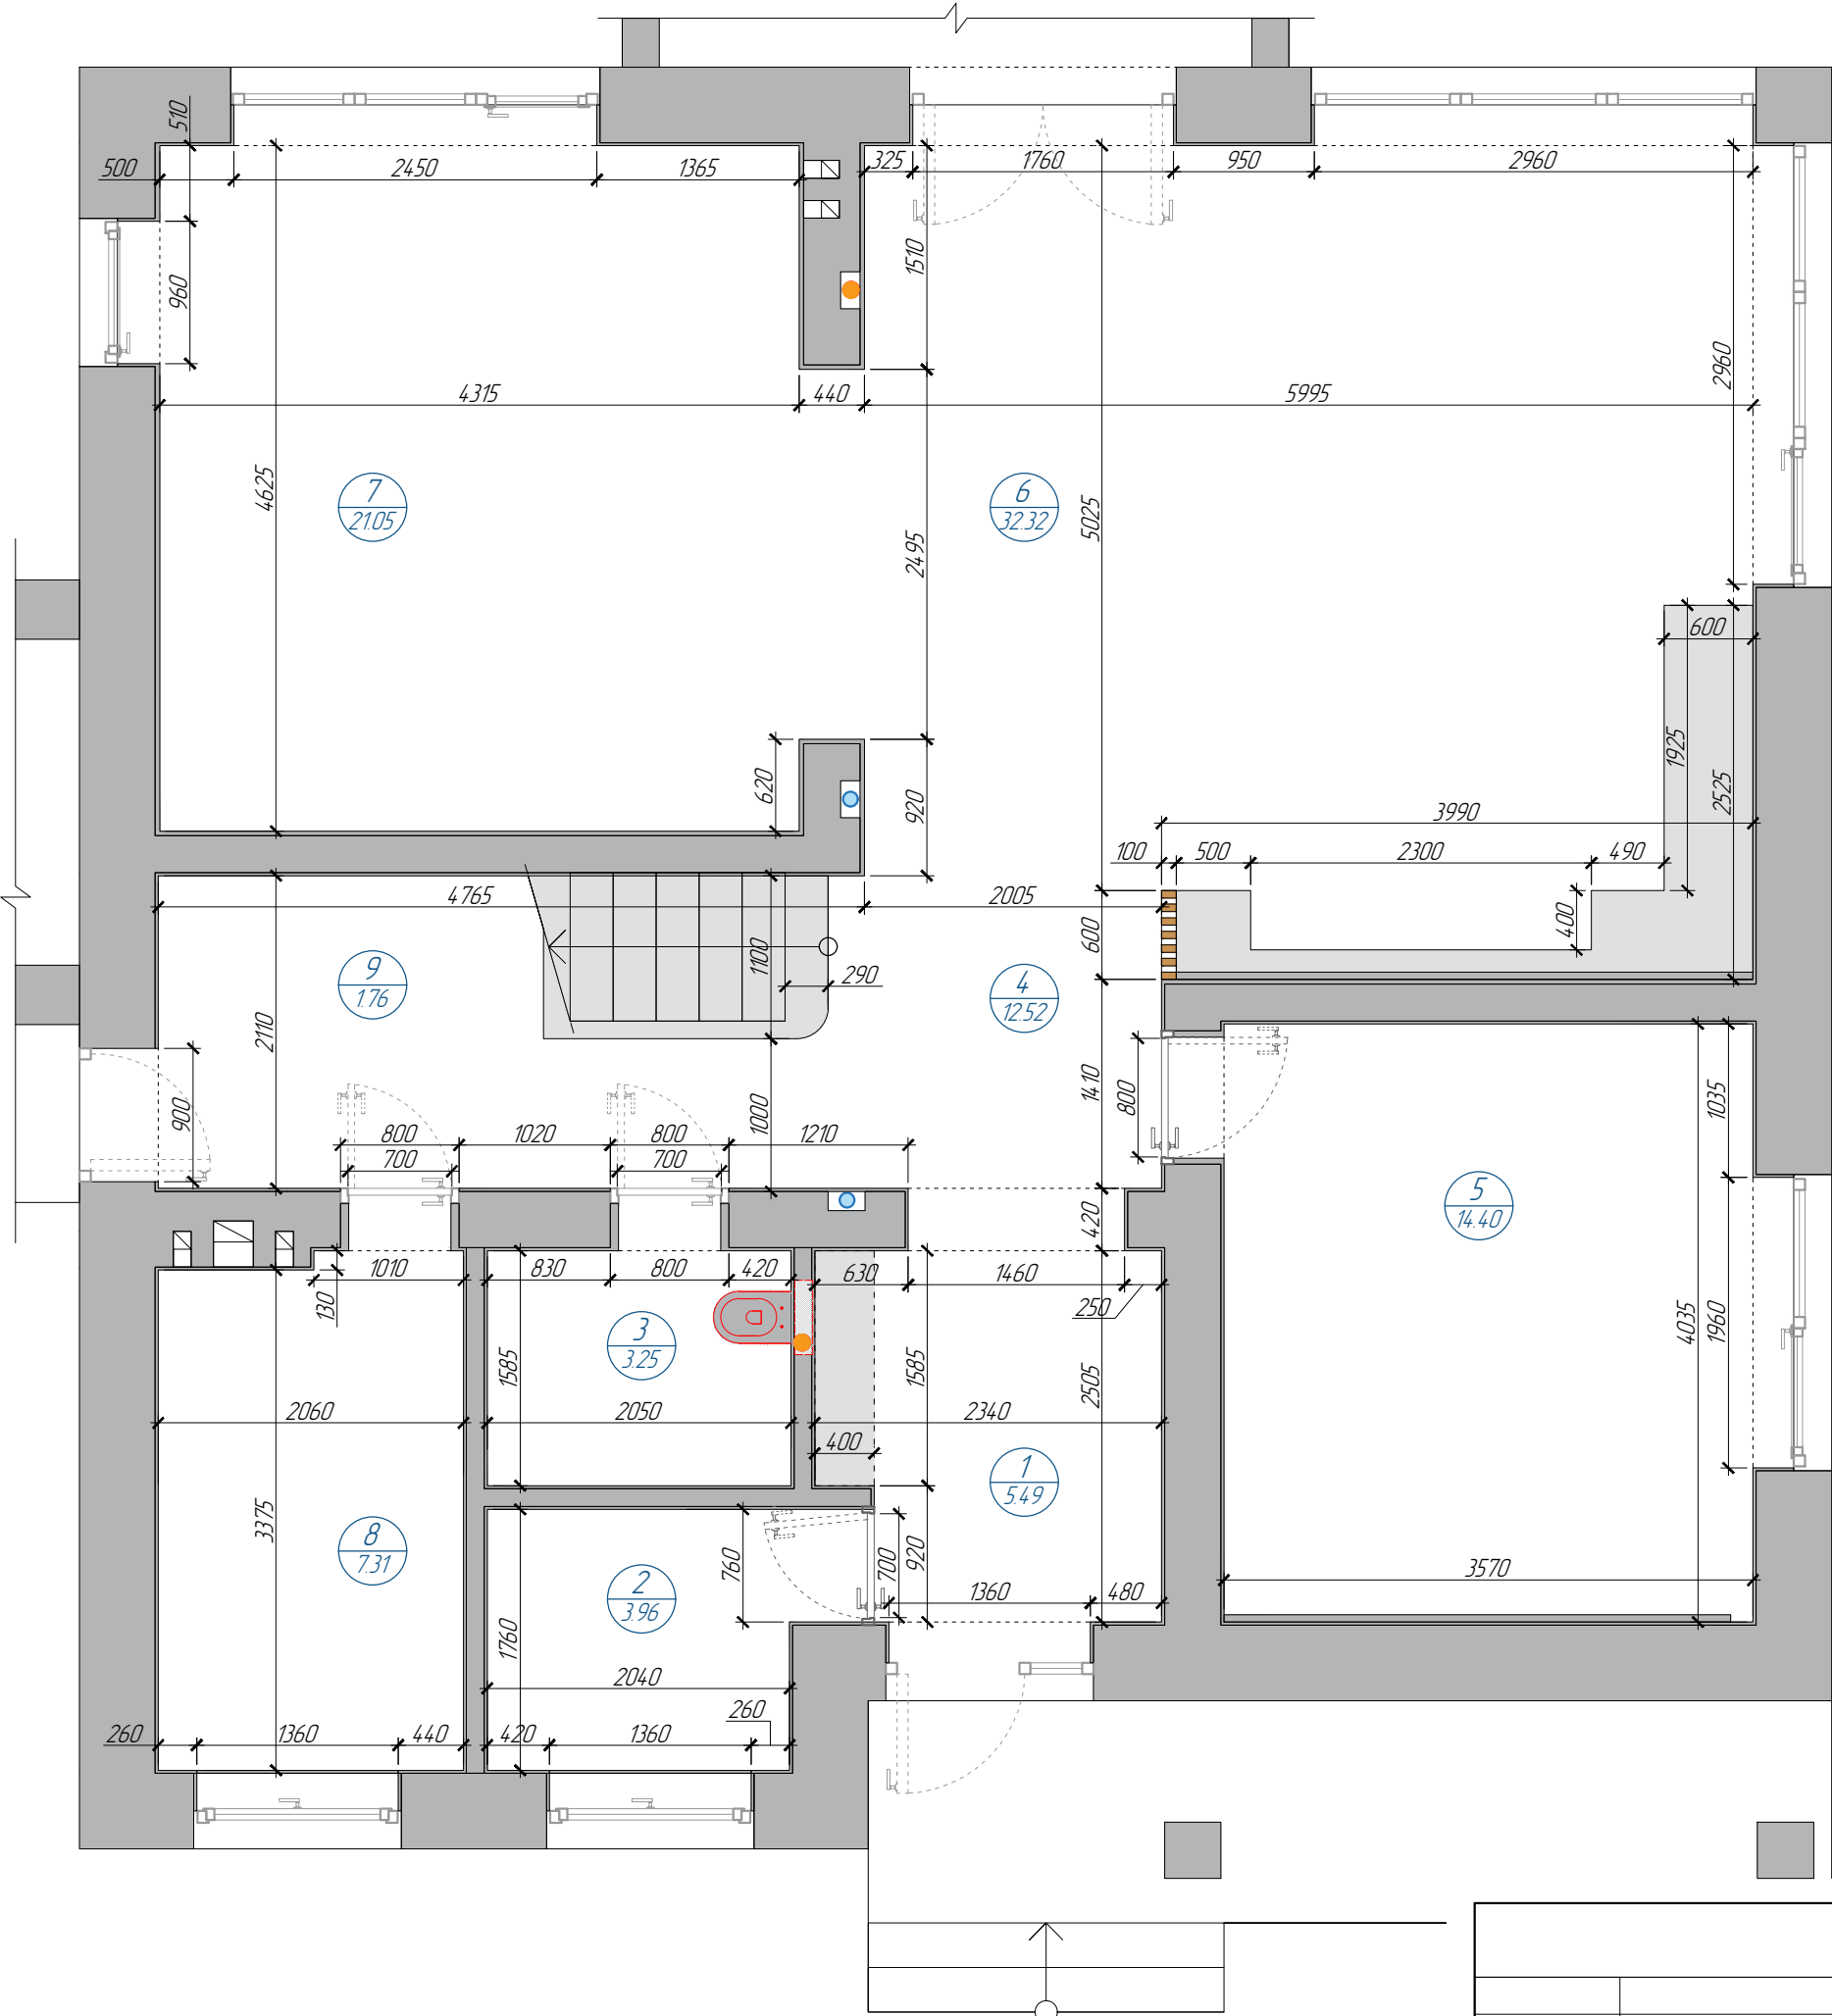

Экспликация помещений					
Этаж	№ пом.	Наименование помещения	Площадь , м ²		Примечание
			осн.	вспом.	
1	1	Прихожая		549	
	2	Гардеробная		396	
	3	Санузел гостей		325	
	4	Лестничный холл		1252	
	5	Комната няни	14.40		
	6	Гостиная	32.32		
	7	Кухня –столовая	2105		
	8	Котельная		731	
	9	Тех. помещение		176	
2	10	Лестничный холл		833	
	11	Мастер –спальня	20.10		
	12	Ванная комната		517	
	13	Гардеробная		574	
	14	Детская комната	18.88		
	15	Кабинет	14.41		
	16	Санузел		560	
	17	Гостевая комната	14.80		
		Итого по помещениям	135.96	59.13	
Общая площадь помещений дома			195.09		


УСЛОВНЫЕ ОБОЗНАЧЕНИЯ

- стены и перегородки из керамоблока
- стояк канализации
- стояк ливневой канализации

ПРИМЕЧАНИЯ

1. Все размеры указаны с учетом штукатурного слоя и плитки

План 2 этажа

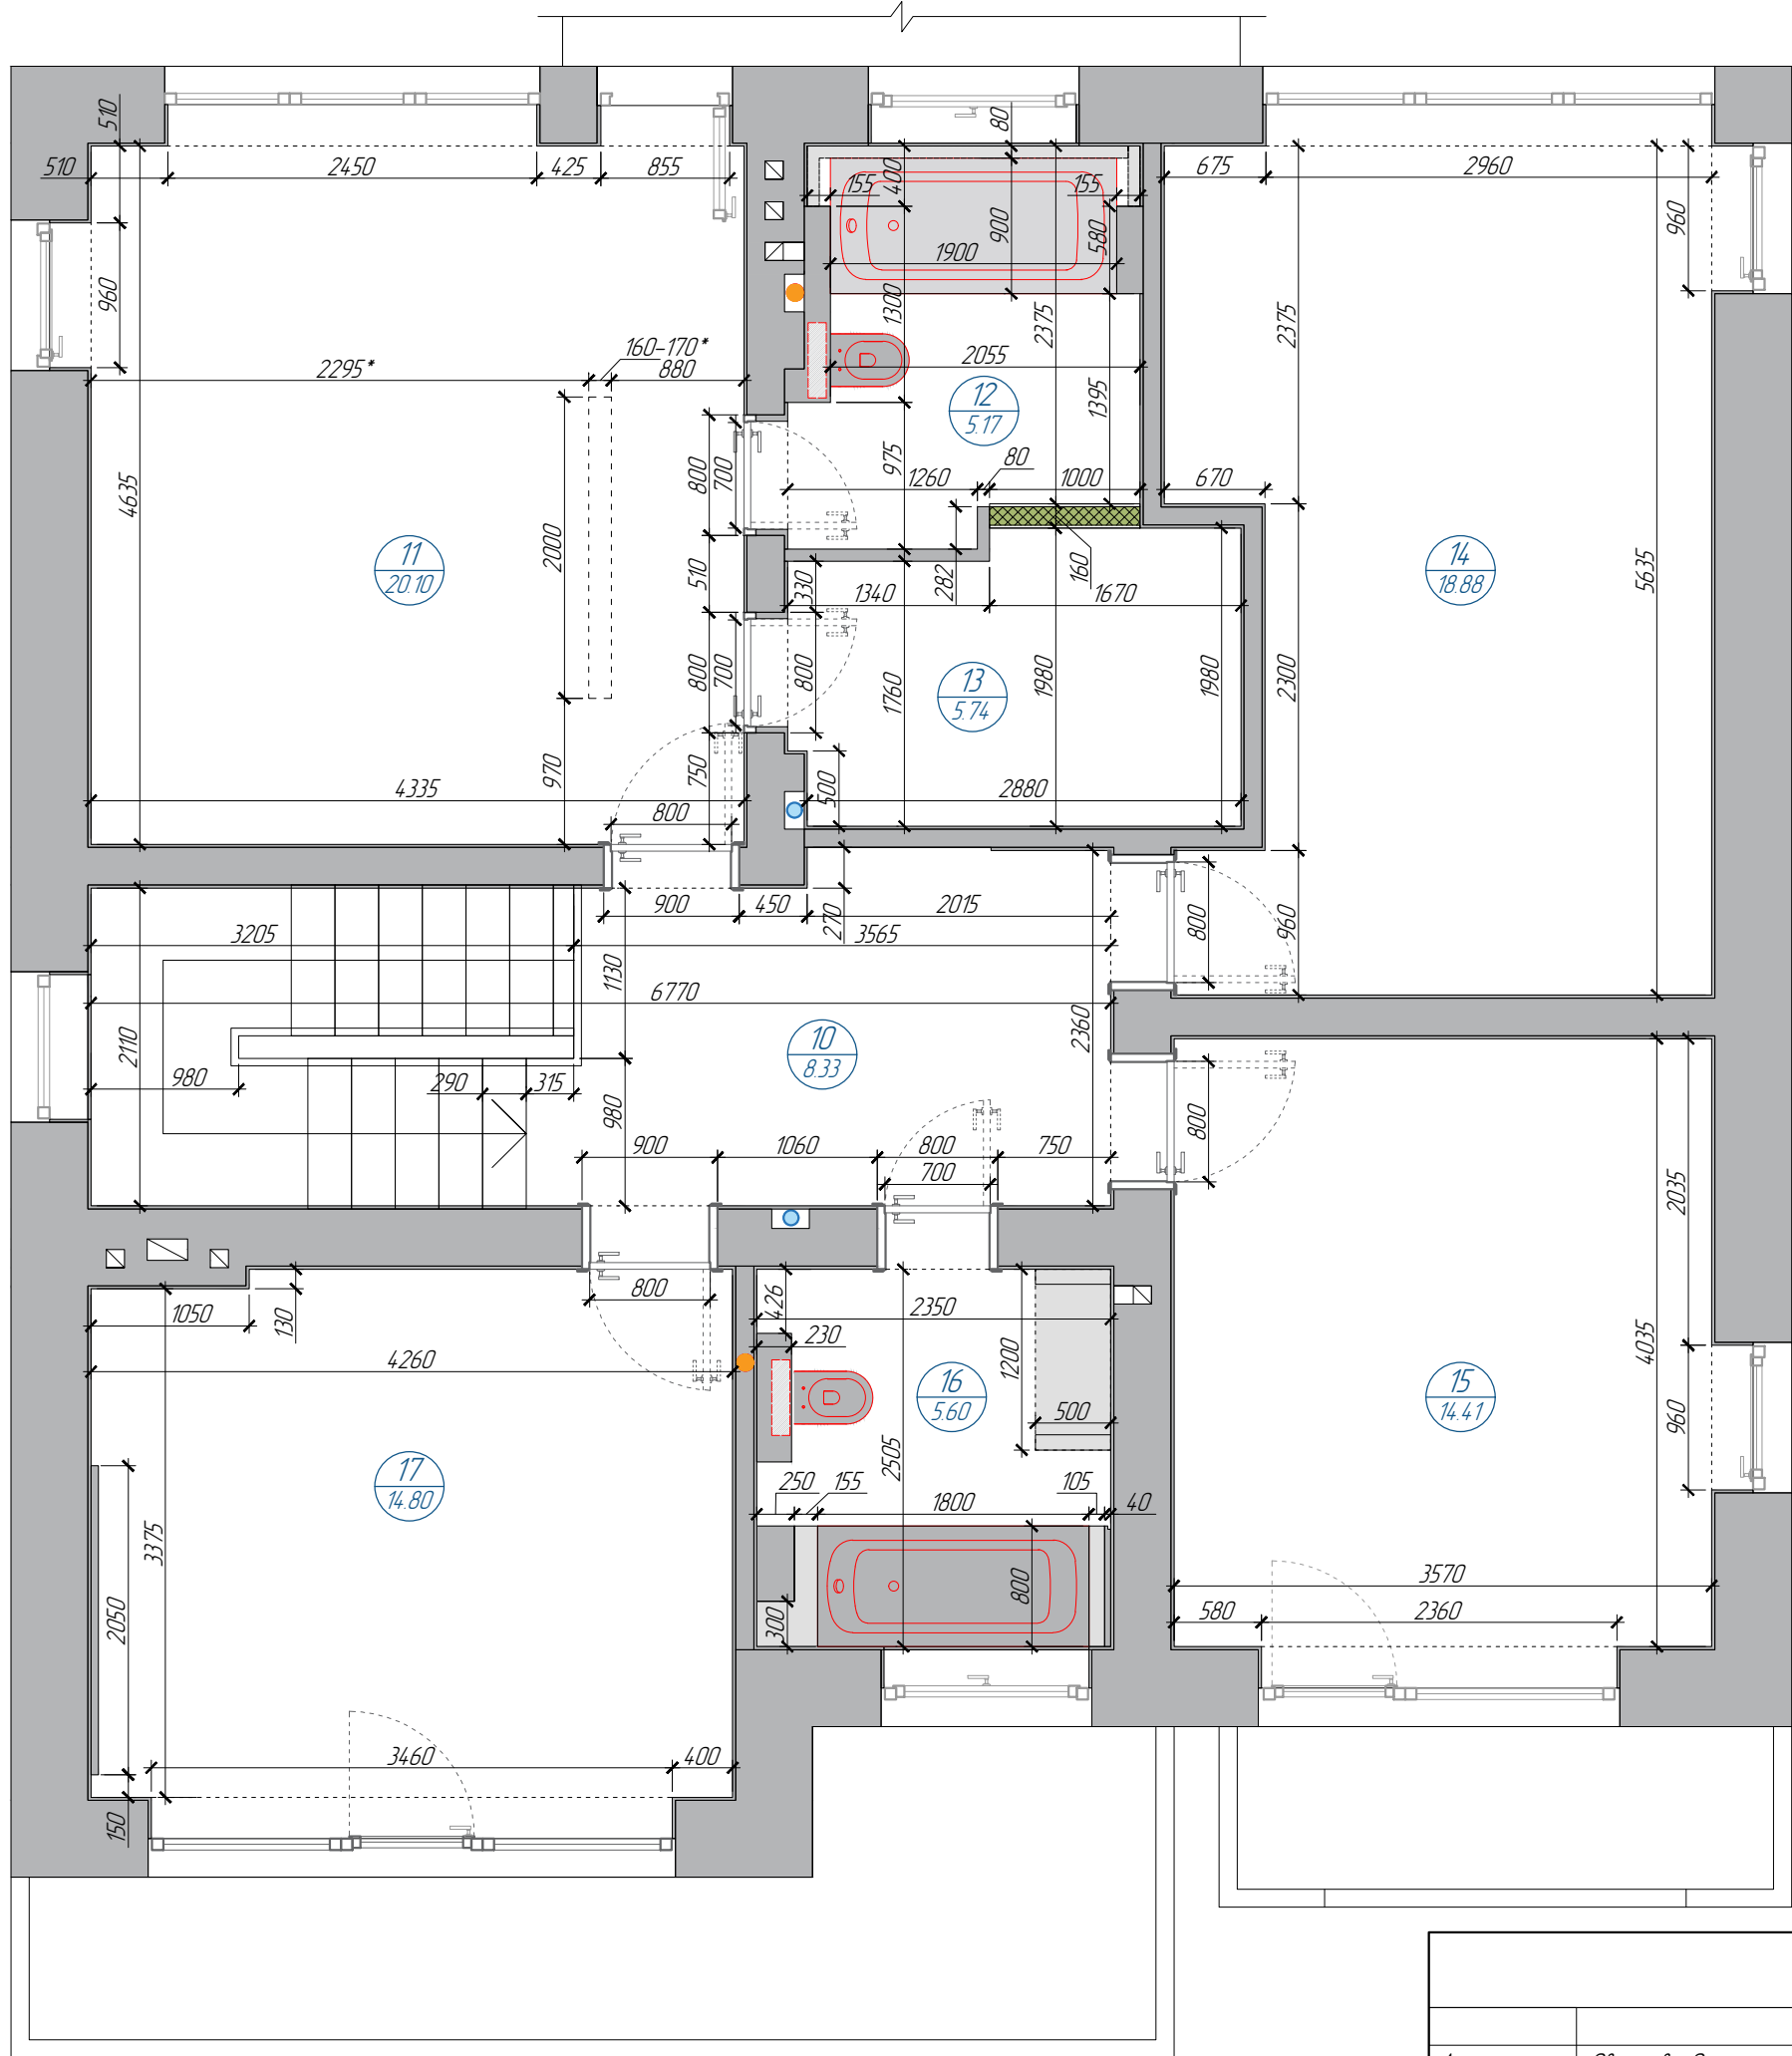

Экспликация помещений					
Этаж	№ пом.	Наименование помещения	Площадь , м ²		Примечание
			осн.	вспом.	
1	1	Прихожая		5.49	
	2	Гардеробная		3.96	
	3	Санузел гостей		3.25	
	4	Лестничный холл		12.52	
	5	Комната няни	14.40		
	6	Гостиная	32.32		
	7	Кухня –столовая	21.05		
	8	Котельная		7.31	
	9	Тех. помещение		1.76	
2	10	Лестничный холл		8.33	
	11	Мастер –спальня	20.10		
	12	Ванная комната		5.17	
	13	Гардеробная		5.74	
	14	Детская комната	18.88		
	15	Кабинет	14.41		
	16	Санузел		5.60	
	17	Гостевая комната	14.80		
		Итого по помещениям	135.96	59.13	
Общая площадь помещений дома			195.09		

УСЛОВНЫЕ ОБОЗНАЧЕНИЯ

- стены и перегородки из керамблока
- стояк канализации
- стояк ливневой канализации


кп РАЙТ ЭКО

Архитектор Овчарова Ольга

План 2 этажа

ООО ЧИПАРОВА
PROJECT

План расстановки мебели . 1 этаж

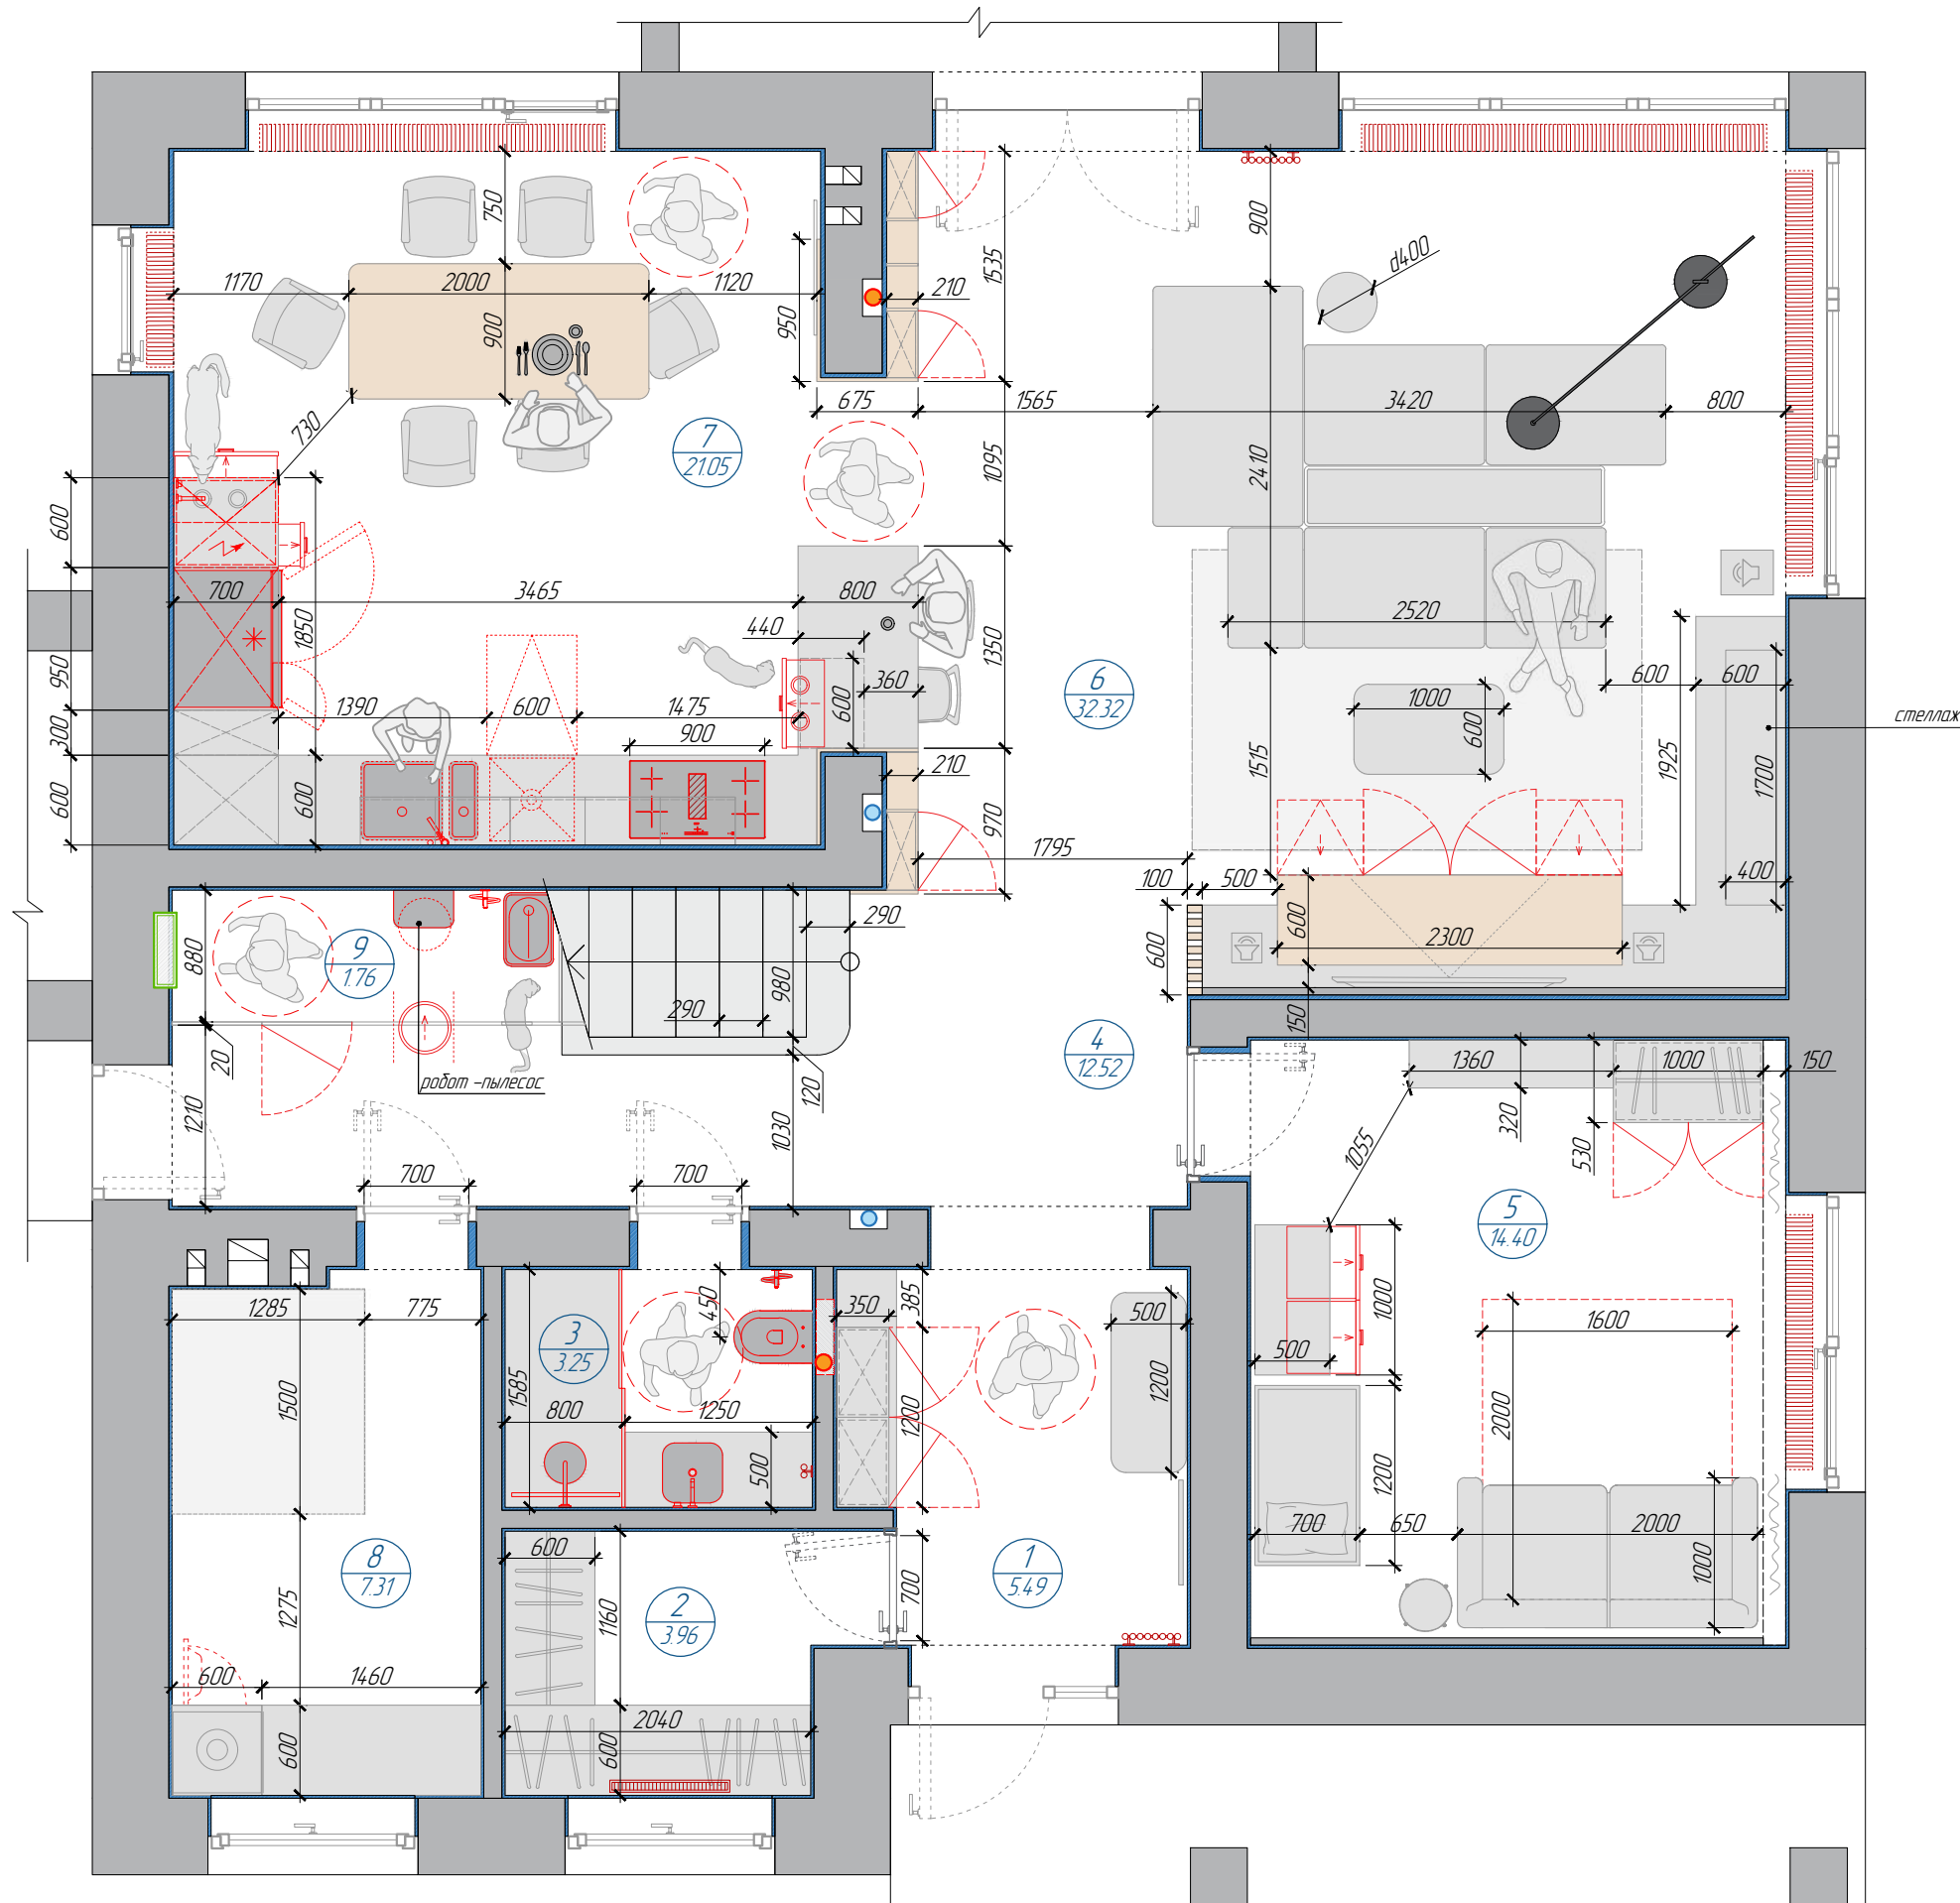

Экспликация помещений					
Этаж	№ пом.	Наименование помещения	Площадь , м ²		Примечание
			осн.	вспом.	
1	1	Прихожая		549	
	2	Гардеробная		396	
	3	Санузел гостей		325	
	4	Лестничный холл		1252	
	5	Комната няни	14.40		
	6	Гостиная	32.32		
	7	Кухня –столовая	2105		
	8	Котельная		731	
	9	Тех. помещение		176	
2	10	Лестничный холл		833	
	11	Мастер –спальня	2010		
	12	Ванная комната		517	
	13	Гардеробная		574	
	14	Детская комната	1888		
	15	Кабинет	14.41		
	16	Санузел		560	
	17	Гостевая комната	14.80		
		Итого по помещениям	135.96	59.13	
Общая площадь помещений дома			195.09		

УСЛОВНЫЕ ОБОЗНАЧЕНИЯ

- стены и перегородки из керамоблока
- стояк канализации
- стояк ливневой канализации
- штукатурный слой
- внутрипольный конвектор
- панельный радиатор
- вертикальный трубчатый радиатор
- щиты: силовой, слаботочный, для блоков led- подсветок


кп РАЙТ ЭКО

Архитектор
Овчарова Ольга

План расстановки мебели . 1 этаж

ООО ЧАРОВА
PROJECT

План расстановки мебели . 2 этаж

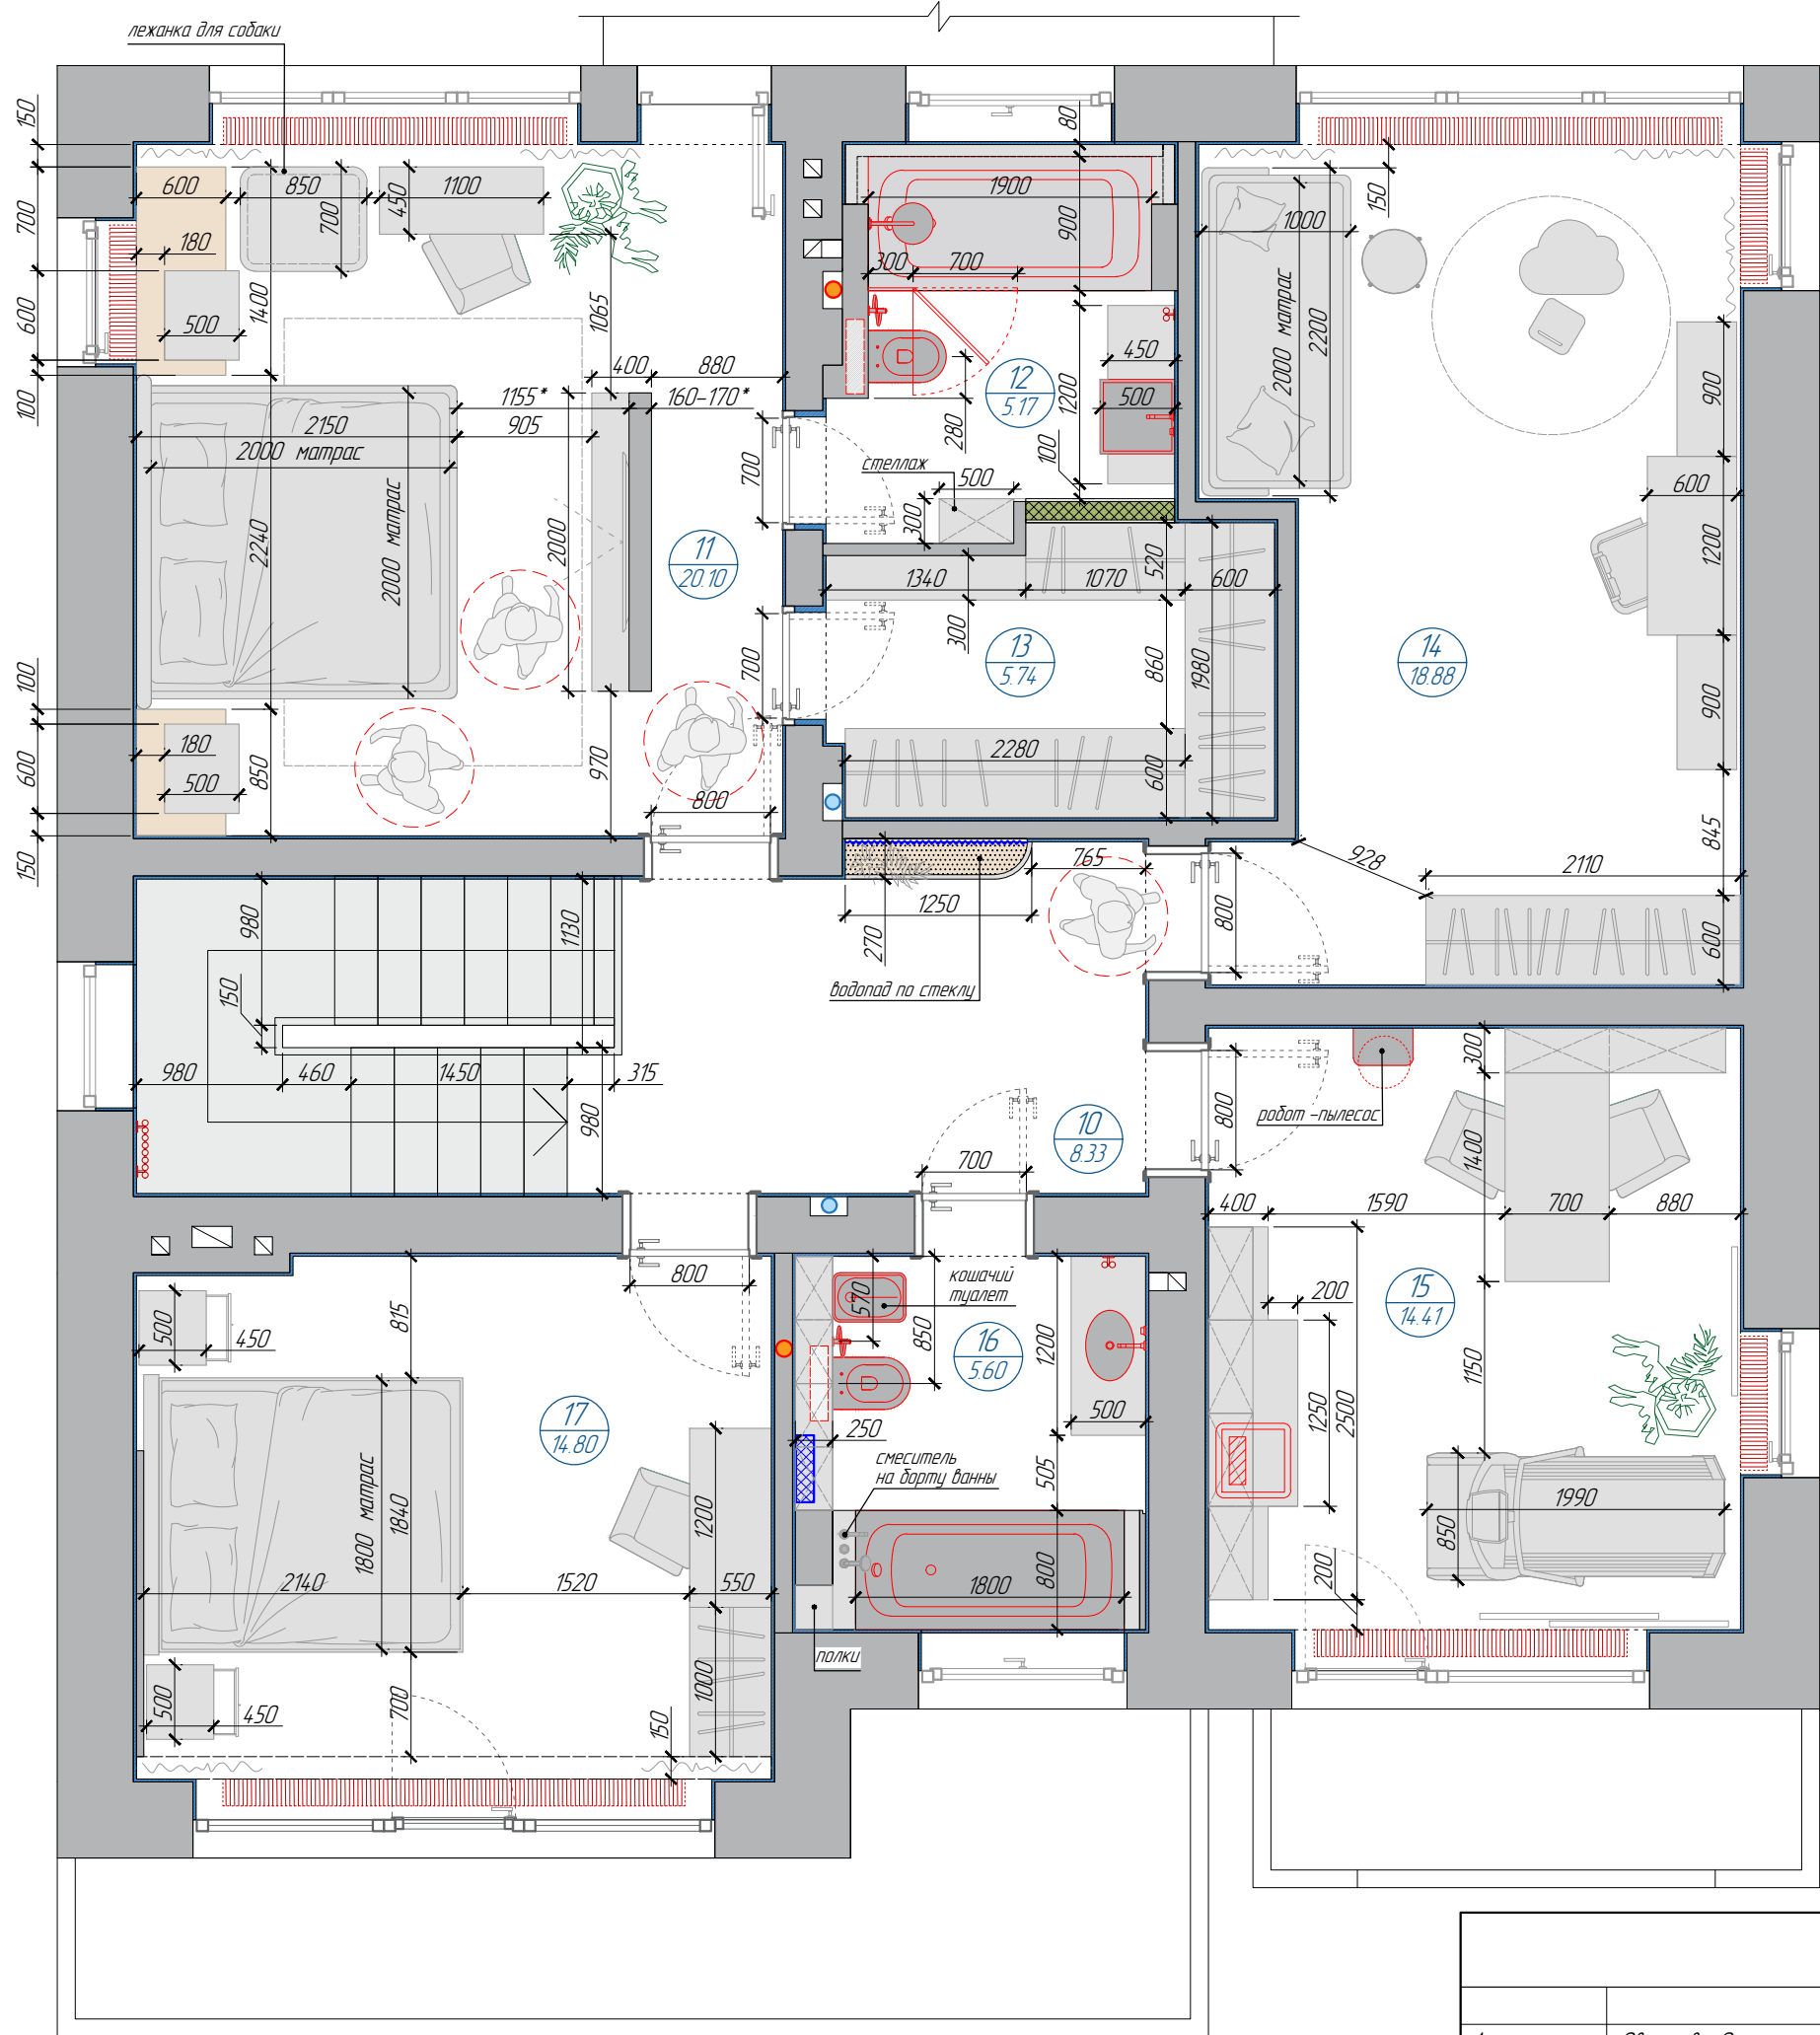

Экспликация помещений					
Этаж	№ пом.	Наименование помещения	Площадь , м ²		Примечание
			осн.	вспом.	
1	1	Прихожая		5.49	
	2	Гардеробная		3.96	
	3	Санузел гостей		3.25	
	4	Лестничный холл		12.52	
	5	Комната няни	14.40		
	6	Гостиная	32.32		
	7	Кухня –столовая	21.05		
	8	Котельная		7.31	
	9	Тех. помещение		1.76	
2	10	Лестничный холл		8.33	
	11	Мастер –спальня	20.10		
	12	Ванная комната		5.17	
	13	Гардеробная		5.74	
	14	Детская комната	18.88		
	15	Кабинет	14.41		
	16	Санузел		5.60	
	17	Гостевая комната	14.80		
		Итого по помещениям	135.96	59.13	
Общая площадь помещений дома			195.09		

УСЛОВНЫЕ ОБОЗНАЧЕНИЯ

- стены и перегородки из керамоблока
- стояк канализации
- стояк ливневой канализации
- штукатурный слой
- внутрипольный конвектор
- панельный радиатор
- вертикальный трубчатый радиатор

Схема санузла. 1 этаж



Схема санузла. 2 этаж



Схема санузла при спальне. 2 этаж




Схема ТВ-зоны в гостиной



Схема ТВ-зоны в спальне



План размещения
сантехнического оборудования.
1 эт.

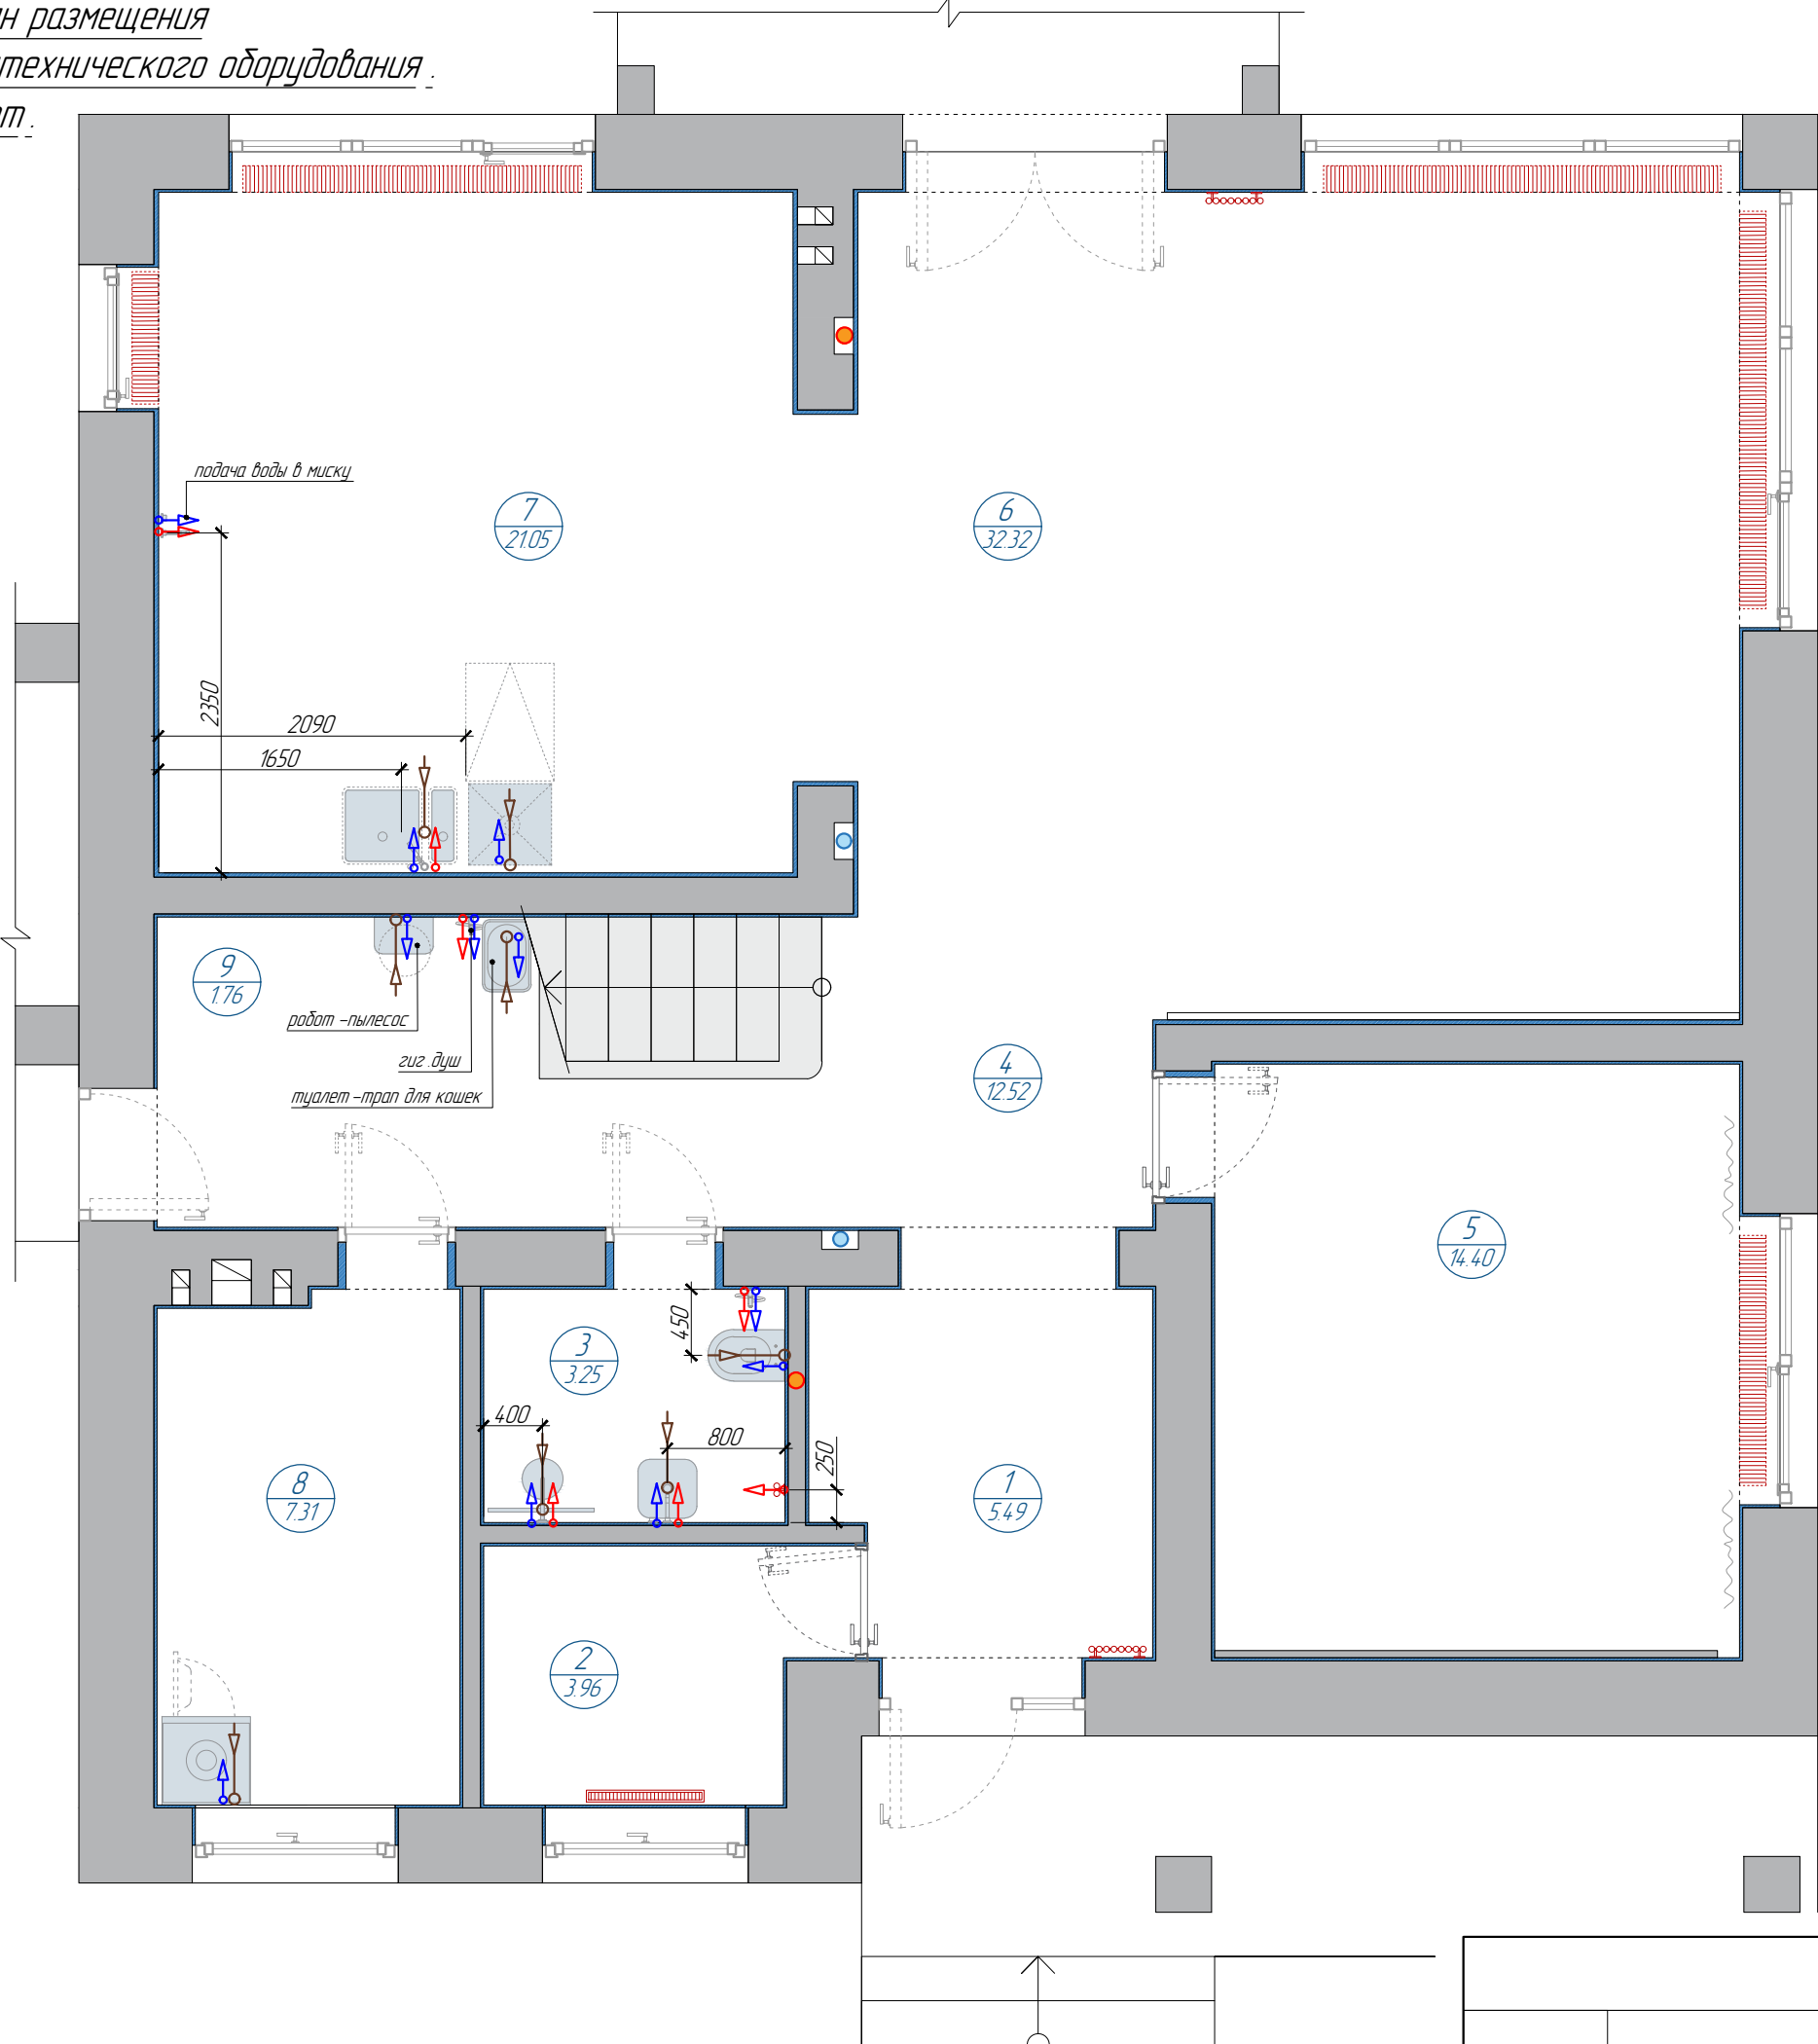

Экспликация помещений					
Этаж	№ пом.	Наименование помещения	Площадь, м²		Примечание
			осн.	вспом.	
1	1	Прихожая		549	
	2	Гардеробная		396	
	3	Санузел гостей		325	
	4	Лестничный холл		1252	
	5	Комната няни	1440		
	6	Гостиная	3232		
	7	Кухня - столовая	2105		
	8	Котельная		731	
	9	Тех. помещение		176	
2	10	Лестничный холл		833	
	11	Мастер - спальня	2010		
	12	Ванная комната		517	
	13	Гардеробная		574	
	14	Детская комната	1888		
	15	Кабинет	1441		
	16	Санузел		560	
	17	Гостевая комната	1480		
Итого по помещениям			13596	5913	
Общая площадь помещений дома			19509		


УСЛОВНЫЕ ОБОЗНАЧЕНИЯ

- стены и перегородки из керамоблока
- стояк канализации
- стояк ливневой канализации
- штукатурный слой
- внутрипольный конвектор
- панельный радиатор
- вертикальный трубчатый радиатор
- подводка холодной воды
- подводка горячей воды
- вывод канализации

ПРИМЕЧАНИЯ

- Любые расхождения проектных размеров с фактическими, нестыковки, изменение конструктивных решений согласовывать с автором проекта в рамках авторского надзора
- Подводку к оборудованию осуществлять строго в соответствии с техническими картами купленного оборудования

План размещения
сантехнического оборудования.
2 эт.

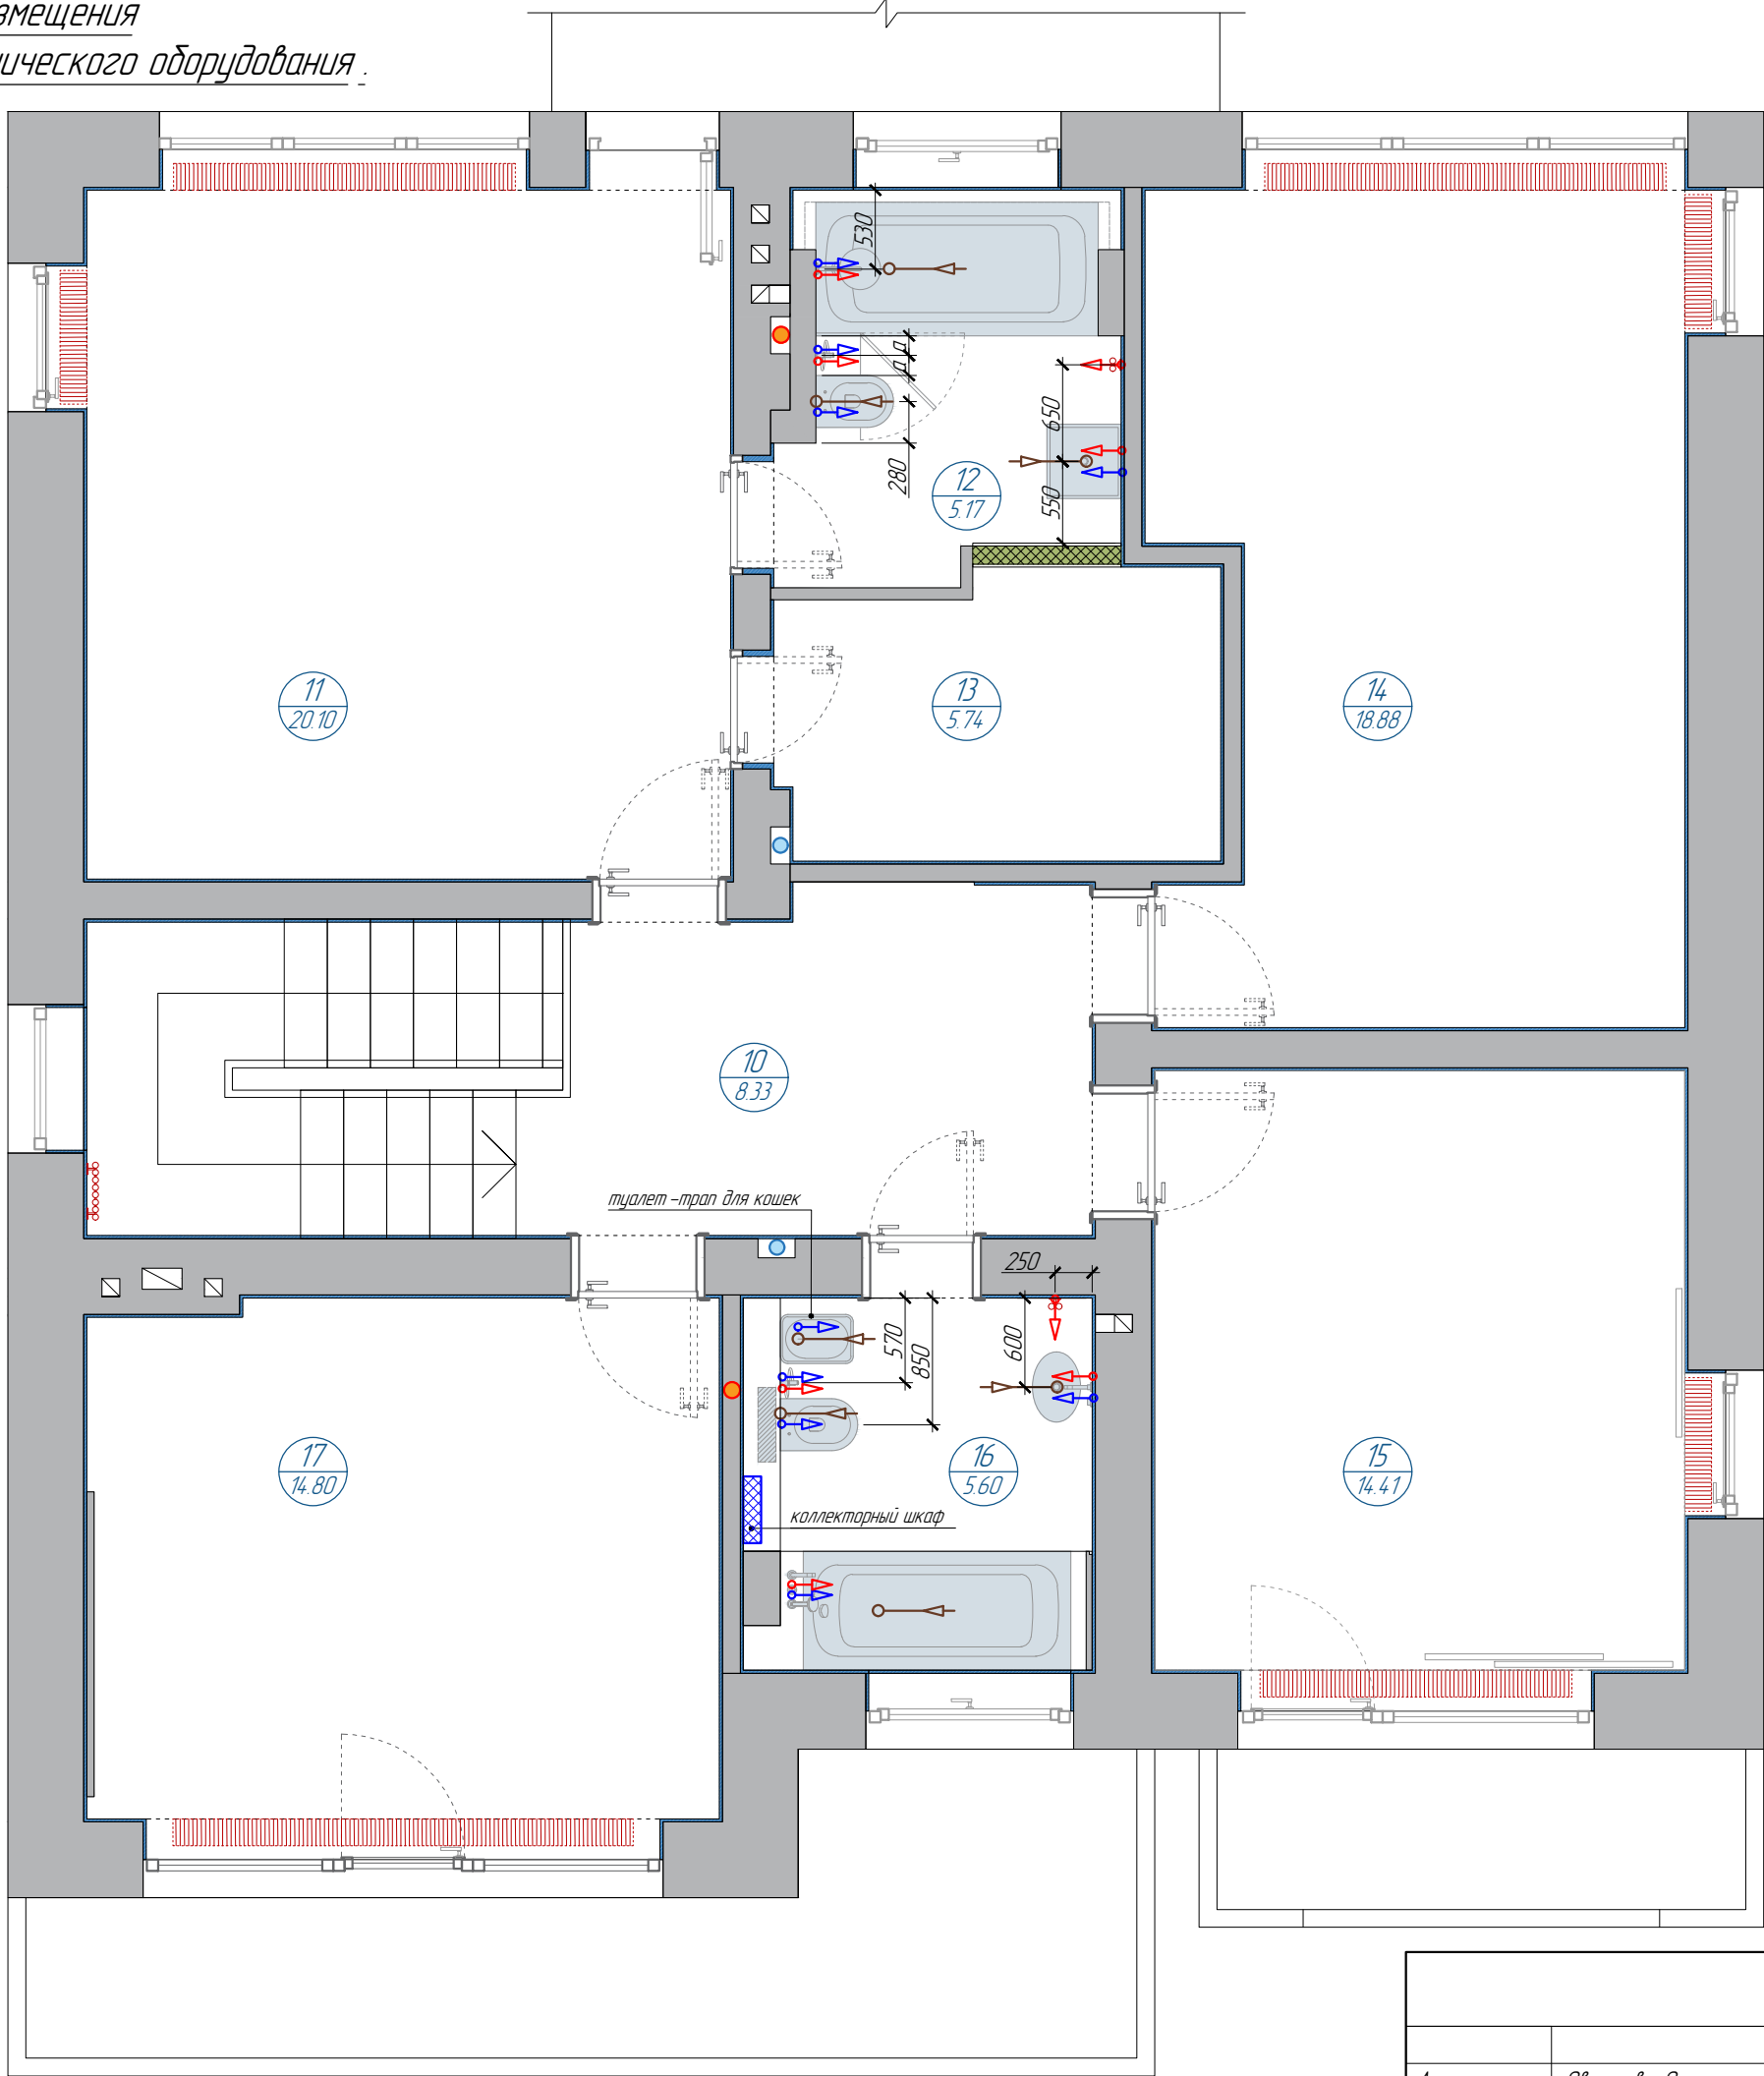

Экспликация помещений					
Этаж	№ пом.	Наименование помещения	Площадь , м ²		Примечание
			осн.	вспом.	
1	1	Прихожая		5.49	
	2	Гардеробная		3.96	
	3	Санузел гостей		3.25	
	4	Лестничный холл		12.52	
	5	Комната няни	14.40		
	6	Гостиная	32.32		
	7	Кухня –столовая	21.05		
	8	Котельная		7.31	
	9	Тех. помещение		1.76	
2	10	Лестничный холл		8.33	
	11	Мастер –спальня	20.10		
	12	Ванная комната		5.17	
	13	Гардеробная		5.74	
	14	Детская комната	18.88		
	15	Кабинет	14.41		
	16	Санузел		5.60	
	17	Гостевая комната	14.80		
		Итого по помещениям	135.96	59.13	
Общая площадь помещений дома			195.09		

УСЛОВНЫЕ ОБОЗНАЧЕНИЯ


- стены и перегородки из керамоблока
- стояк канализации
- стояк ливневой канализации
- штукатурный слой
- внутрипольный конвектор
- панельный радиатор
- вертикальный трубчатый радиатор
- подводка холодной воды
- подводка горячей воды
- вывод канализации

ПРИМЕЧАНИЯ

- Любые расхождения проектных размеров с фактическими, нестыковки, изменение конструктивных решений согласовывать с автором проекта в рамках авторского надзора
- Подводку к оборудованию осуществлять строго в соответствии с техническими картами купленного оборудования

План размещения электрооборудования

1 этаж

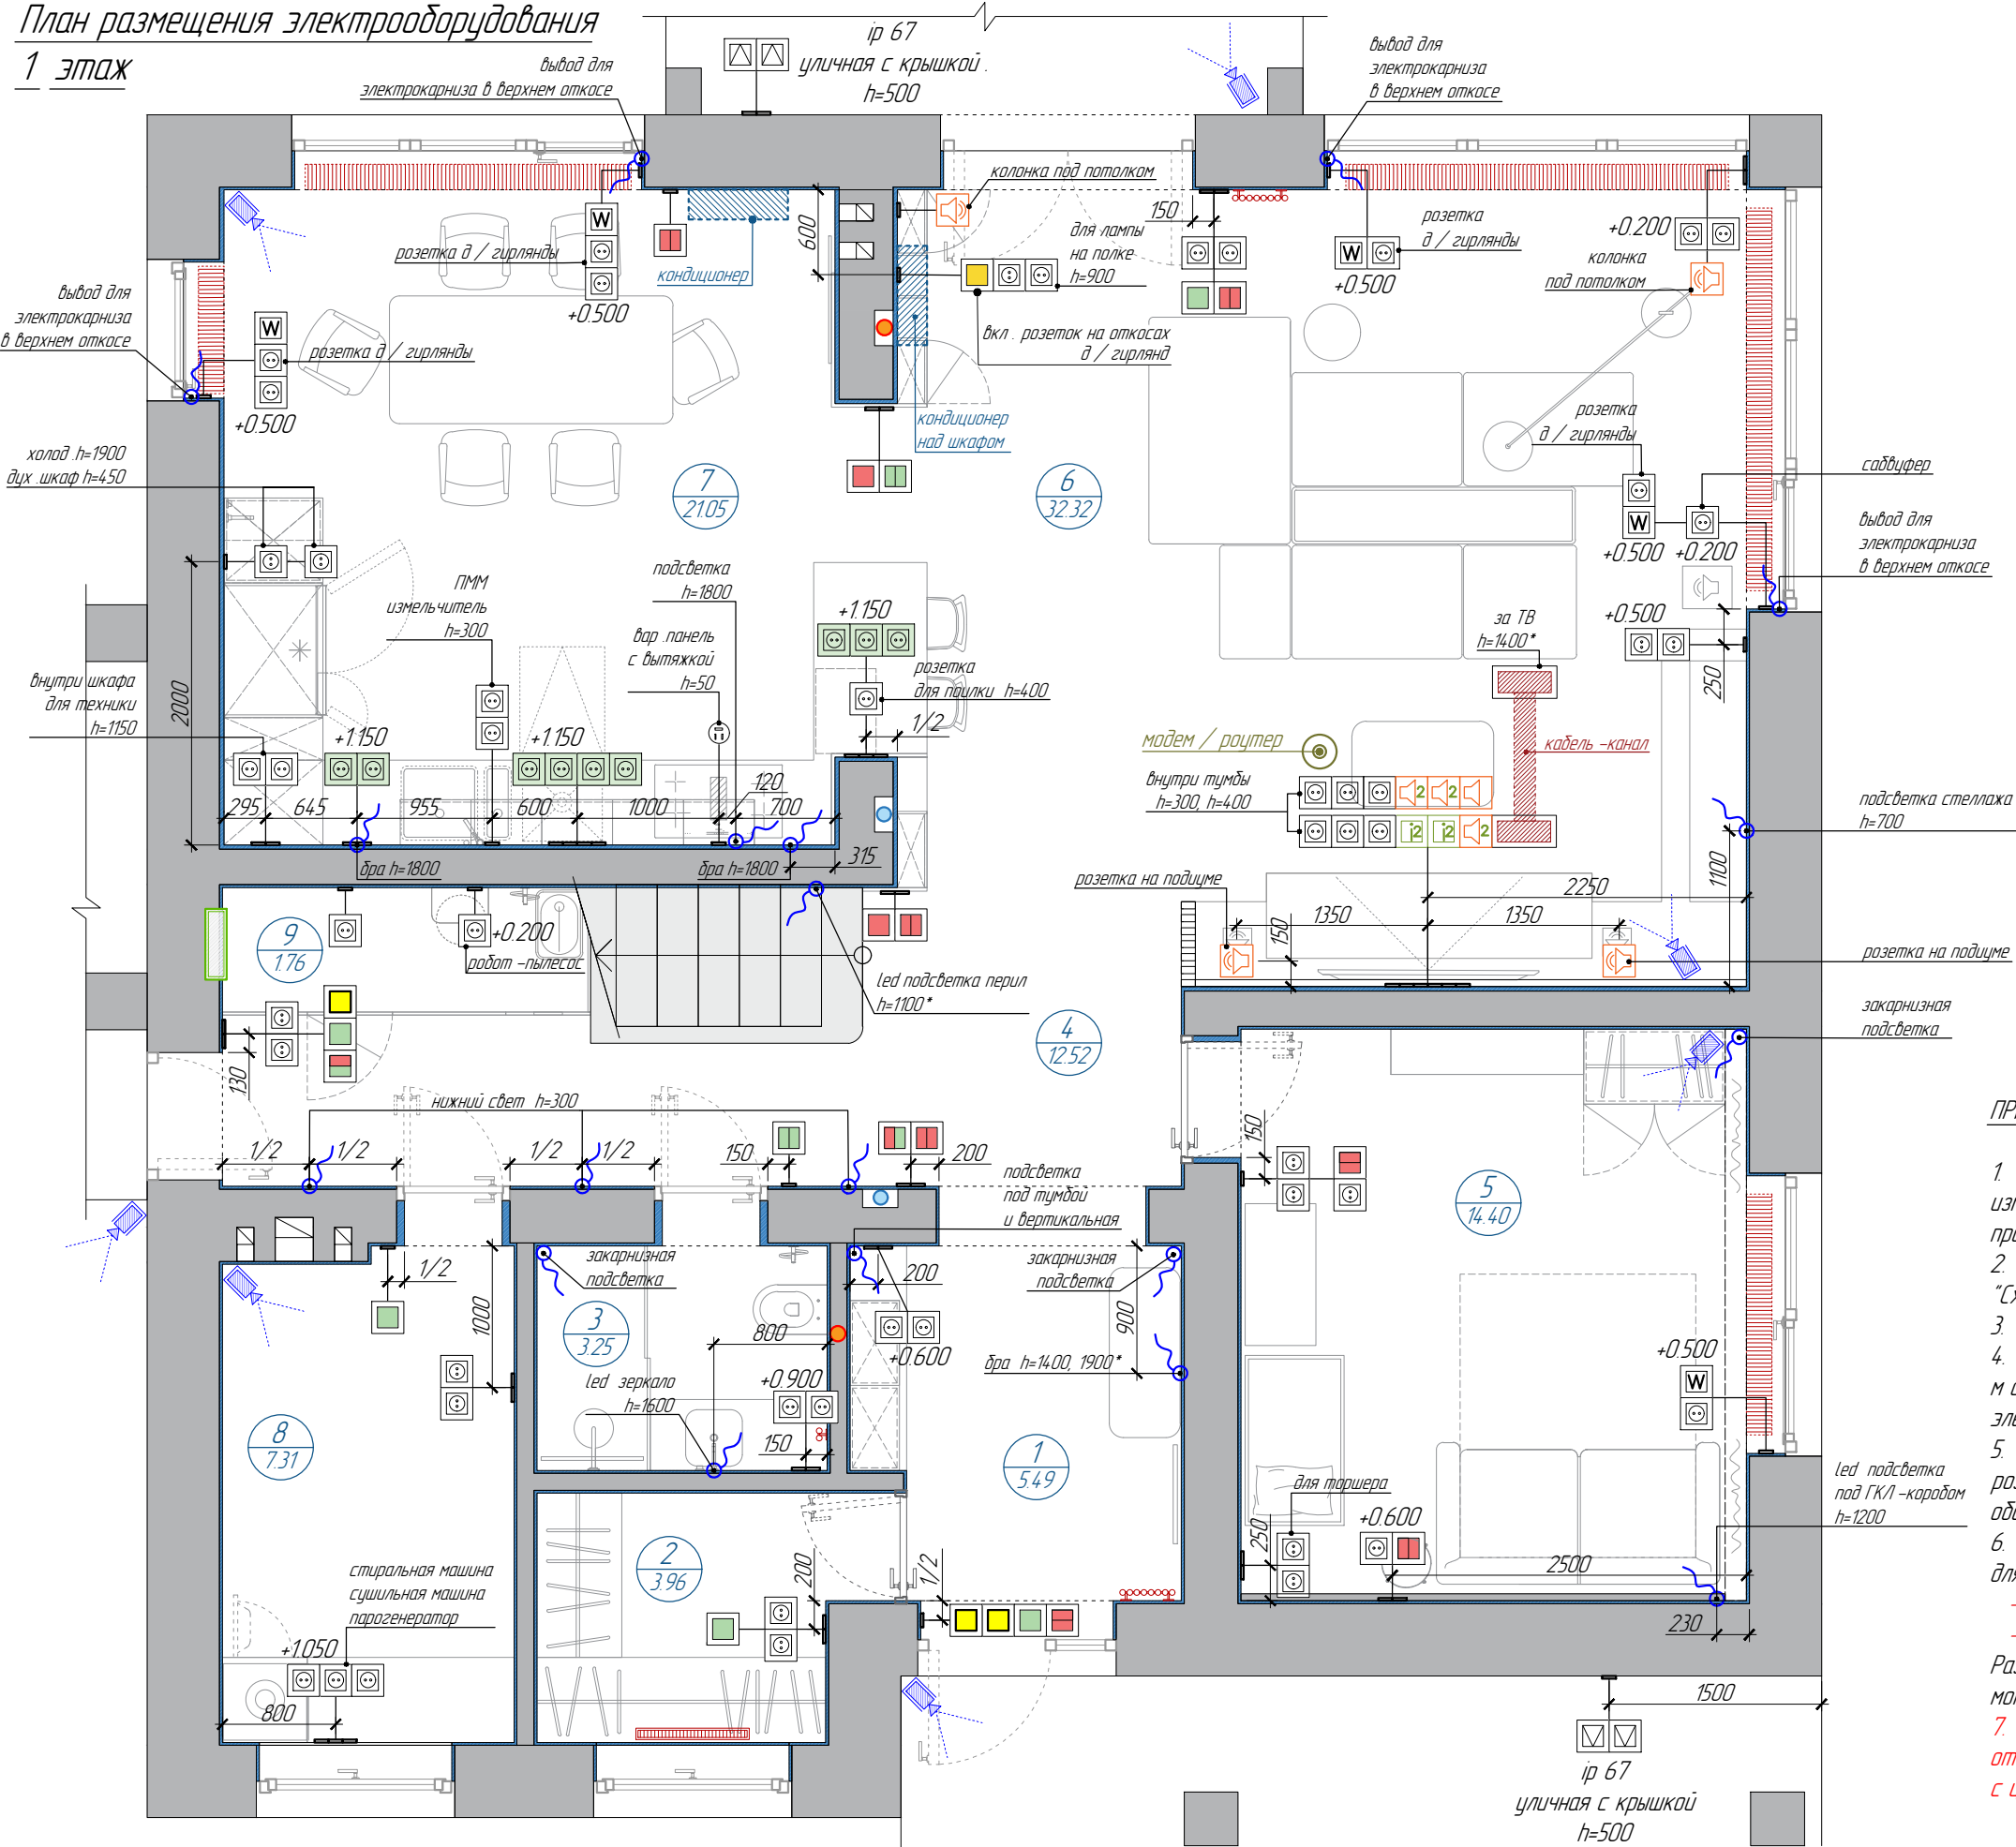


УСЛОВНЫЕ ОБОЗНАЧЕНИЯ	
	штепсельная розетка для скрытой установки
	штепсельная розетка для скрытой установки над столешницей
	штепсельная розетка для скрытой установки с крышкой
	терморегулятор внутрипольного конвектора
	кабель - канал
	розетка RG-45
	щиток
	модем, роутер
	вывод провода для прямого подключения
	выключатель одноклавишный
	выключатель двухклавишный
	переключатель одноклавишный
	переключатель двухклавишный
	выключатель одноклавишный (к нему запитана розетка для гирлянды)
	контрольный выключатель (на весь свет)
	потолочная точка доступа wi-fi
	камера видеонаблюдения

ПРИМЕЧАНИЯ

- Любые расхождения проектных размеров с фактическими, нестыковки, изменение конструктивных решений и т.п. согласовывать с автором проекта в рамках авторского надзора
 - Данный лист смотреть совместно с листами "Схема размещения групп светильников с привязкой к выключателям"
 - Высоты указаны от отметки чистого пола 0.000
 - Все розетки располагать на высоте 0.3 м, а выключатели на высоте 0.9 м от уровня чистого пола до оси электроприбора или группы электроприборов, если не указано иное
 - К выключателям для праздничного освещения (гирлянд) запитываются розетки на откосах, предназначенные для подключения светового оборудования
 - На этапе разводки электрики предусмотреть выводы для системы кондиционирования, а также:
 - видеонаблюдения
 - охранной сигнализации
- Размещение выводов выполнить согласно предписаниям от организаций, монтирующих данные системы
7. Для выключателей, расположенных в непосредственной близости от радиаторов отопления, обеспечить изоляцию силовых кабелей с целью исключения нагрева электрооборудования

План размещения электрооборудования

2 этаж

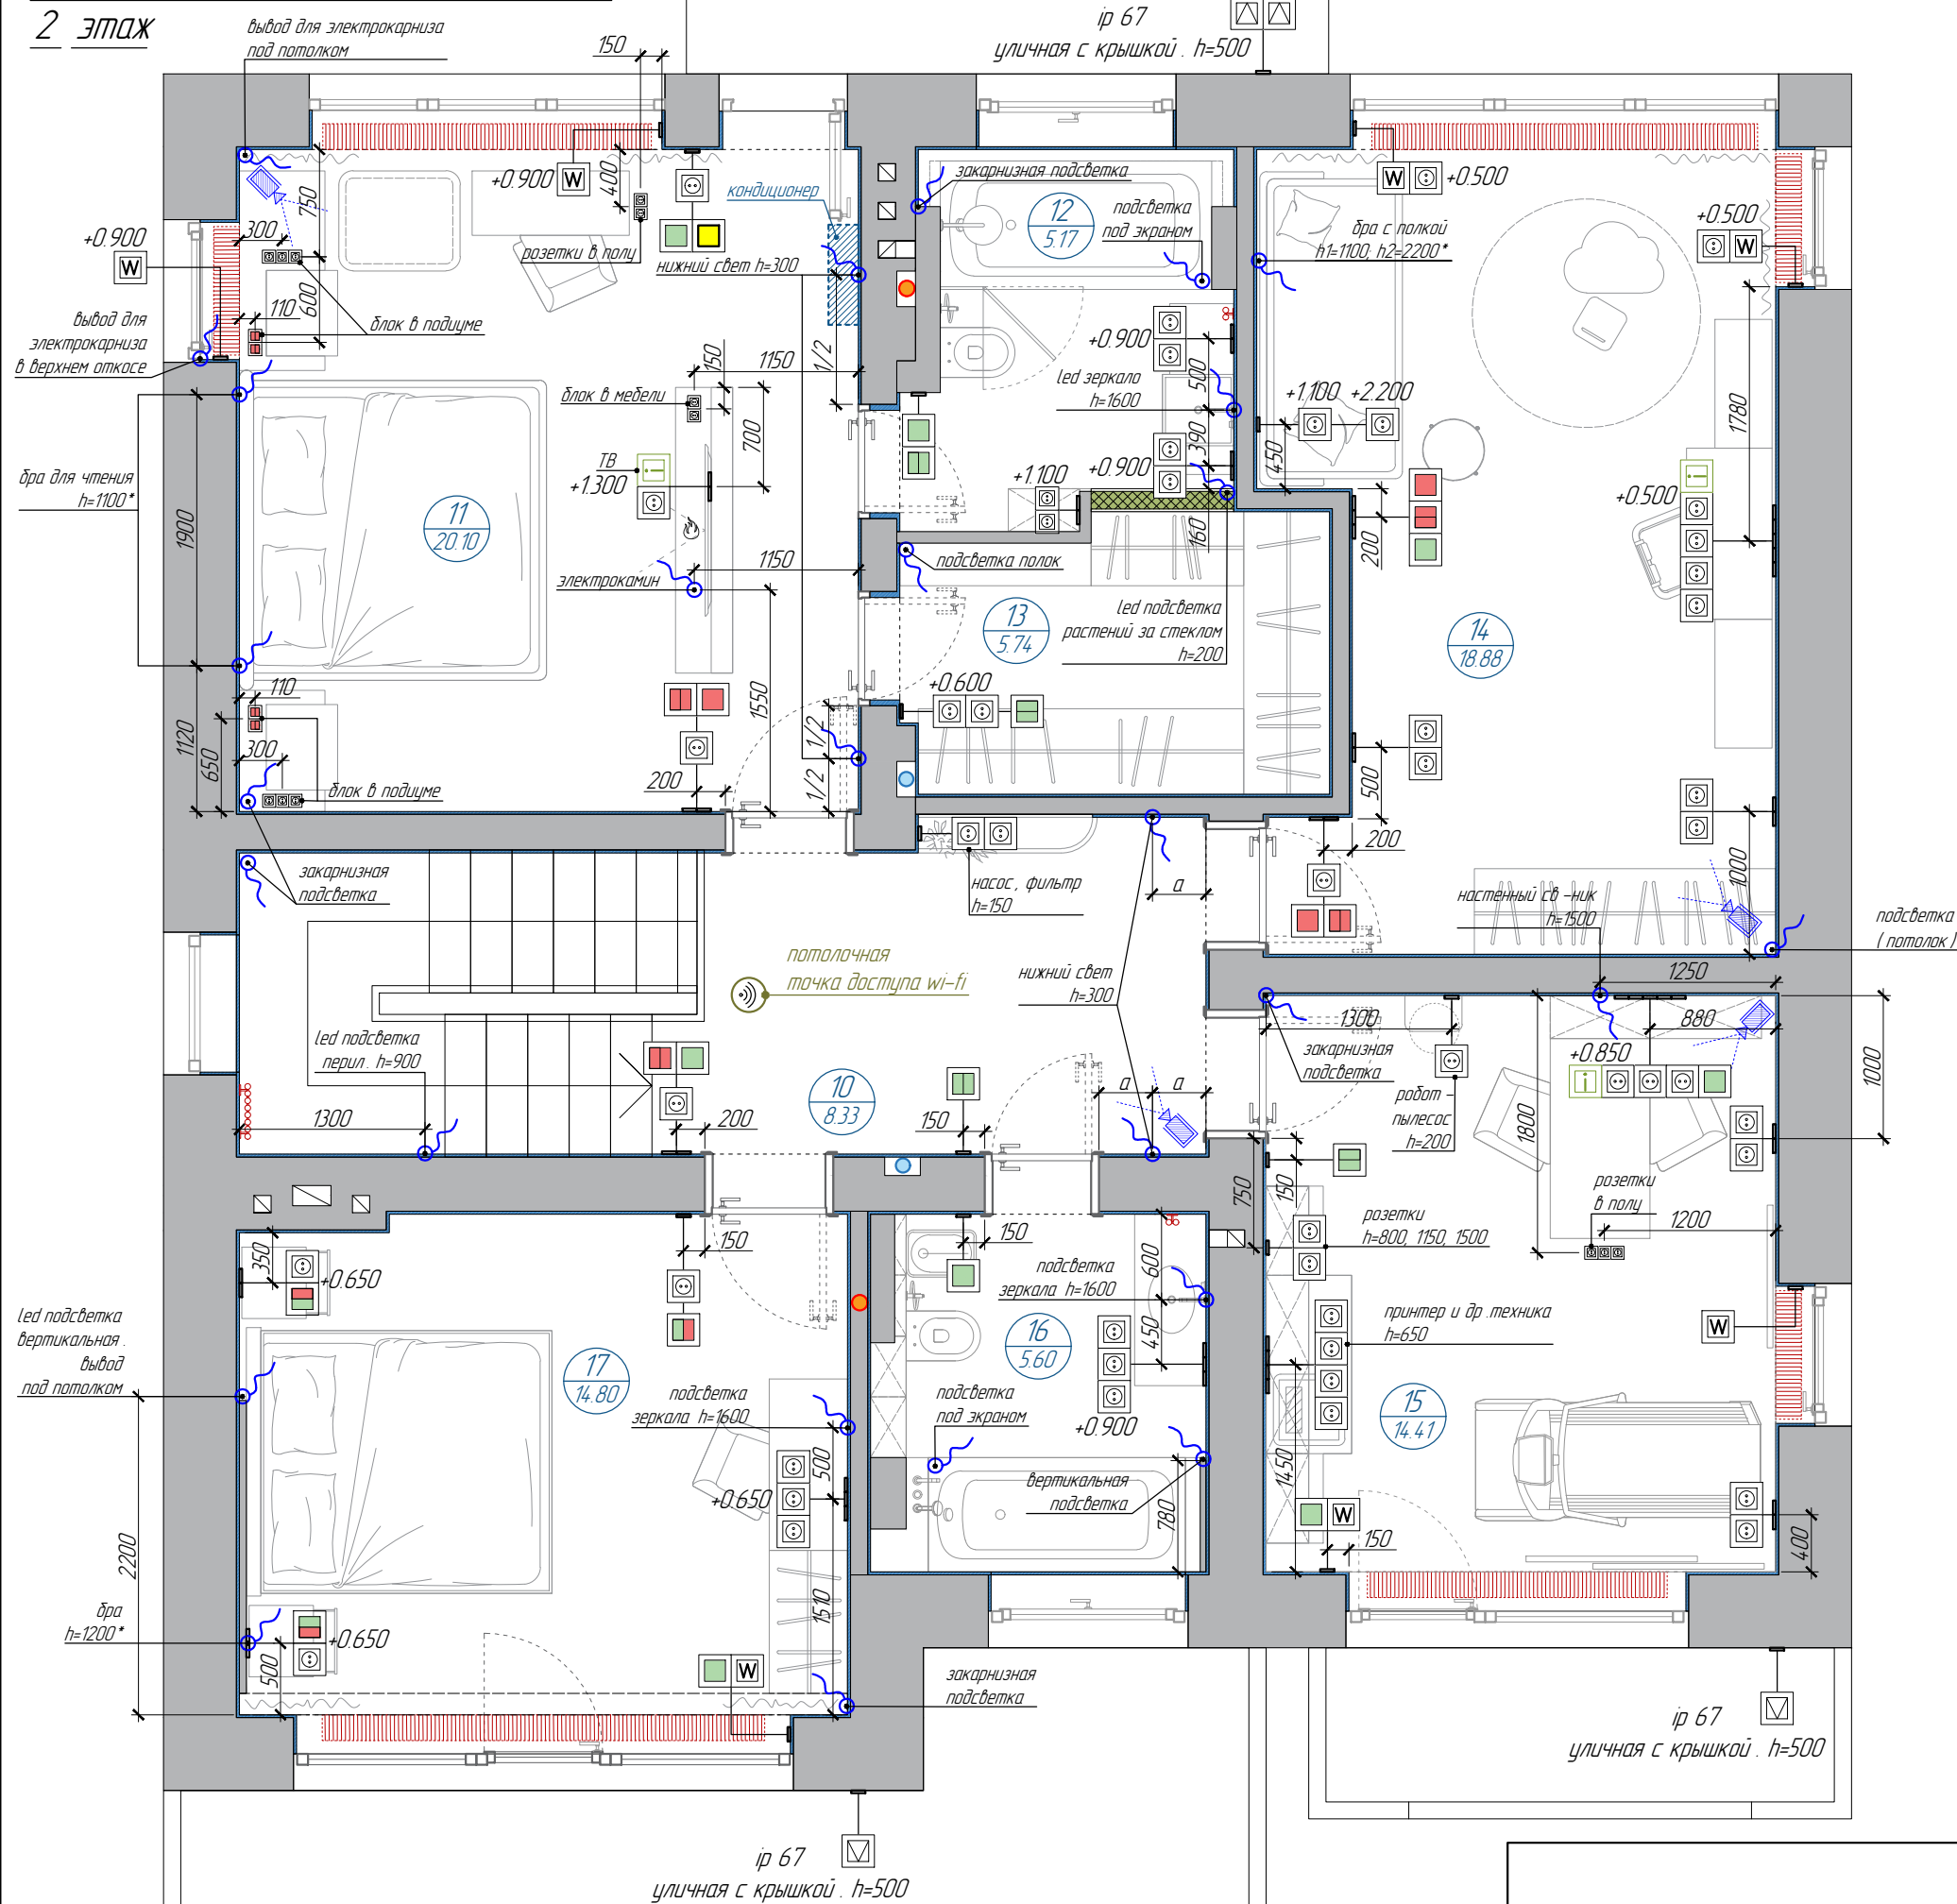


УСЛОВНЫЕ ОБОЗНАЧЕНИЯ	
	штепсельная розетка для скрытой установки
	штепсельная розетка для скрытой установки над столешницей
	штепсельная розетка для скрытой установки С КРЫШКОЙ
	терморегулятор внутрипольного конвектора
	кабель -канал
	розетка RG-45
	щиток
	модем, роутер
	вывод провода для прямого подключения
	выключатель одноклавишный
	выключатель двухклавишный
	переключатель одноклавишный
	переключатель двухклавишный
	выключатель одноклавишный (к нему запитана розетка для гирлянды)
	контрольный выключатель (на весь свет)
	потолочная точка доступа wi-fi
	камера видеонаблюдения

ПРИМЕЧАНИЯ

- Любые расхождения проектных размеров с фактическими, нестыковки, изменение конструктивных решений и т.п. согласовывать с автором проекта в рамках авторского надзора
 - Данный лист смотреть совместно с листами "Схема размещения групп светильников с привязкой к выключателям"
 - Высоты указаны от отметки чистого пола 0.000
 - Все розетки располагать на высоте 0.3 м, а выключатели на высоте 0.9 м от уровня чистого пола до оси электроприбора или группы электроприборов, если не указано иное
 - К выключателям для праздничного освещения (гирлянд) запитываются розетки на откосах, предназначенные для подключения светового оборудования
 - На этапе разводки электрики предусмотреть выводы для системы кондиционирования, а также:
 - видеонаблюдения
 - охранной сигнализации
- Размещение выводов выполнить согласно предписаниям от организаций, монтирующих данные системы
7. Для выключателей, расположенных в непосредственной близости от радиаторов отопления, обеспечить изоляцию силовых кабелей с целью исключения нагрева электрооборудования

Схема освещения . 1 этаж

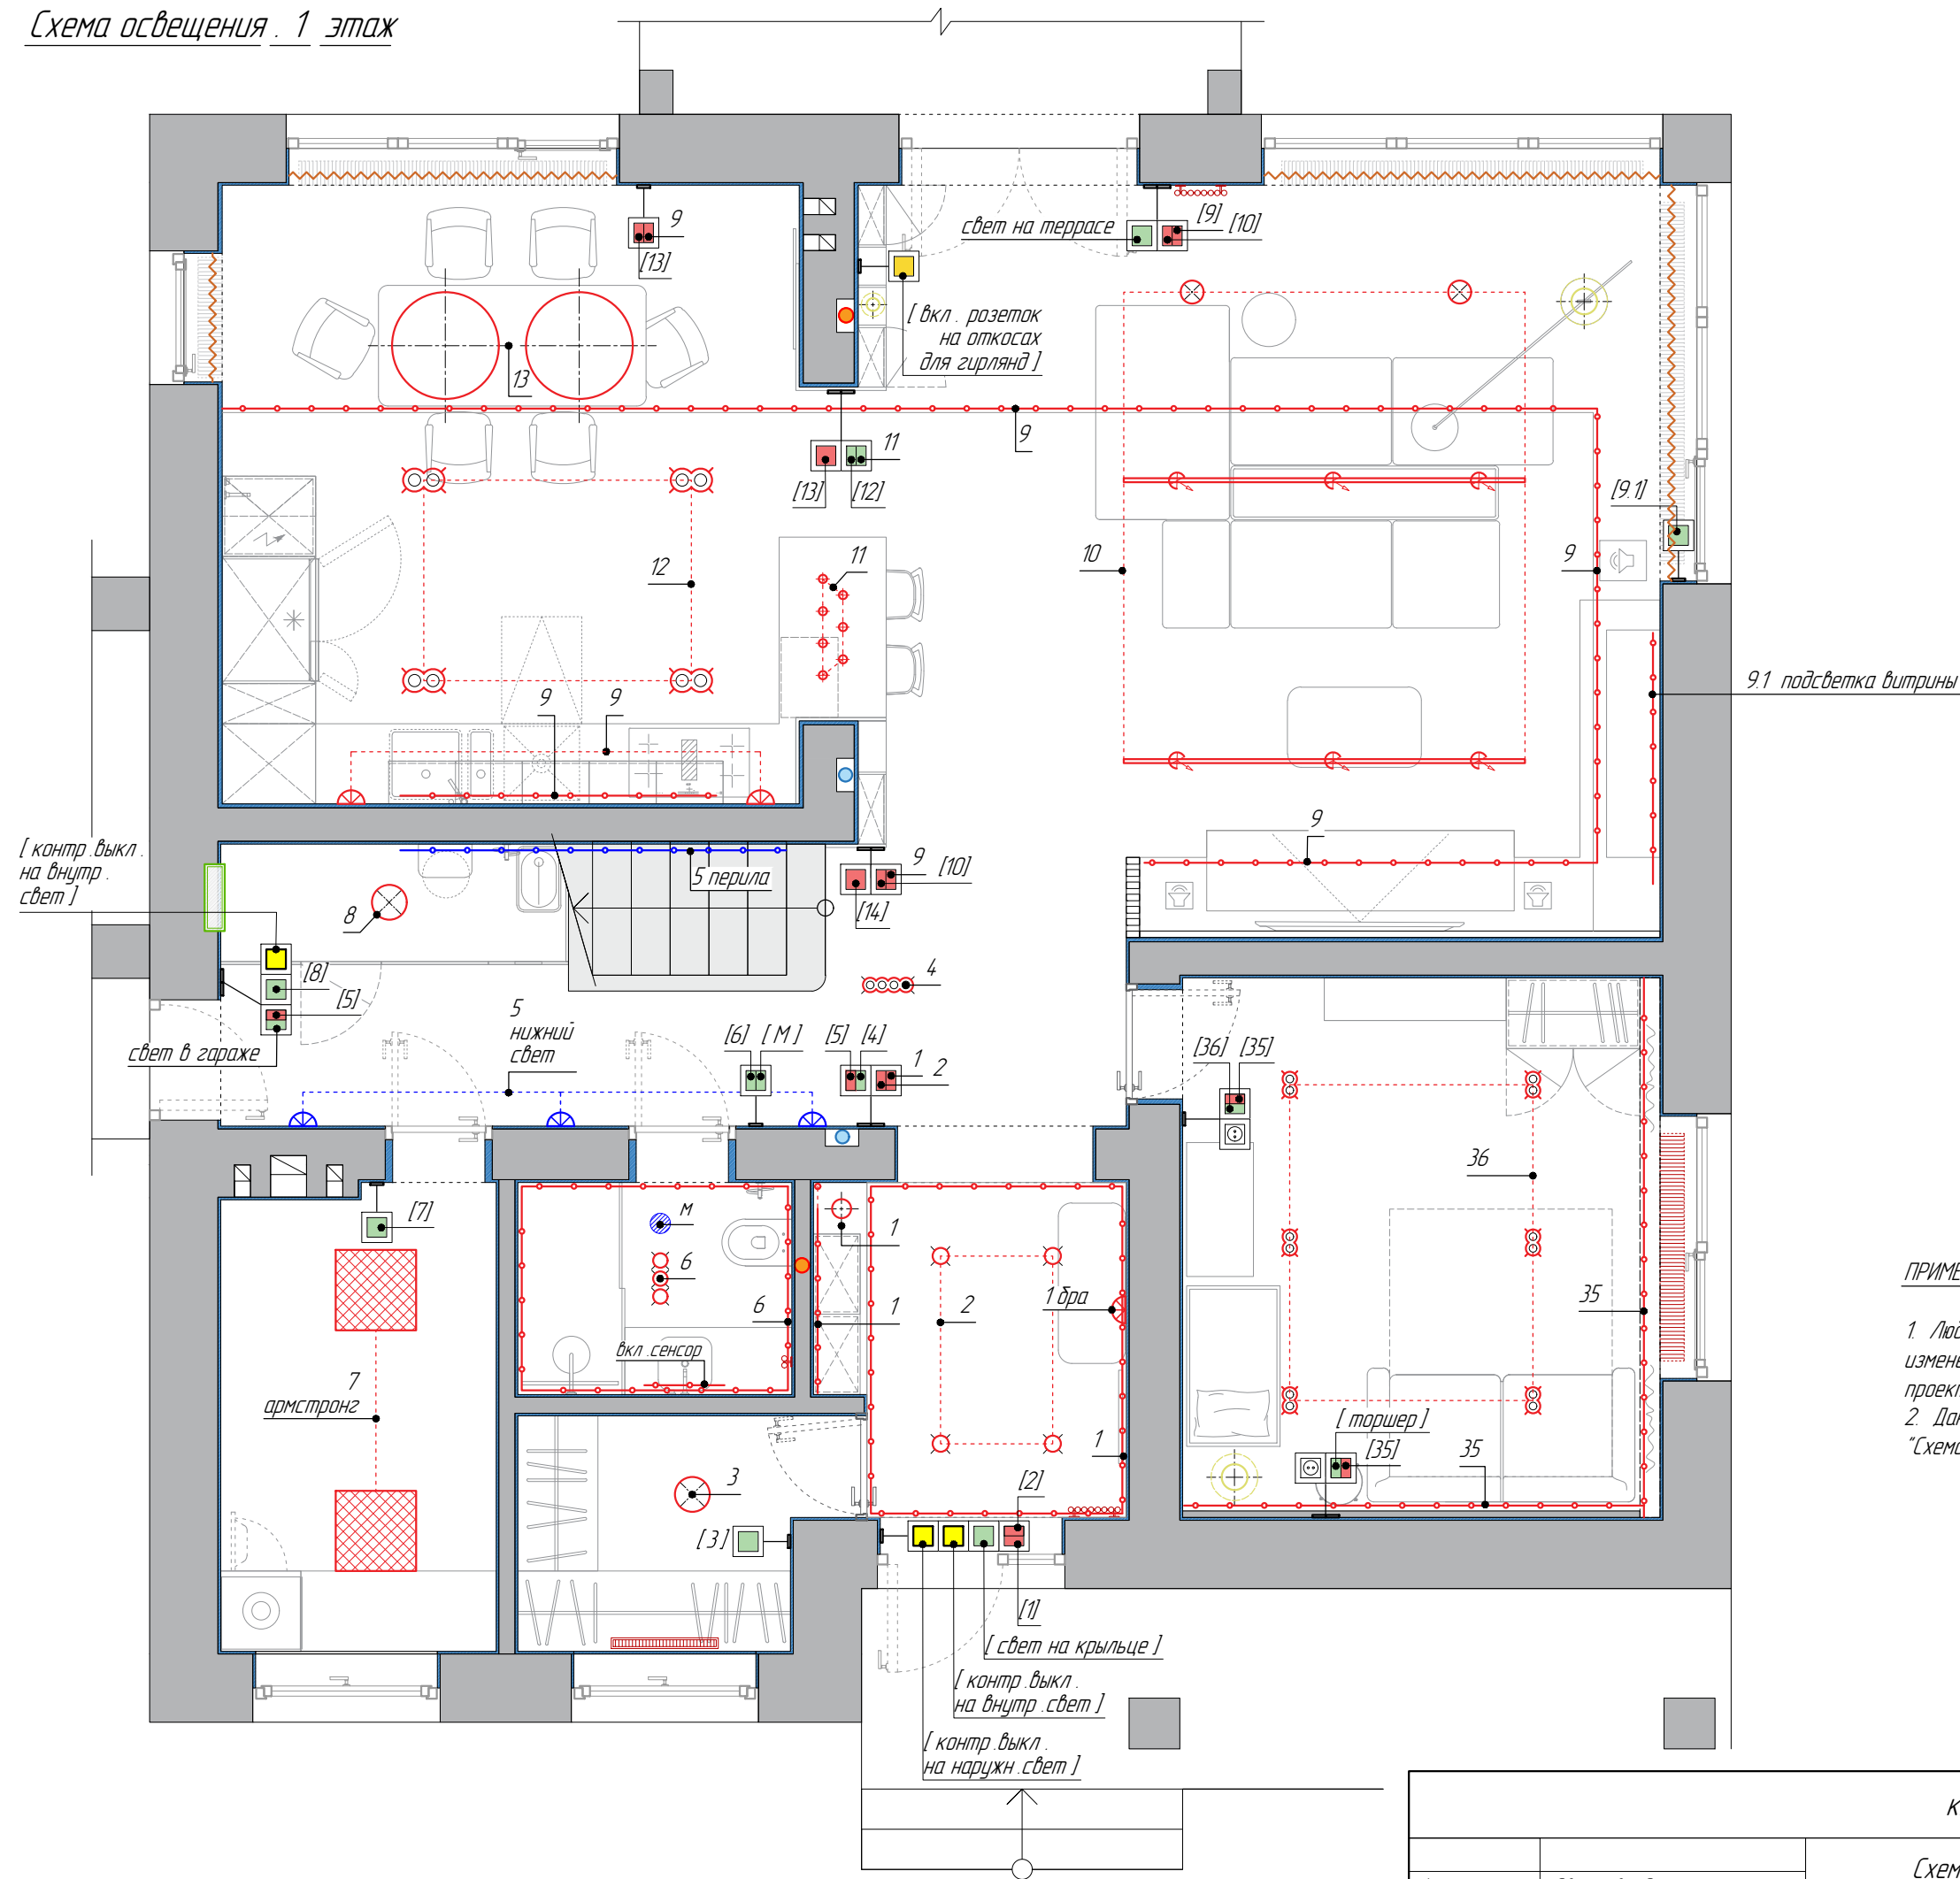

	УСЛОВНЫЕ ОБОЗНАЧЕНИЯ
	электровентилятор
	люстра/подвесной св-ник
	потолочный накладной светильник
	потолочный встраиваемый св-ник
	потолочный встраиваемый св-ник двойной
	настенный светильник (бра)
	трековый светильник
	led подсветка
	гирлянда
	выключатель одноклавишный
	выключатель двухклавишный
	выключатель проходной
	выключатель проходной двухклавишный
	напольный / настольный светильник
	контрольный выключатель

ПРИМЕЧАНИЯ


- Любые расхождения проектных размеров с фактическими, нестыковки, изменение конструктивных решений и т.п., согласовывать с автором проекта в рамках авторского надзора
- Данный лист смотреть совместно с листами "Схема размещения электрооборудования" и "Схема потолка"

кп РАЙТ ЭКО

Архитектор Овчарова Ольга

Схема освещения . 1 этаж

ООО ЧИПАРОВА
PROJECT

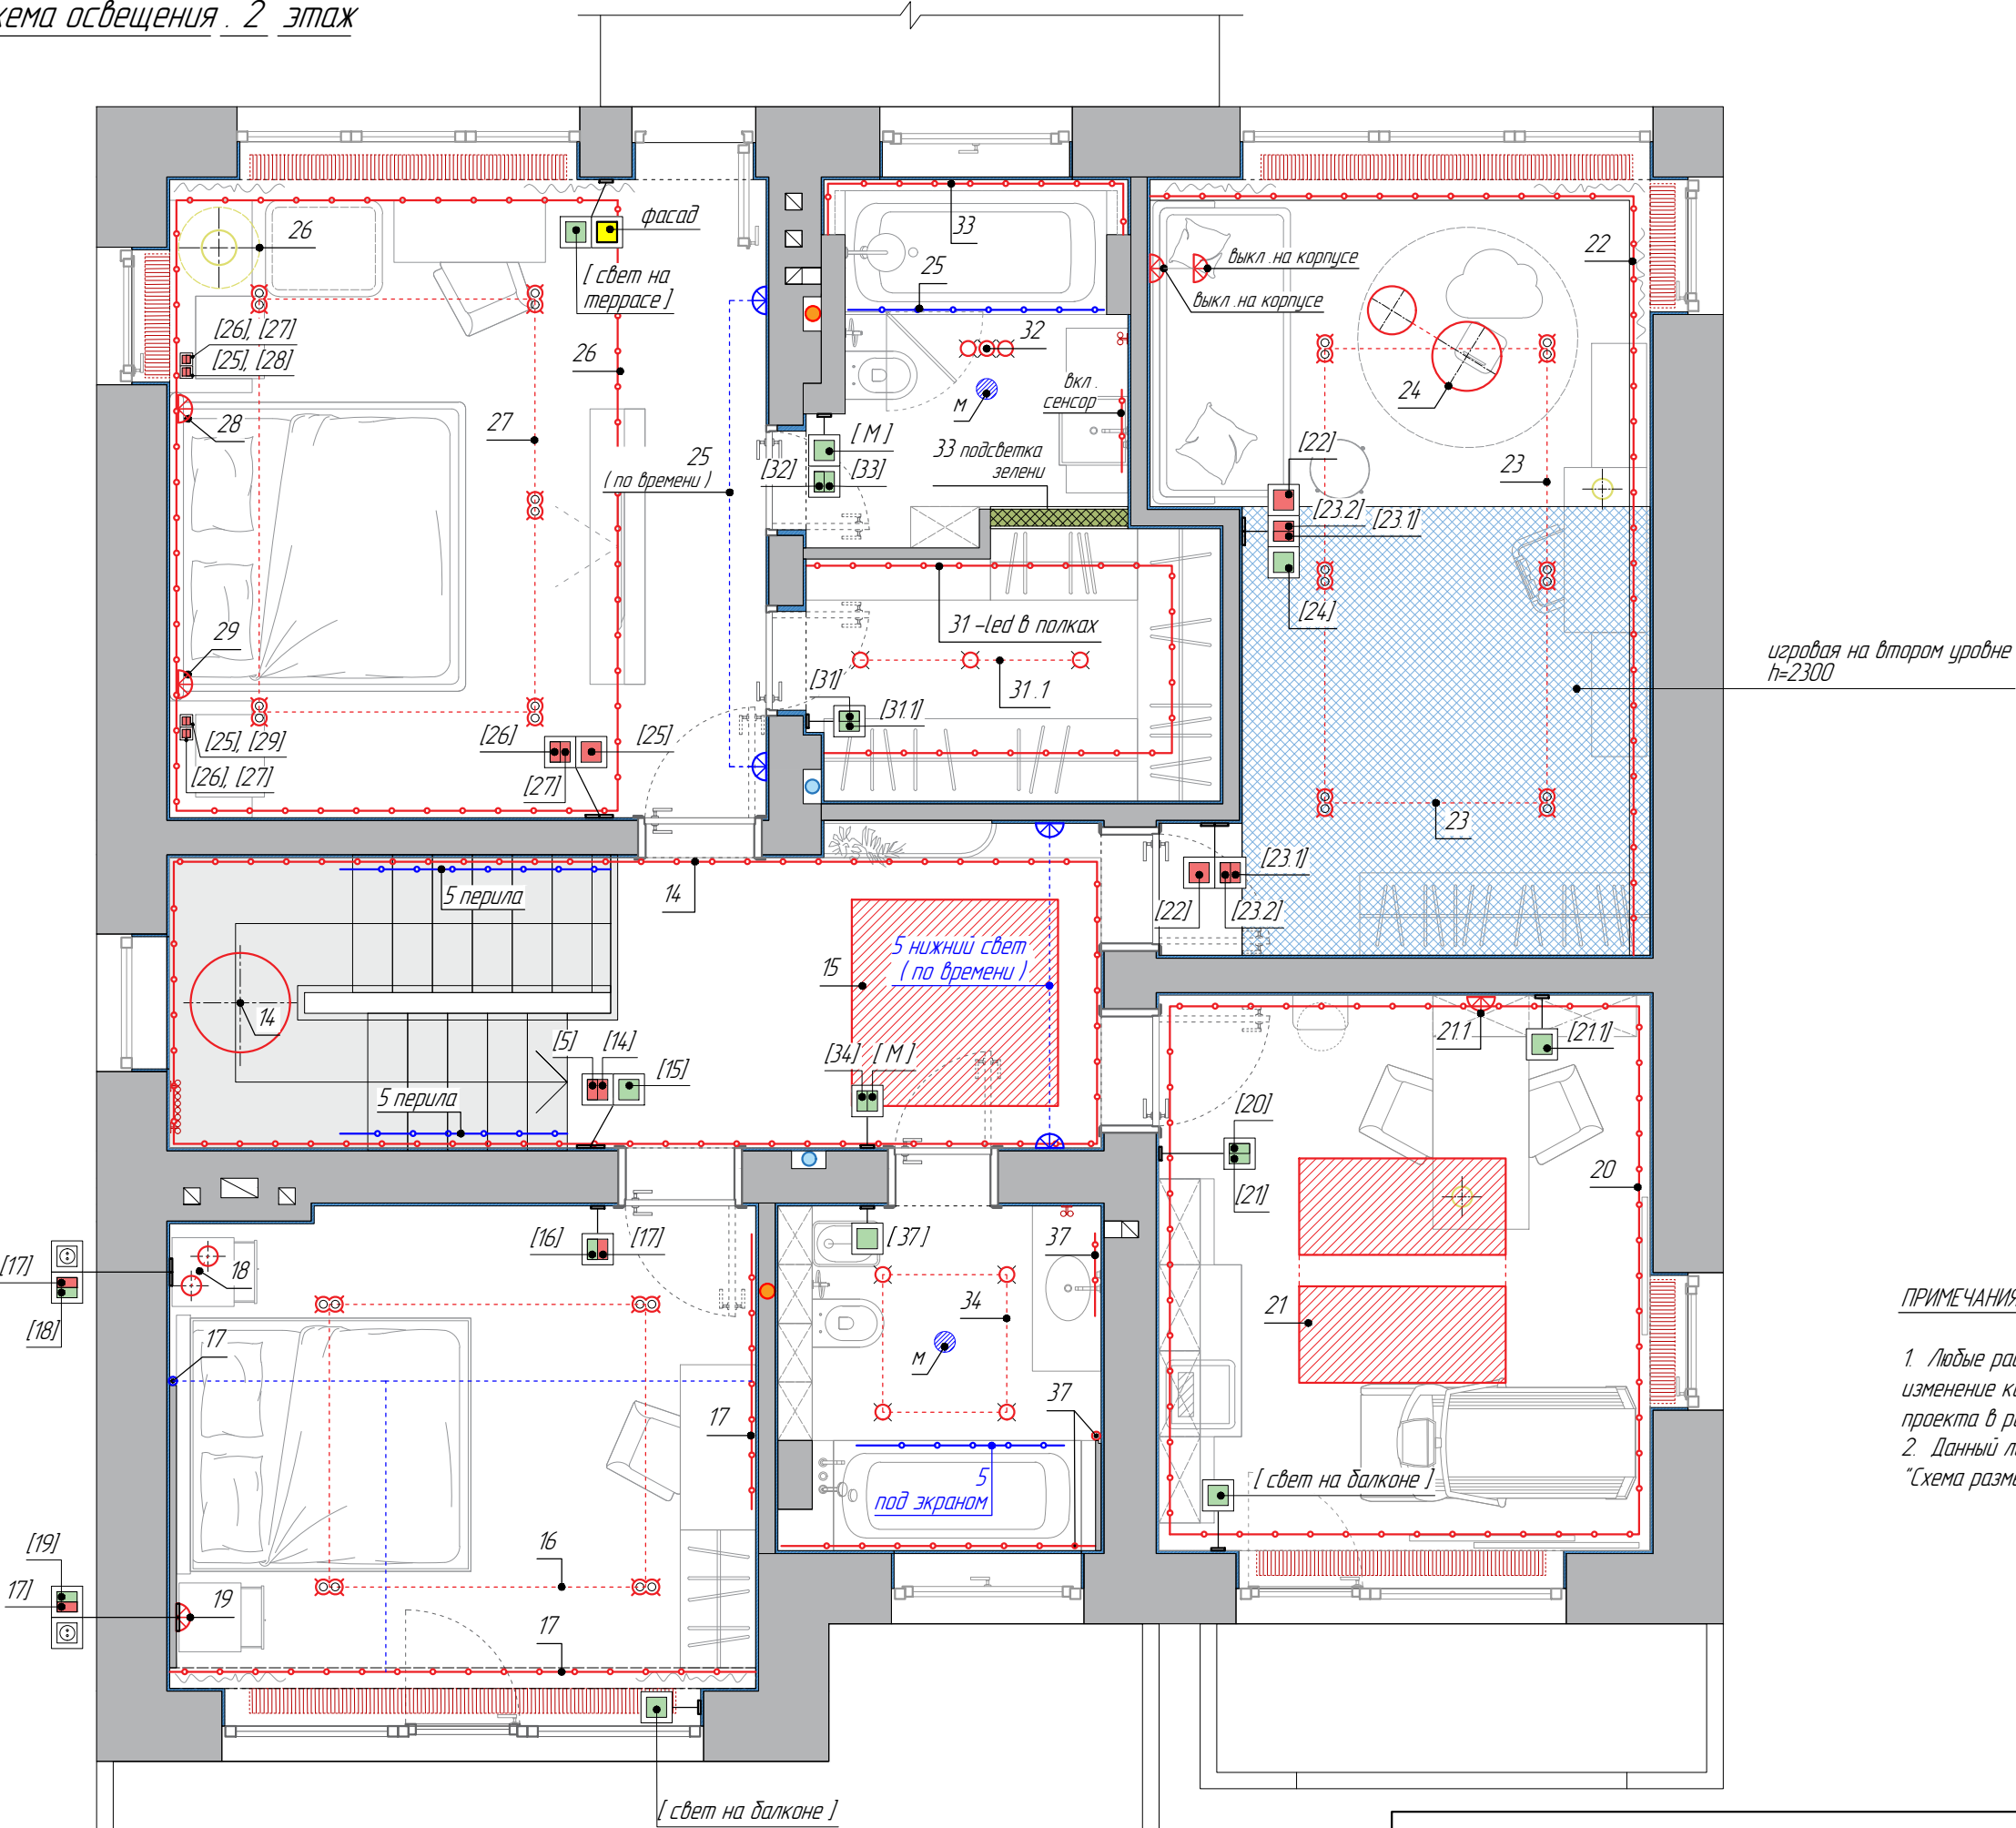

	УСЛОВНЫЕ ОБОЗНАЧЕНИЯ
	электровентилятор
	люстра/подвесной св-ник
	потолочный накладной светильник
	потолочный встраиваемый св-ник
	потолочный встраиваемый св-ник двойной
	настенный светильник (бра)
	трековый светильник
	led подсветка
	световой потолок
	выключатель одноклавишный
	выключатель двухклавишный
	выключатель проходной
	выключатель проходной двухклавишный
	напольный / настольный светильник

ПРИМЕЧАНИЯ

- Любые расхождения проектных размеров с фактическими, нестыковки, изменение конструктивных решений и т.п., согласовывать с автором проекта в рамках авторского надзора
- Данный лист смотреть совместно с листами "Схема размещения электрооборудования" и "Схема потолка"

кп РАЙТ ЭКО


Архитектор Овчарова Ольга

Схема освещения . 2 этаж

ООО ЧАЛОВА
PROJECT

Схема участков водяного тёплого пола

1 этаж

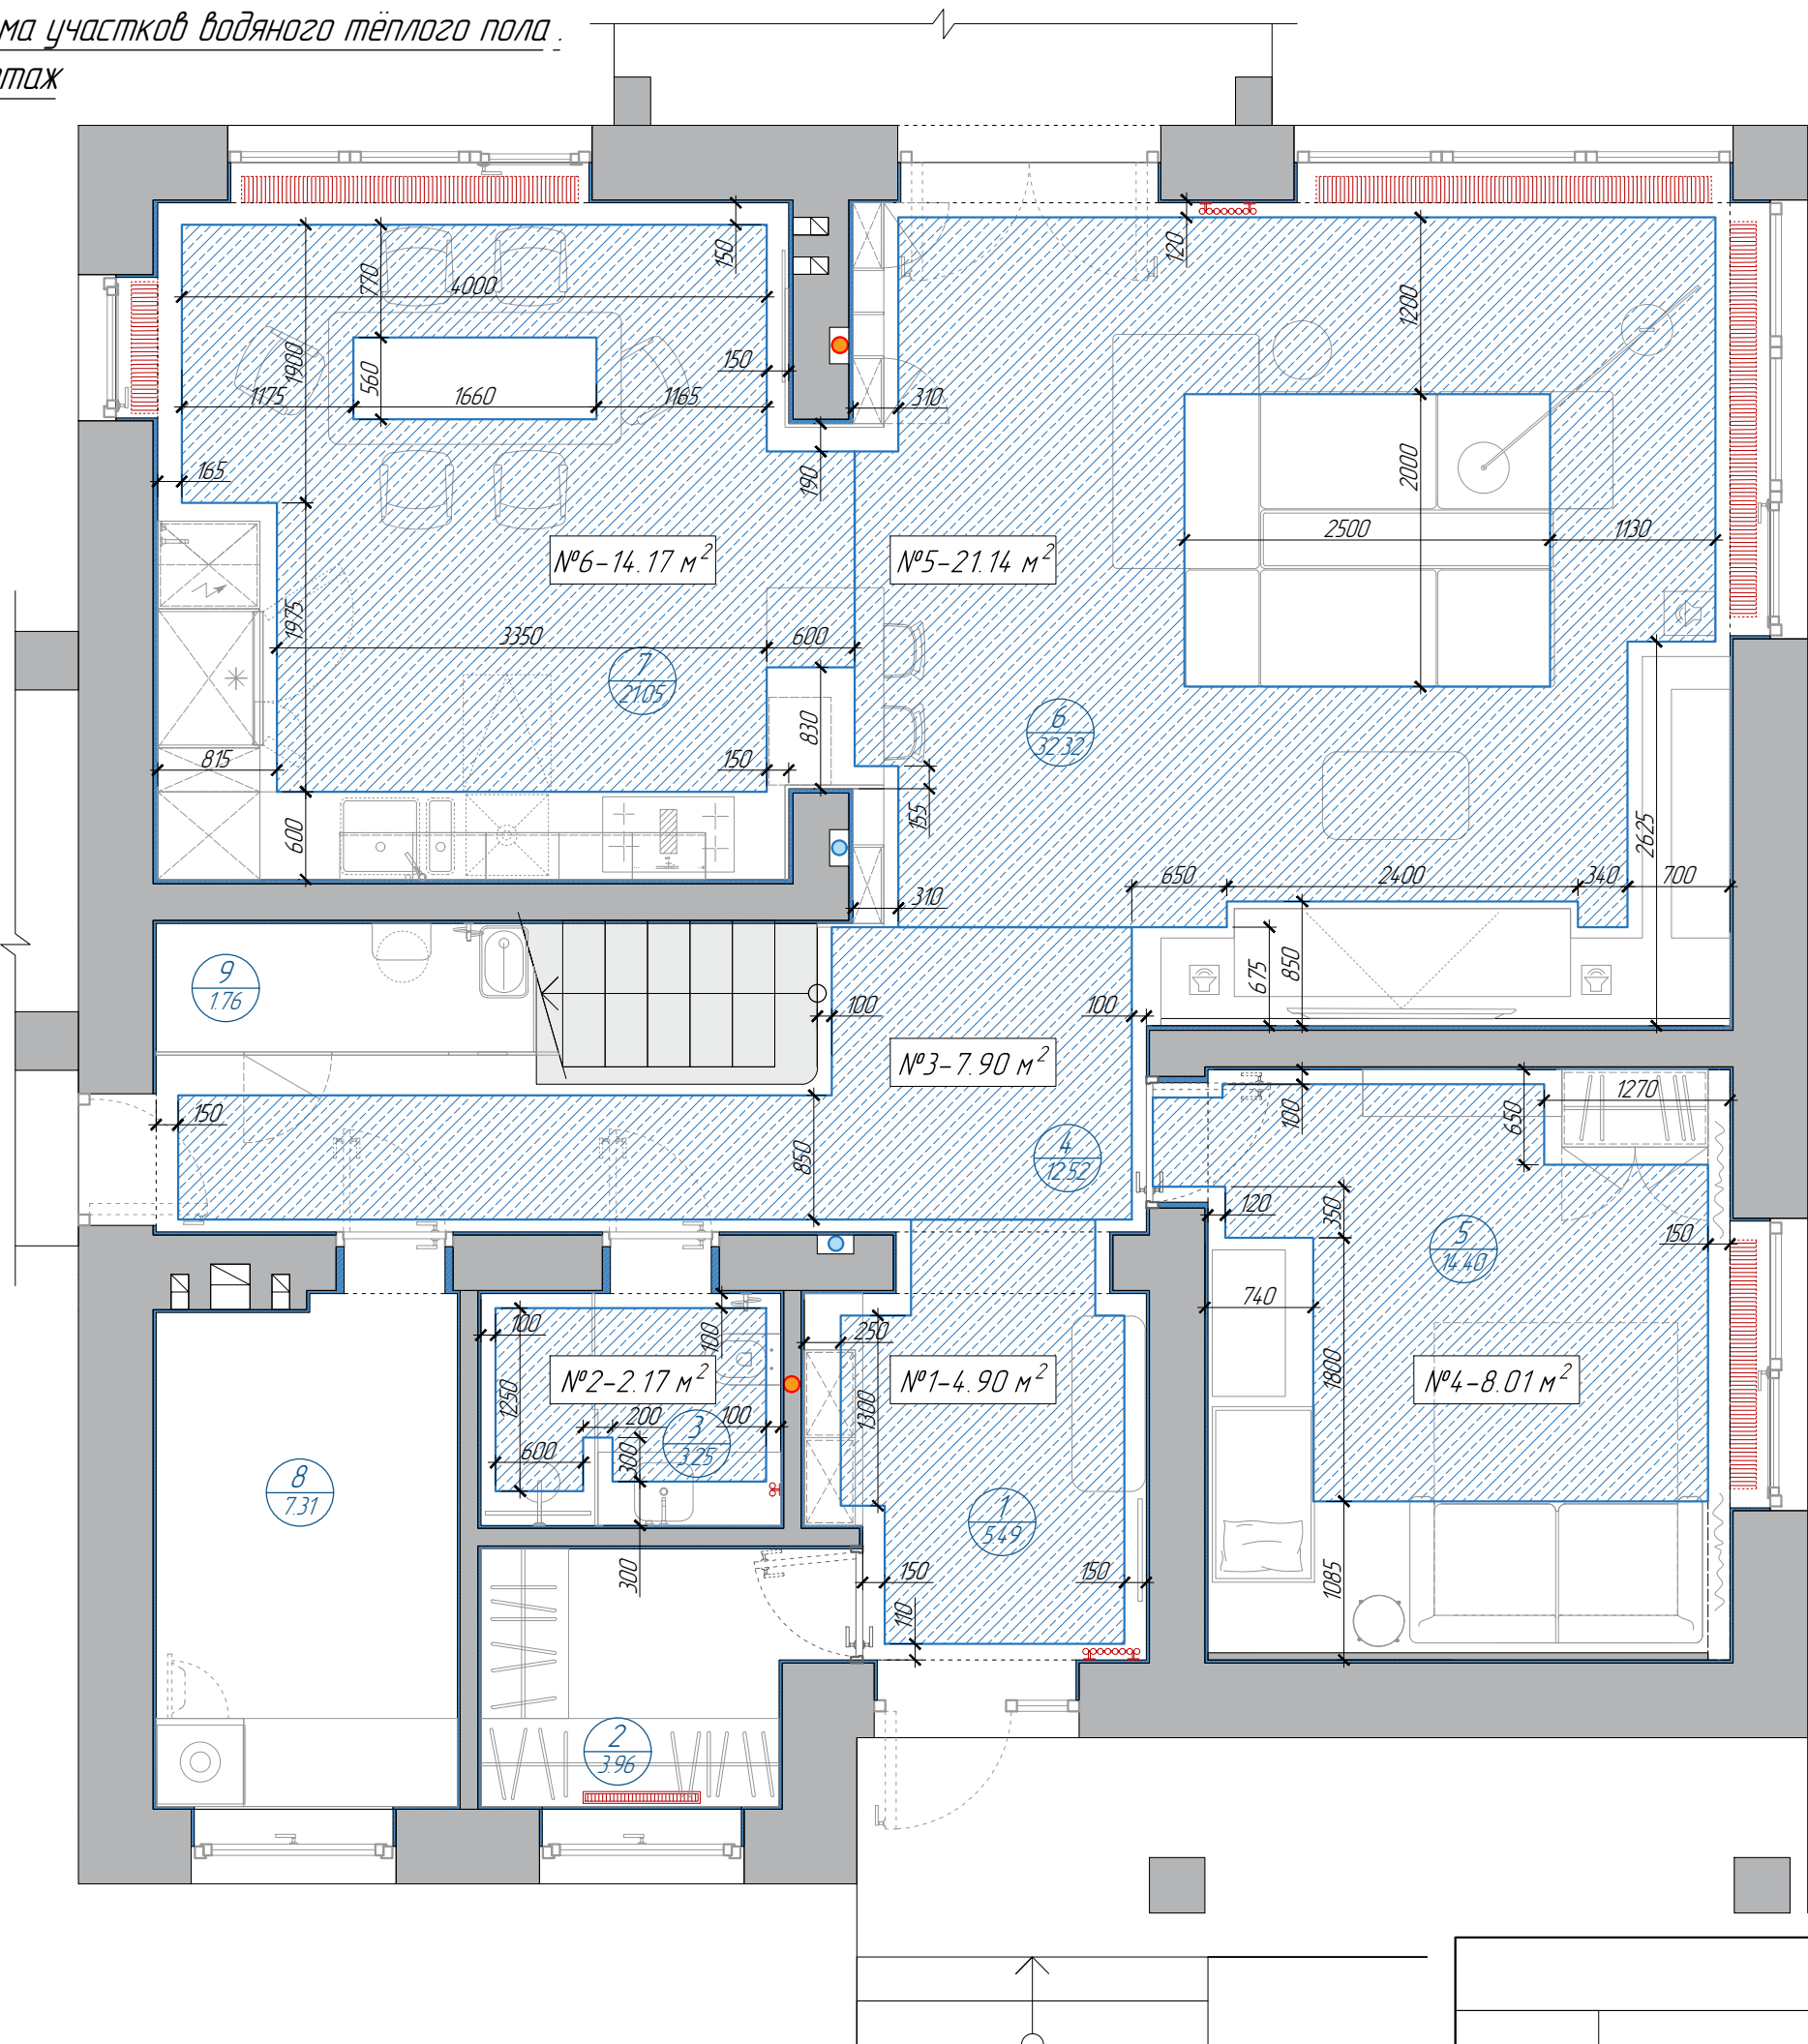

Экспликация помещений					
Этаж	№ пом.	Наименование помещения	Площадь , м ²		Примечание
			осн.	вспом.	
1	1	Прихожая		5.49	
	2	Гардеробная		3.96	
	3	Санузел гостей		3.25	
	4	Лестничный холл		12.52	
	5	Комната няни	14.40		
	6	Гостиная	32.32		
	7	Кухня –столовая	21.05		
	8	Котельная		7.31	
	9	Тех. помещение		1.76	
2	10	Лестничный холл		8.33	
	11	Мастер –спальня	20.10		
	12	Ванная комната		5.17	
	13	Гардеробная		5.74	
	14	Детская комната	18.88		
	15	Кабинет	14.41		
	16	Санузел		5.60	
	17	Гостевая комната	14.80		
		Итого по помещениям	135.96	59.13	
Общая площадь помещений дома			195.09		

Технико -экономические показатели

Вид теплого пола	Этаж	S, м ²
Водяной теплый пол	1	58.29

УСЛОВНЫЕ ОБОЗНАЧЕНИЯ

- стены и перегородки из керамоблока
- стояк канализации
- стояк лифтовой канализации
- штукатурный слой
- внутрипольный конвектор
- панельный радиатор
- вертикальный трубчатый радиатор
- участок размещения водяного тёплого пола
- №6-14.17 м² номер и площадь участка

ПРИМЕЧАНИЯ

1. При монтаже теплых полов учитывать тип напольного покрытия и требования от производителя напольных покрытий к устройству теплого пола


кп РАЙТ ЭКО

Архитектор
Овчарова Ольга

Схема участков
водяного тёплого пола. 1 этаж

ООО ЧАЛОВА
PROJECT

Схема участков водяного тёплого пола
2 этаж

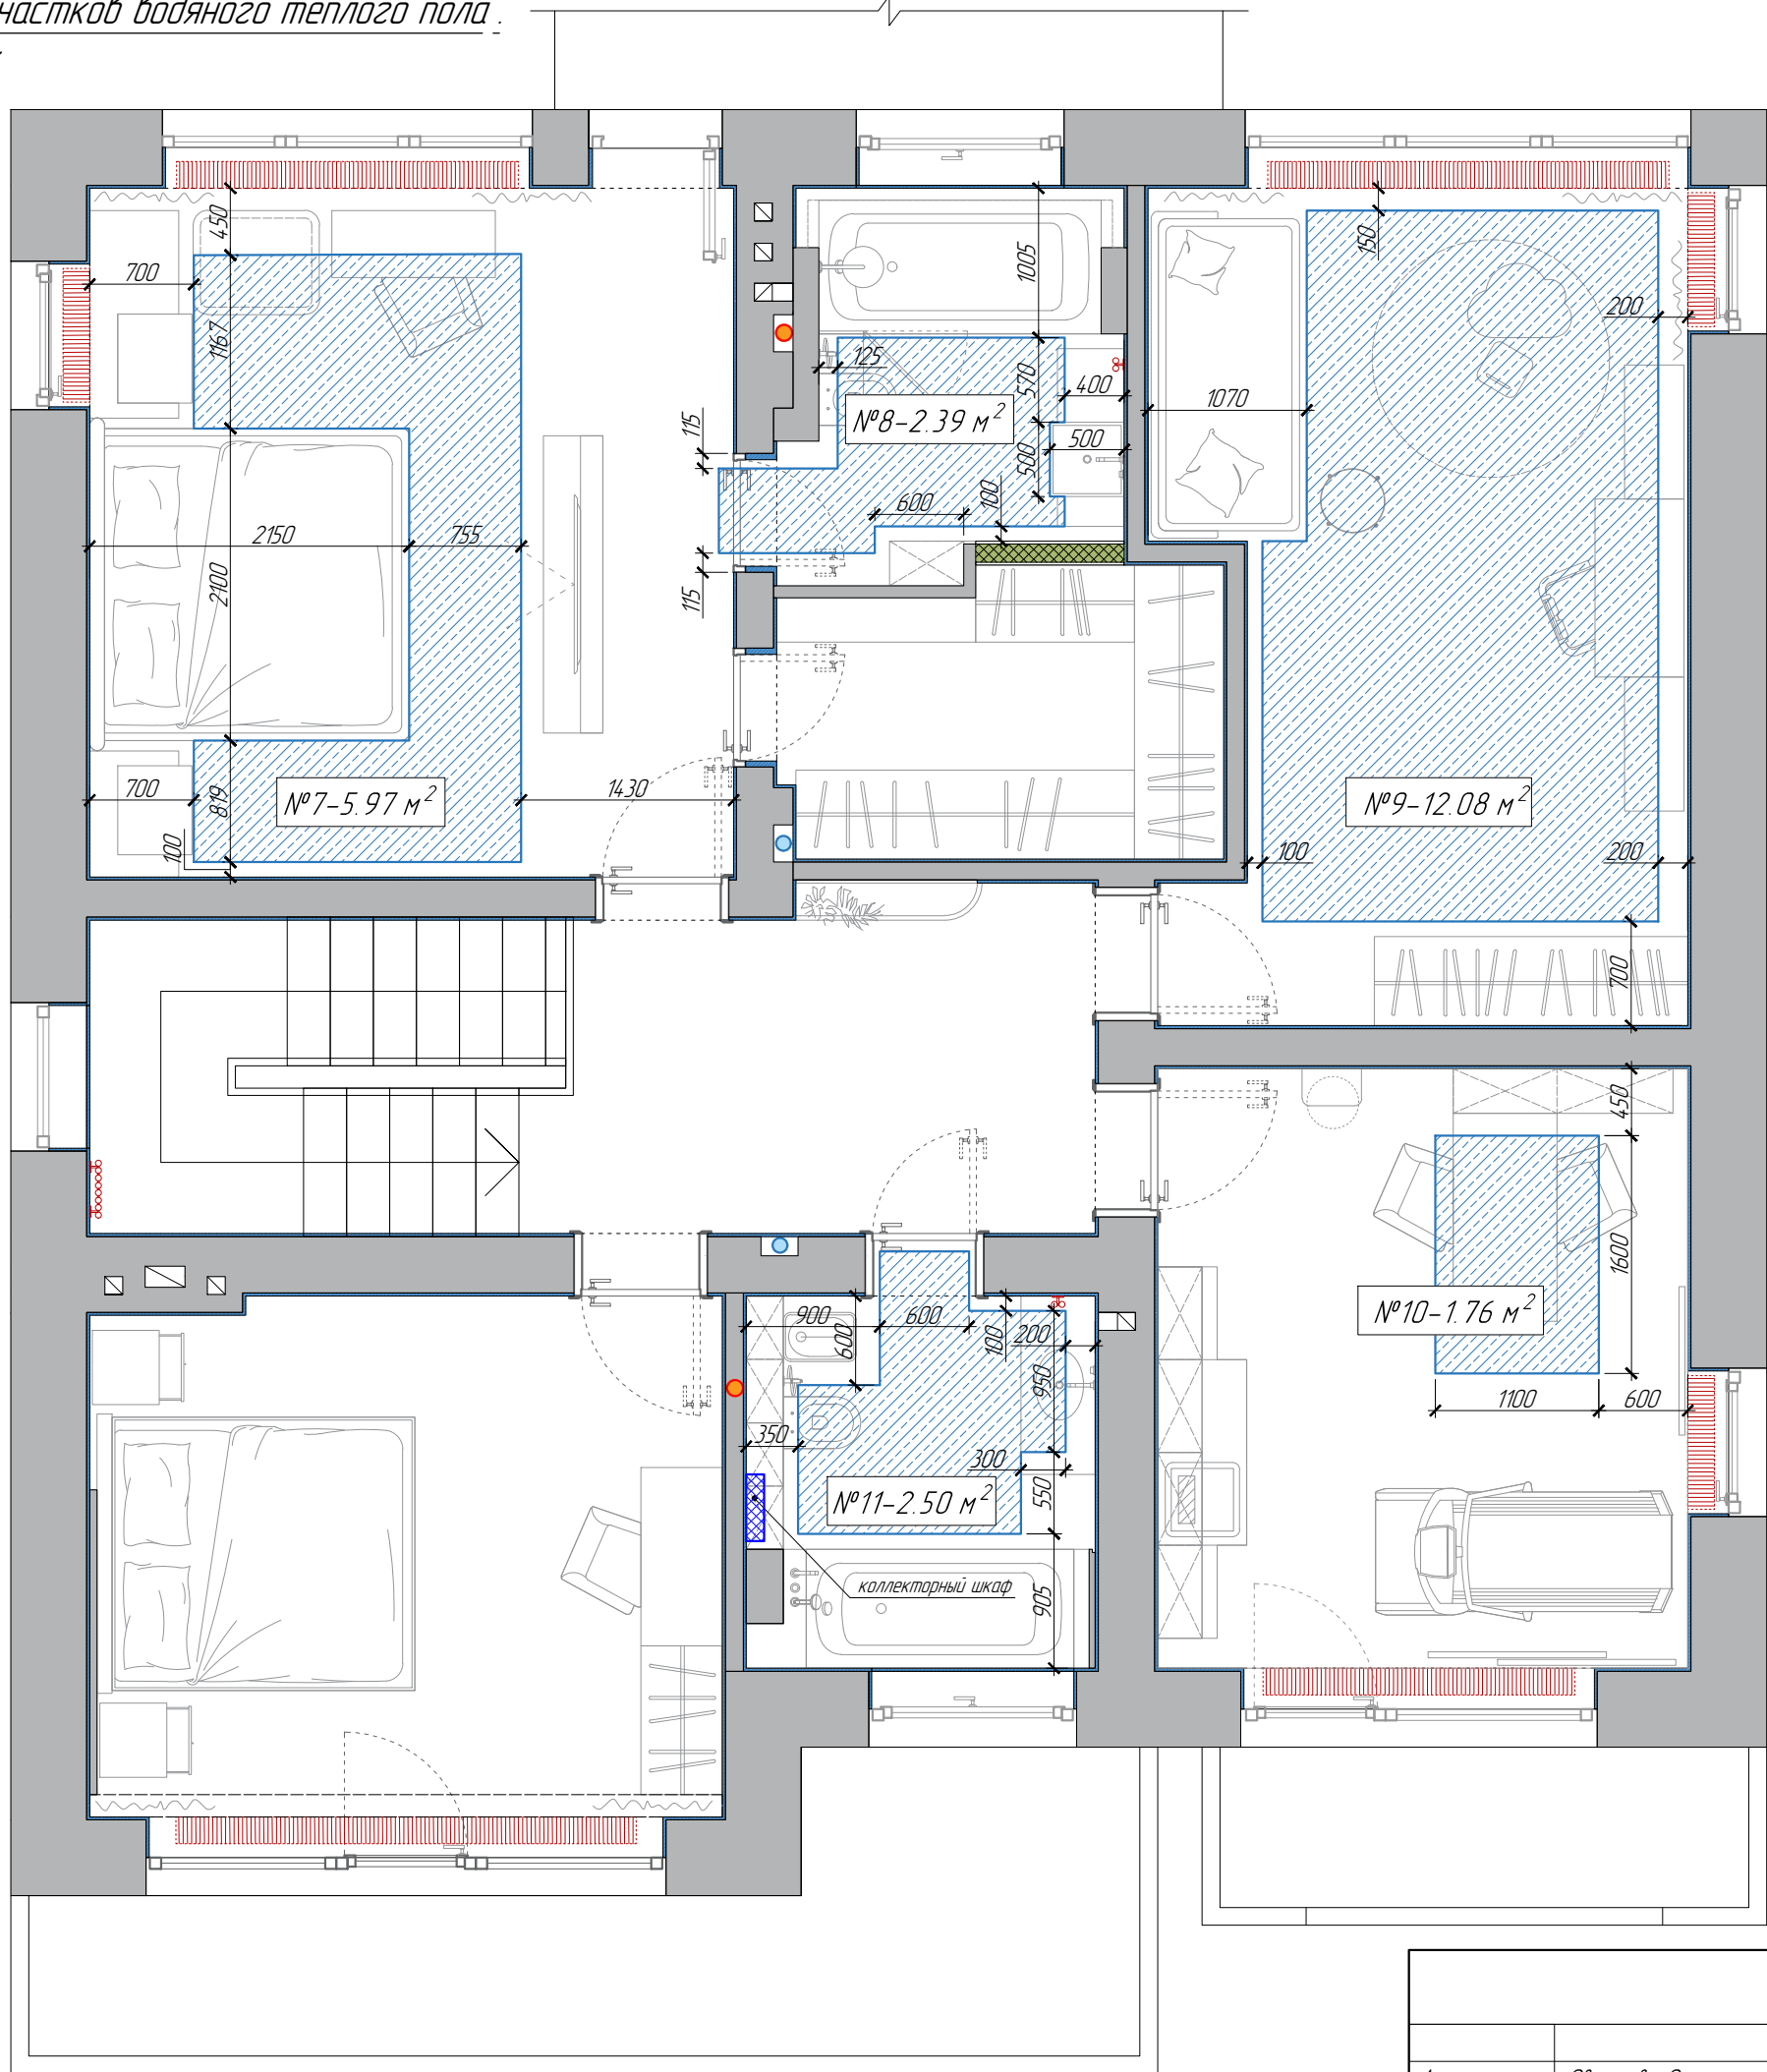

Экспликация помещений					
Этаж	№ пом.	Наименование помещения	Площадь , м ²		Примечание
			осн.	вспом.	
1	1	Прихожая		5.49	
	2	Гардеробная		3.96	
	3	Санузел гостей		3.25	
	4	Лестничн. холл		12.52	
	5	Комната няни	14.40		
	6	Гостиная	32.32		
	7	Кухня –столовая	21.05		
	8	Котельная		7.31	
	9	Тех. помещение		1.76	
2	10	Лестничн. холл		8.33	
	11	Мастер –спальня	20.10		
	12	Ванная комната		5.17	
	13	Гардеробная		5.74	
	14	Детская комната	18.88		
	15	Кабинет	14.41		
	16	Санузел		5.60	
	17	Гостевая комната	14.80		
		Итого по помещениям	135.96	59.13	
Общая площадь помещений дома			195.09		

Технико - экономические показатели

Вид теплого пола	Этаж	S, м²
Водяной теплый пол	2	24.7

УСЛОВНЫЕ ОБОЗНАЧЕНИЯ


- стены и перегородки из керамоблока
- стояк канализации
- стояк лифтовой канализации
- штукатурный слой
- внутрипольный конвектор
- панельный радиатор
- вертикальный трубчатый радиатор
- участок размещения водяного тёплого пола
- №6-9.2 м² номер и площадь участка

ПРИМЕЧАНИЯ

1. При монтаже теплых полов учитывать тип напольного покрытия и требования от производителя напольных покрытий к устройству теплого пола

кп РАЙТ ЭКО			
Архитектор	Овчарова Ольга	Схема участков водяного тёплого пола. 2 этаж	ООО ЧАЛОВА PROJECT

Схема потолка. 1 эт.

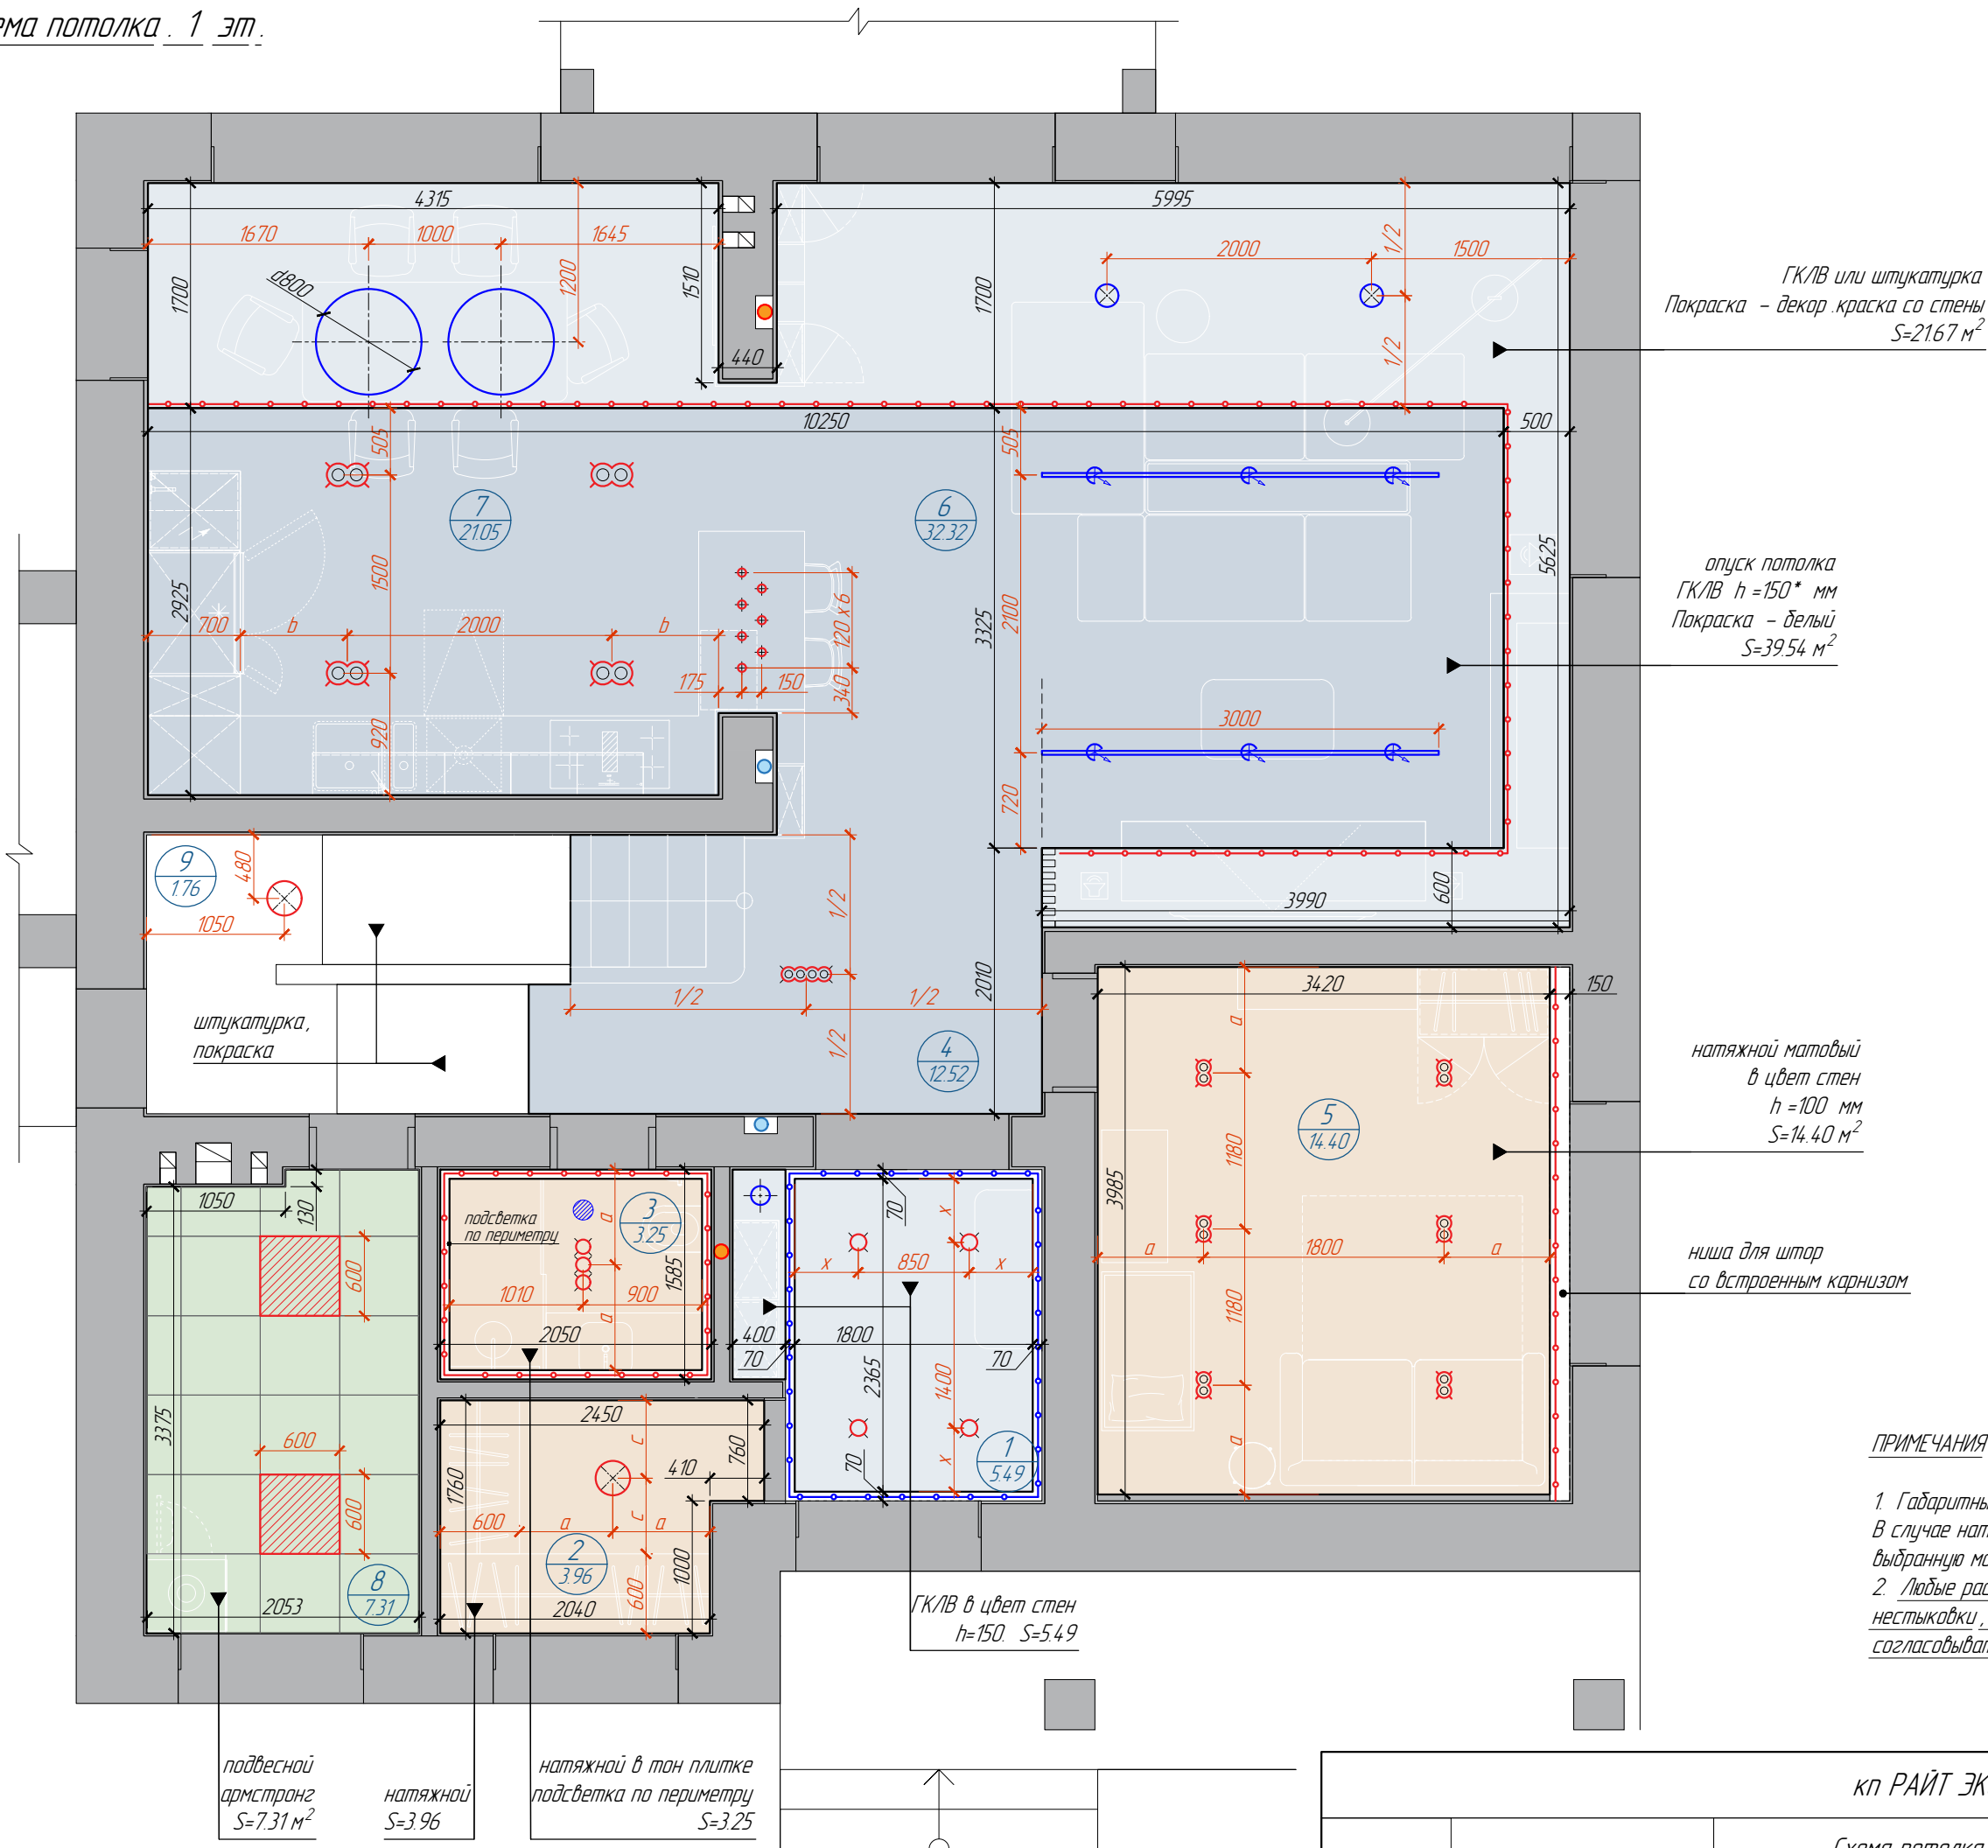


УСЛОВНЫЕ ОБОЗНАЧЕНИЯ	
	электровентилятор
	люстра/подвесной св-ник
	потолочный накладной светильник
	потолочный встраиваемый св-ник
	потолочный встраиваемый св-ник
	трековый светильник
	led подсветка
	световой потолок

УСЛОВНЫЕ ОБОЗНАЧЕНИЯ	
	стены и перегородки из керамоблока
	стояк канализации
	стояк ливневой канализации
	потолок ГКЛ
	натяжной потолок
	потолок Армстронг

ПРИМЕЧАНИЯ

- Габаритные размеры ниш указаны по выступающим элементам. В случае натяжных потолков – данный размер корректируется под выбранную модель профиля
- Любые расхождения проектных размеров с фактическими, нестыковки, изменение конструктивных решений и т.п., согласовывать с автором проекта в рамках АН

Схема потолка . 2 эт.

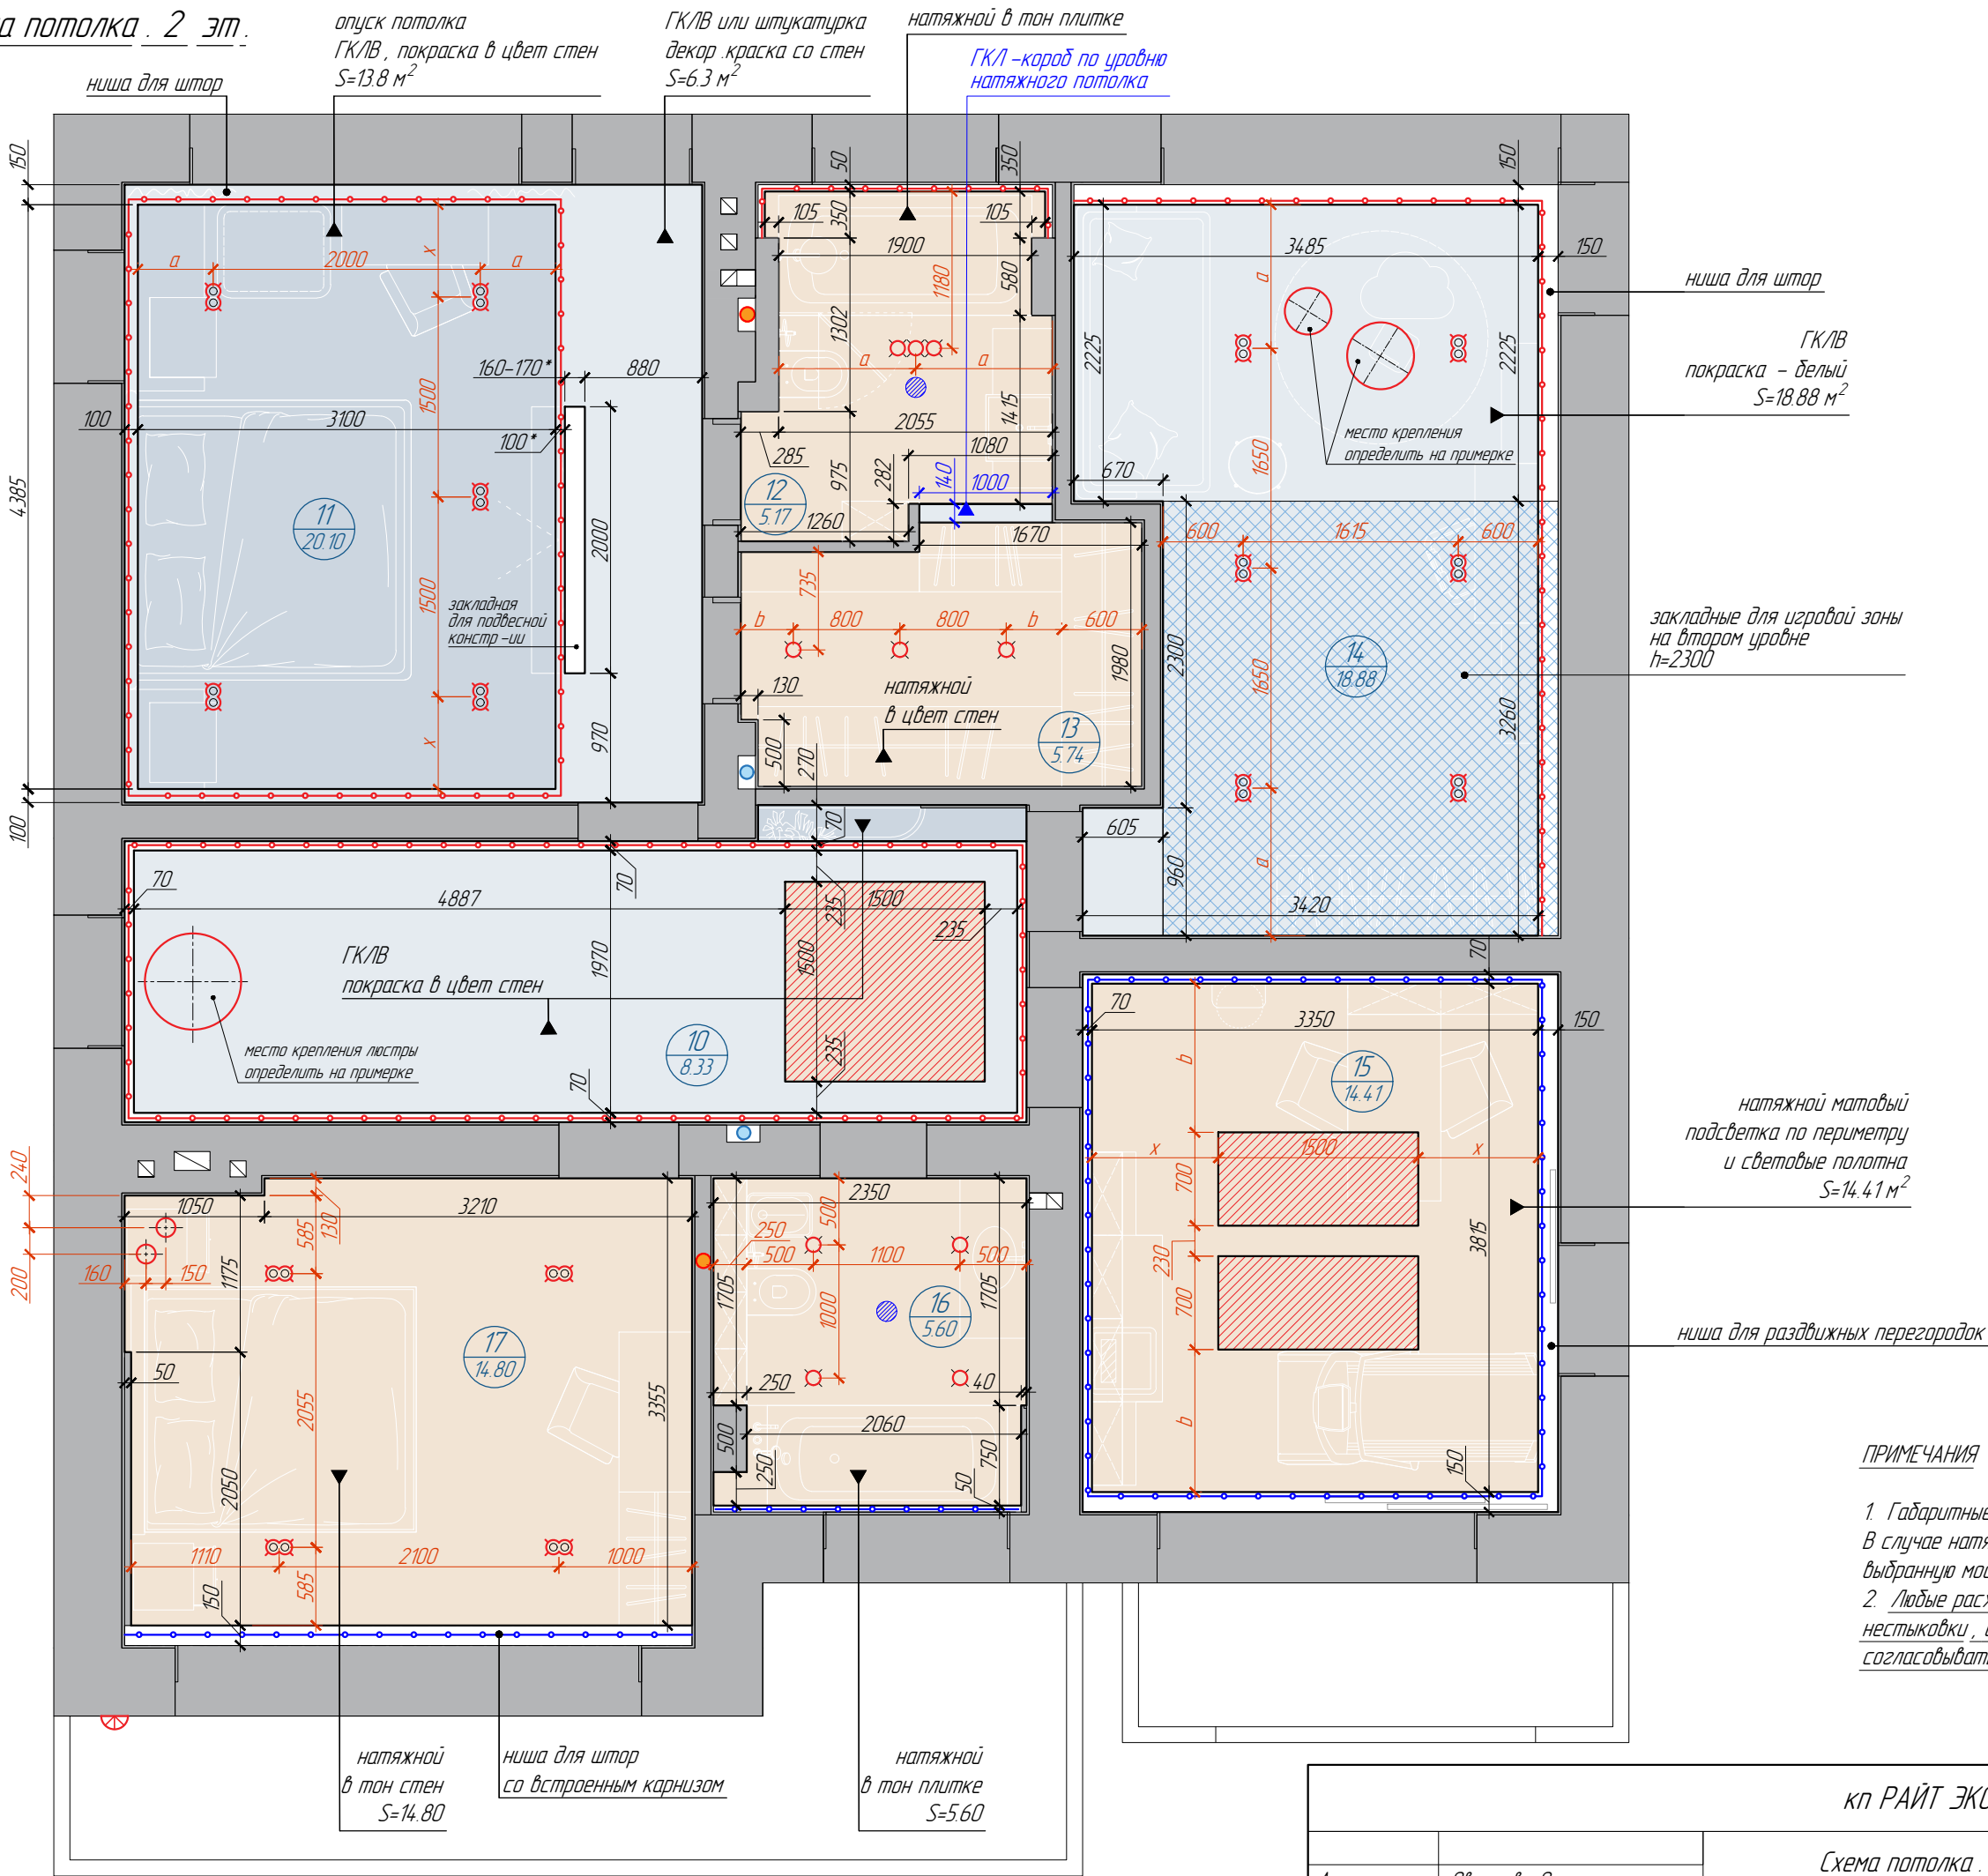

УСЛОВНЫЕ ОБОЗНАЧЕНИЯ	
	электровентилятор
	люстра/подвесной св-ник
	потолочный накладной светильник
	потолочный встраиваемый св-ник
	потолочный встраиваемый св-ник
	трековый светильник
	led подсветка
	световой потолок

УСЛОВНЫЕ ОБОЗНАЧЕНИЯ	
	стены и перегородки из керамоблока
	стояк канализации
	стояк ливневой канализации
	потолок ГКЛ
	натяжной потолок

ПРИМЕЧАНИЯ

- Габаритные размеры ниш указаны по выступающим элементам. В случае натяжных потолков - данный размер корректируется под выбранную модель профиля
- Любые расхождения проектных размеров с фактическими, нестыковки, изменение конструктивных решений и т.п., согласовывать с автором проекта в рамках АН