

## Прихожая. Коллаж-концепция



## Плинтус скрытый из напольного керамогранита



## Холл. Коллаж-концепция

св-ники Китай  
или  
световой  
натяжной потолок

Двери межкомнатные  
ACADEMY  
Slim Soft Touch  
высота полотна - 2200

кварцвинил  
или  
инженерная доска

панели полистирол  
Decor Dizayn DD901  
150x10x2000

поручень настенный  
из дерева  
с подсветкой

стекло



Плинтус скрытый из  
напольного керамогранита



дверь скрытая  
ABS кромка

потолок ГКЛ,  
св-ник гипсовый  
встраиваемый  
ARTPOLE SGS26



встраиваемый  
гипсовый св-ник  
Stellanova SUBRA-E



светильник  
подвесной  
Китай

подсветка  
по  
периметру

потолок ГКЛ  
в цвет стен

покраска

ВОДОПАД ПО СТЕКЛУ

Снизу - база  
под насос,  
камни и искусств.  
растения

Сверху  
(за рельефным  
карнизом)  
выпуск воды



ступени  
и площадка  
- микроцемент



мебельная  
конструкция  
с дверью  
в тех. помещение

отверстие  
для кошки

первая ступень  
- подиум,  
покрытие -  
микроцемент

керамогранит ИТАЛОН  
Сильвер. Натуральный  
900x1800



# Кухня-гостиная. Коллаж-концепция



накладной светильник  
в стиле трековых  
Maytoni Basis Rot

шкаф-витрина  
для Lego

декорат.краска  
ASTI velato

подсветка  
закарнизная  
вдоль ступени

панели под камень  
из полиуретана, Китай,

встраиваемый  
магнитный  
шинопровод  
MAYTONI

опуск потолка  
ГКЛ  
цвет белый

потолок-  
штукатурка,  
декорат.краска  
ASTI velato

декорат.краска  
ASTI velato

потолок ГКЛ,  
св-ники гипсовые встраиваемые  
ARTPOLE SGS37



св-ник подвесной  
Китай

св-ник - бра Затмение

св-ник подвесной  
Китай



декорат.краска  
ASTI velato

покраска - белый

мебельная конструкция  
стеллажей


тумба, встроенная  
в нишу в подиуме

керамогранит ИТАЛОН  
Сильвер Натуральный  
900x1800

декорат.краска  
ASTI velato

керамогранит 120x60  
Zodiac Civic Lm

Плинтус скрытый  
из напольного керамогранита

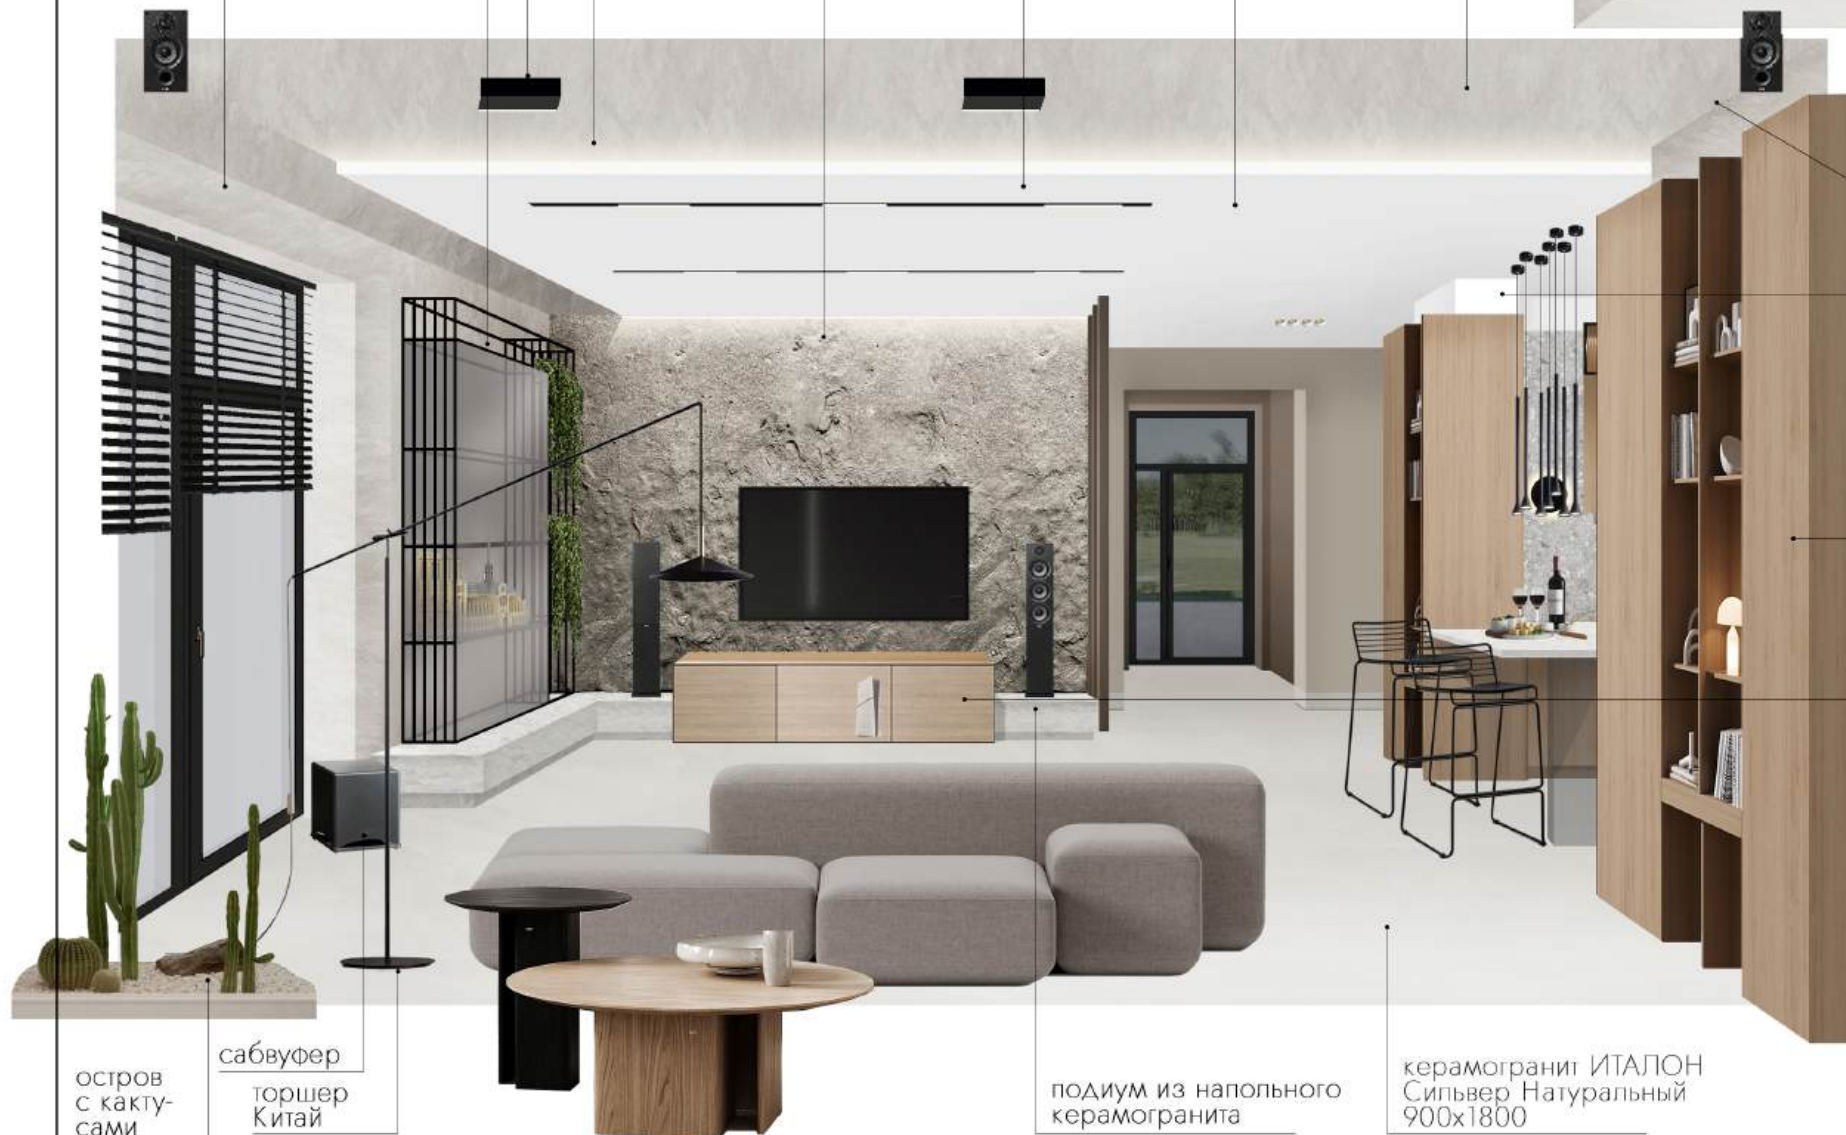

остров  
с какту-  
сами


сабвуфер  
торшер  
Китай

подиум из напольного  
керамогранита

керамогранит ИТАЛОН  
Сильвер Натуральный  
900x1800



## Гостевая 1 эт. Коллаж-концепция

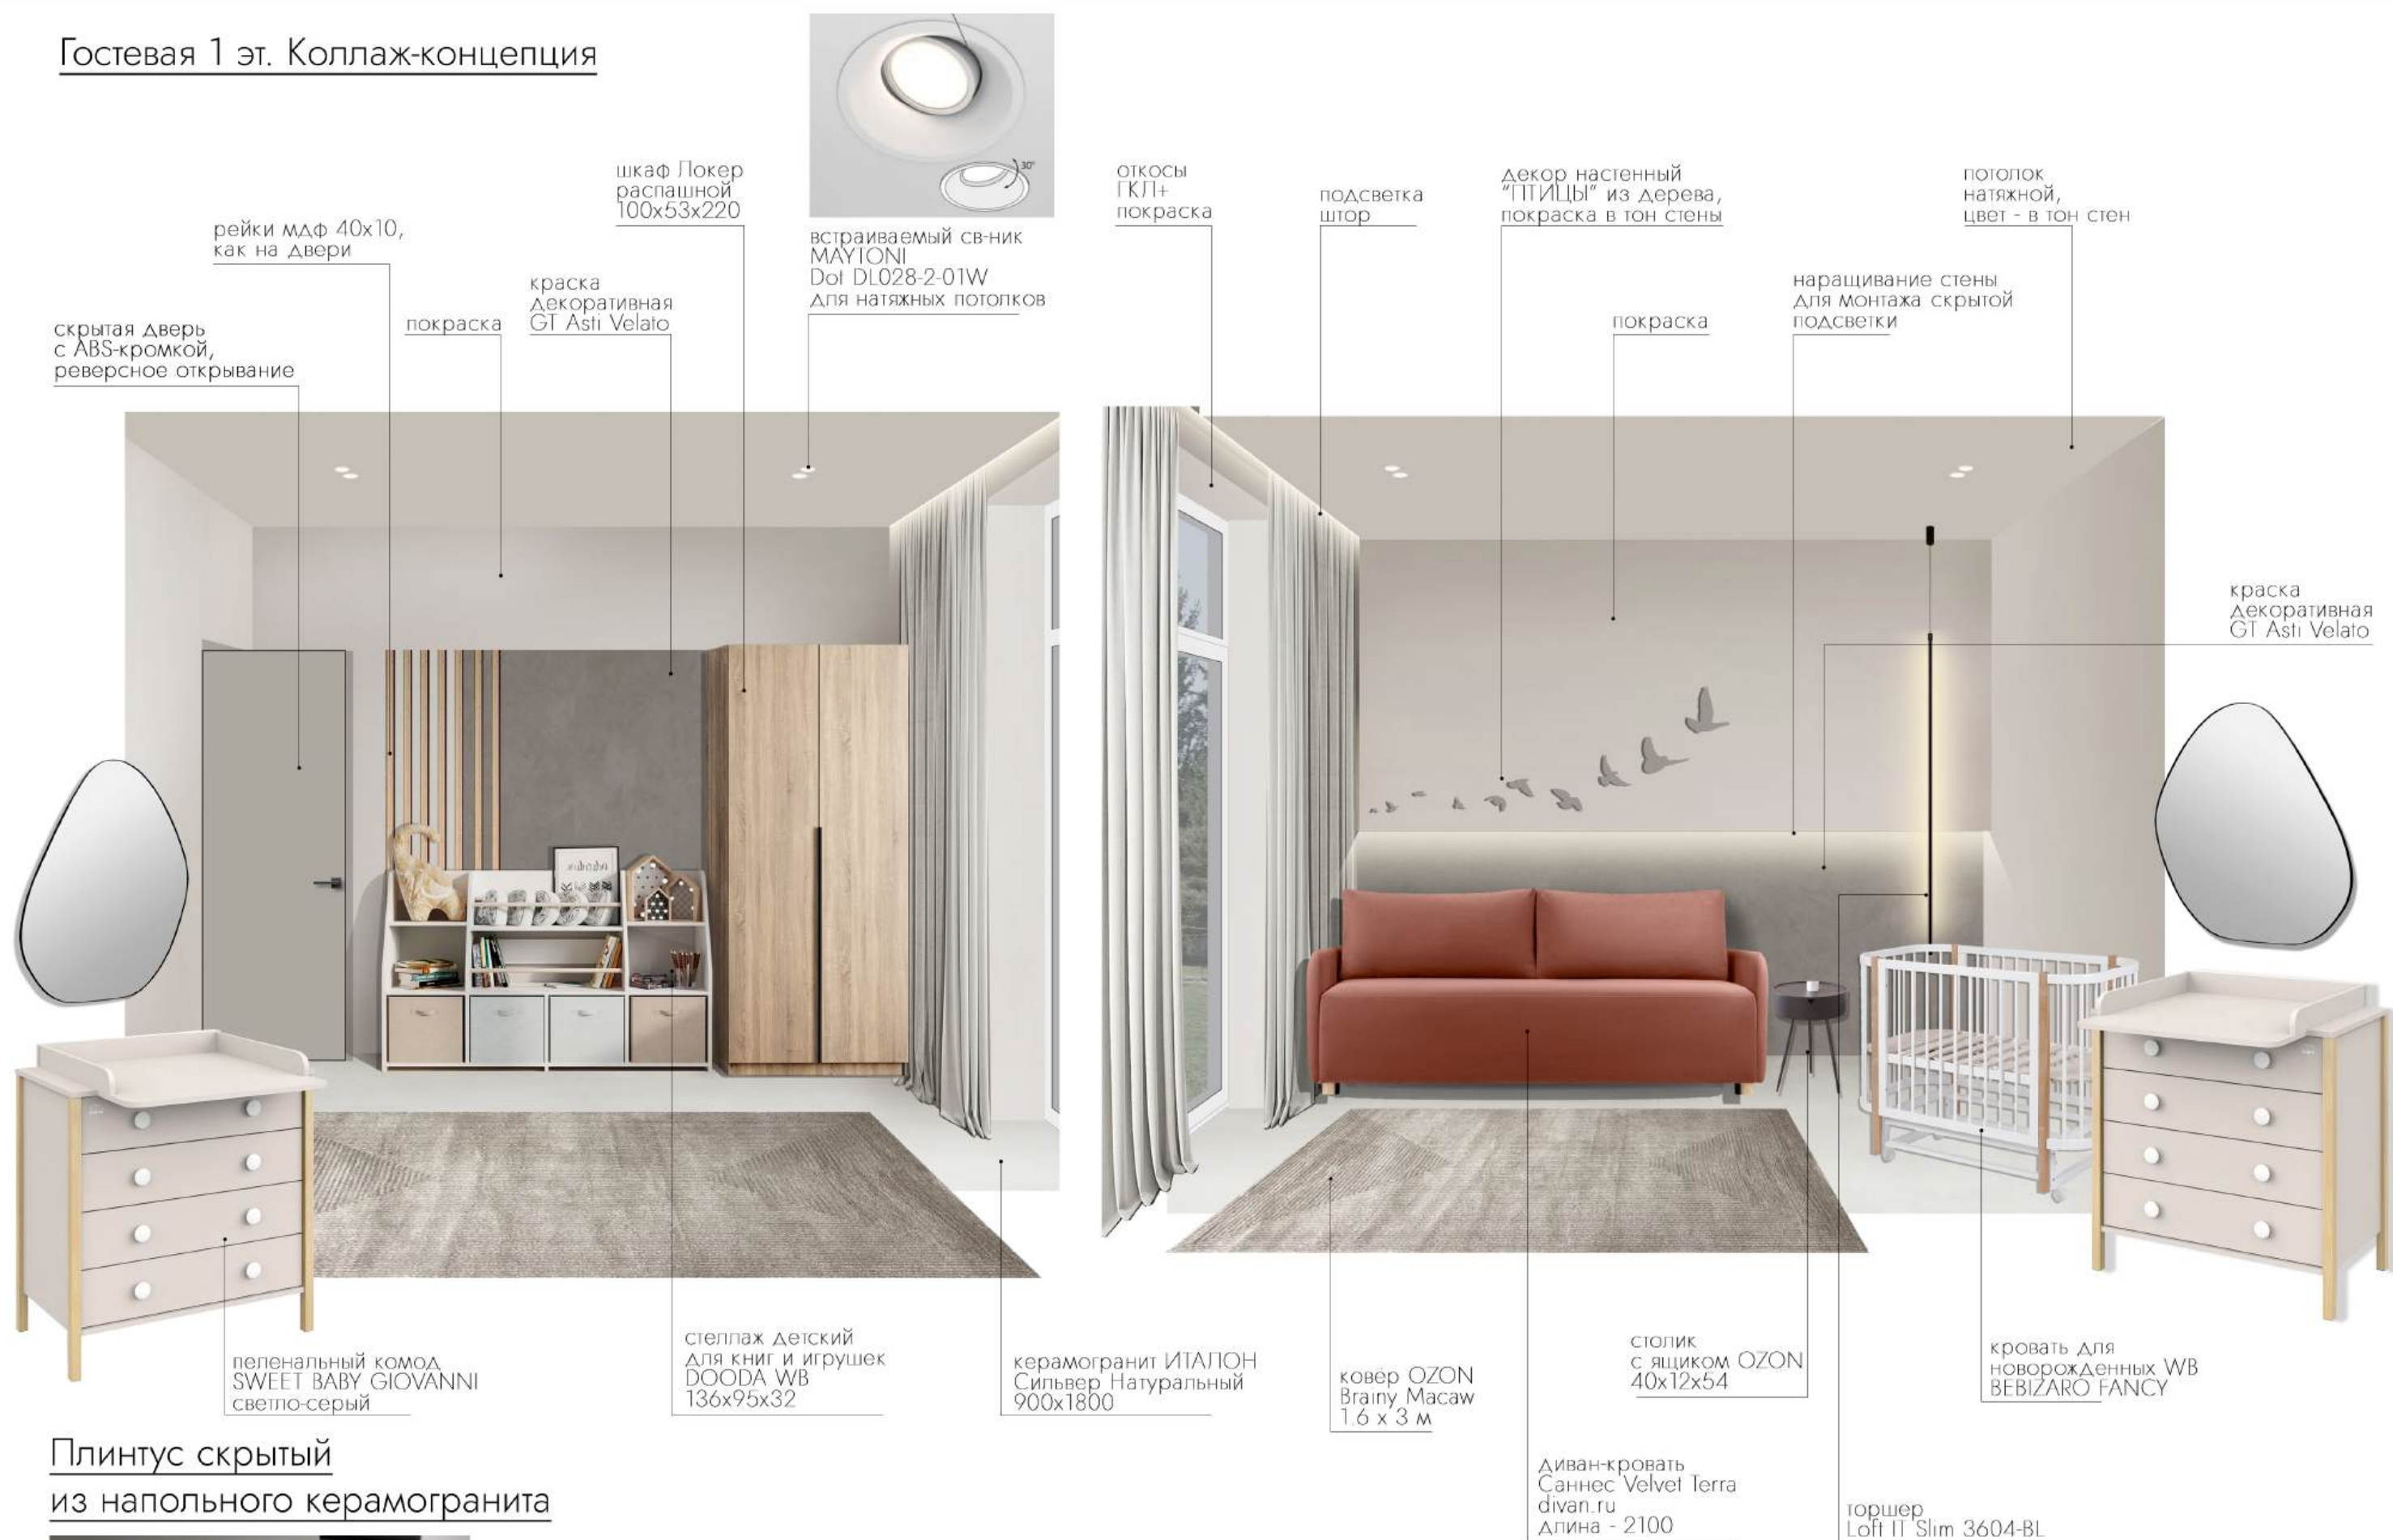

### Плинтус скрытый

из напольного керамогранита



# Санузел 1 эт. Коллаж-концепция

потолок натяжной  
в тон плитке

закарнизная подсветка  
по периметру

керамогранит 600x1200  
Simpolo гладкий

полотенцесушитель  
(электрический?)

зеркало с подсветкой

встраиваемый смеситель  
для раковины

подвесная тумба

подвесной унитаз  
с инсталляцией,  
гигиенический душ

керамогранит ИТАЛОН  
Сильвер Натуральный  
900x1800

встраиваемый св-ник  
MAYTONI  
Dot DL028-2-01W  
Для натяжных потолков



керамогранит 600x1200  
Simpolo рельеф

душевая система никель  
накладная

полка навесная металл  
OZON

керамогранит 600x1200  
Simpolo рельеф

керамогранит 600x1200  
Simpolo гладкий

керамогранит ИТАЛОН  
Сильвер Натуральный  
900x1800





## Гостевая 2 эт. Коллаж-концепция



встраиваемый св-ник  
MAYTONI  
Dot DL028-2-01W  
Для натяжных потолков

зеркало на заказ  
с подсветкой снизу

покраска в цвет шкафа

покраска

откосы  
ГКЛ+  
покраска

подсветка  
штор

покраска  
в цвет  
шкафа

наращивание стены  
для монтажа скрытой  
подсветки

подвесные  
св-ники  
Китай

потолок  
натяжной,  
цвет - белый



Плинтус скрытый



шкаф распашной  
Квелен-2 Terra  
96x55x220



покраска

декор.  
краска  
Asti Velato

бра Китай

Прикроватная  
тумба консоль  
"Лестер"  
543x407x216

кварцвинил  
или инженерная доска


МФ Агат двухспальная кровать,  
с подъемным механизмом RIMINI,  
180x200 см

Стул REYNAUX 1

Двери межкомнатные  
ACADEMY  
Slim Soft Touch  
высота полотна - 2200




# Санузел 3 эт. Коллаж-концепция

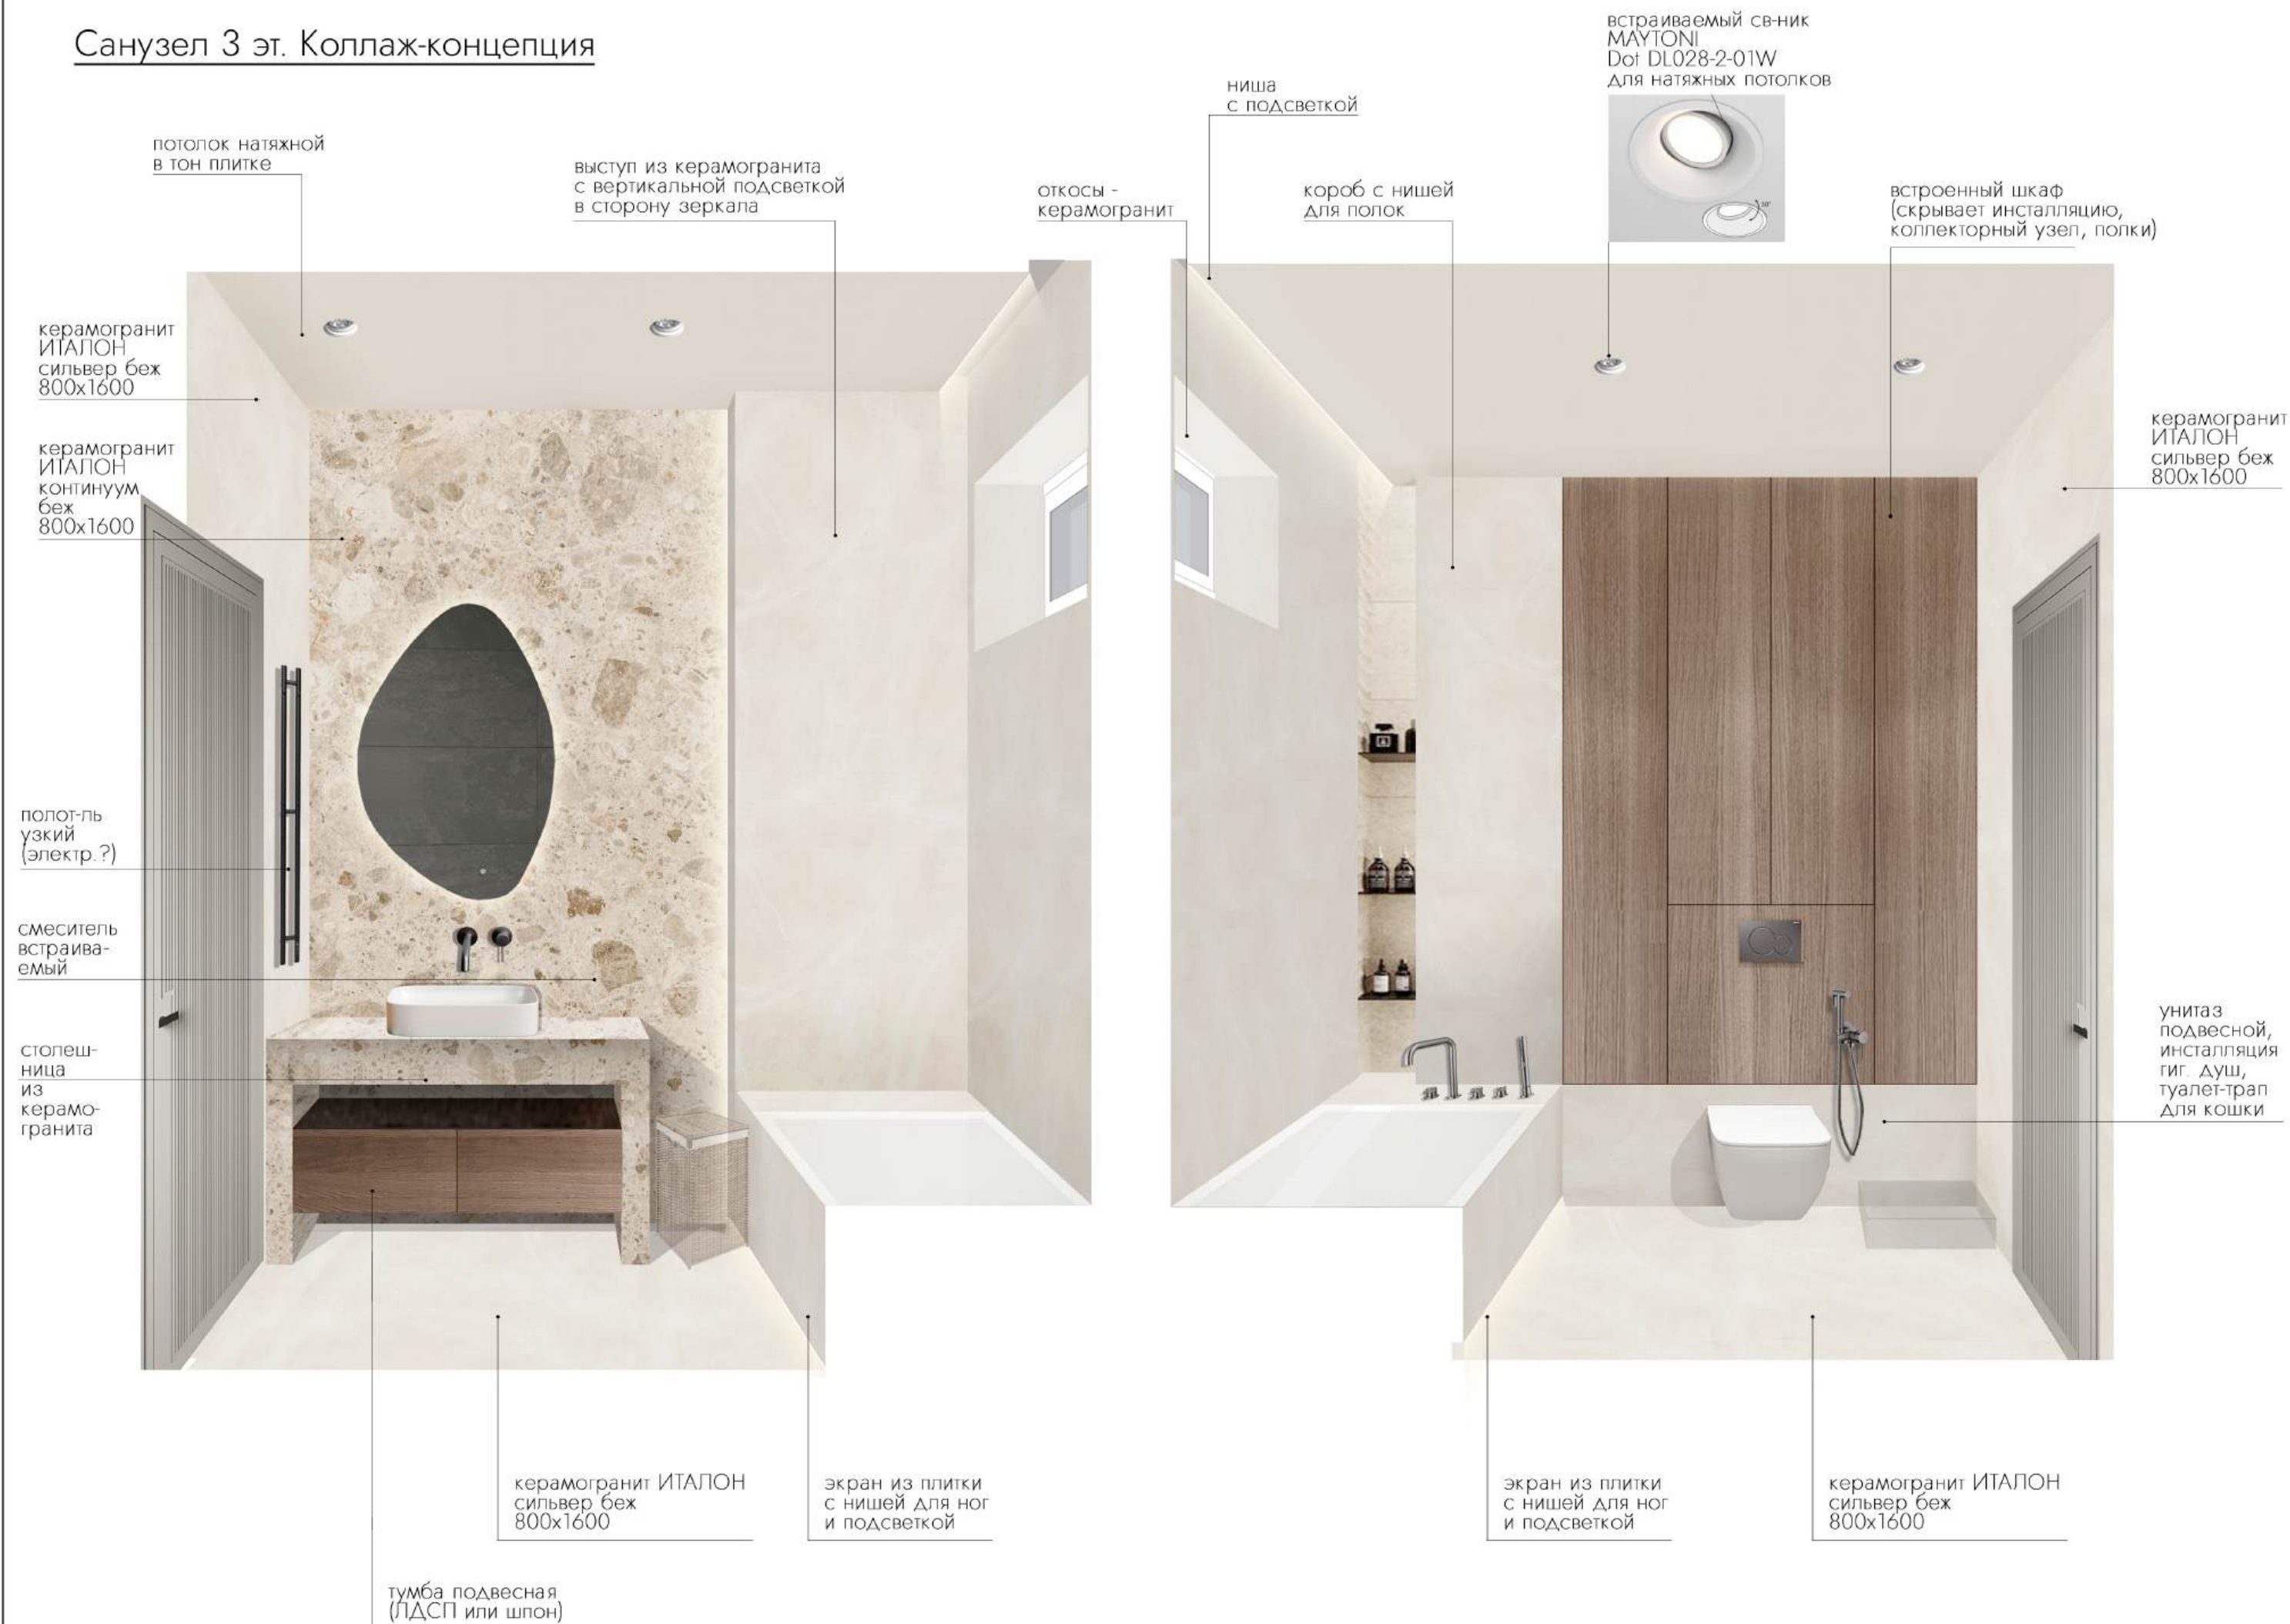



# Кабинет. Коллаж-концепция

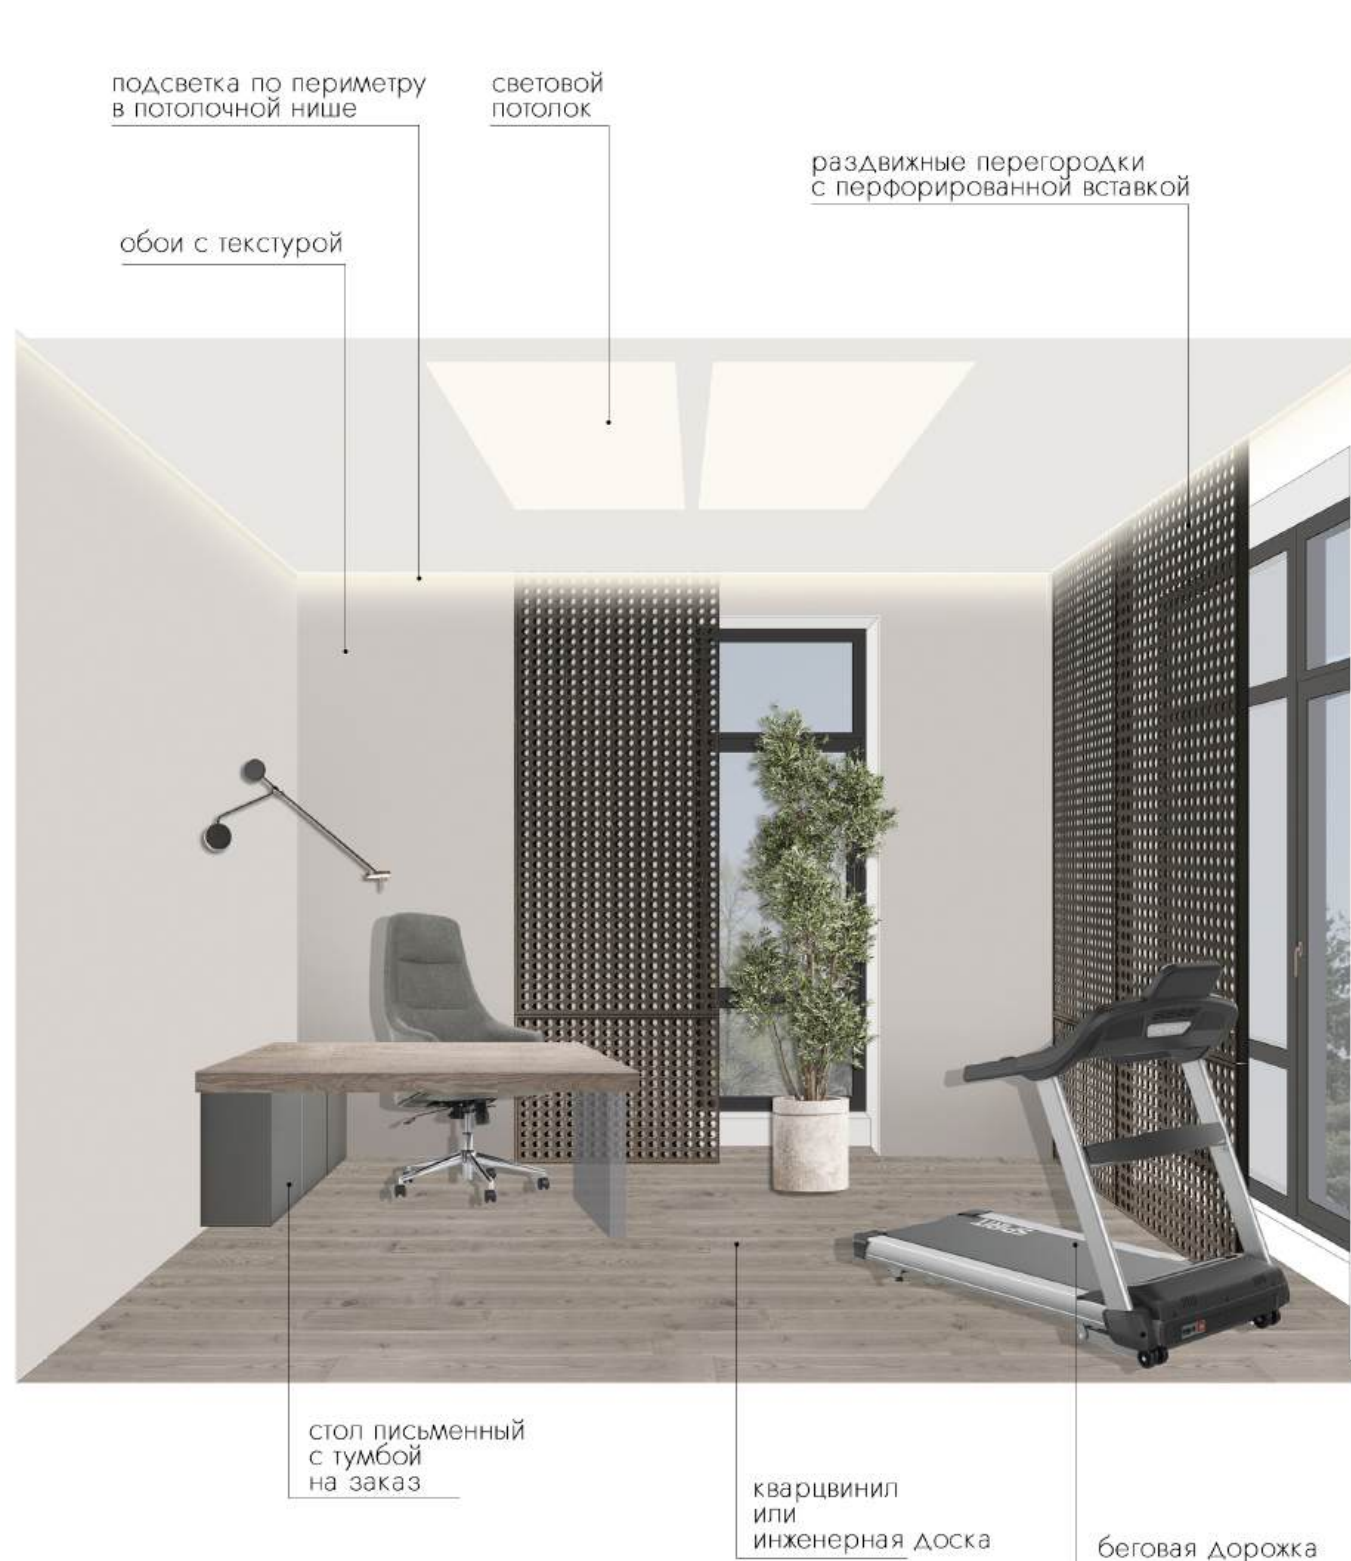

## Плинтус скрытый





# Детская. Коллаж-концепция

потолок ГКЛ,  
св-ники гипсовые  
встраиваемые  
ARTPOLE SGS37



покраска

Двери межкомнатные  
ACADEMY  
Slim Soft Touch  
высота полотна - 2200

пробковые панели  
на клей

игровая  
на втором ярусе:  
сетка по деревянному  
каркасу

стеллаж Лесли  
Plywood White  
91x41x202

покраска

закарнизная  
подсветка

светильники  
Китай



флизелиновые фотообои  
на стену Dekor Vinyl  
"Таинственный лес в тумане"  
400x270 см. OZON

Кровать двухъярусная  
CARVER 1 733263

бра  
на каждом уровне

тумба прикроватная  
Вита

панели мебельные  
с перфорацией  
для полок

Письменный стол  
Лесли Plywood White

стул Слинг  
вращающийся

шкаф трехсекционный HOFF  
Fun 134.4x190x51.6 см

кварцвинил  
или  
инженерная доска



Плинтус скрытый





# Спальня. Коллаж-концепция

отделка стены  
тонируемыми  
досками и рейками



потолок ГКЛ,  
св-ники гипсовые  
встраиваемые  
ARTPOLE SGS37



покраска

потолок  
декоративная  
краска (или шт-ка)

декоративная  
краска (или шт-ка)

подвесная конструкция  
металлокаркас, ГКЛ,  
отделка панелями  
из полиуретана под камень

отделка откоса  
досками со стены

покраска откоса

потолок ГКЛ  
в цвет стен

покраска

навесные кашпо  
с растениями

зеркало  
тонируемое

бра

закарнизная  
подсветка



Электрокамин паровой.  
Тумба из ЛДСП

Двери межкомнатные  
ACADEMY  
Slim Soft Touch  
высота полотна - 2200

торшер Китай

встраиваемый  
гипсовый  
светильник  
SUBRA-M 60

тумба  
подиум с нишей для тумб  
ЛДСП под дерево

столик туалетный с зеркалом и  
ящиком, WB, 1100x400

стул OZON

кварцвинил  
или инженерная  
доска

Плинтус скрытый





# Санузел 2 эт. Коллаж-концепция

потолок  
натяжной

покраска

короб под  
инсталляцию  
Панели полиуретан  
под травертин, на клей  
(или керамогранит  
600x1200)

дверь скрытая,  
реверсное открывание

полка из плитки

душ. система  
встраиваемая

подвесной унитаз  
с инсталляцией,  
гигиенический душ

экран ванны  
с нишей для ног  
и подсветкой

подсветка закарнизная  
и вертикальная  
(до борта ванны или до полки)

короб с нишей

полки в нише

встраиваемый св-ник  
MAYTONI  
Dot DL028-2-01W  
для натяжных потолков



композиция из сухой травы  
с подсветкой  
за стеклянной  
перегородкой  
(доступ из гардеробной)

встроенный шкаф  
с открытой нишей  
и ящиками

панели полиуретан  
под травертин, на клей  
(или керамогранит  
600x1200)

покраска

зеркало органической  
формы Continent

встраиваемый смеситель

раковина из бетона,  
тумбы по бокам


керамогранит 600x1200  
ИТАЛОН СНОУ  
натуральный

керамогранит 600x1200  
ИТАЛОН СНОУ  
натуральный





План опорный, 1 этаж

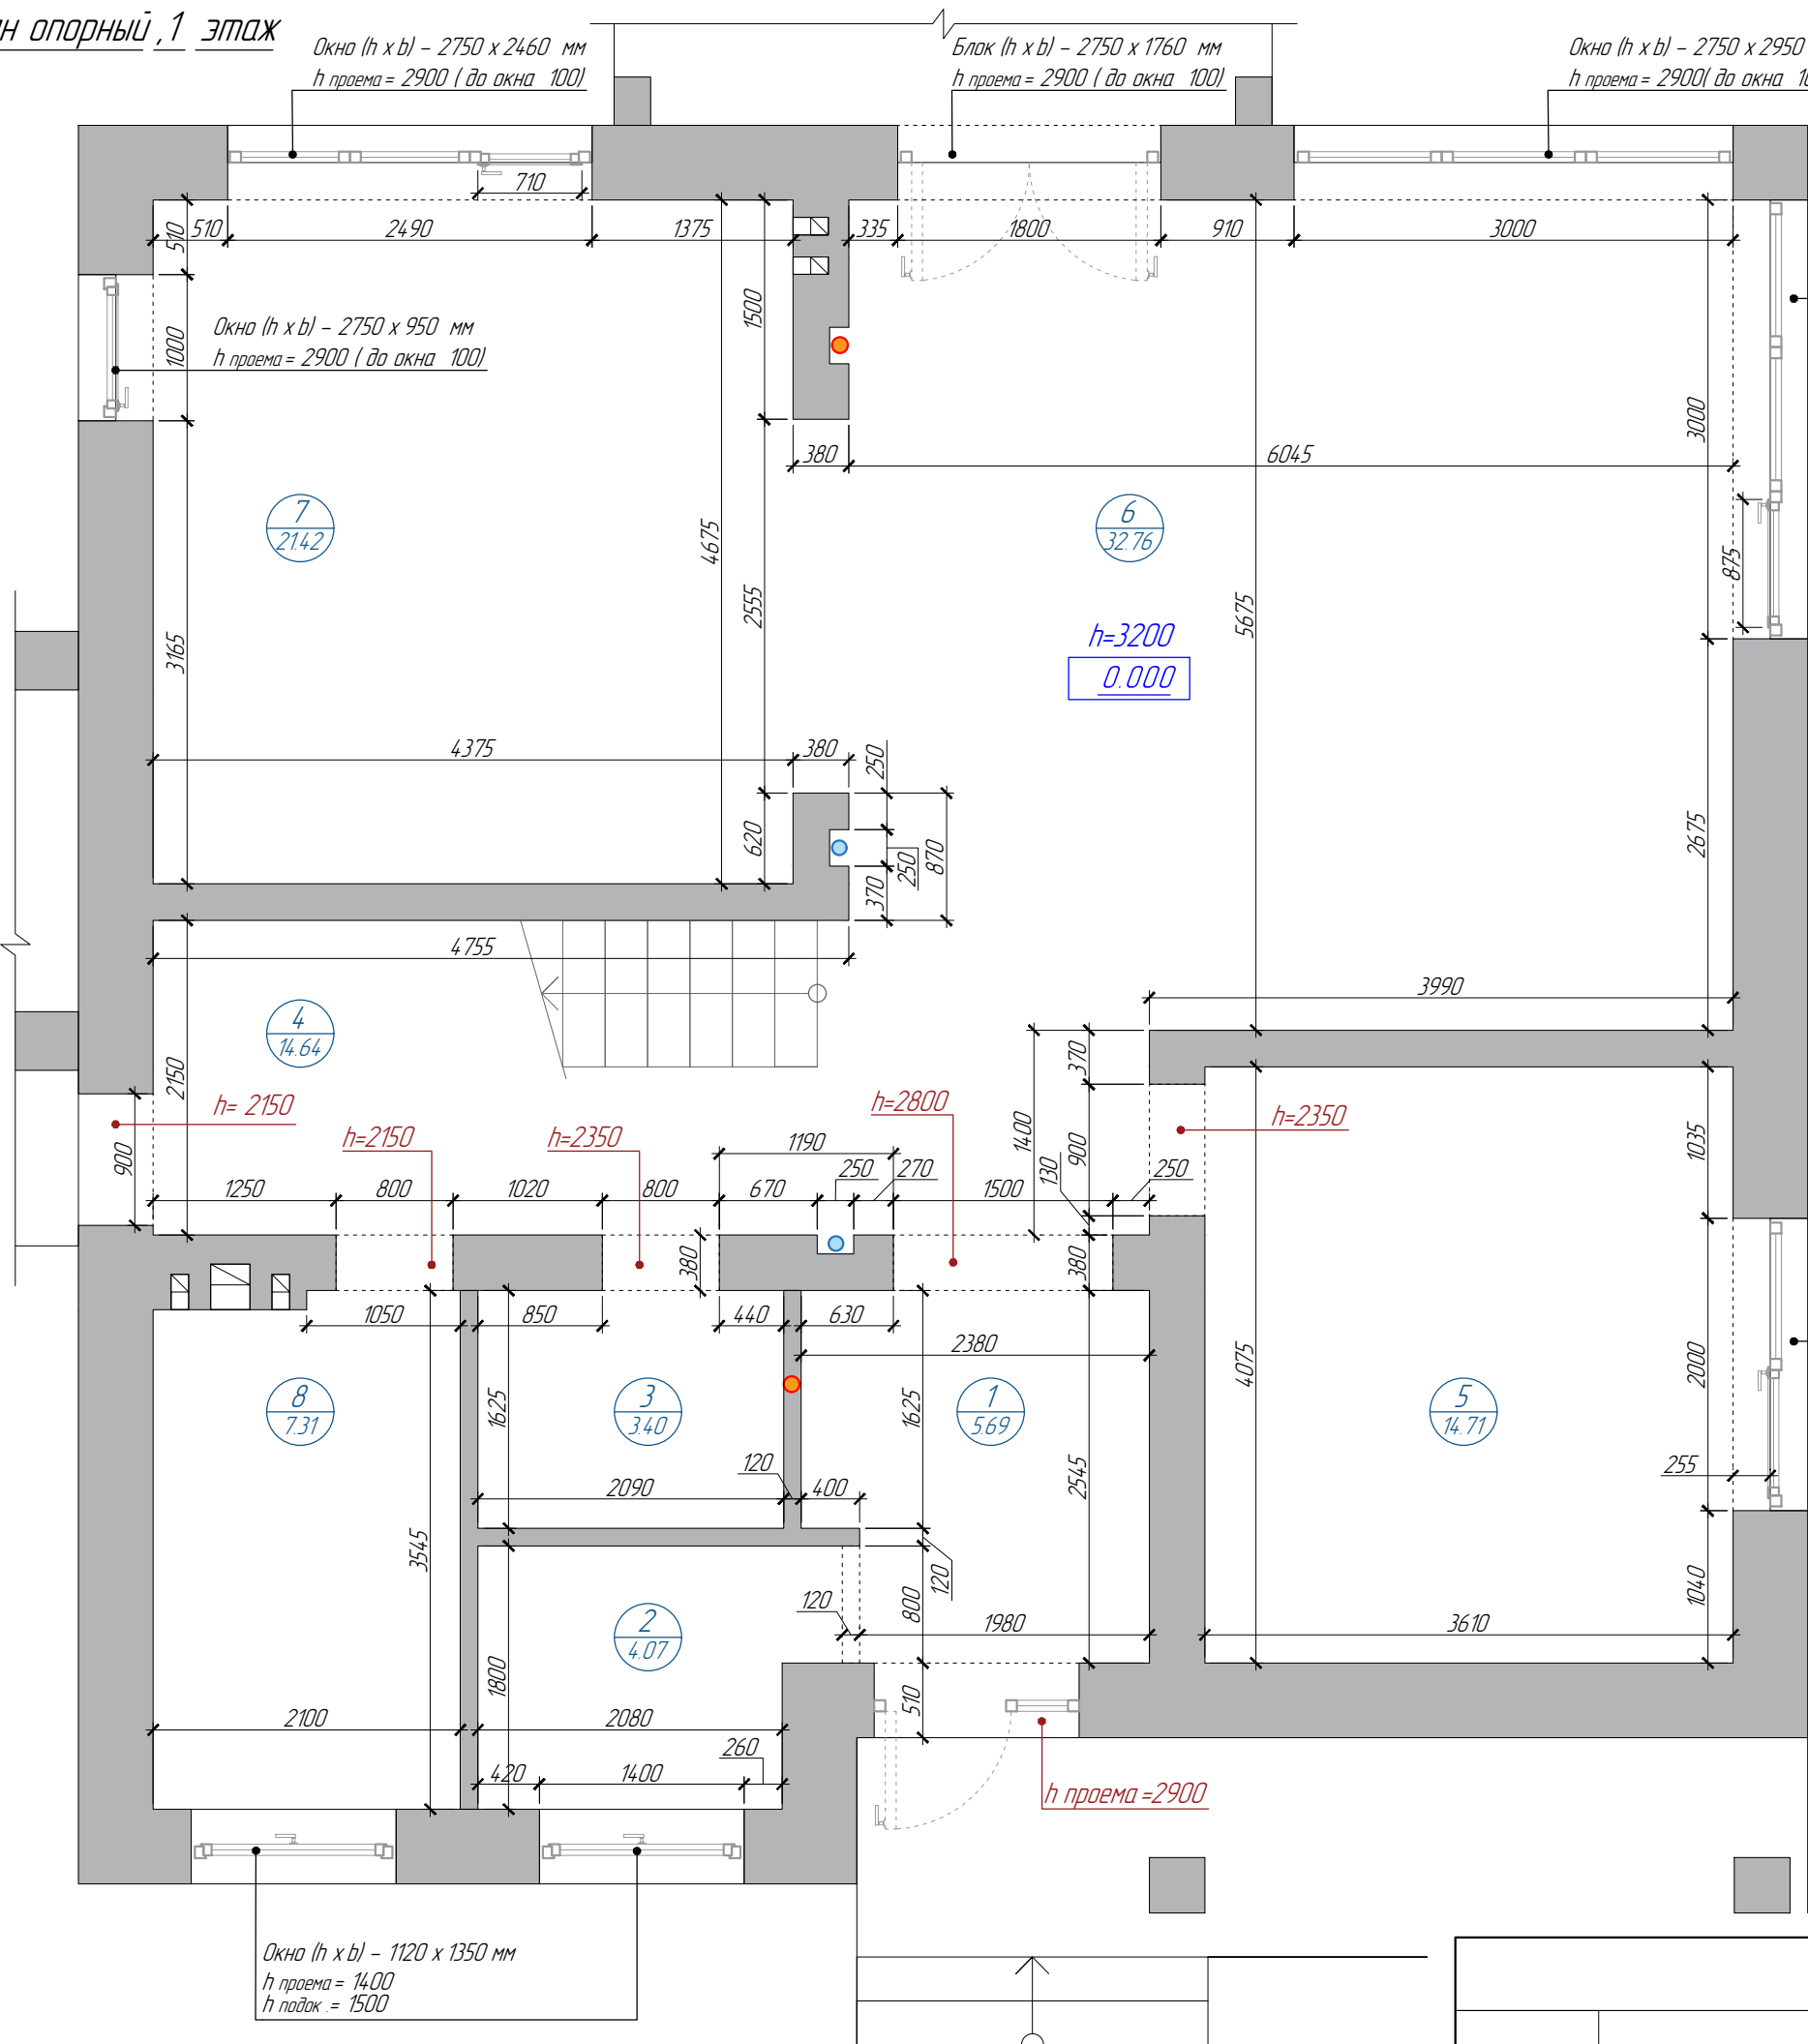

| Экспликация помещений        |        |                        |                          |        |            |
|------------------------------|--------|------------------------|--------------------------|--------|------------|
| Этаж                         | № пом. | Наименование помещения | Площадь , м <sup>2</sup> |        | Примечание |
|                              |        |                        | осн.                     | вспом. |            |
| 1                            | 1      | Прихожая               |                          | 5.69   |            |
|                              | 2      | Гардеробная            |                          | 4.07   |            |
|                              | 3      | Санузел гостей         |                          | 3.40   |            |
|                              | 4      | Лестничный холл        |                          | 14.64  |            |
|                              | 5      | Комната няни           | 14.71                    |        |            |
|                              | 6      | Гостиная               | 32.76                    |        |            |
|                              | 7      | Кухня –столовая        | 21.42                    |        |            |
|                              | 8      | Котельная              |                          | 7.31   |            |
| 2                            | 10     | Лестничный холл        |                          | 8.54   |            |
|                              | 11     | Мастер –спальня        | 20.45                    |        |            |
|                              | 12     | Ванная комната         |                          | 6.33   |            |
|                              | 13     | Гардеробная            |                          | 4.25   |            |
|                              | 14     | Детская комната        | 20.49                    |        |            |
|                              | 15     | Кабинет                | 14.71                    |        |            |
|                              | 16     | Санузел                |                          | 6.08   |            |
|                              | 17     | Гостевая комната       | 15.11                    |        |            |
|                              |        | Итого по помещениям    | 139.65                   | 60.31  |            |
| Общая площадь помещений дома |        |                        | 199.96                   |        |            |

УСЛОВНЫЕ ОБОЗНАЧЕНИЯ

- стены и перегородки из керамоблока
- стояк канализации
- стояк ливневой канализации

кп РАЙТ ЭКО


Архитектор Овчарова Ольга

Опорный план. 1 этаж

ООО ЧИЛДРОН  
PROJECT



План опорный, 2 этаж

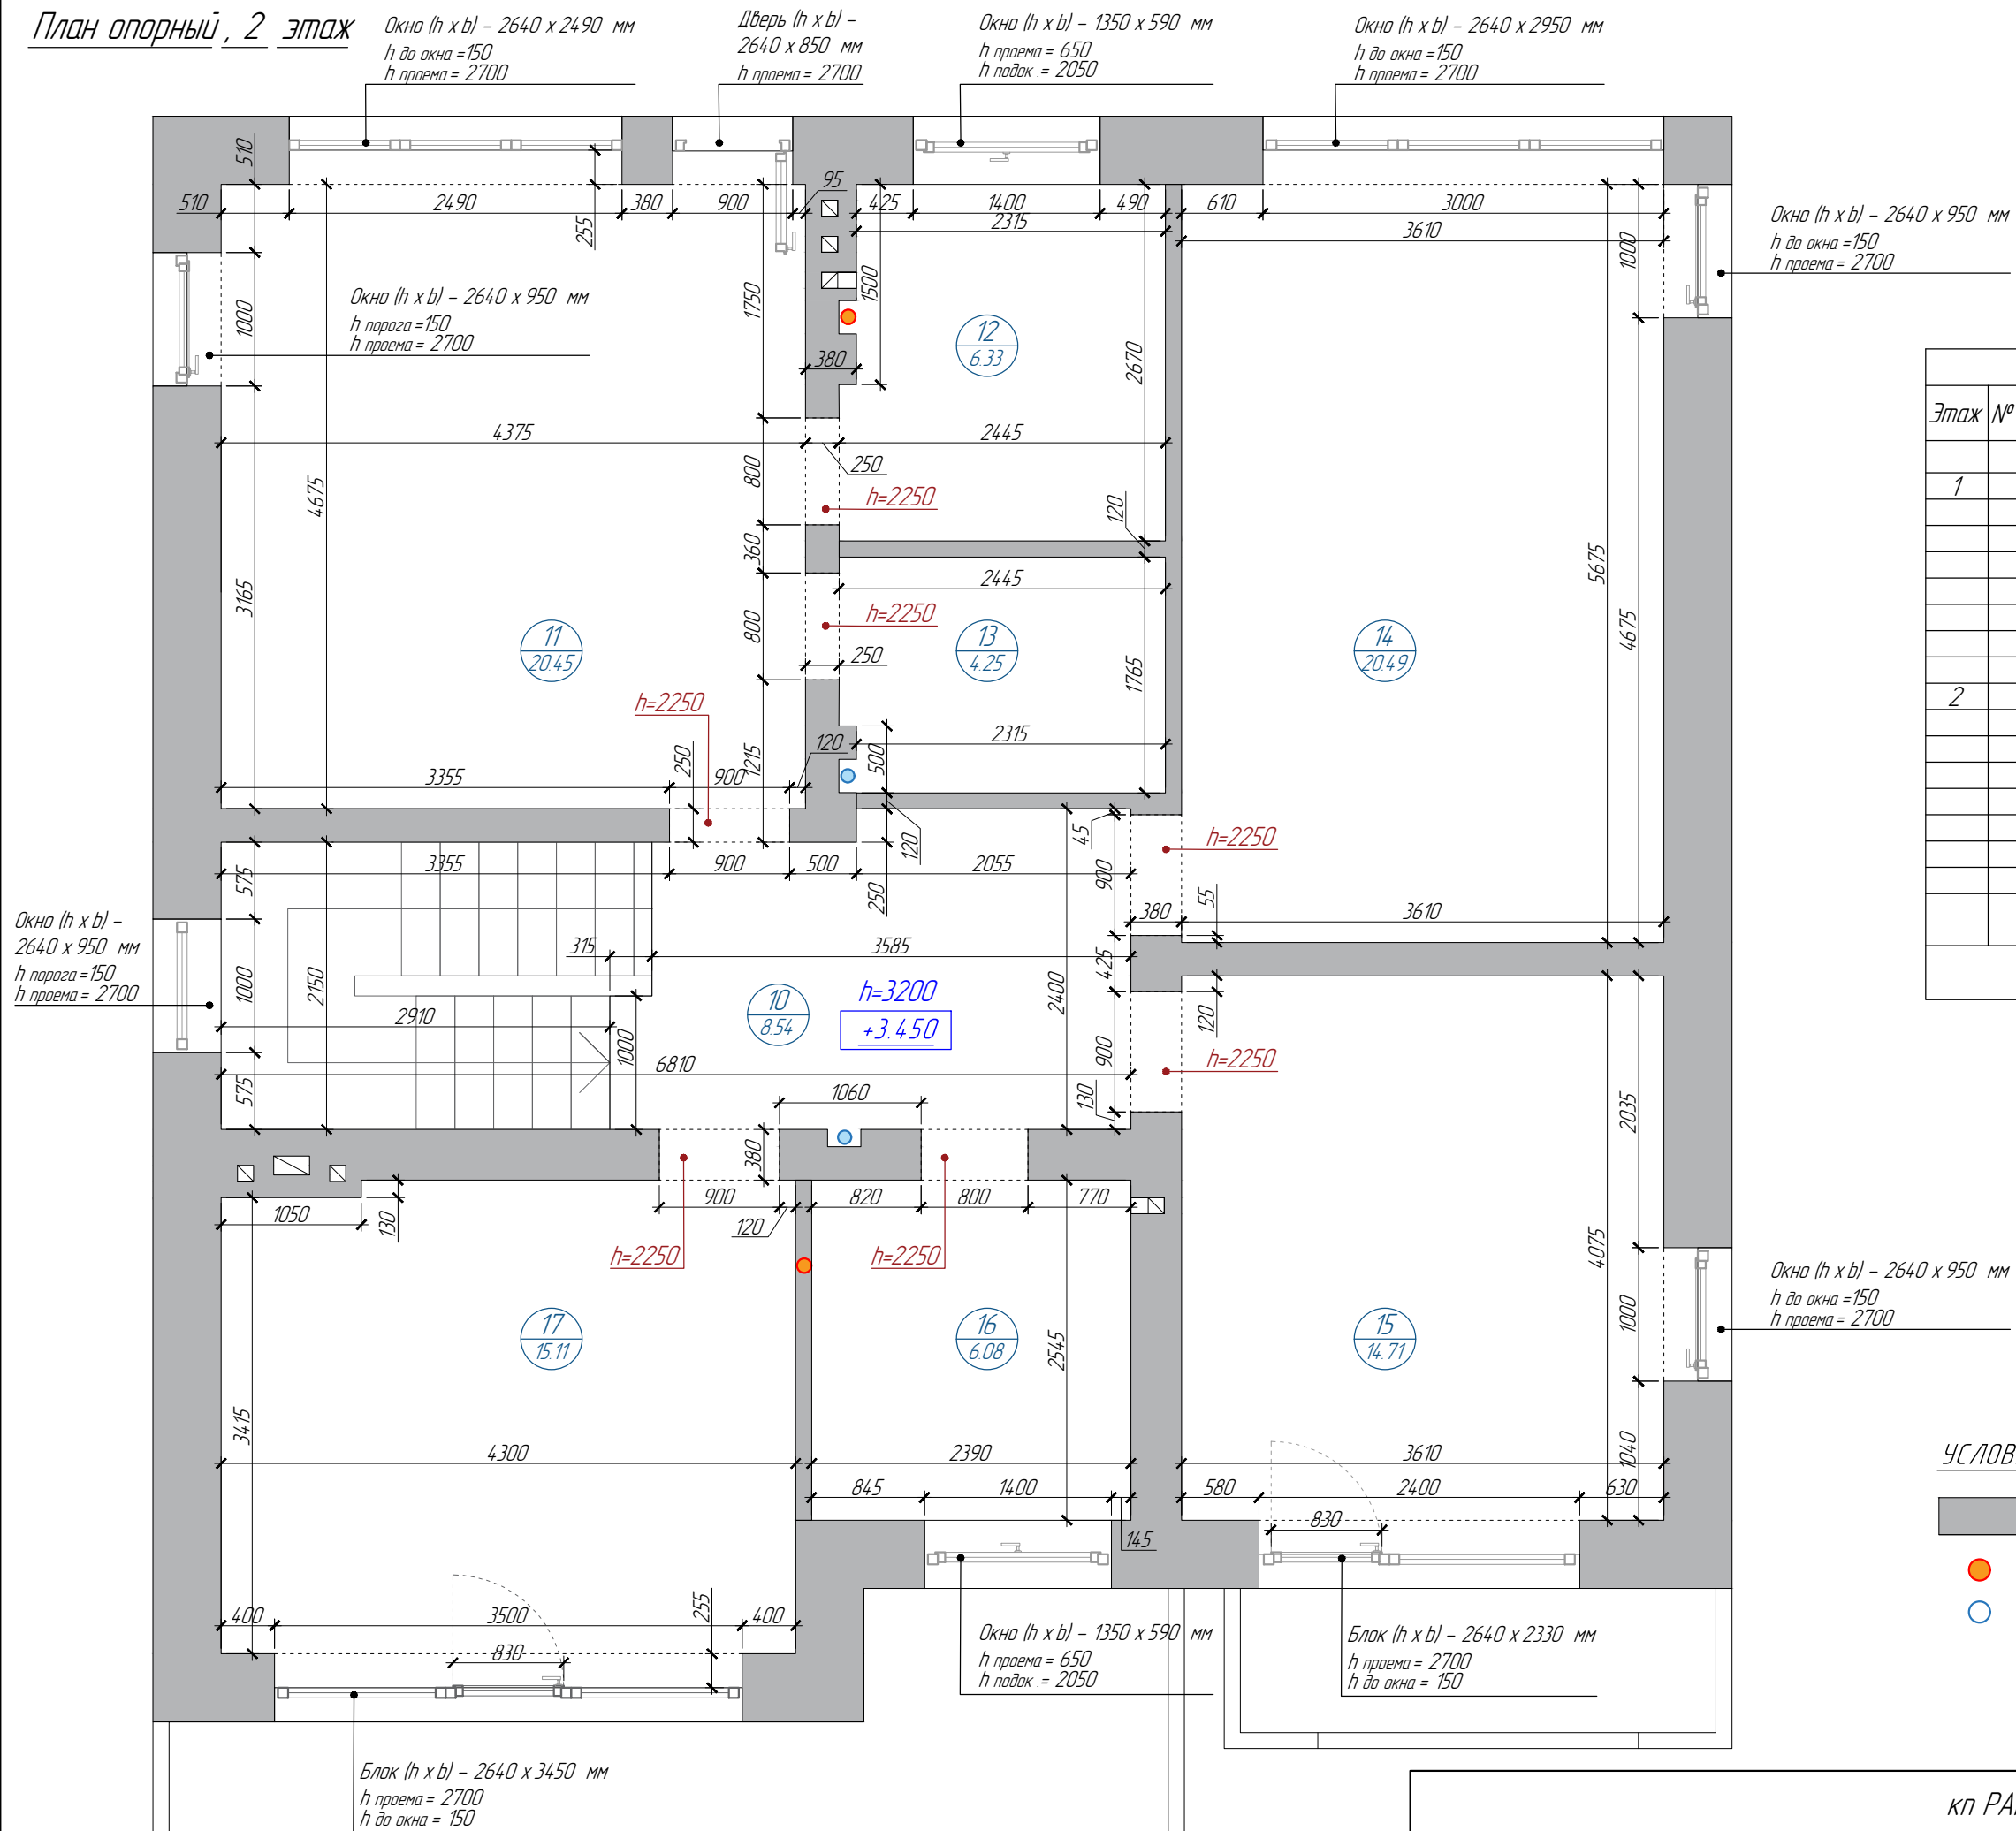

| Экспликация помещений        |        |                        |                         |        |            |
|------------------------------|--------|------------------------|-------------------------|--------|------------|
| Этаж                         | № пом. | Наименование помещения | Площадь, м <sup>2</sup> |        | Примечание |
|                              |        |                        | осн.                    | вспом. |            |
| 1                            | 1      | Прихожая               |                         | 5.69   |            |
|                              | 2      | Гардеробная            |                         | 4.07   |            |
|                              | 3      | Санузел гостевой       |                         | 3.40   |            |
|                              | 4      | Лестничный холл        |                         | 14.64  |            |
|                              | 5      | Комната няни           | 14.71                   |        |            |
|                              | 6      | Гостиная               | 32.76                   |        |            |
|                              | 7      | Кухня -столовая        | 214.2                   |        |            |
|                              | 8      | Котельная              |                         | 7.31   |            |
| 2                            | 10     | Лестничный холл        |                         | 8.54   |            |
|                              | 11     | Мастер -спальня        | 20.45                   |        |            |
|                              | 12     | Ванная комната         |                         | 6.33   |            |
|                              | 13     | Гардеробная            |                         | 4.25   |            |
|                              | 14     | Детская комната        | 20.49                   |        |            |
|                              | 15     | Кабинет                | 14.71                   |        |            |
|                              | 16     | Санузел                |                         | 6.08   |            |
|                              | 17     | Гостевая комната       | 15.11                   |        |            |
|                              |        | Итого по помещениям    | 139.65                  | 60.31  |            |
| Общая площадь помещений дома |        |                        | 199.96                  |        |            |

УСЛОВНЫЕ ОБОЗНАЧЕНИЯ


-  стены и перегородки из керамблока
-  стояк канализации
-  стоякливневой канализации

кп РАЙТ ЭКО

Опорный план. 2 этаж

ΟΙΚΟΧΑΡΩΝ  
PROJECT



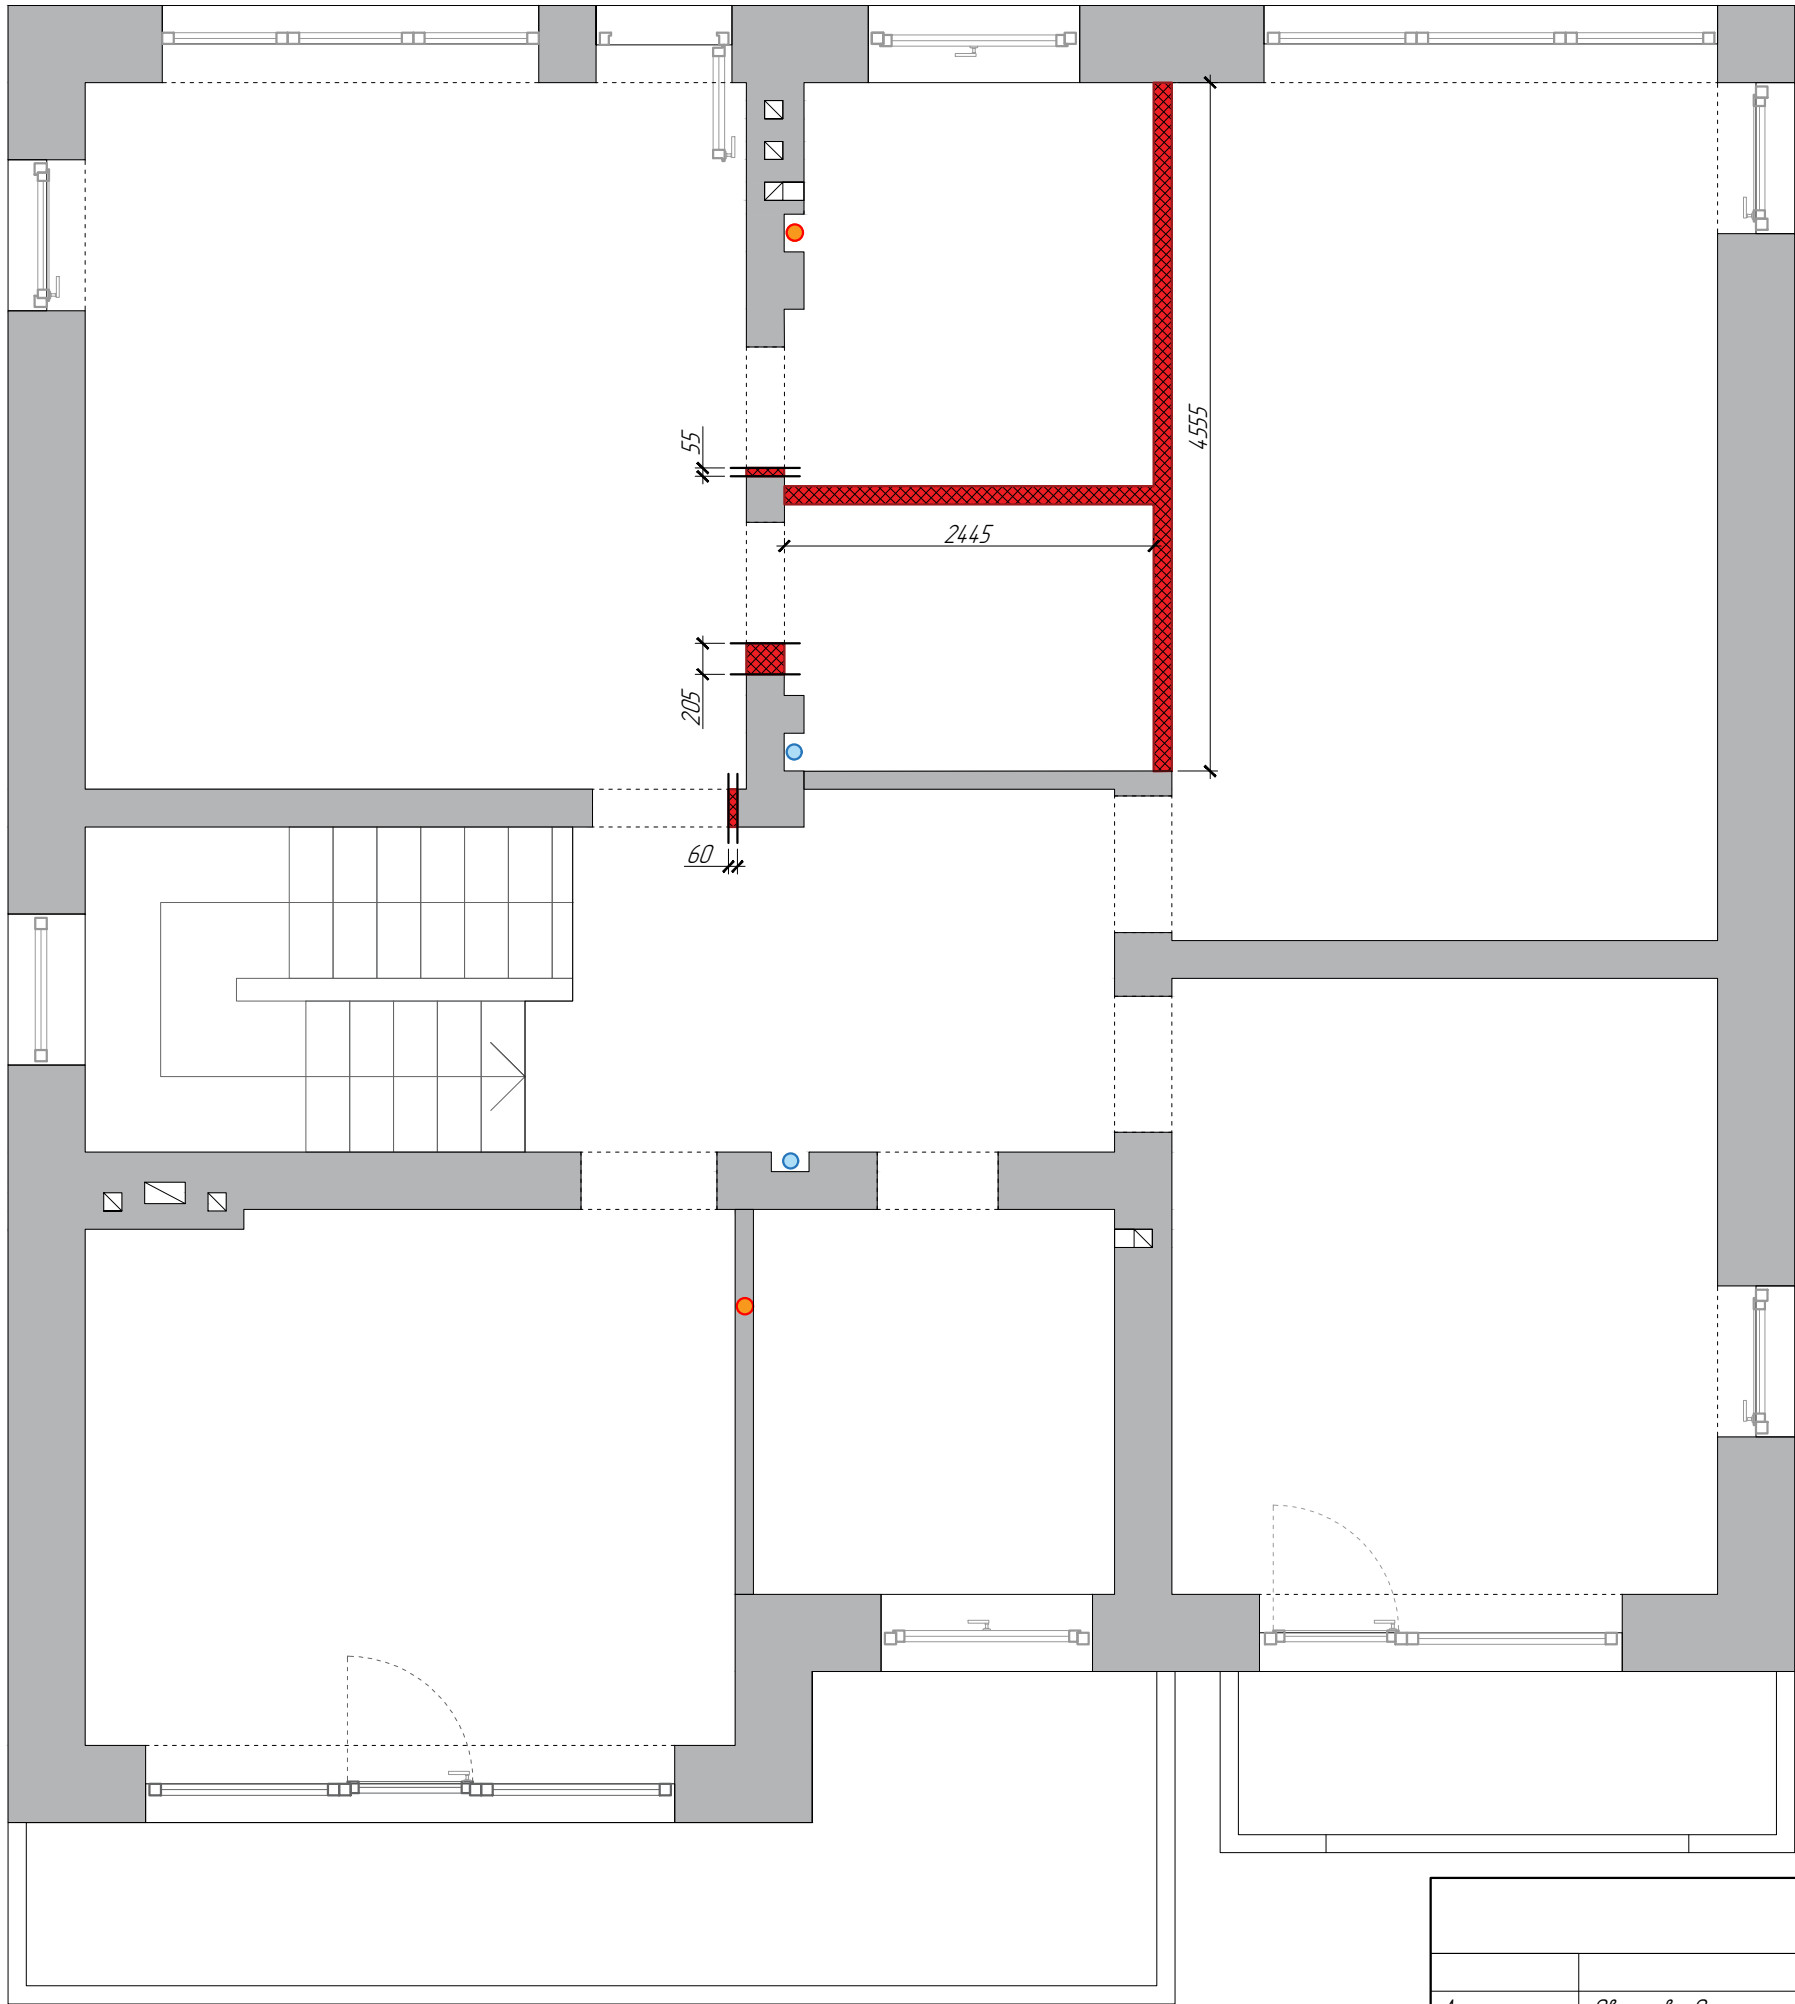

УСЛОВНЫЕ ОБОЗНАЧЕНИЯ

- стены и перегородки из керамоблока
- стояк канализации
- стояк ливневой канализации
- демонтируемые перегородки и их фрагменты




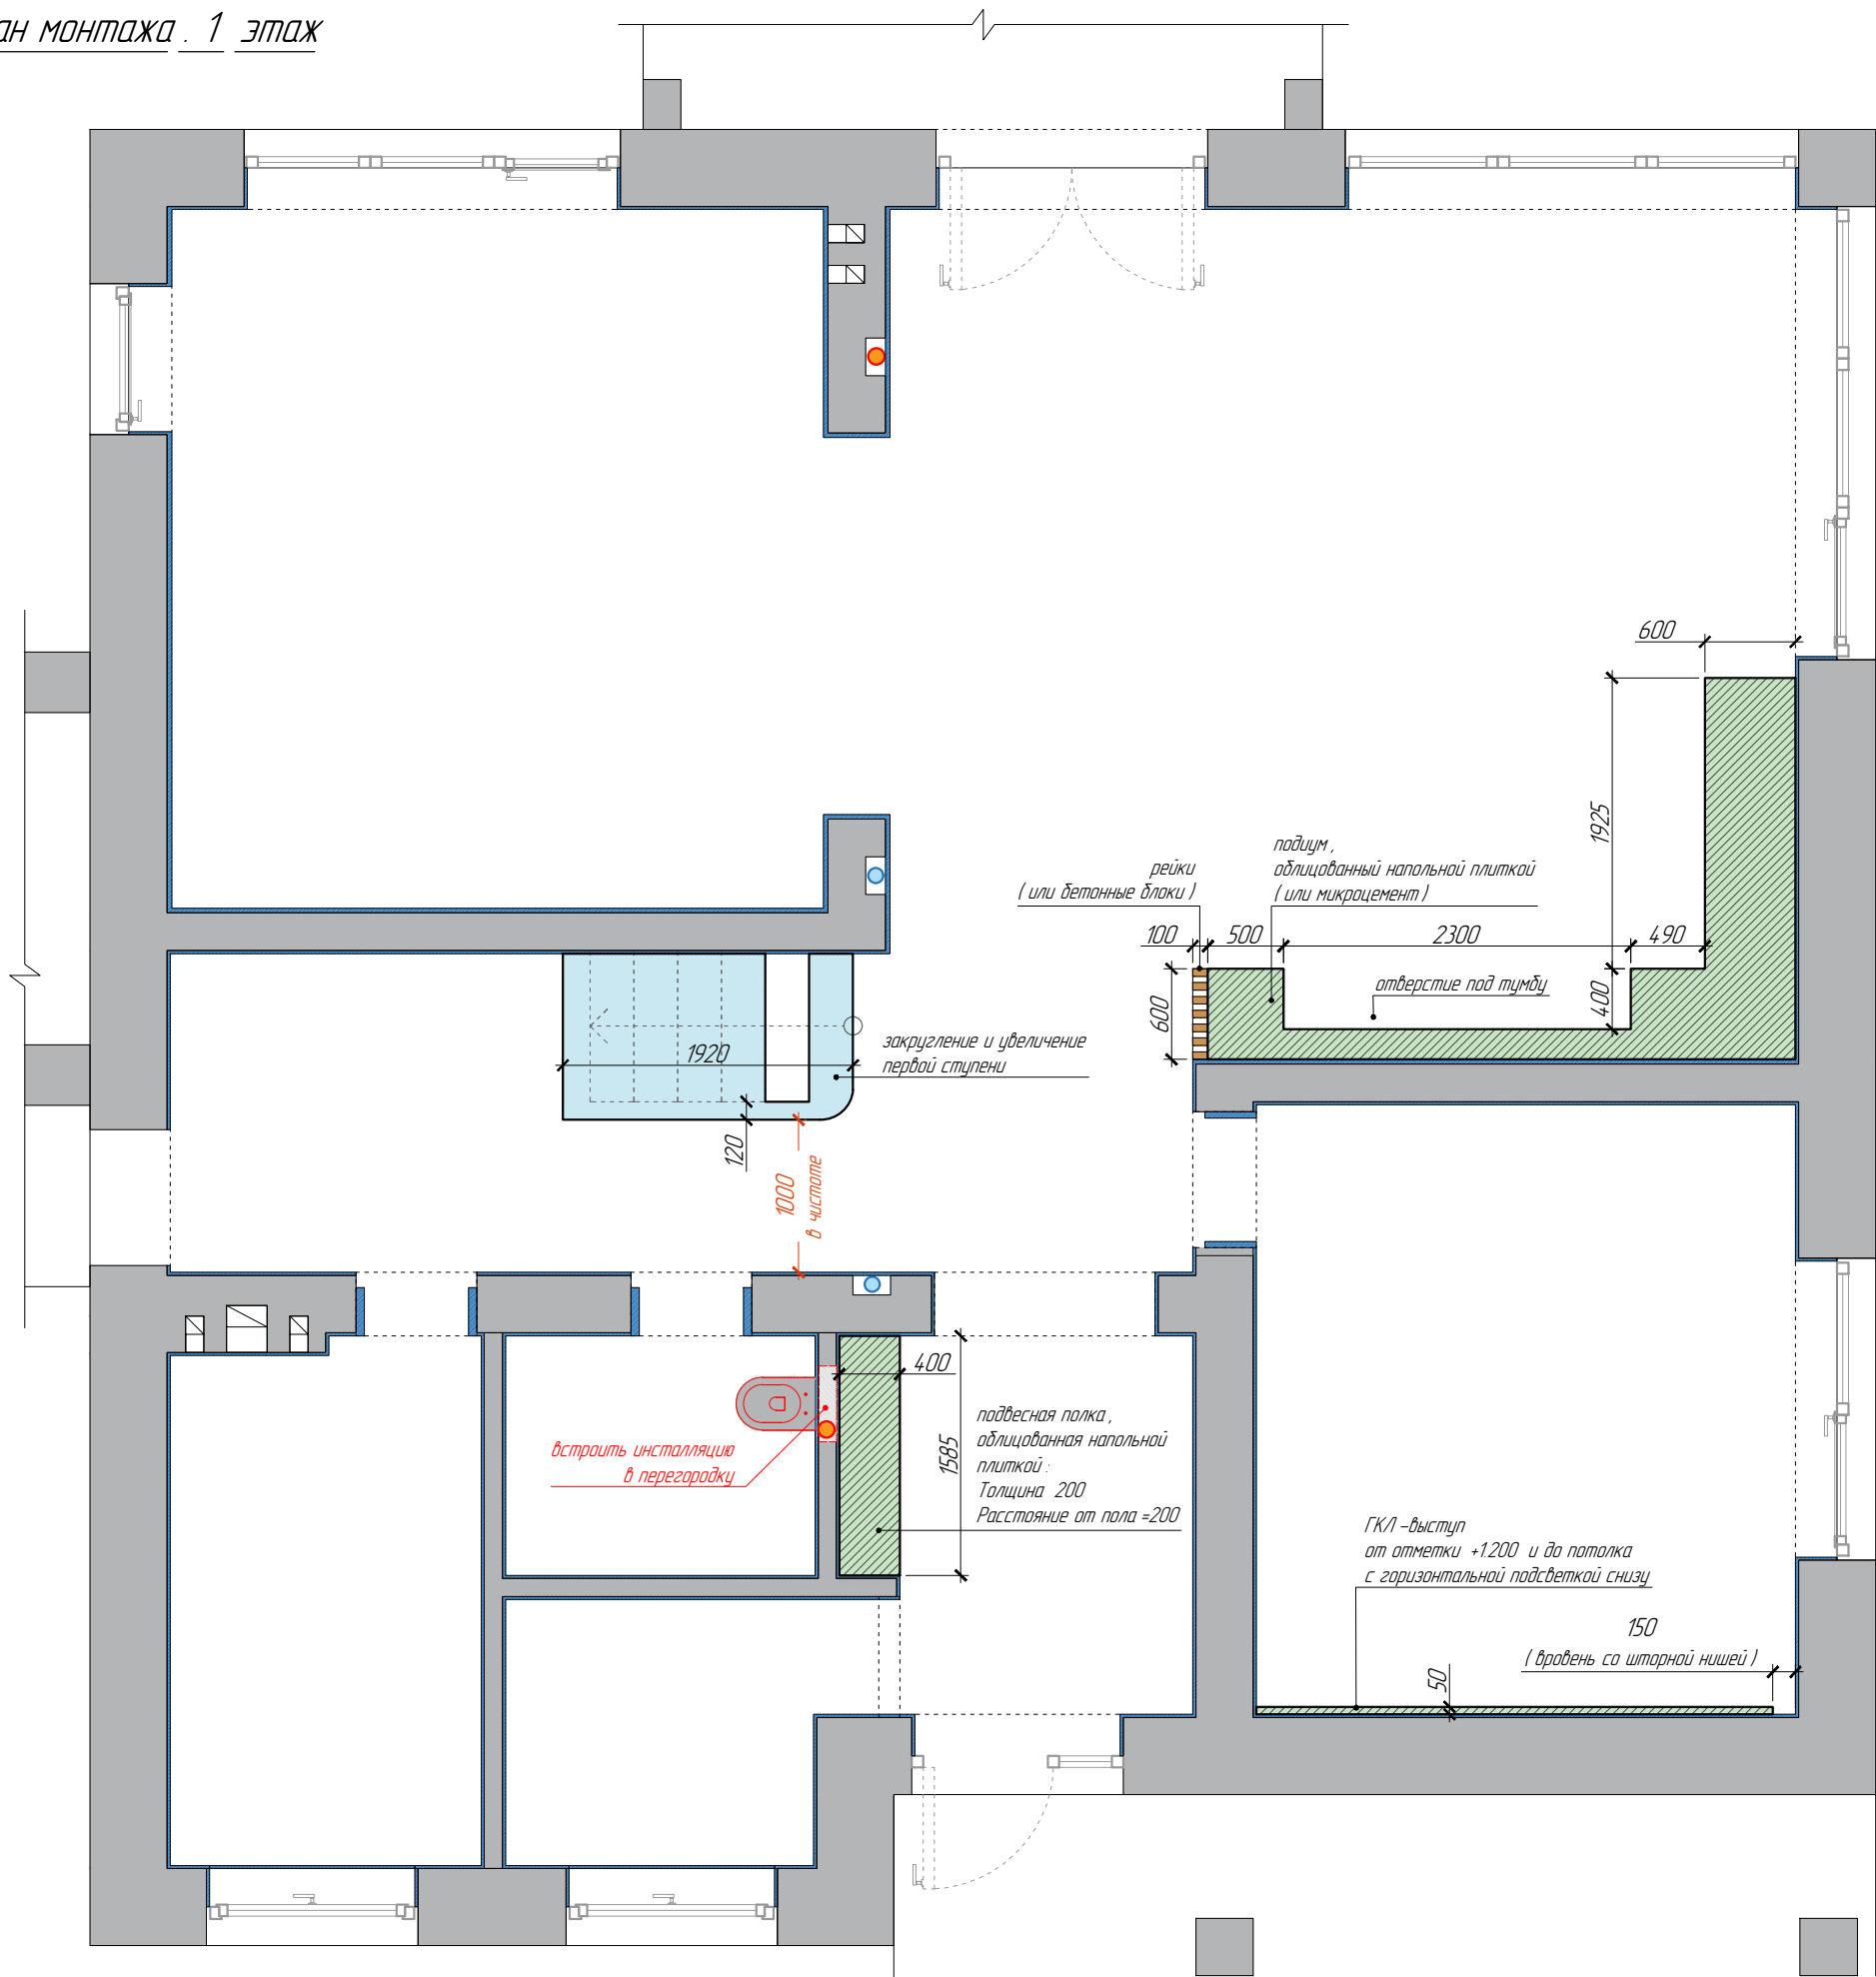


Схема подиума в гостиной

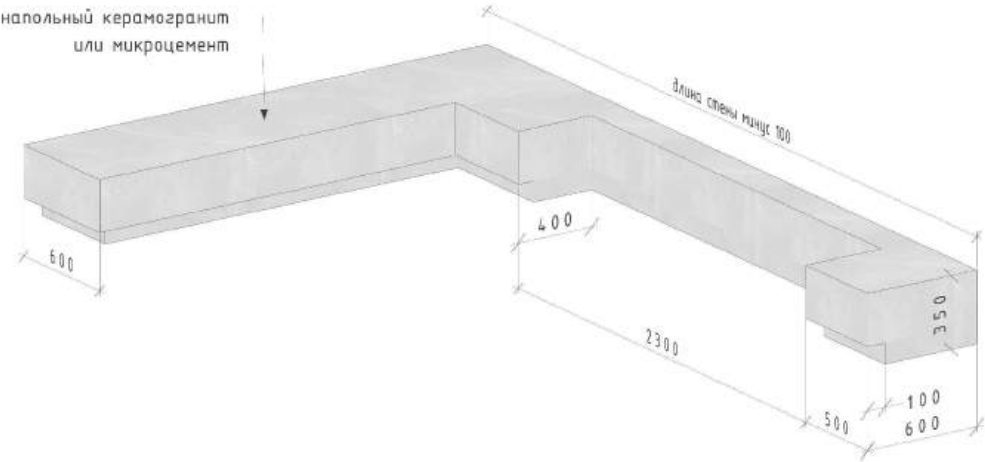

УСЛОВНЫЕ ОБОЗНАЧЕНИЯ

- стены и перегородки из керамоблока
- стояк канализации
- стояк ливневой канализации
- возводимые перегородки из пазогребневых блоков
- возводимые перегородки из керамоблоков
- возводимые конструкции из ГКЛВ
- важные размеры
- штукатурный слой

ПРИМЕЧАНИЯ

- Все конструкции возводятся с отм. 0.000 до отметки потолка, если не указано иное
- Внутренние и внешние углы, к которым будет примыкать встроенная мебель, вывести 90° как на плане, так и по вертикали.


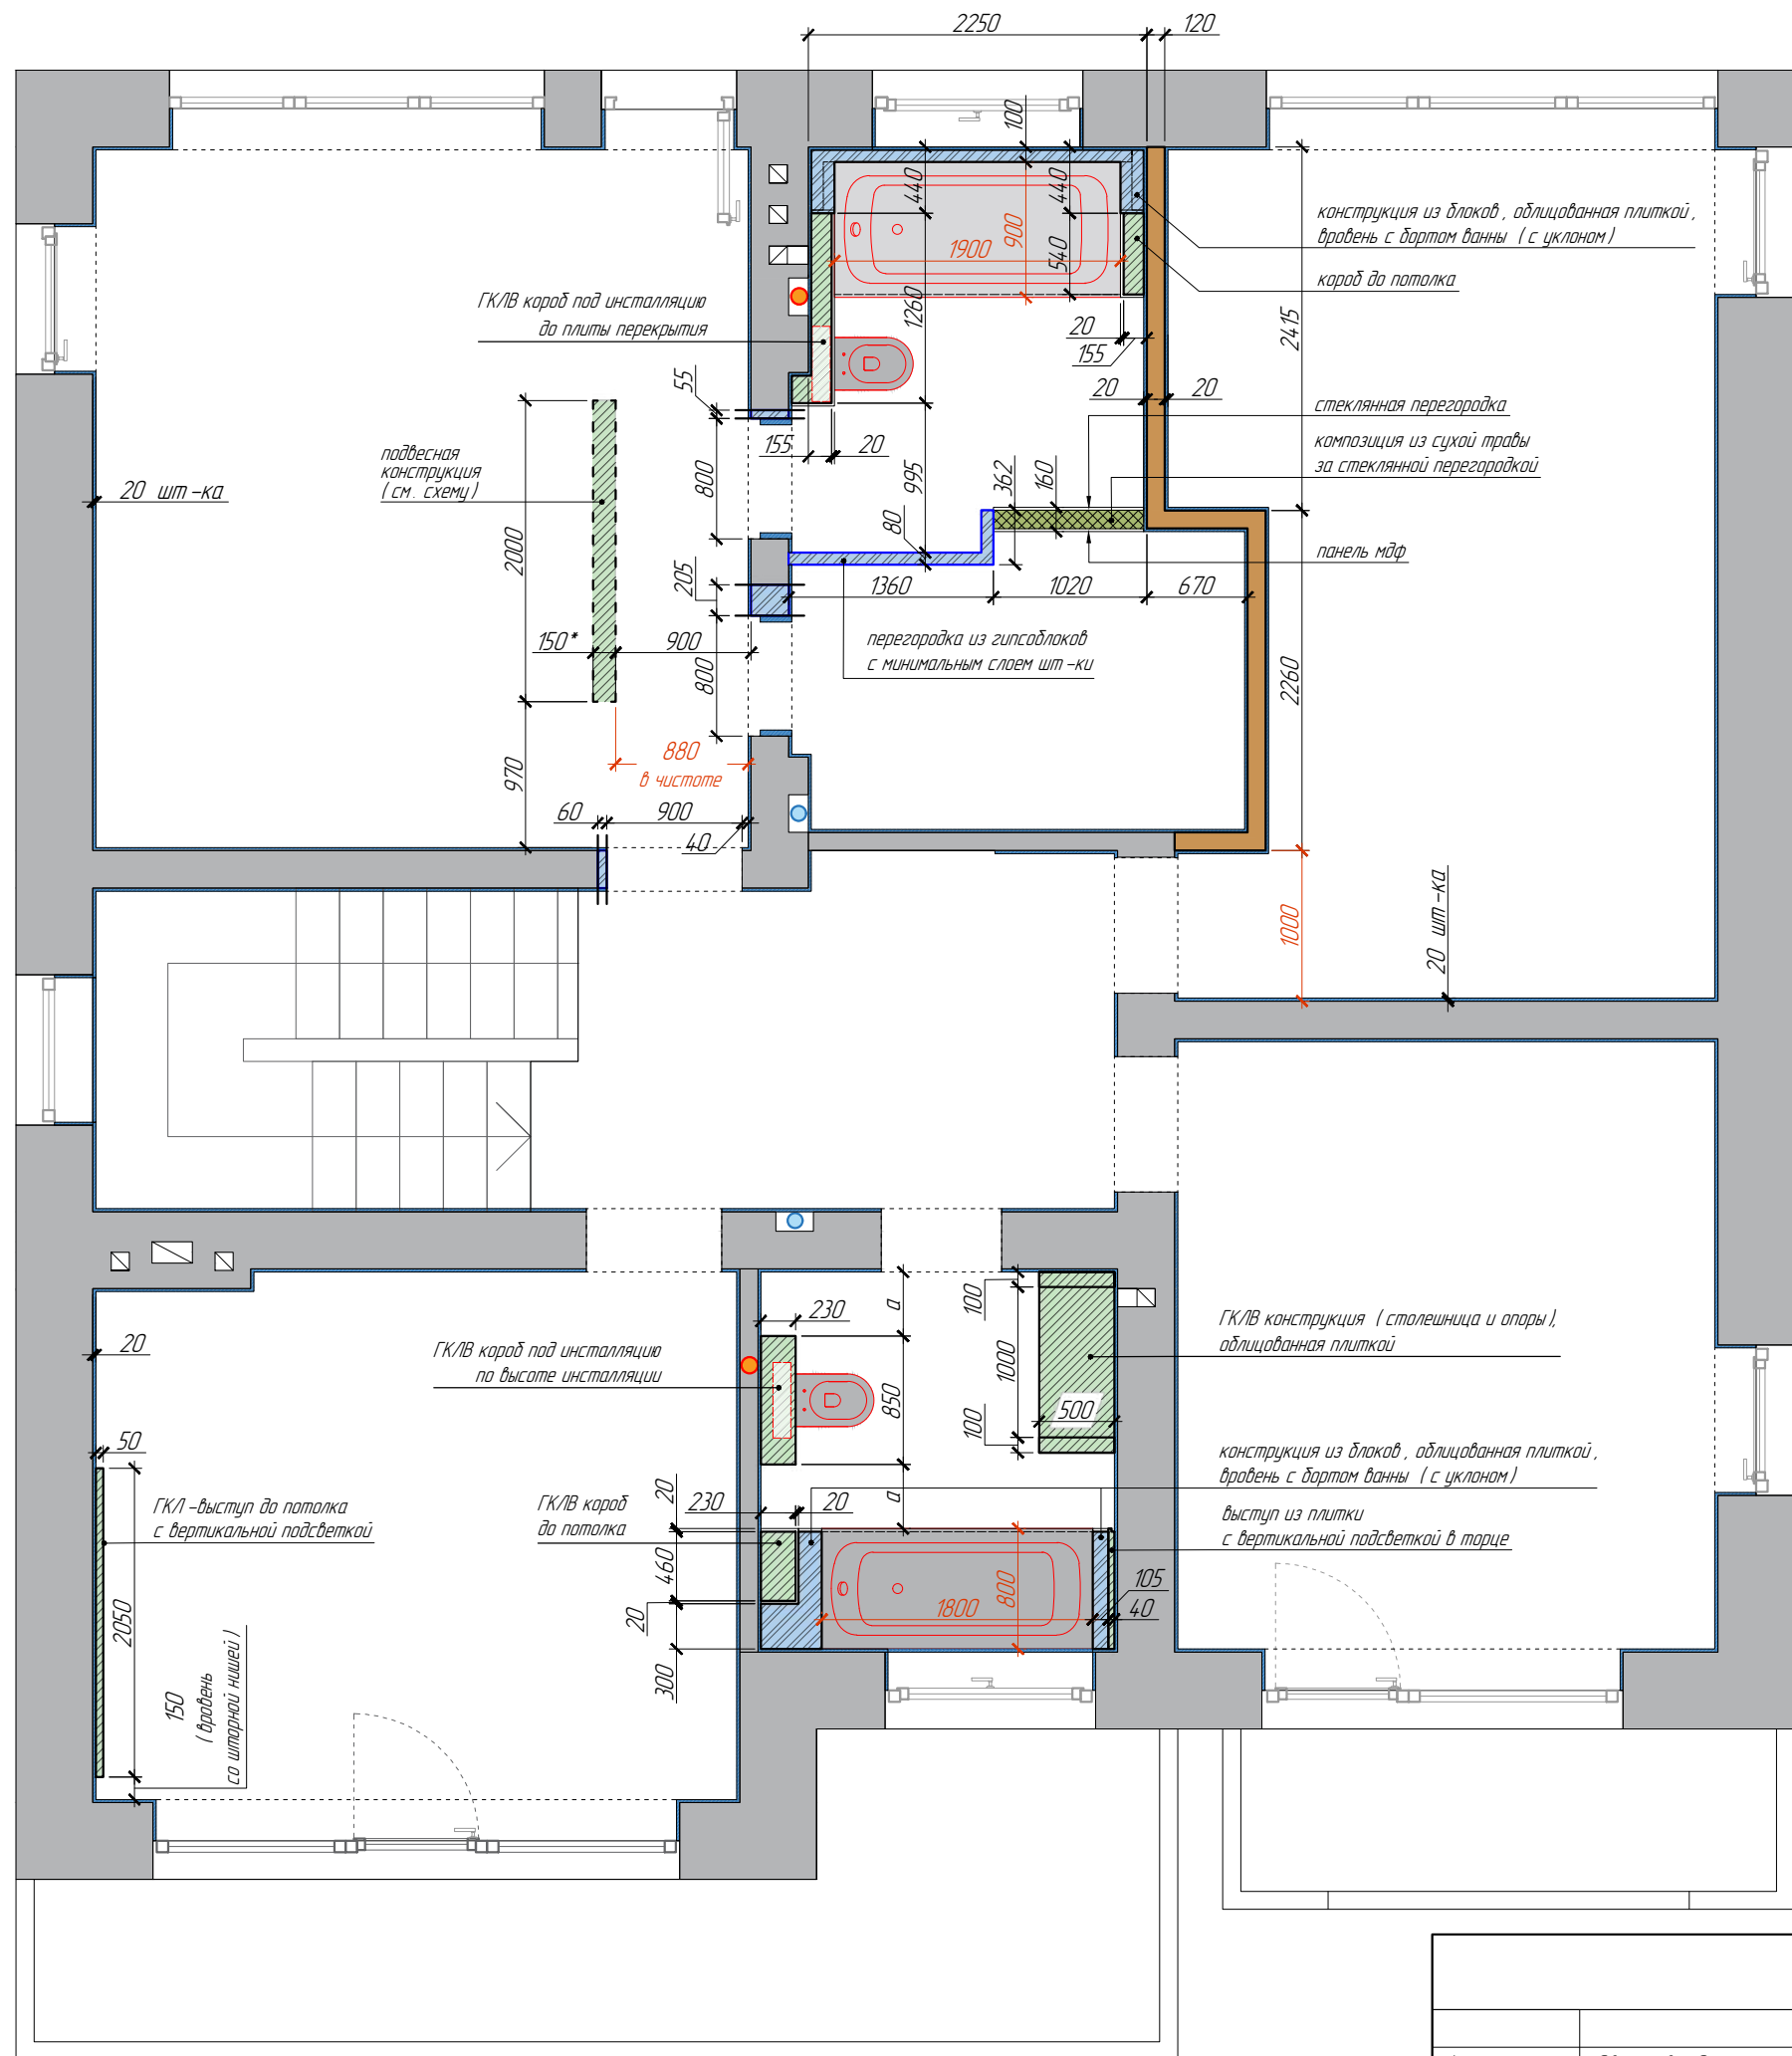


Схема подвесной конструкции под ТВ в спальне

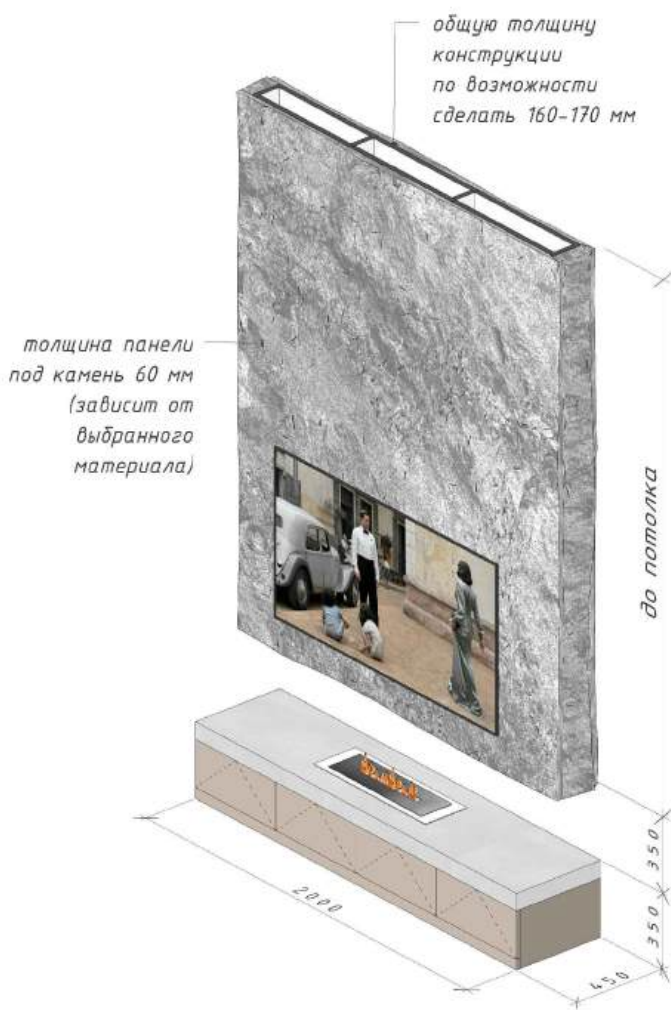

УСЛОВНЫЕ ОБОЗНАЧЕНИЯ

- стены и перегородки из керамоблока
- стояк канализации
- стоякливневой канализации
- возводимые перегородки из пазогребневыхблоков
- возводимые перегородки из керамоблоков
- возводимые конструкции из ГК/ЛВ
- важные размеры
- штукатурный слой

ПРИМЕЧАНИЯ

- Все конструкции возводятся с отм. 0.000 до отметки потолка, если не указано иное
- Внутренние и внешние углы, к которым будет примыкать встраиваемая мебель, вывести 90° как на плане, так и по вертикали.

кп РАЙТ ЭКО


План монтажа 2 этаж

ООО ЧАЛОВА

Архитектор Овчарова Ольга



План 1 этажа

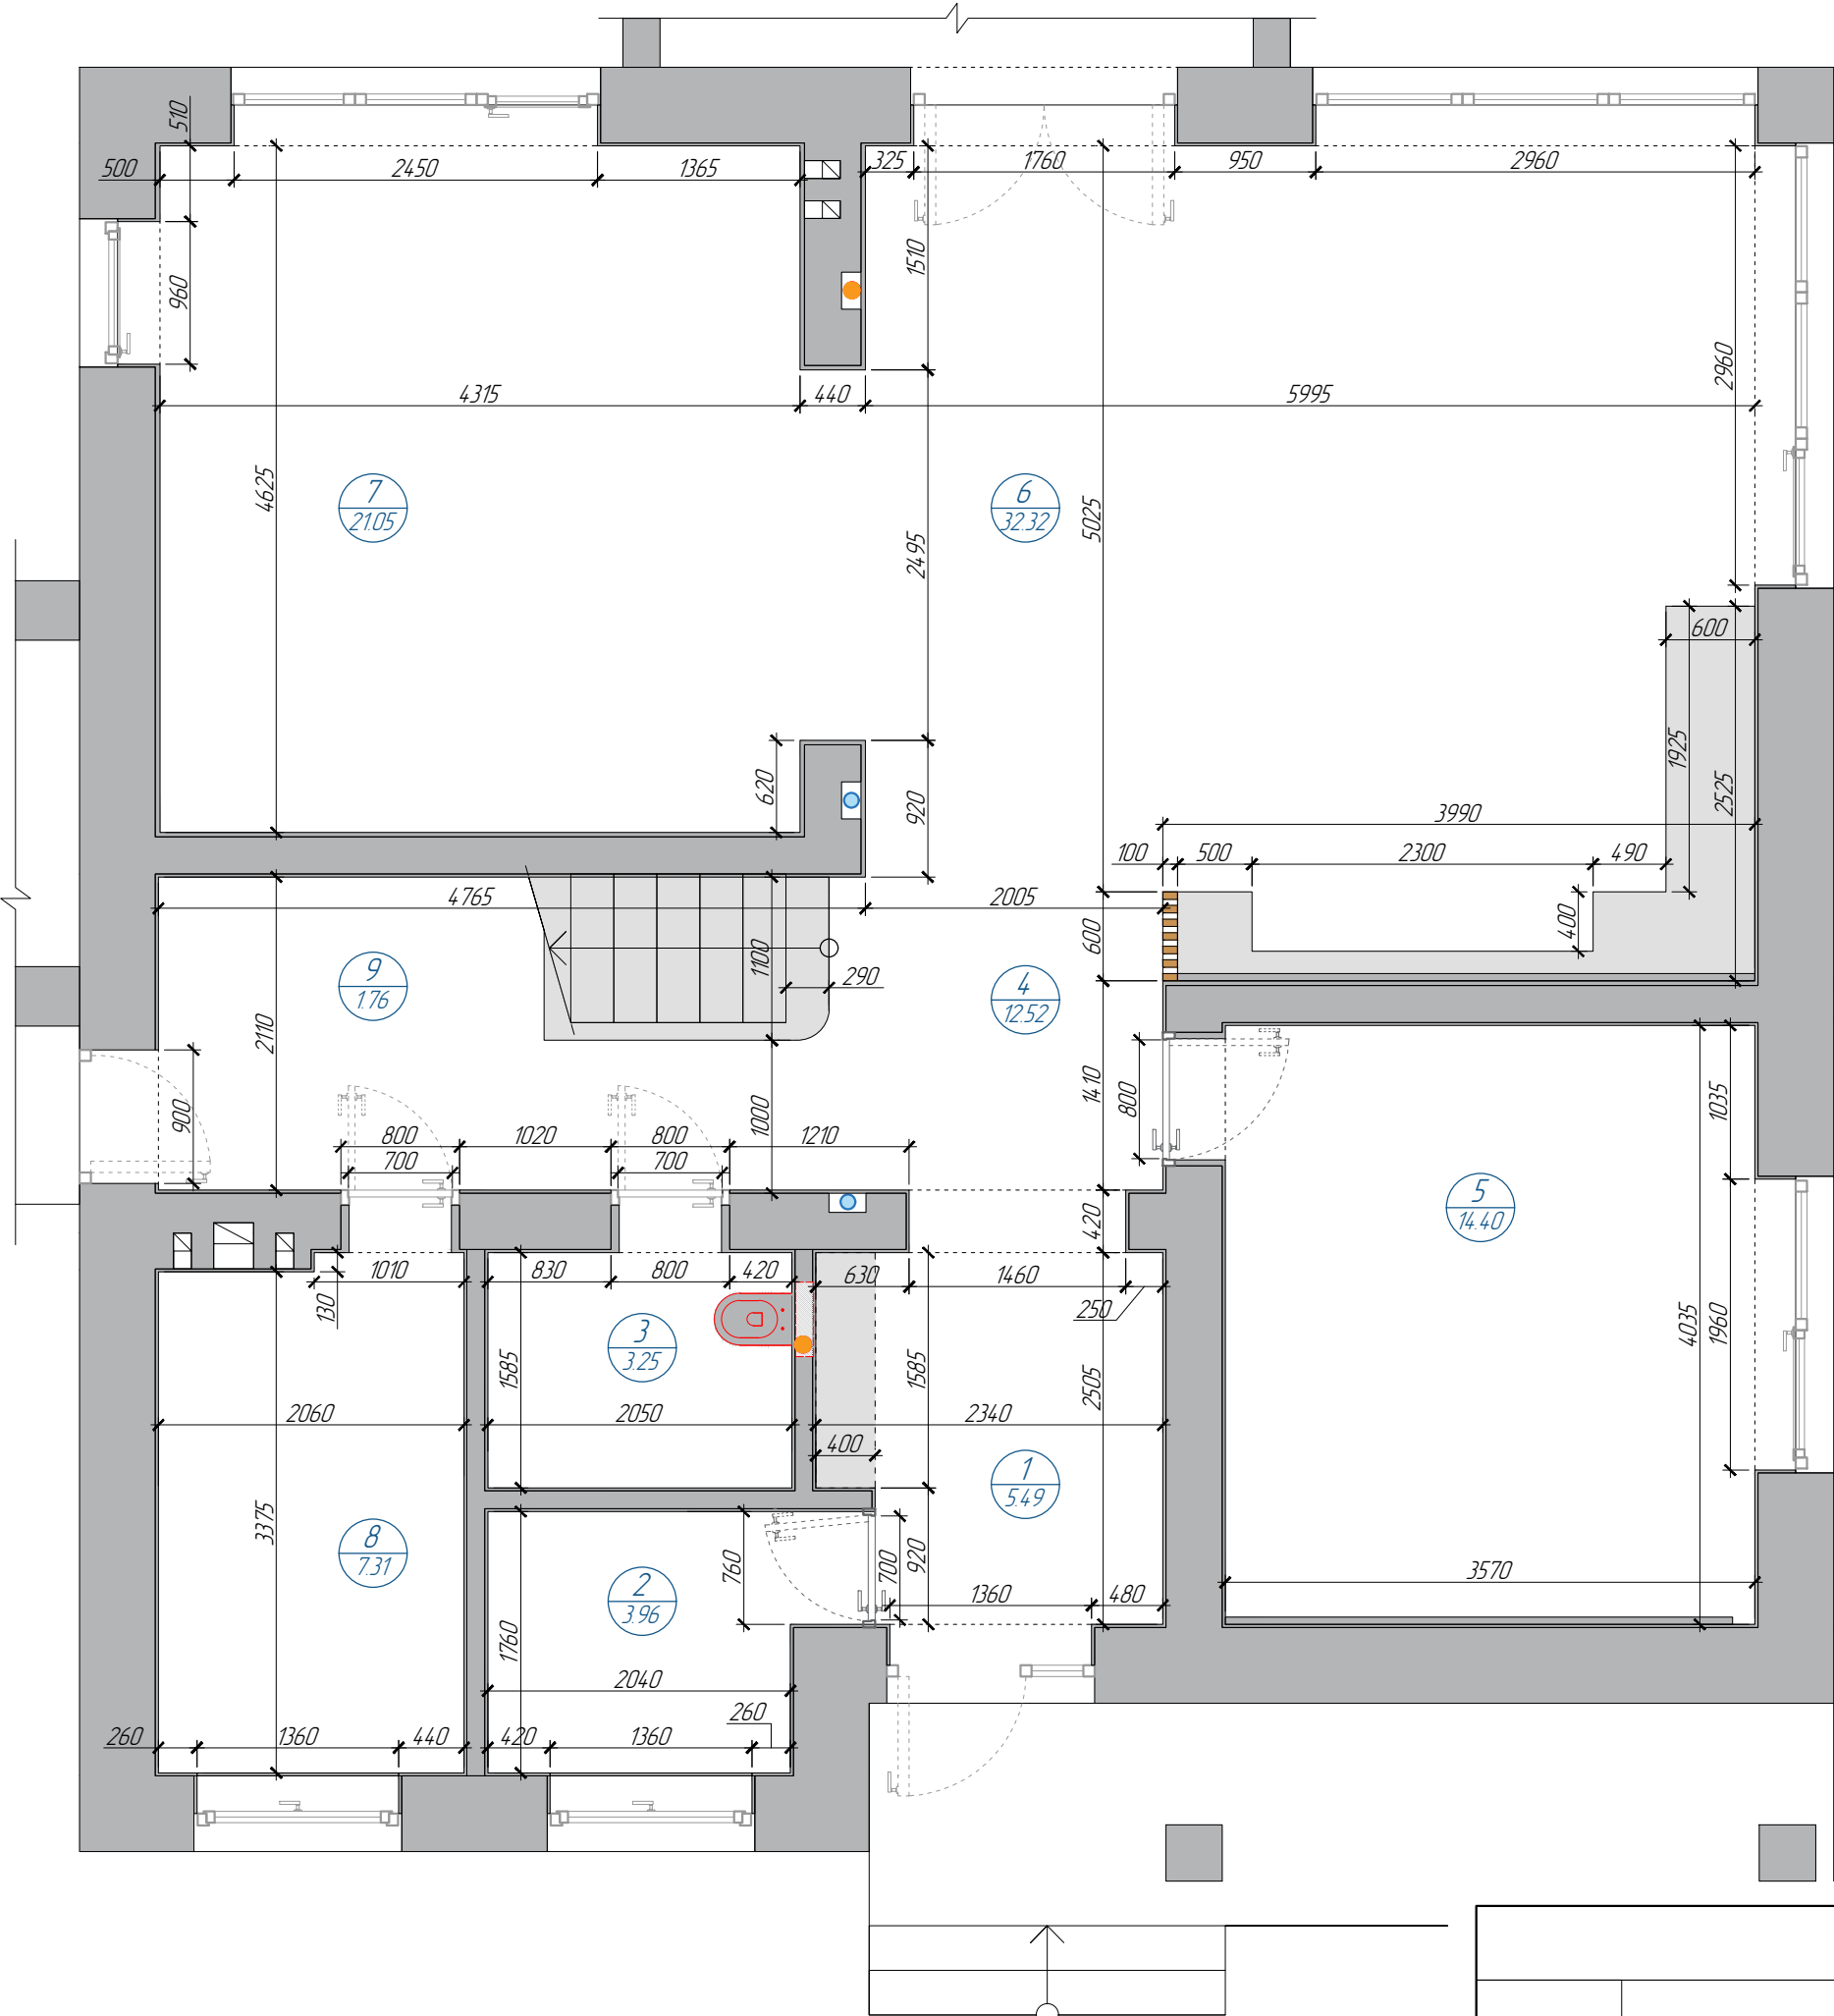

| Экспликация помещений        |        |                        |                          |        |            |
|------------------------------|--------|------------------------|--------------------------|--------|------------|
| Этаж                         | № пом. | Наименование помещения | Площадь , м <sup>2</sup> |        | Примечание |
|                              |        |                        | осн.                     | вспом. |            |
| 1                            | 1      | Прихожая               |                          | 549    |            |
|                              | 2      | Гардеробная            |                          | 396    |            |
|                              | 3      | Санузел гостей         |                          | 325    |            |
|                              | 4      | Лестничный холл        |                          | 1252   |            |
|                              | 5      | Комната няни           | 14.40                    |        |            |
|                              | 6      | Гостиная               | 32.32                    |        |            |
|                              | 7      | Кухня –столовая        | 2105                     |        |            |
|                              | 8      | Котельная              |                          | 731    |            |
|                              | 9      | Тех. помещение         |                          | 176    |            |
| 2                            | 10     | Лестничный холл        |                          | 833    |            |
|                              | 11     | Мастер –спальня        | 20.10                    |        |            |
|                              | 12     | Ванная комната         |                          | 517    |            |
|                              | 13     | Гардеробная            |                          | 574    |            |
|                              | 14     | Детская комната        | 18.88                    |        |            |
|                              | 15     | Кабинет                | 14.41                    |        |            |
|                              | 16     | Санузел                |                          | 560    |            |
|                              | 17     | Гостевая комната       | 14.80                    |        |            |
|                              |        | Итого по помещениям    | 135.96                   | 59.13  |            |
| Общая площадь помещений дома |        |                        | 195.09                   |        |            |


УСЛОВНЫЕ ОБОЗНАЧЕНИЯ

- стены и перегородки из керамоблока
- стояк канализации
- стояк ливневой канализации

ПРИМЕЧАНИЯ

1. Все размеры указаны с учетом штукатурного слоя и плитки

План 2 этажа

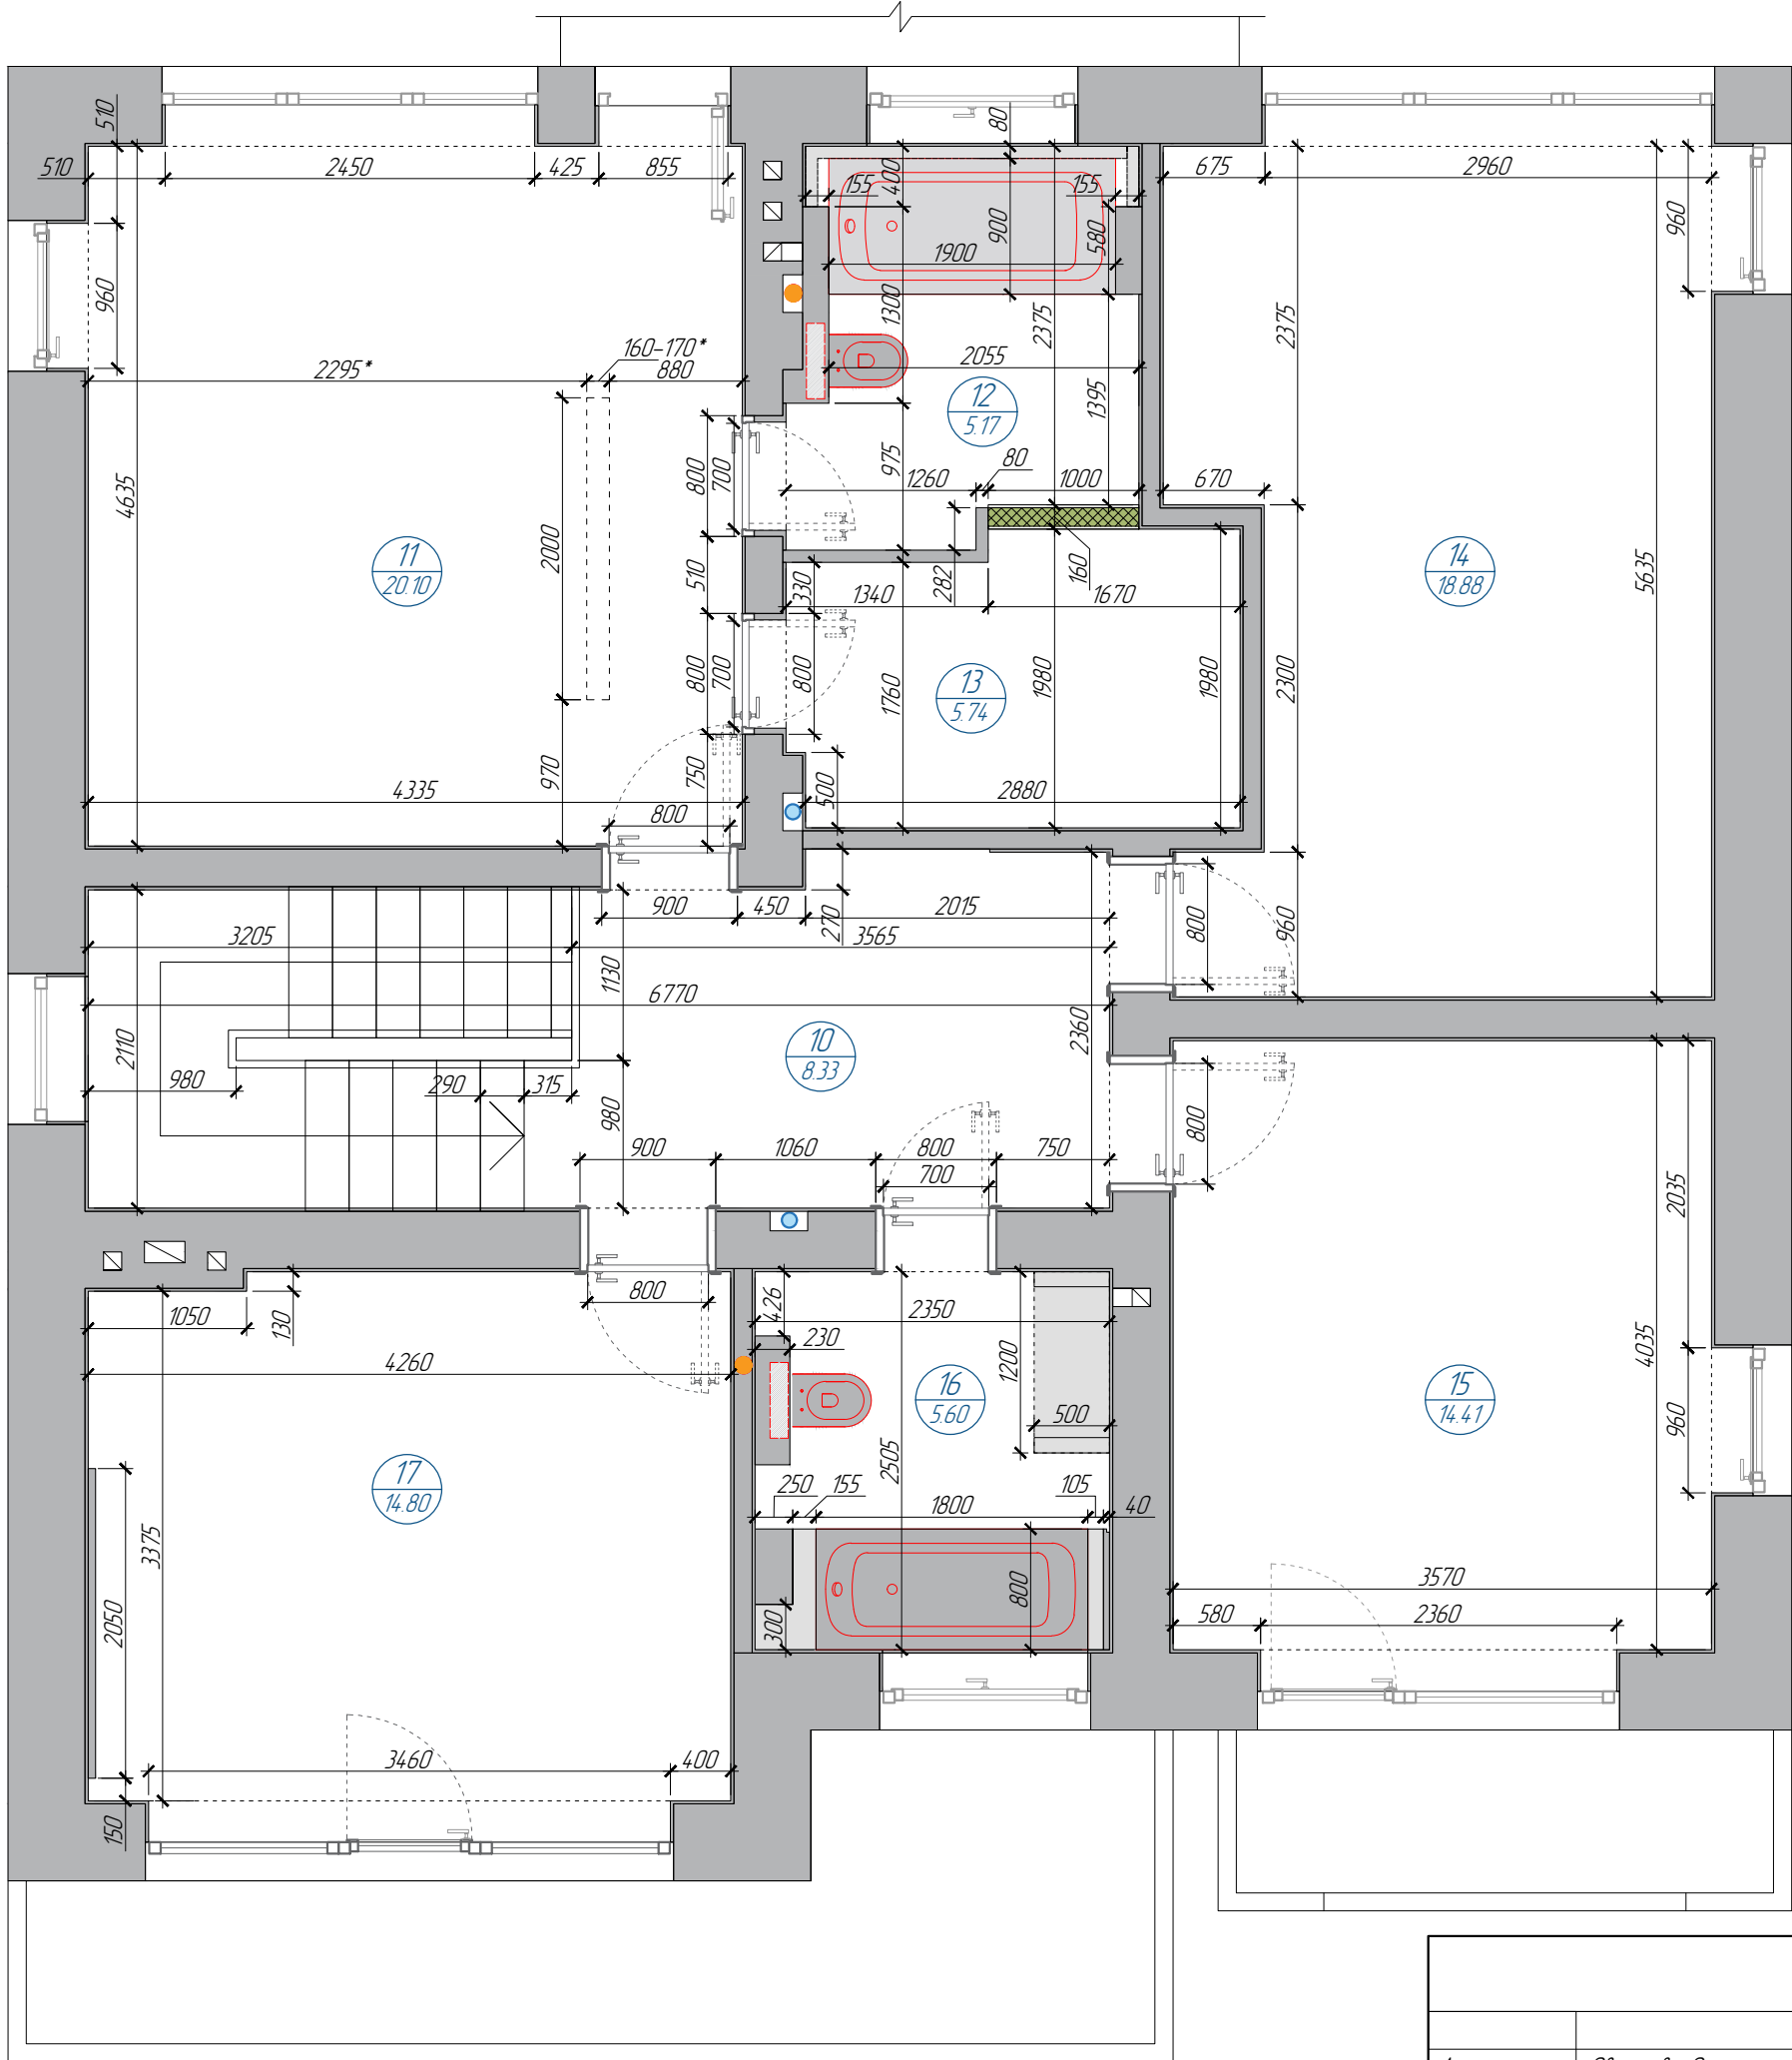


| Экспликация помещений        |        |                        |                          |        |            |
|------------------------------|--------|------------------------|--------------------------|--------|------------|
| Этаж                         | № пом. | Наименование помещения | Площадь , м <sup>2</sup> |        | Примечание |
|                              |        |                        | осн.                     | вспом. |            |
| 1                            | 1      | Прихожая               |                          | 5.49   |            |
|                              | 2      | Гардеробная            |                          | 3.96   |            |
|                              | 3      | Санузел гостей         |                          | 3.25   |            |
|                              | 4      | Лестничный холл        |                          | 12.52  |            |
|                              | 5      | Комната няни           | 14.40                    |        |            |
|                              | 6      | Гостиная               | 32.32                    |        |            |
|                              | 7      | Кухня –столовая        | 21.05                    |        |            |
|                              | 8      | Котельная              |                          | 7.31   |            |
|                              | 9      | Тех. помещение         |                          | 1.76   |            |
| 2                            | 10     | Лестничный холл        |                          | 8.33   |            |
|                              | 11     | Мастер –спальня        | 20.10                    |        |            |
|                              | 12     | Ванная комната         |                          | 5.17   |            |
|                              | 13     | Гардеробная            |                          | 5.74   |            |
|                              | 14     | Детская комната        | 18.88                    |        |            |
|                              | 15     | Кабинет                | 14.41                    |        |            |
|                              | 16     | Санузел                |                          | 5.60   |            |
|                              | 17     | Гостевая комната       | 14.80                    |        |            |
|                              |        | Итого по помещениям    | 135.96                   | 59.13  |            |
| Общая площадь помещений дома |        |                        | 195.09                   |        |            |

УСЛОВНЫЕ ОБОЗНАЧЕНИЯ

- стены и перегородки из керамблока
- стояк канализации
- стояк ливневой канализации



План расстановки мебели . 1 этаж

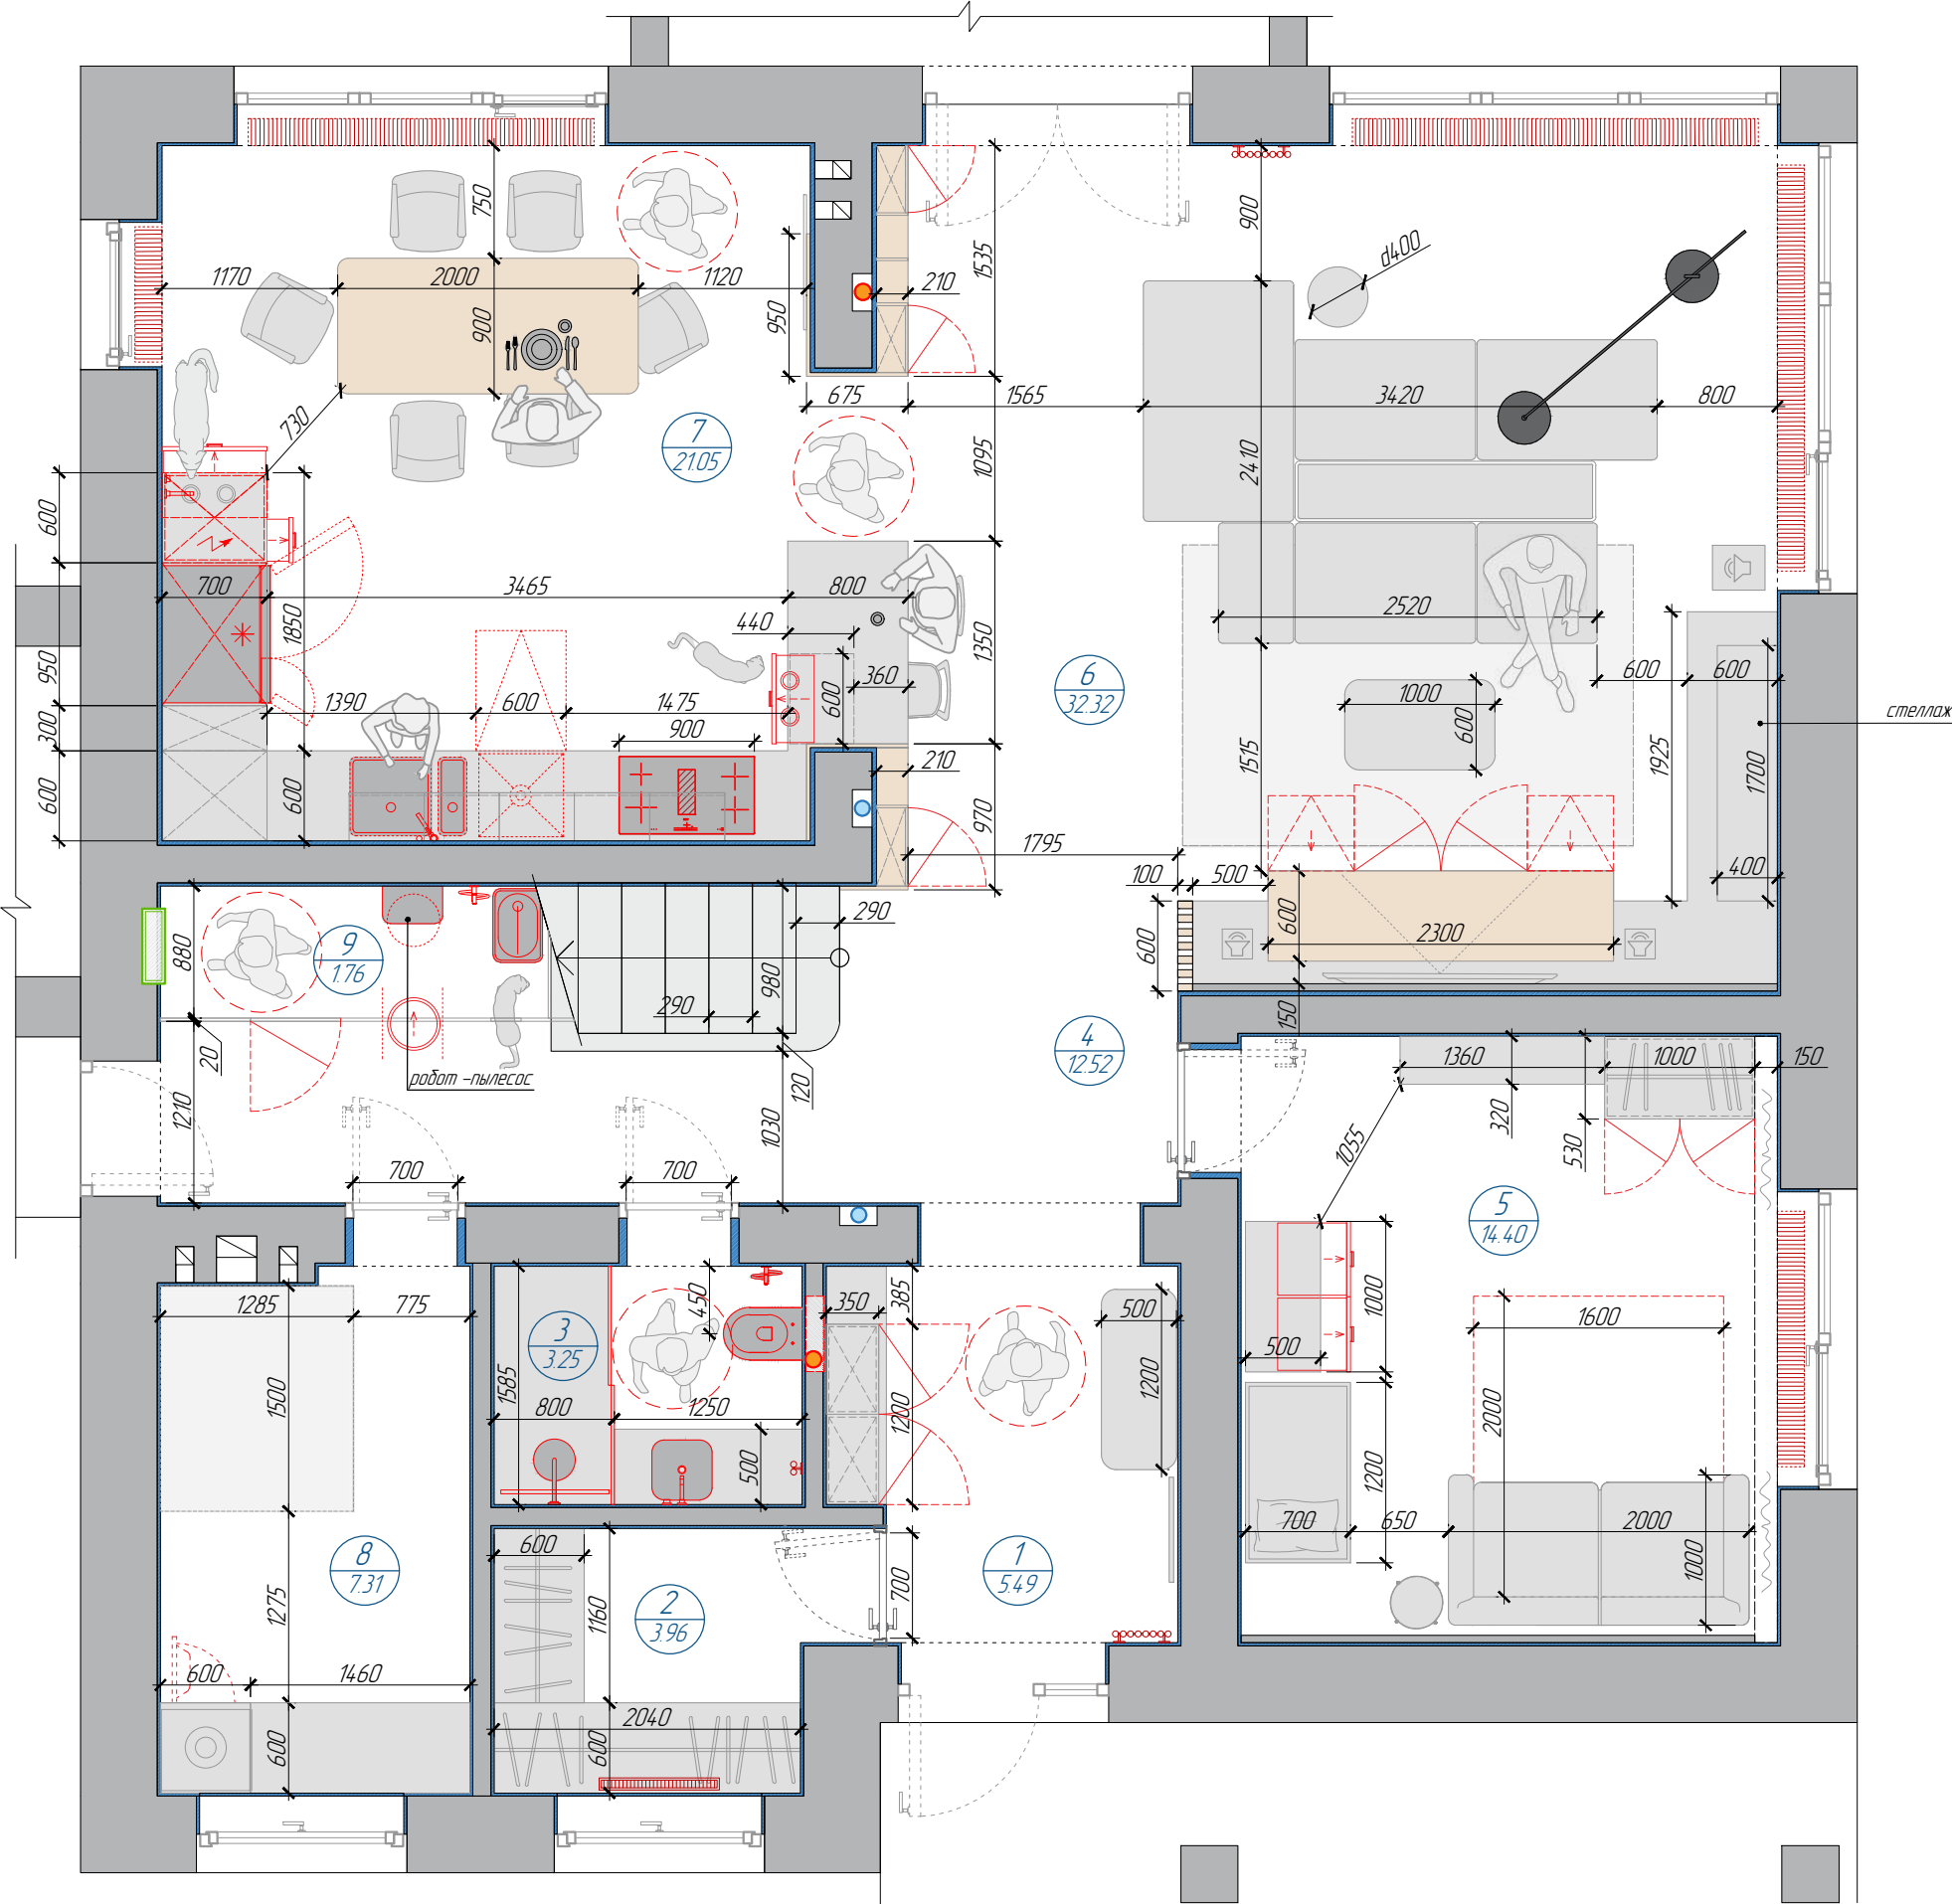

| Экспликация помещений        |        |                        |                          |        |            |
|------------------------------|--------|------------------------|--------------------------|--------|------------|
| Этаж                         | № пом. | Наименование помещения | Площадь , м <sup>2</sup> |        | Примечание |
|                              |        |                        | осн.                     | вспом. |            |
| 1                            | 1      | Прихожая               |                          | 54.9   |            |
|                              | 2      | Гардеробная            |                          | 3.96   |            |
|                              | 3      | Санузел гостей         |                          | 3.25   |            |
|                              | 4      | Лестничный холл        |                          | 12.52  |            |
|                              | 5      | Комната няни           | 14.40                    |        |            |
|                              | 6      | Гостиная               | 32.32                    |        |            |
|                              | 7      | Кухня –столовая        | 21.05                    |        |            |
|                              | 8      | Котельная              |                          | 7.31   |            |
|                              | 9      | Тех. помещение         |                          | 1.76   |            |
| 2                            | 10     | Лестничный холл        |                          | 8.33   |            |
|                              | 11     | Мастер –спальня        | 20.10                    |        |            |
|                              | 12     | Ванная комната         |                          | 5.17   |            |
|                              | 13     | Гардеробная            |                          | 5.74   |            |
|                              | 14     | Детская комната        | 18.88                    |        |            |
|                              | 15     | Кабинет                | 14.41                    |        |            |
|                              | 16     | Санузел                |                          | 5.60   |            |
|                              | 17     | Гостевая комната       | 14.80                    |        |            |
|                              |        | Итого по помещениям    | 135.96                   | 59.13  |            |
| Общая площадь помещений дома |        |                        | 195.09                   |        |            |

УСЛОВНЫЕ ОБОЗНАЧЕНИЯ

- стены и перегородки из керамоблока
- стояк канализации
- стояк ливневой канализации
- штукатурный слой
- внутрипольный конвектор
- панельный радиатор
- вертикальный трубчатый радиатор
- щиты: силовой, слаботочный, для блоков led- подсветок


кп РАЙТ ЭКО

Архитектор  
Овчарова Ольга

План расстановки мебели . 1 этаж

ООО ЧАРОВА  
PROJECT

План расстановки мебели . 2 этаж

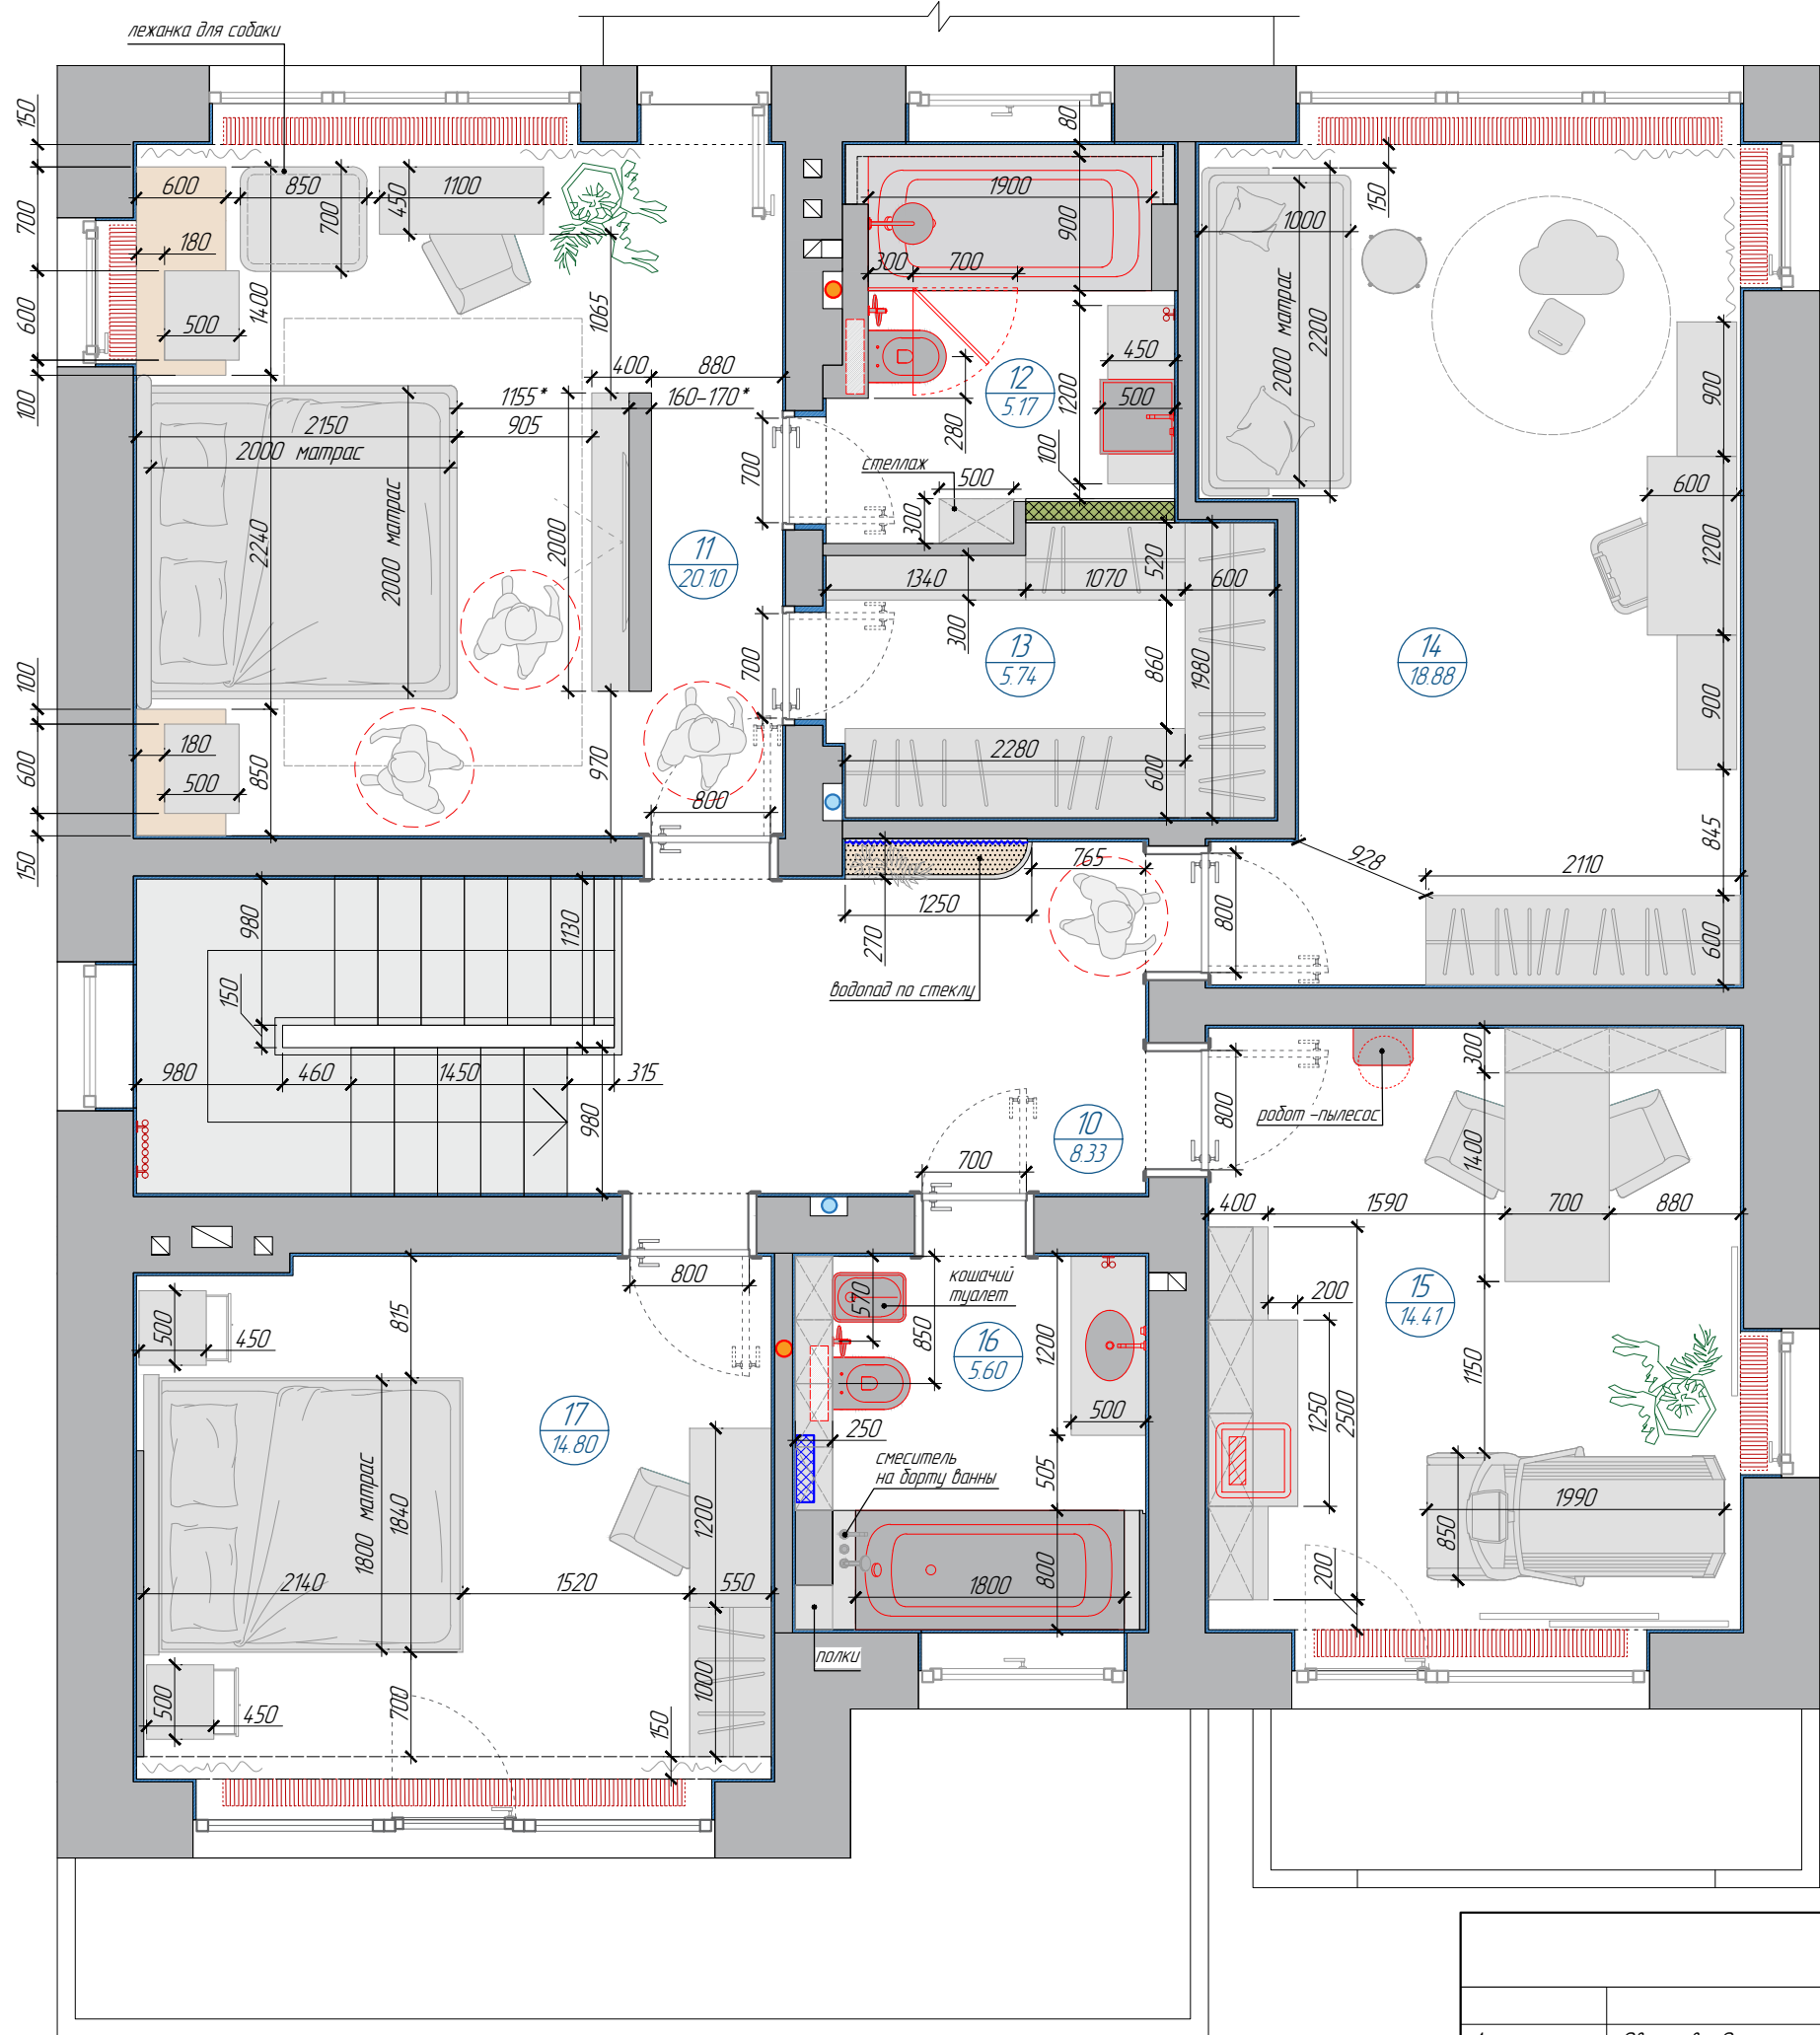

| Экспликация помещений        |        |                        |                          |        |            |
|------------------------------|--------|------------------------|--------------------------|--------|------------|
| Этаж                         | № пом. | Наименование помещения | Площадь , м <sup>2</sup> |        | Примечание |
|                              |        |                        | осн.                     | вспом. |            |
| 1                            | 1      | Прихожая               |                          | 5.49   |            |
|                              | 2      | Гардеробная            |                          | 3.96   |            |
|                              | 3      | Санузел гостей         |                          | 3.25   |            |
|                              | 4      | Лестничный холл        |                          | 12.52  |            |
|                              | 5      | Комната няни           | 14.40                    |        |            |
|                              | 6      | Гостиная               | 32.32                    |        |            |
|                              | 7      | Кухня –столовая        | 21.05                    |        |            |
|                              | 8      | Котельная              |                          | 7.31   |            |
|                              | 9      | Тех. помещение         |                          | 1.76   |            |
| 2                            | 10     | Лестничный холл        |                          | 8.33   |            |
|                              | 11     | Мастер –спальня        | 20.10                    |        |            |
|                              | 12     | Ванная комната         |                          | 5.17   |            |
|                              | 13     | Гардеробная            |                          | 5.74   |            |
|                              | 14     | Детская комната        | 18.88                    |        |            |
|                              | 15     | Кабинет                | 14.41                    |        |            |
|                              | 16     | Санузел                |                          | 5.60   |            |
|                              | 17     | Гостевая комната       | 14.80                    |        |            |
|                              |        | Итого по помещениям    | 135.96                   | 59.13  |            |
| Общая площадь помещений дома |        |                        | 195.09                   |        |            |

УСЛОВНЫЕ ОБОЗНАЧЕНИЯ

- стены и перегородки из керамоблока
- стояк канализации
- стоякливневой канализации
- штукатурный слой
- внутрипольный конвектор
- панельный радиатор
- вертикальный трубчатый радиатор



Схема санузла. 1 этаж



Схема санузла. 2 этаж





Схема санузла при спальне. 2 этаж





Схема ТВ-зоны в гостиной

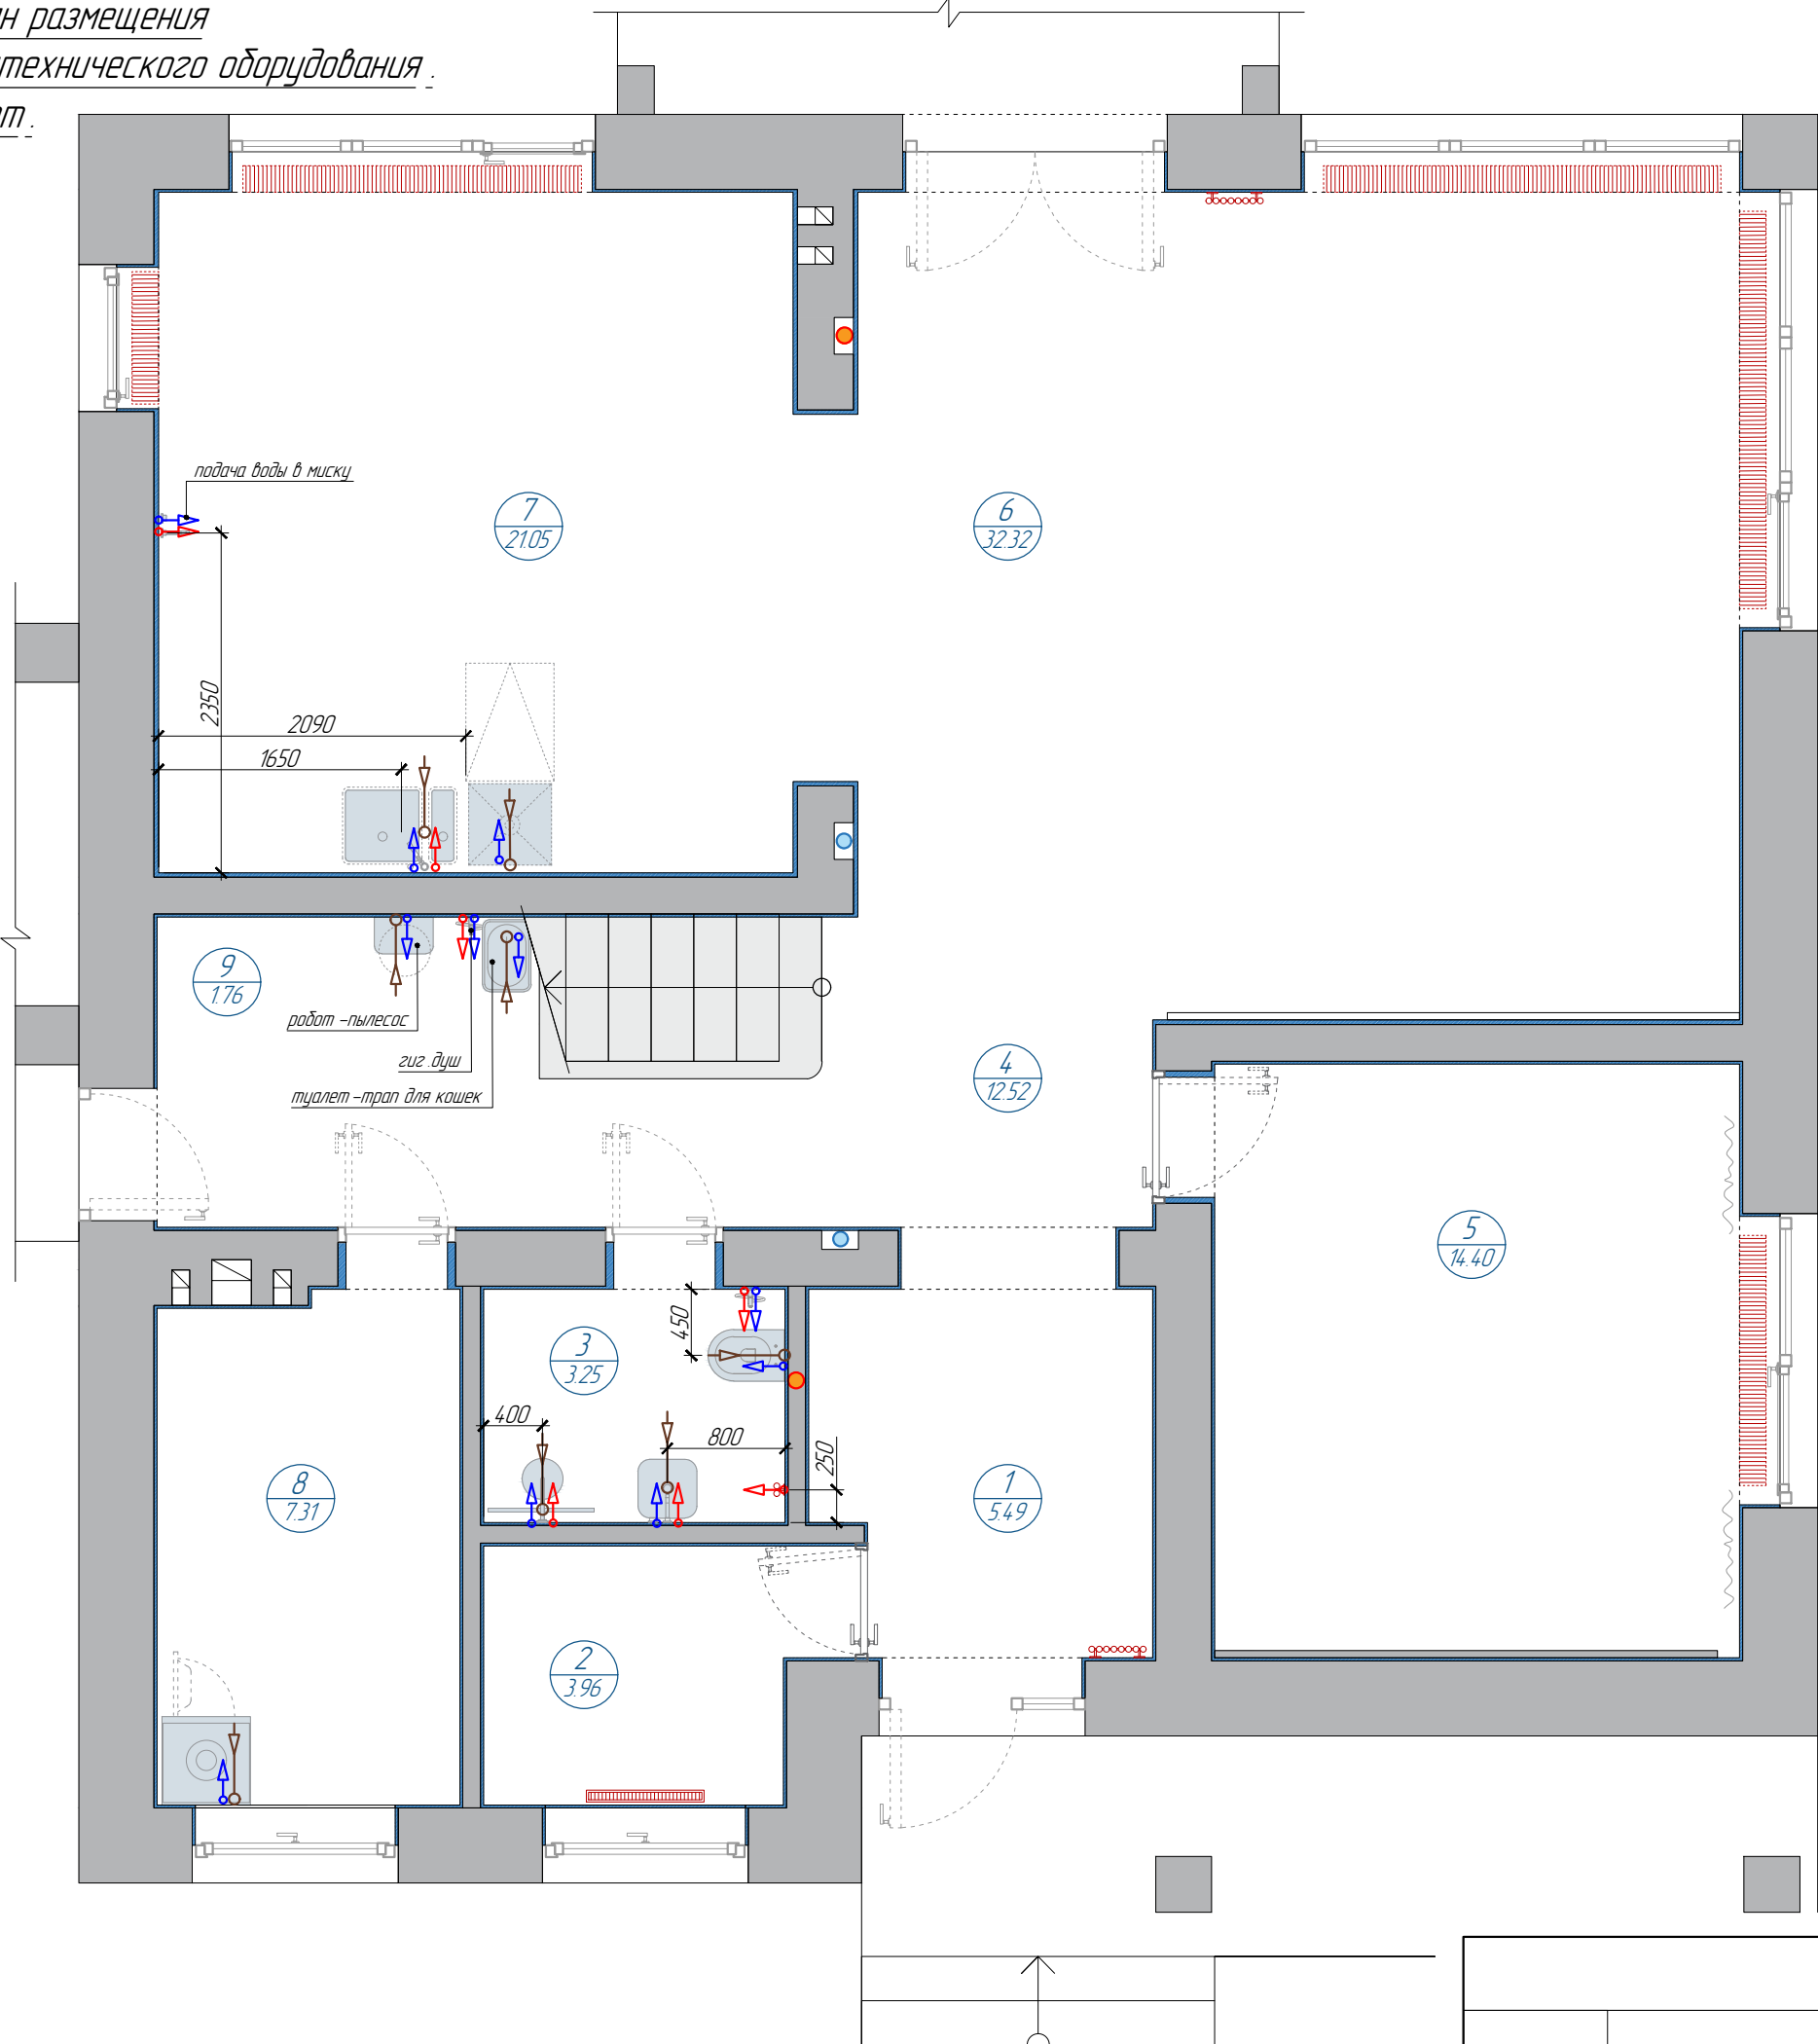




Схема ТВ-зоны в спальне



План размещения  
сантехнического оборудования.  
1 эт.



| Экспликация помещений        |        |                        |             |        |            |
|------------------------------|--------|------------------------|-------------|--------|------------|
| Этаж                         | № пом. | Наименование помещения | Площадь, м² |        | Примечание |
|                              |        |                        | осн.        | вспом. |            |
| 1                            | 1      | Прихожая               |             | 549    |            |
|                              | 2      | Гардеробная            |             | 396    |            |
|                              | 3      | Санузел гостей         |             | 325    |            |
|                              | 4      | Лестничный холл        |             | 1252   |            |
|                              | 5      | Комната няни           | 14.40       |        |            |
|                              | 6      | Гостиная               | 32.32       |        |            |
|                              | 7      | Кухня - столовая       | 21.05       |        |            |
|                              | 8      | Котельная              |             | 7.31   |            |
|                              | 9      | Тех. помещение         |             | 1.76   |            |
| 2                            | 10     | Лестничный холл        |             | 8.33   |            |
|                              | 11     | Мастер - спальня       | 20.10       |        |            |
|                              | 12     | Ванная комната         |             | 5.17   |            |
|                              | 13     | Гардеробная            |             | 5.74   |            |
|                              | 14     | Детская комната        | 18.88       |        |            |
|                              | 15     | Кабинет                | 14.41       |        |            |
|                              | 16     | Санузел                |             | 5.60   |            |
|                              | 17     | Гостевая комната       | 14.80       |        |            |
| Итого по помещениям          |        |                        | 135.96      | 59.13  |            |
| Общая площадь помещений дома |        |                        | 195.09      |        |            |

УСЛОВНЫЕ ОБОЗНАЧЕНИЯ


- стены и перегородки из керамоблока
- стояк канализации
- стояк ливневой канализации
- штукатурный слой
- внутрипольный конвектор
- панельный радиатор
- вертикальный трубчатый радиатор
- подводка холодной воды
- подводка горячей воды
- вывод канализации

ПРИМЕЧАНИЯ

- Любые расхождения проектных размеров с фактическими, нестыковки, изменение конструктивных решений согласовывать с автором проекта в рамках авторского надзора
- Подводку к оборудованию осуществлять строго в соответствии с техническими картами купленного оборудования



План размещения  
сантехнического оборудования.  
2 эт.

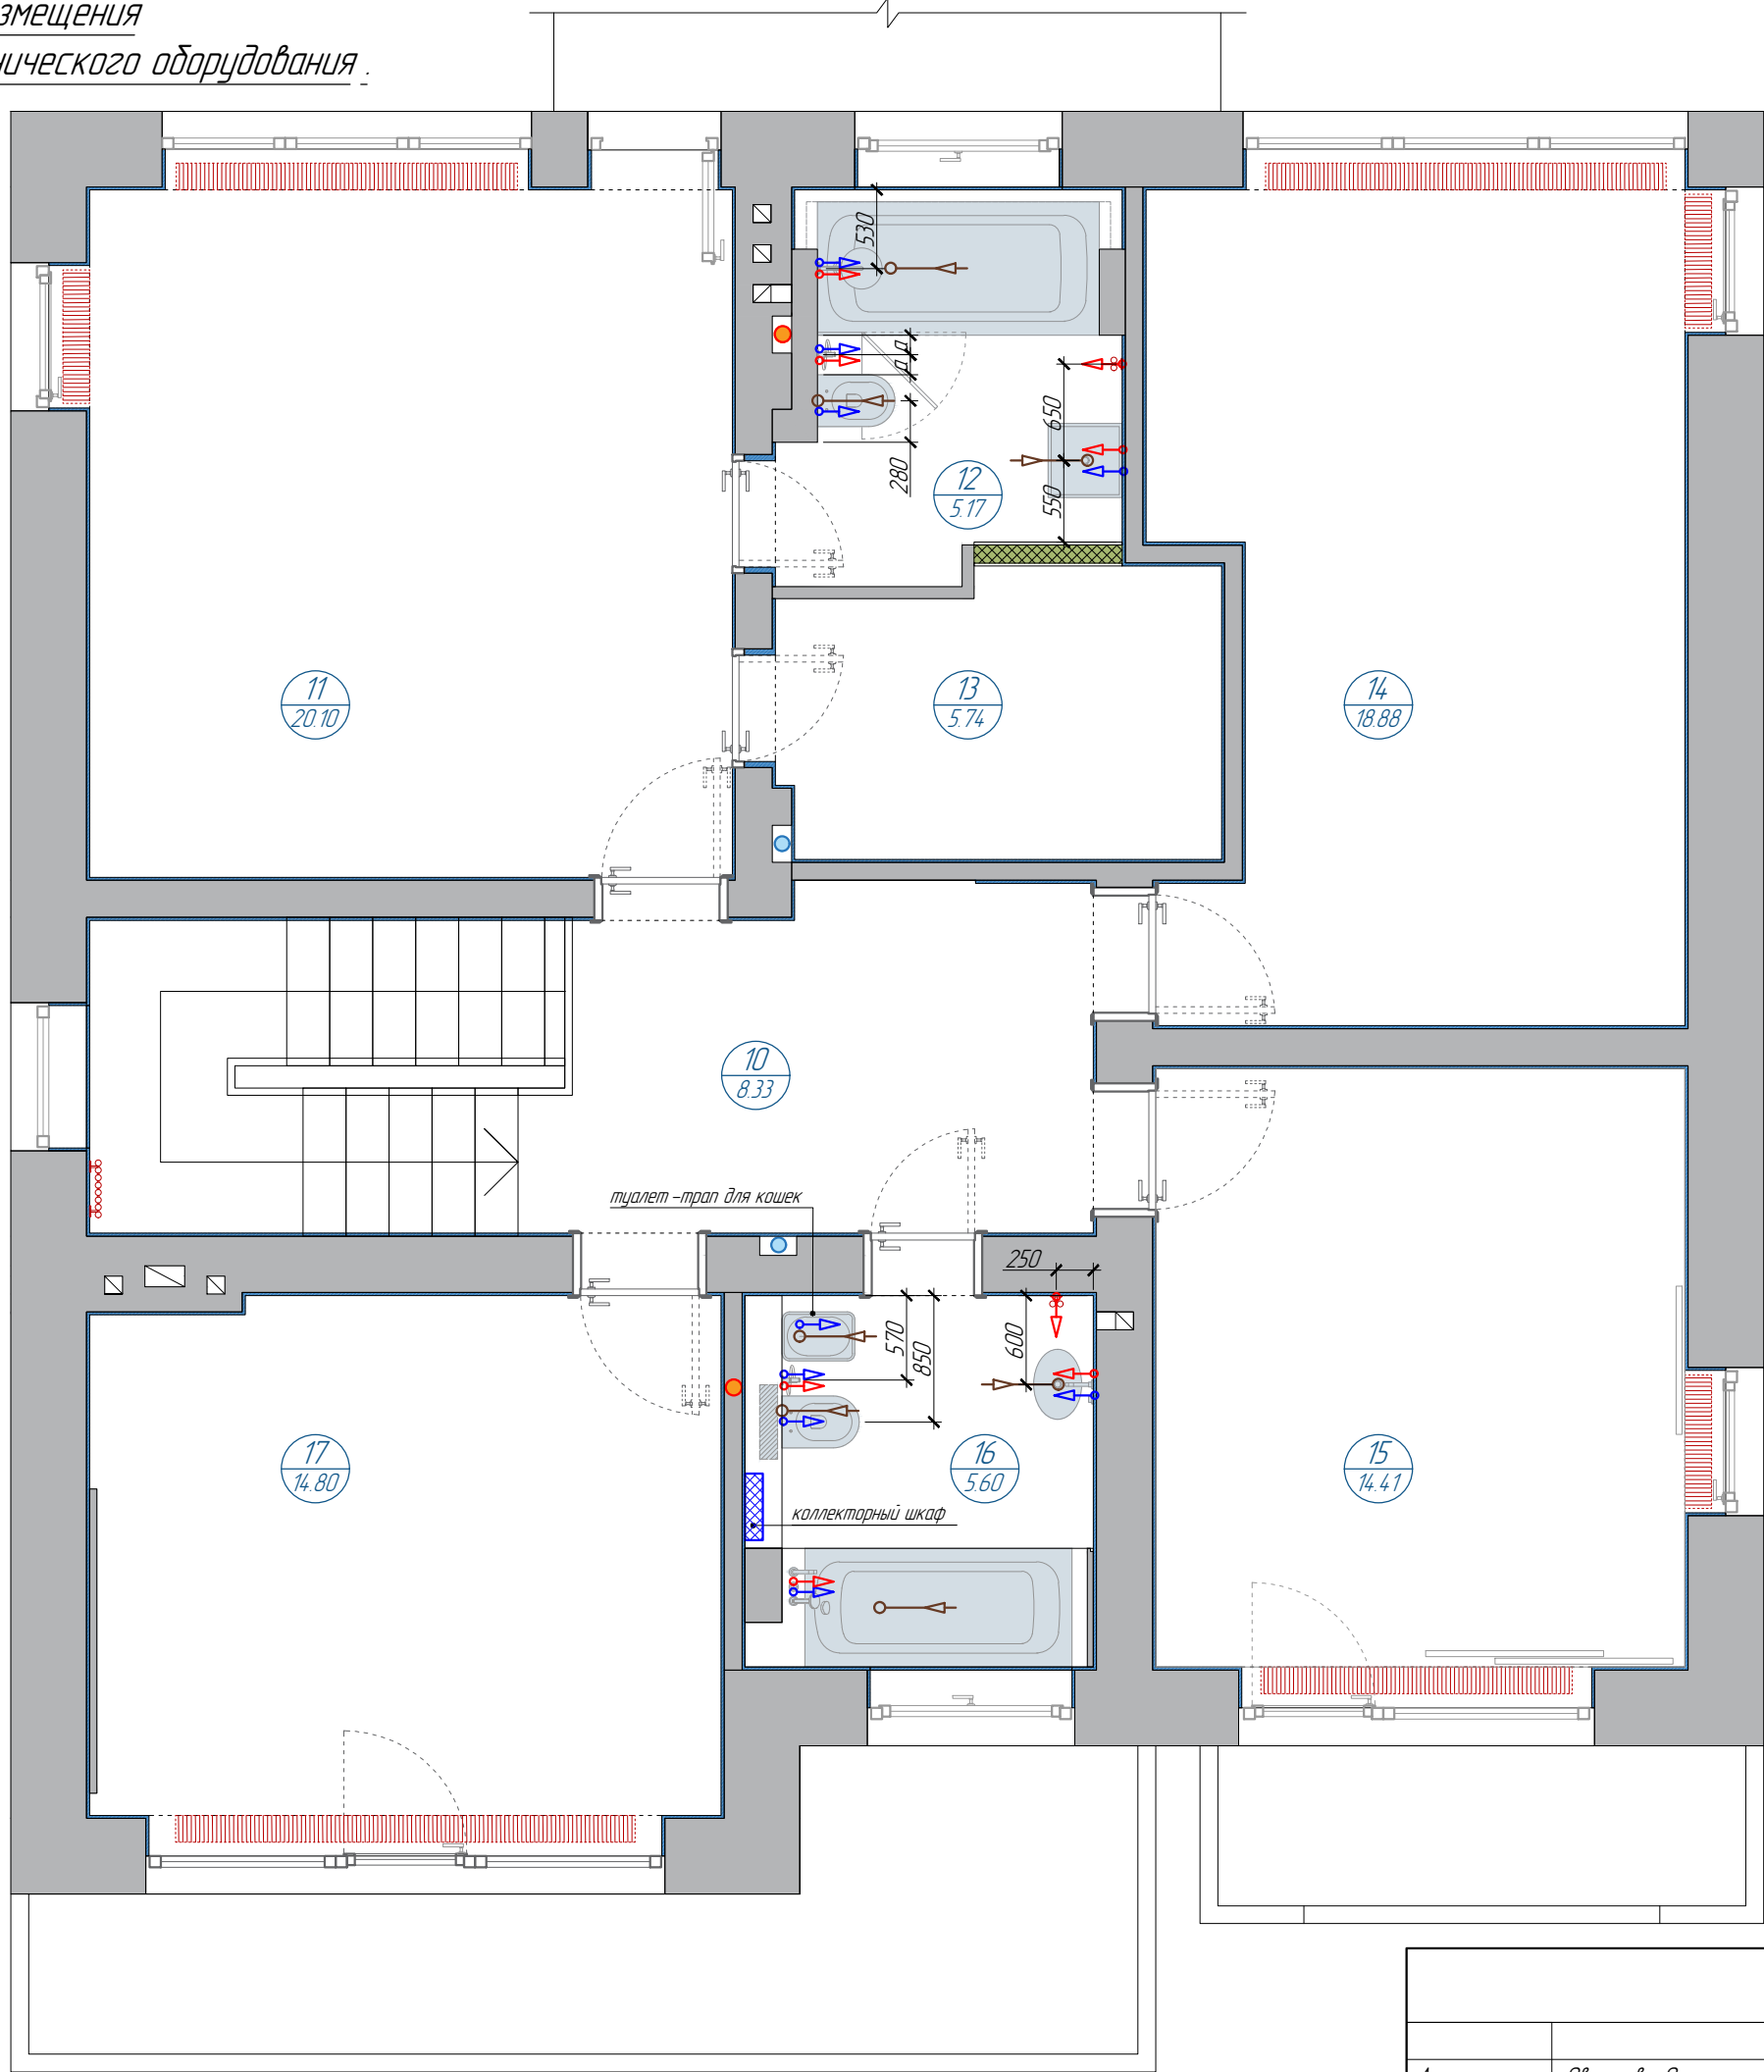

| Экспликация помещений        |        |                        |                          |        |            |
|------------------------------|--------|------------------------|--------------------------|--------|------------|
| Этаж                         | № пом. | Наименование помещения | Площадь , м <sup>2</sup> |        | Примечание |
|                              |        |                        | осн.                     | вспом. |            |
| 1                            | 1      | Прихожая               |                          | 5.49   |            |
|                              | 2      | Гардеробная            |                          | 3.96   |            |
|                              | 3      | Санузел гостей         |                          | 3.25   |            |
|                              | 4      | Лестничный холл        |                          | 12.52  |            |
|                              | 5      | Комната няни           | 14.40                    |        |            |
|                              | 6      | Гостиная               | 32.32                    |        |            |
|                              | 7      | Кухня –столовая        | 21.05                    |        |            |
|                              | 8      | Котельная              |                          | 7.31   |            |
|                              | 9      | Тех. помещение         |                          | 1.76   |            |
| 2                            | 10     | Лестничный холл        |                          | 8.33   |            |
|                              | 11     | Мастер –спальня        | 20.10                    |        |            |
|                              | 12     | Ванная комната         |                          | 5.17   |            |
|                              | 13     | Гардеробная            |                          | 5.74   |            |
|                              | 14     | Детская комната        | 18.88                    |        |            |
|                              | 15     | Кабинет                | 14.41                    |        |            |
|                              | 16     | Санузел                |                          | 5.60   |            |
|                              | 17     | Гостевая комната       | 14.80                    |        |            |
|                              |        | Итого по помещениям    | 135.96                   | 59.13  |            |
| Общая площадь помещений дома |        |                        | 195.09                   |        |            |


УСЛОВНЫЕ ОБОЗНАЧЕНИЯ

- стены и перегородки из керамоблока
- стояк канализации
- стояк ливневой канализации
- штукатурный слой
- внутрипольный конвектор
- панельный радиатор
- вертикальный трубчатый радиатор
- подводка холодной воды
- подводка горячей воды
- вывод канализации

ПРИМЕЧАНИЯ

- Любые расхождения проектных размеров с фактическими, нестыковки, изменение конструктивных решений согласовывать с автором проекта в рамках авторского надзора
- Подводку к оборудованию осуществлять строго в соответствии с техническими картами купленного оборудования

План размещения электрооборудования  
1 этаж

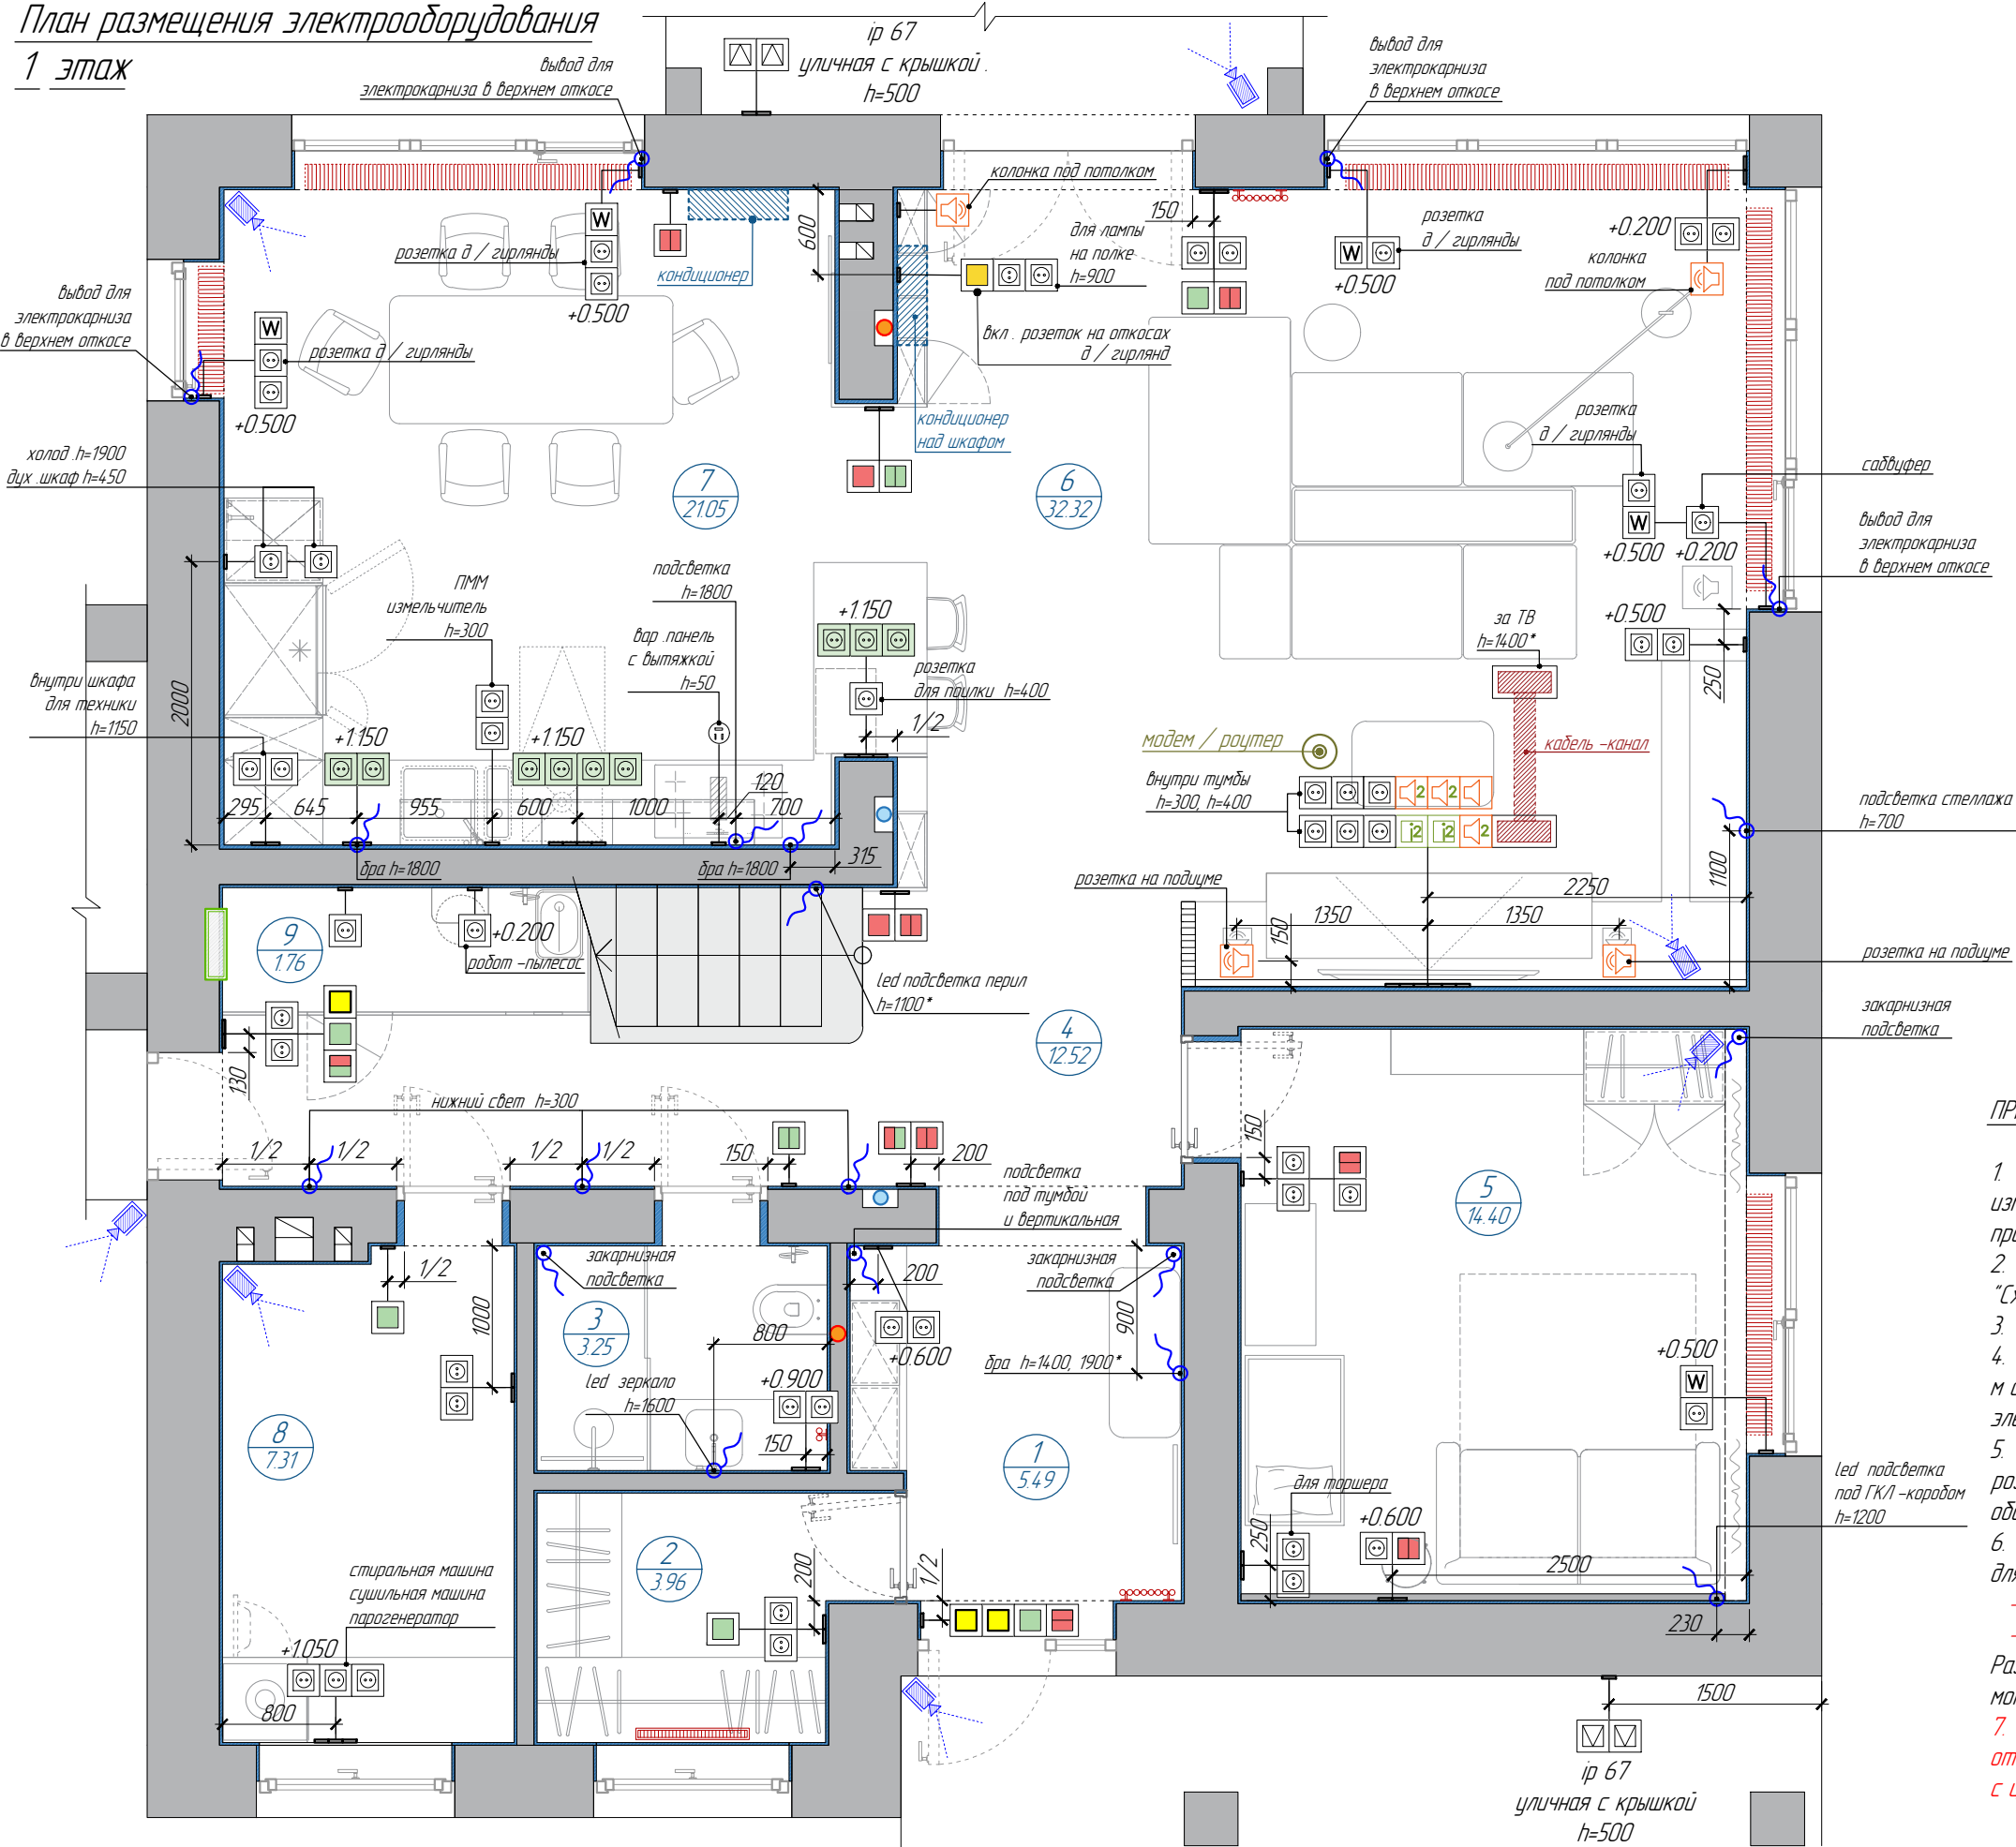

| УСЛОВНЫЕ ОБОЗНАЧЕНИЯ |                                                                  |
|----------------------|------------------------------------------------------------------|
|                      | штепсельная розетка для скрытой установки                        |
|                      | штепсельная розетка для скрытой установки над столешницей        |
|                      | штепсельная розетка для скрытой установки с крышкой              |
|                      | терморегулятор внутрипольного конвектора                         |
|                      | кабель - канал                                                   |
|                      | розетка RG-45                                                    |
|                      | щиток                                                            |
|                      | модем, роутер                                                    |
|                      | вывод провода для прямого подключения                            |
|                      | выключатель одноклавишный                                        |
|                      | выключатель двухклавишный                                        |
|                      | переключатель одноклавишный                                      |
|                      | переключатель двухклавишный                                      |
|                      | выключатель одноклавишный (к нему запитана розетка для гирлянды) |
|                      | контрольный выключатель (на весь свет)                           |
|                      | потолочная точка доступа wi-fi                                   |
|                      | камера видеонаблюдения                                           |


ПРИМЕЧАНИЯ

- Любые расхождения проектных размеров с фактическими, нестыковки, изменение конструктивных решений и т.п. согласовывать с автором проекта в рамках авторского надзора
  - Данный лист смотреть совместно с листами "Схема размещения групп светильников с привязкой к выключателям"
  - Высоты указаны от отметки чистого пола 0.000
  - Все розетки располагать на высоте 0.3 м, а выключатели на высоте 0.9 м от уровня чистого пола до оси электроприбора или группы электроприборов, если не указано иное
  - К выключателям для праздничного освещения (гирлянд) запитываются розетки на откосах, предназначенные для подключения светового оборудования
  - На этапе разводки электрики предусмотреть выводы для системы кондиционирования, а также:
    - видеонаблюдения
    - охранной сигнализации
- Размещение выводов выполнить согласно предписаниям от организаций, монтирующих данные системы
7. Для выключателей, расположенных в непосредственной близости от радиаторов отопления, обеспечить изоляцию силовых кабелей с целью исключения нагрева электрооборудования



План размещения электрооборудования

2 этаж

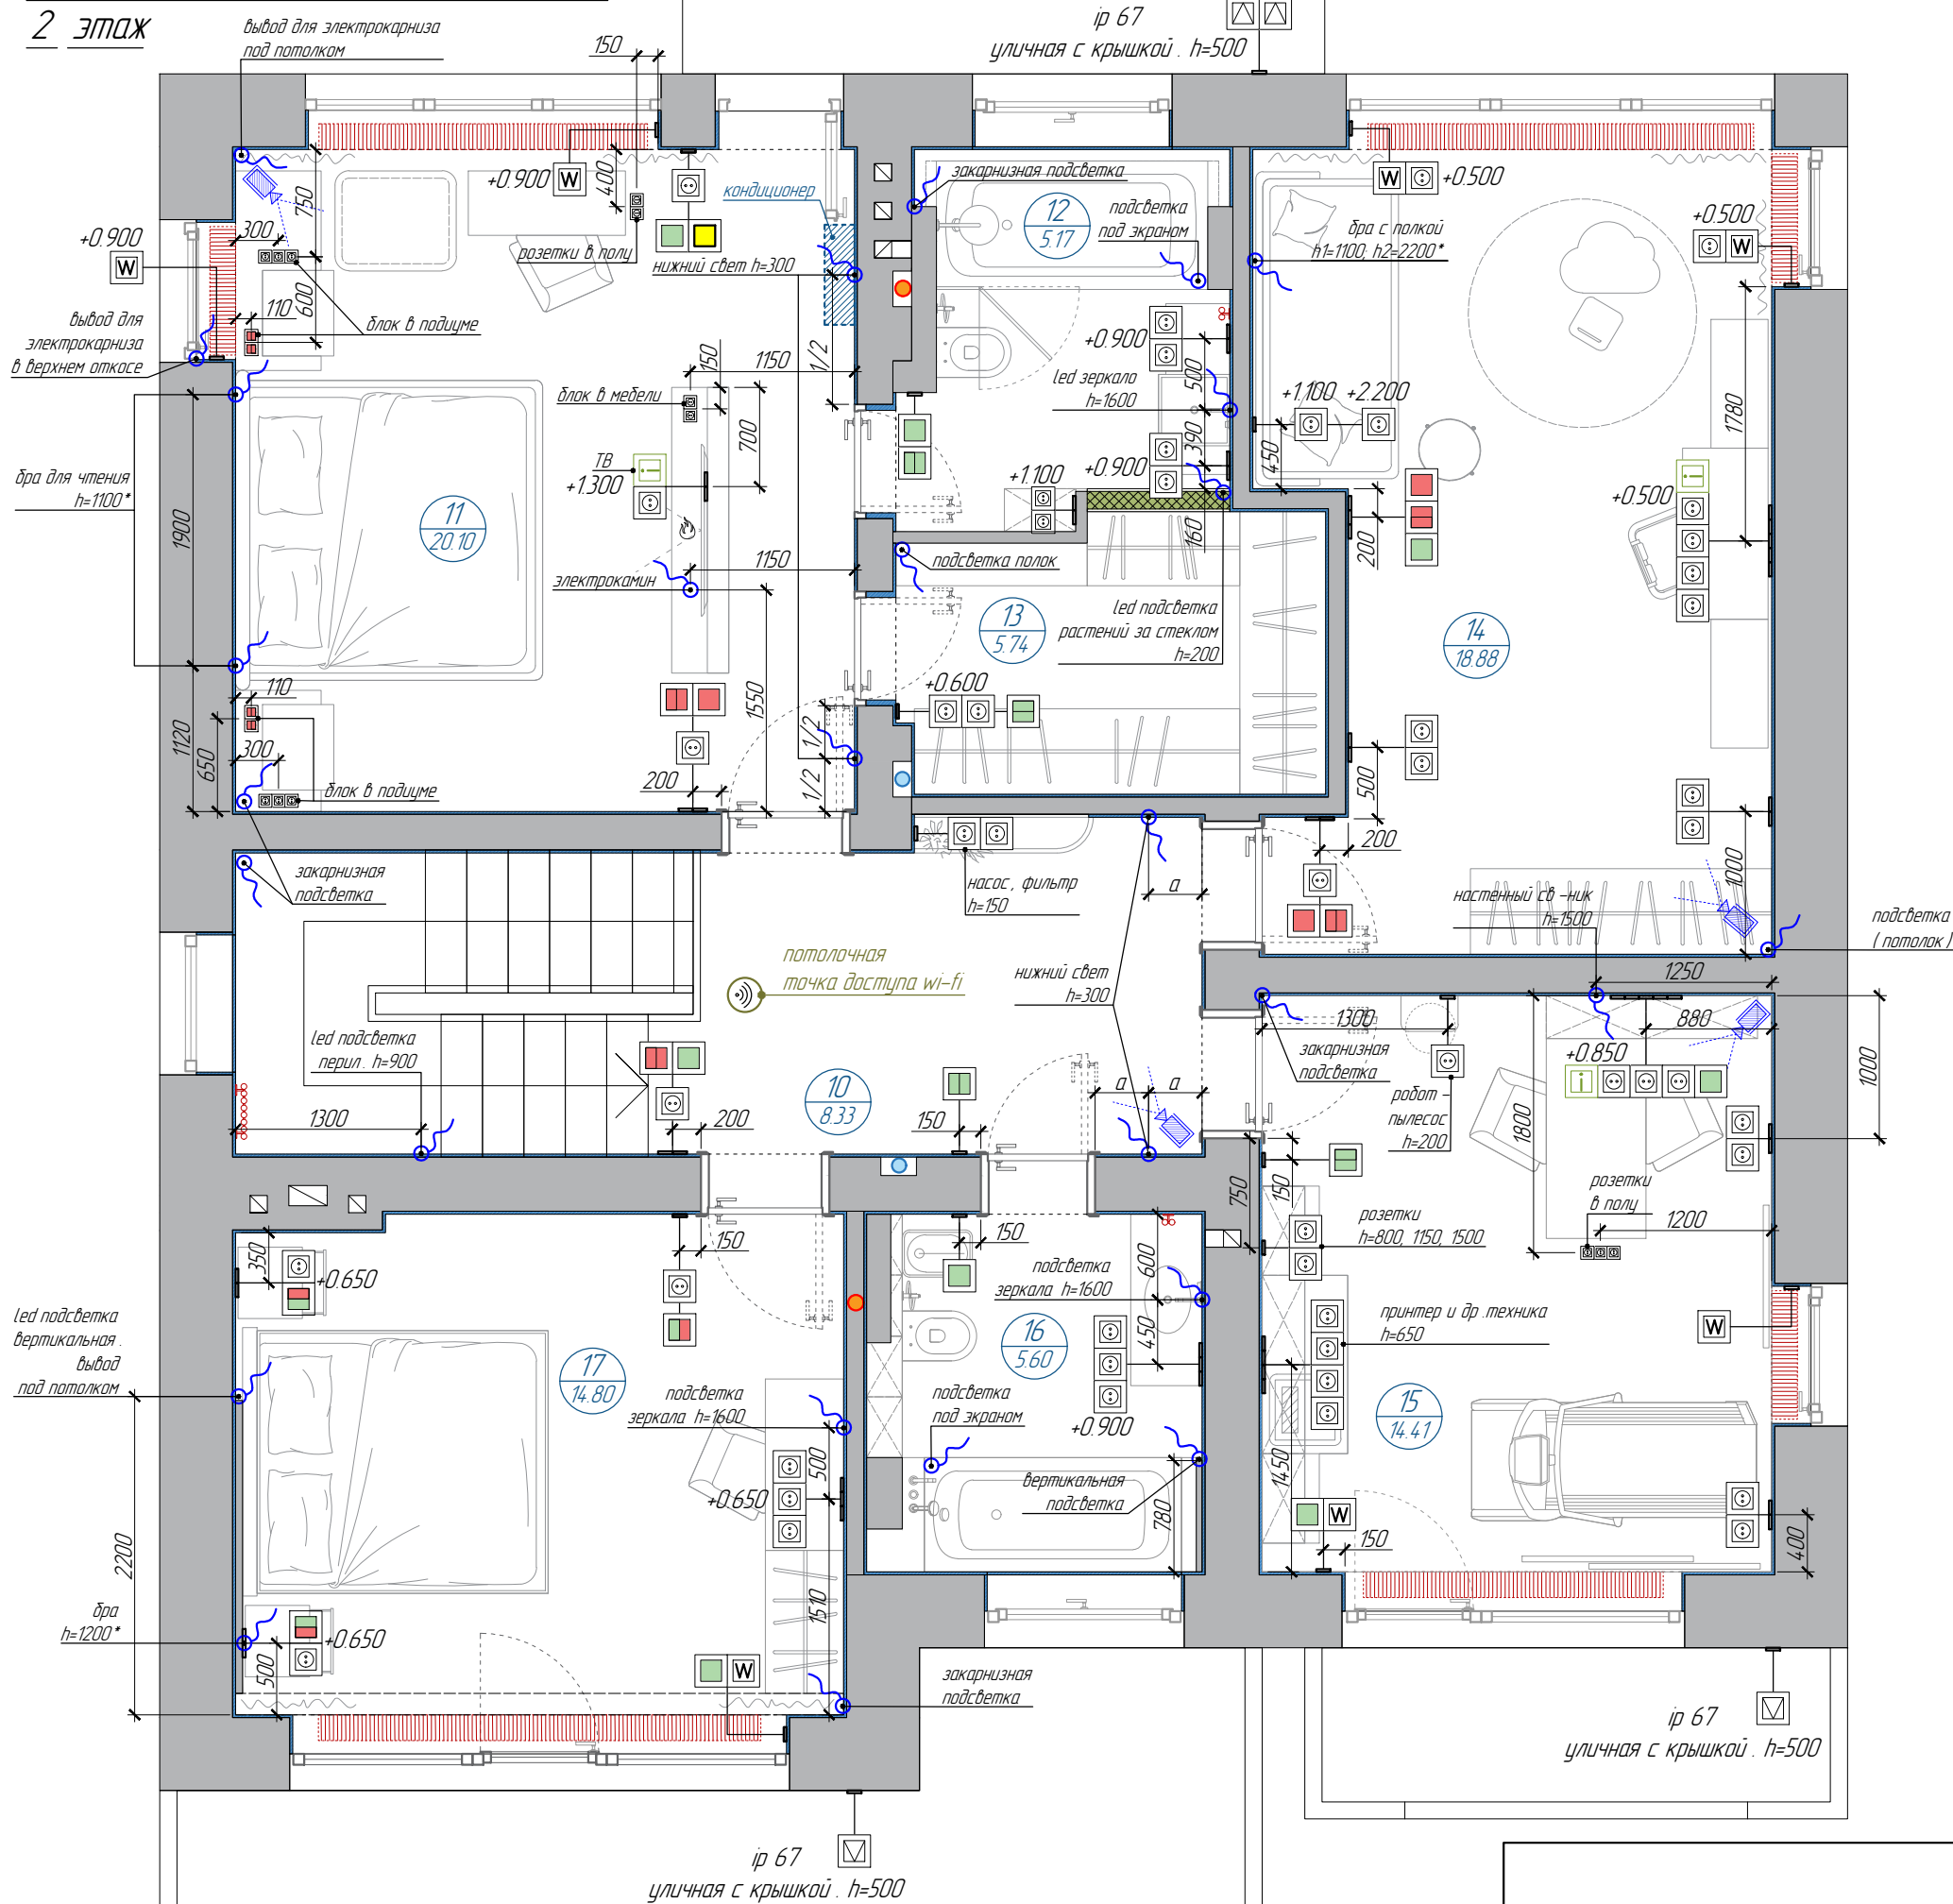

| УСЛОВНЫЕ ОБОЗНАЧЕНИЯ |                                                                  |
|----------------------|------------------------------------------------------------------|
|                      | штепсельная розетка для скрытой установки                        |
|                      | штепсельная розетка для скрытой установки над столешницей        |
|                      | штепсельная розетка для скрытой установки С КРЫШКОЙ              |
|                      | терморегулятор внутрипольного конвектора                         |
|                      | кабель -канал                                                    |
|                      | розетка RG-45                                                    |
|                      | щиток                                                            |
|                      | модем, роутер                                                    |
|                      | вывод провода для прямого подключения                            |
|                      | выключатель одноклавишный                                        |
|                      | выключатель двухклавишный                                        |
|                      | переключатель одноклавишный                                      |
|                      | переключатель двухклавишный                                      |
|                      | выключатель одноклавишный (к нему запитана розетка для гирлянды) |
|                      | контрольный выключатель (на весь свет)                           |
|                      | потолочная точка доступа wi-fi                                   |
|                      | камера видеонаблюдения                                           |

ПРИМЕЧАНИЯ

- Любые расхождения проектных размеров с фактическими, нестыковки, изменение конструктивных решений и т.п. согласовывать с автором проекта в рамках авторского надзора
  - Данный лист смотреть совместно с листами "Схема размещения групп светильников с привязкой к выключателям"
  - Высоты указаны от отметки чистого пола 0.000
  - Все розетки располагать на высоте 0.3 м, а выключатели на высоте 0.9 м от уровня чистого пола до оси электроприбора или группы электроприборов, если не указано иное
  - К выключателям для праздничного освещения (гирлянд) запитываются розетки на откосах, предназначенные для подключения светового оборудования
  - На этапе разводки электрики предусмотреть выводы для системы кондиционирования, а также:
    - видеонаблюдения
    - охранной сигнализации
- Размещение выводов выполнить согласно предписаниям от организаций, монтирующих данные системы
7. Для выключателей, расположенных в непосредственной близости от радиаторов отопления, обеспечить изоляцию силовых кабелей с целью исключения нагрева электрооборудования


кп РАЙТ ЭКО

Архитектор Овчарова Ольга

План размещения электрооборудования. 2 этаж

ОЗВЧАРОВА PROJECT

Схема освещения . 1 этаж

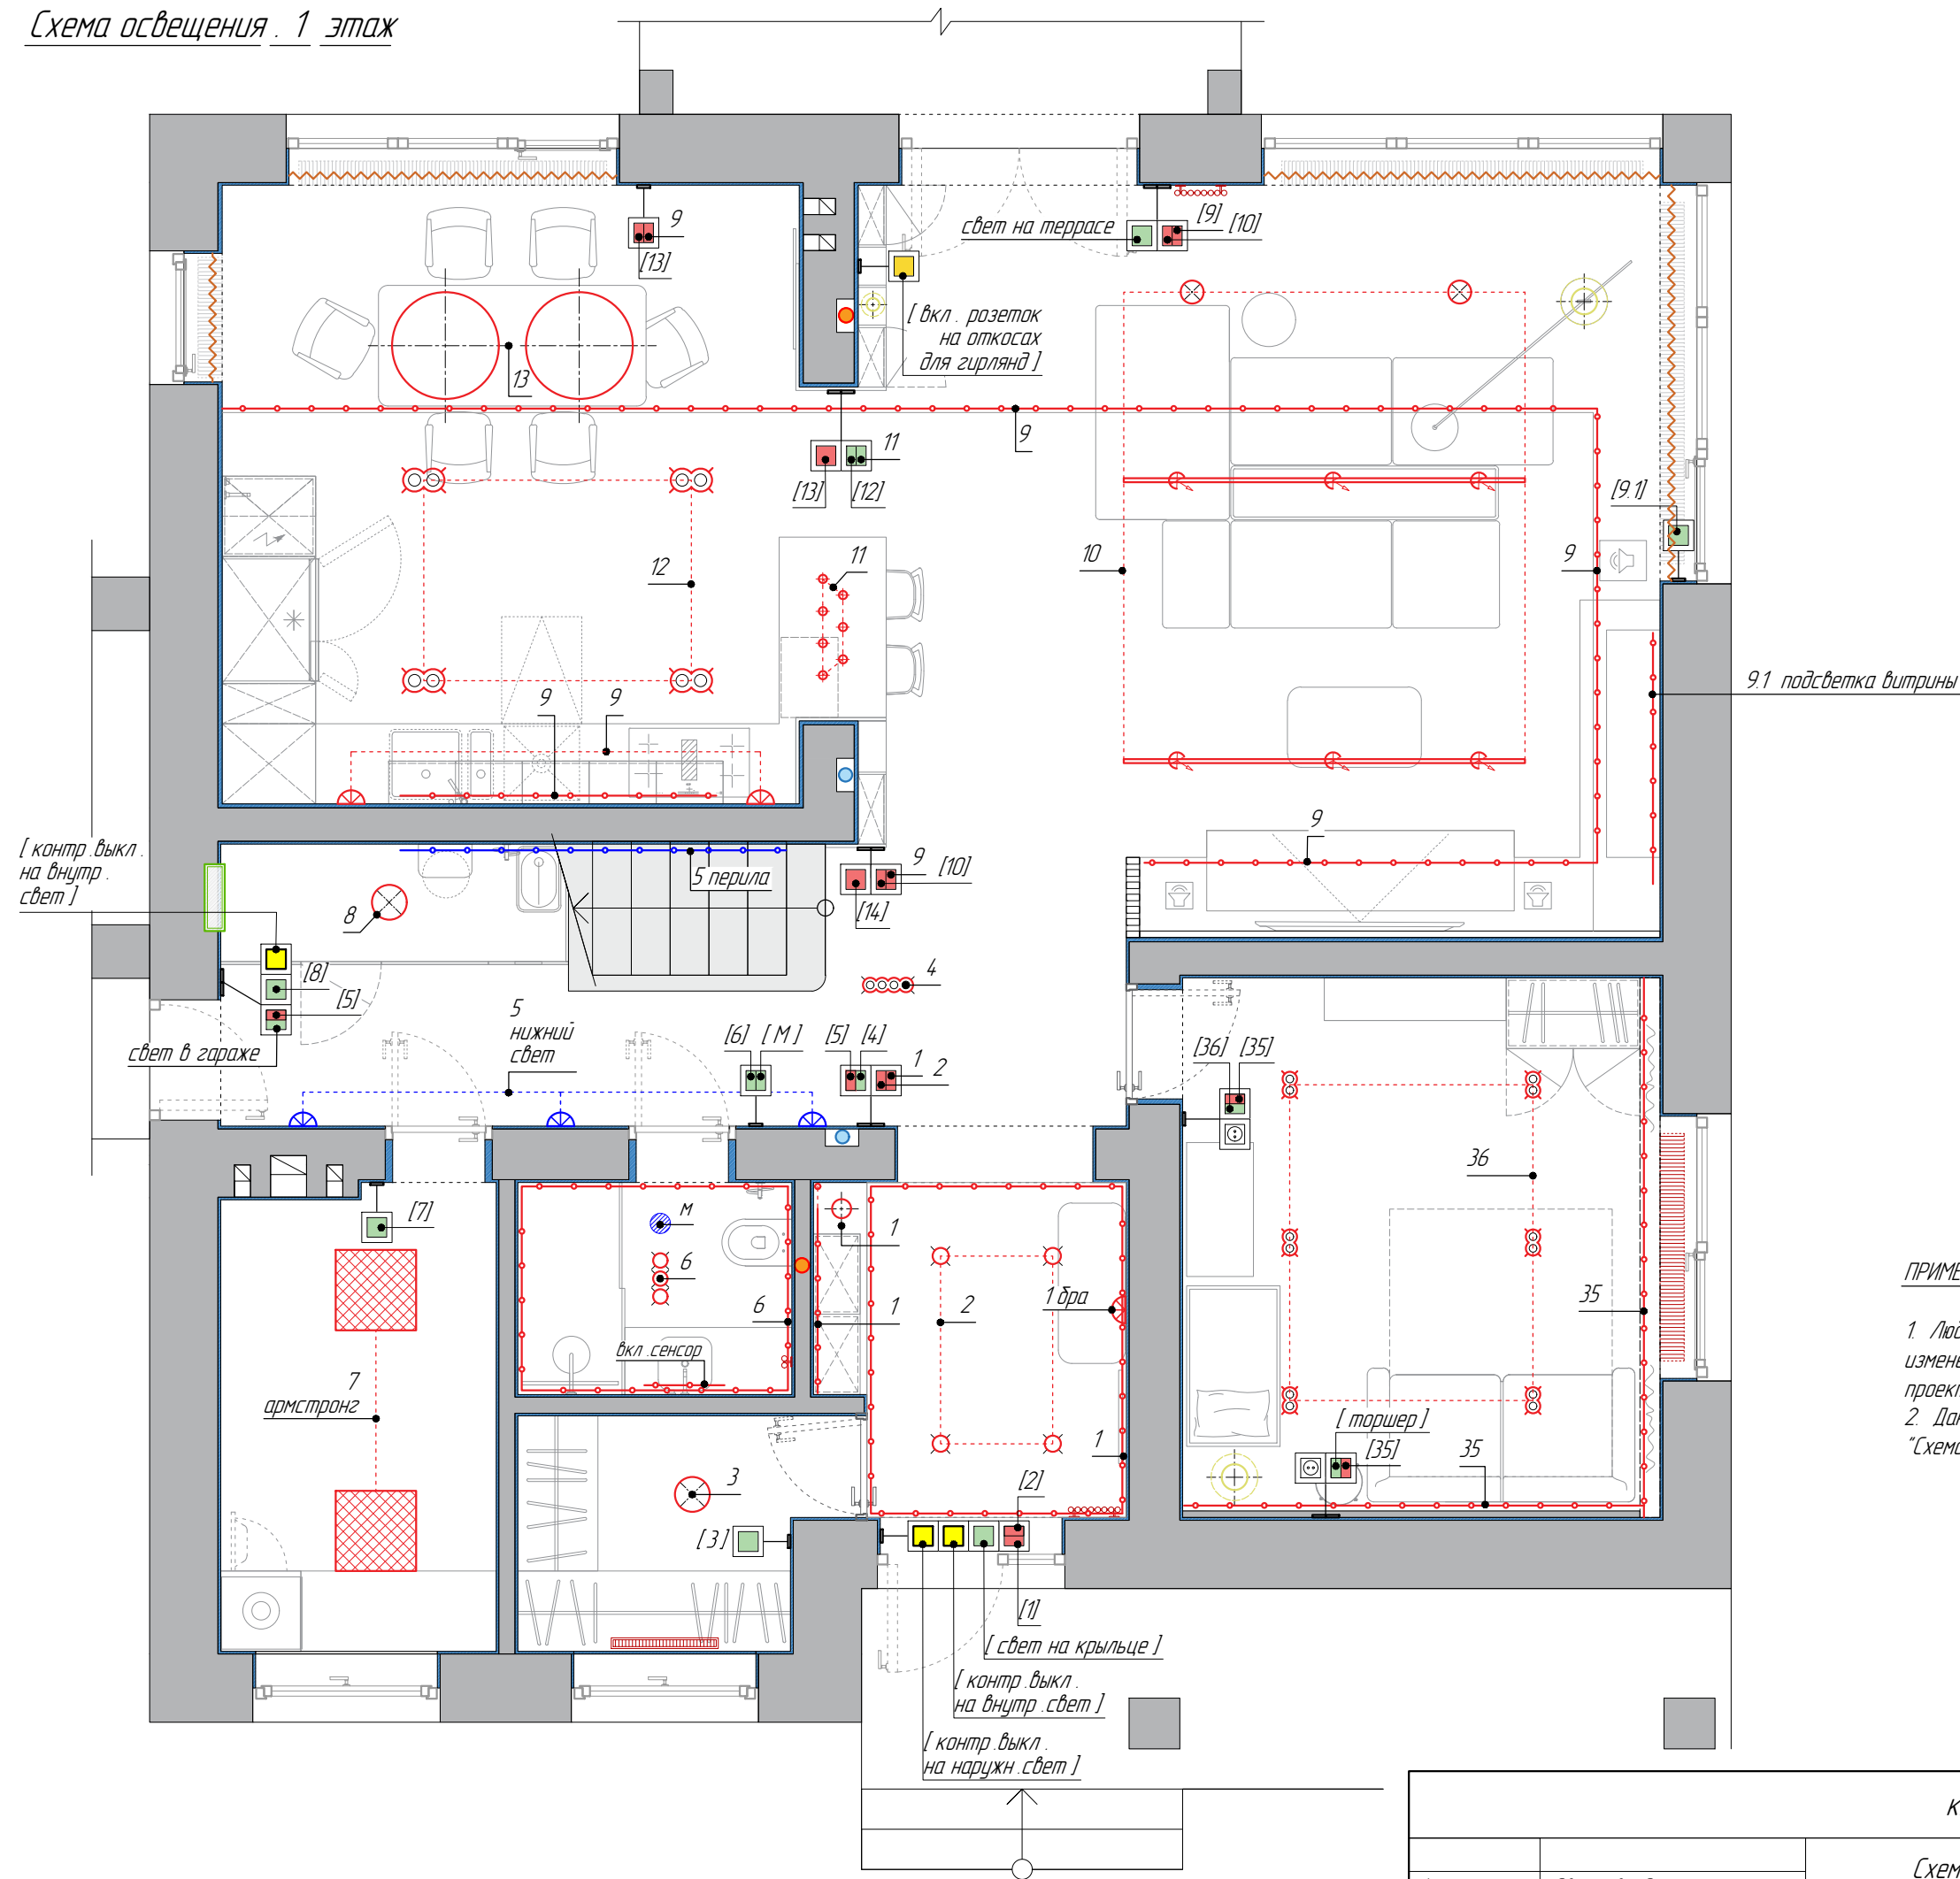

|  | УСЛОВНЫЕ ОБОЗНАЧЕНИЯ                   |
|--|----------------------------------------|
|  | электровентилятор                      |
|  | люстра/подвесной св-ник                |
|  | потолочный накладной светильник        |
|  | потолочный встраиваемый св-ник         |
|  | потолочный встраиваемый св-ник двойной |
|  | настенный светильник (бра)             |
|  | трековый светильник                    |
|  | led подсветка                          |
|  | гирлянда                               |
|  | выключатель одноклавишный              |
|  | выключатель двухклавишный              |
|  | выключатель проходной                  |
|  | выключатель проходной двухклавишный    |
|  | напольный / настольный светильник      |
|  | контрольный выключатель                |

ПРИМЕЧАНИЯ

- Любые расхождения проектных размеров с фактическими, нестыковки, изменение конструктивных решений и т.п., согласовывать с автором проекта в рамках авторского надзора
- Данный лист смотреть совместно с листами "Схема размещения электрооборудования" и "Схема потолка"


кп РАЙТ ЭКО

Архитектор Овчарова Ольга

Схема освещения . 1 этаж

ООО ЧИПАРОВА  
PROJECT



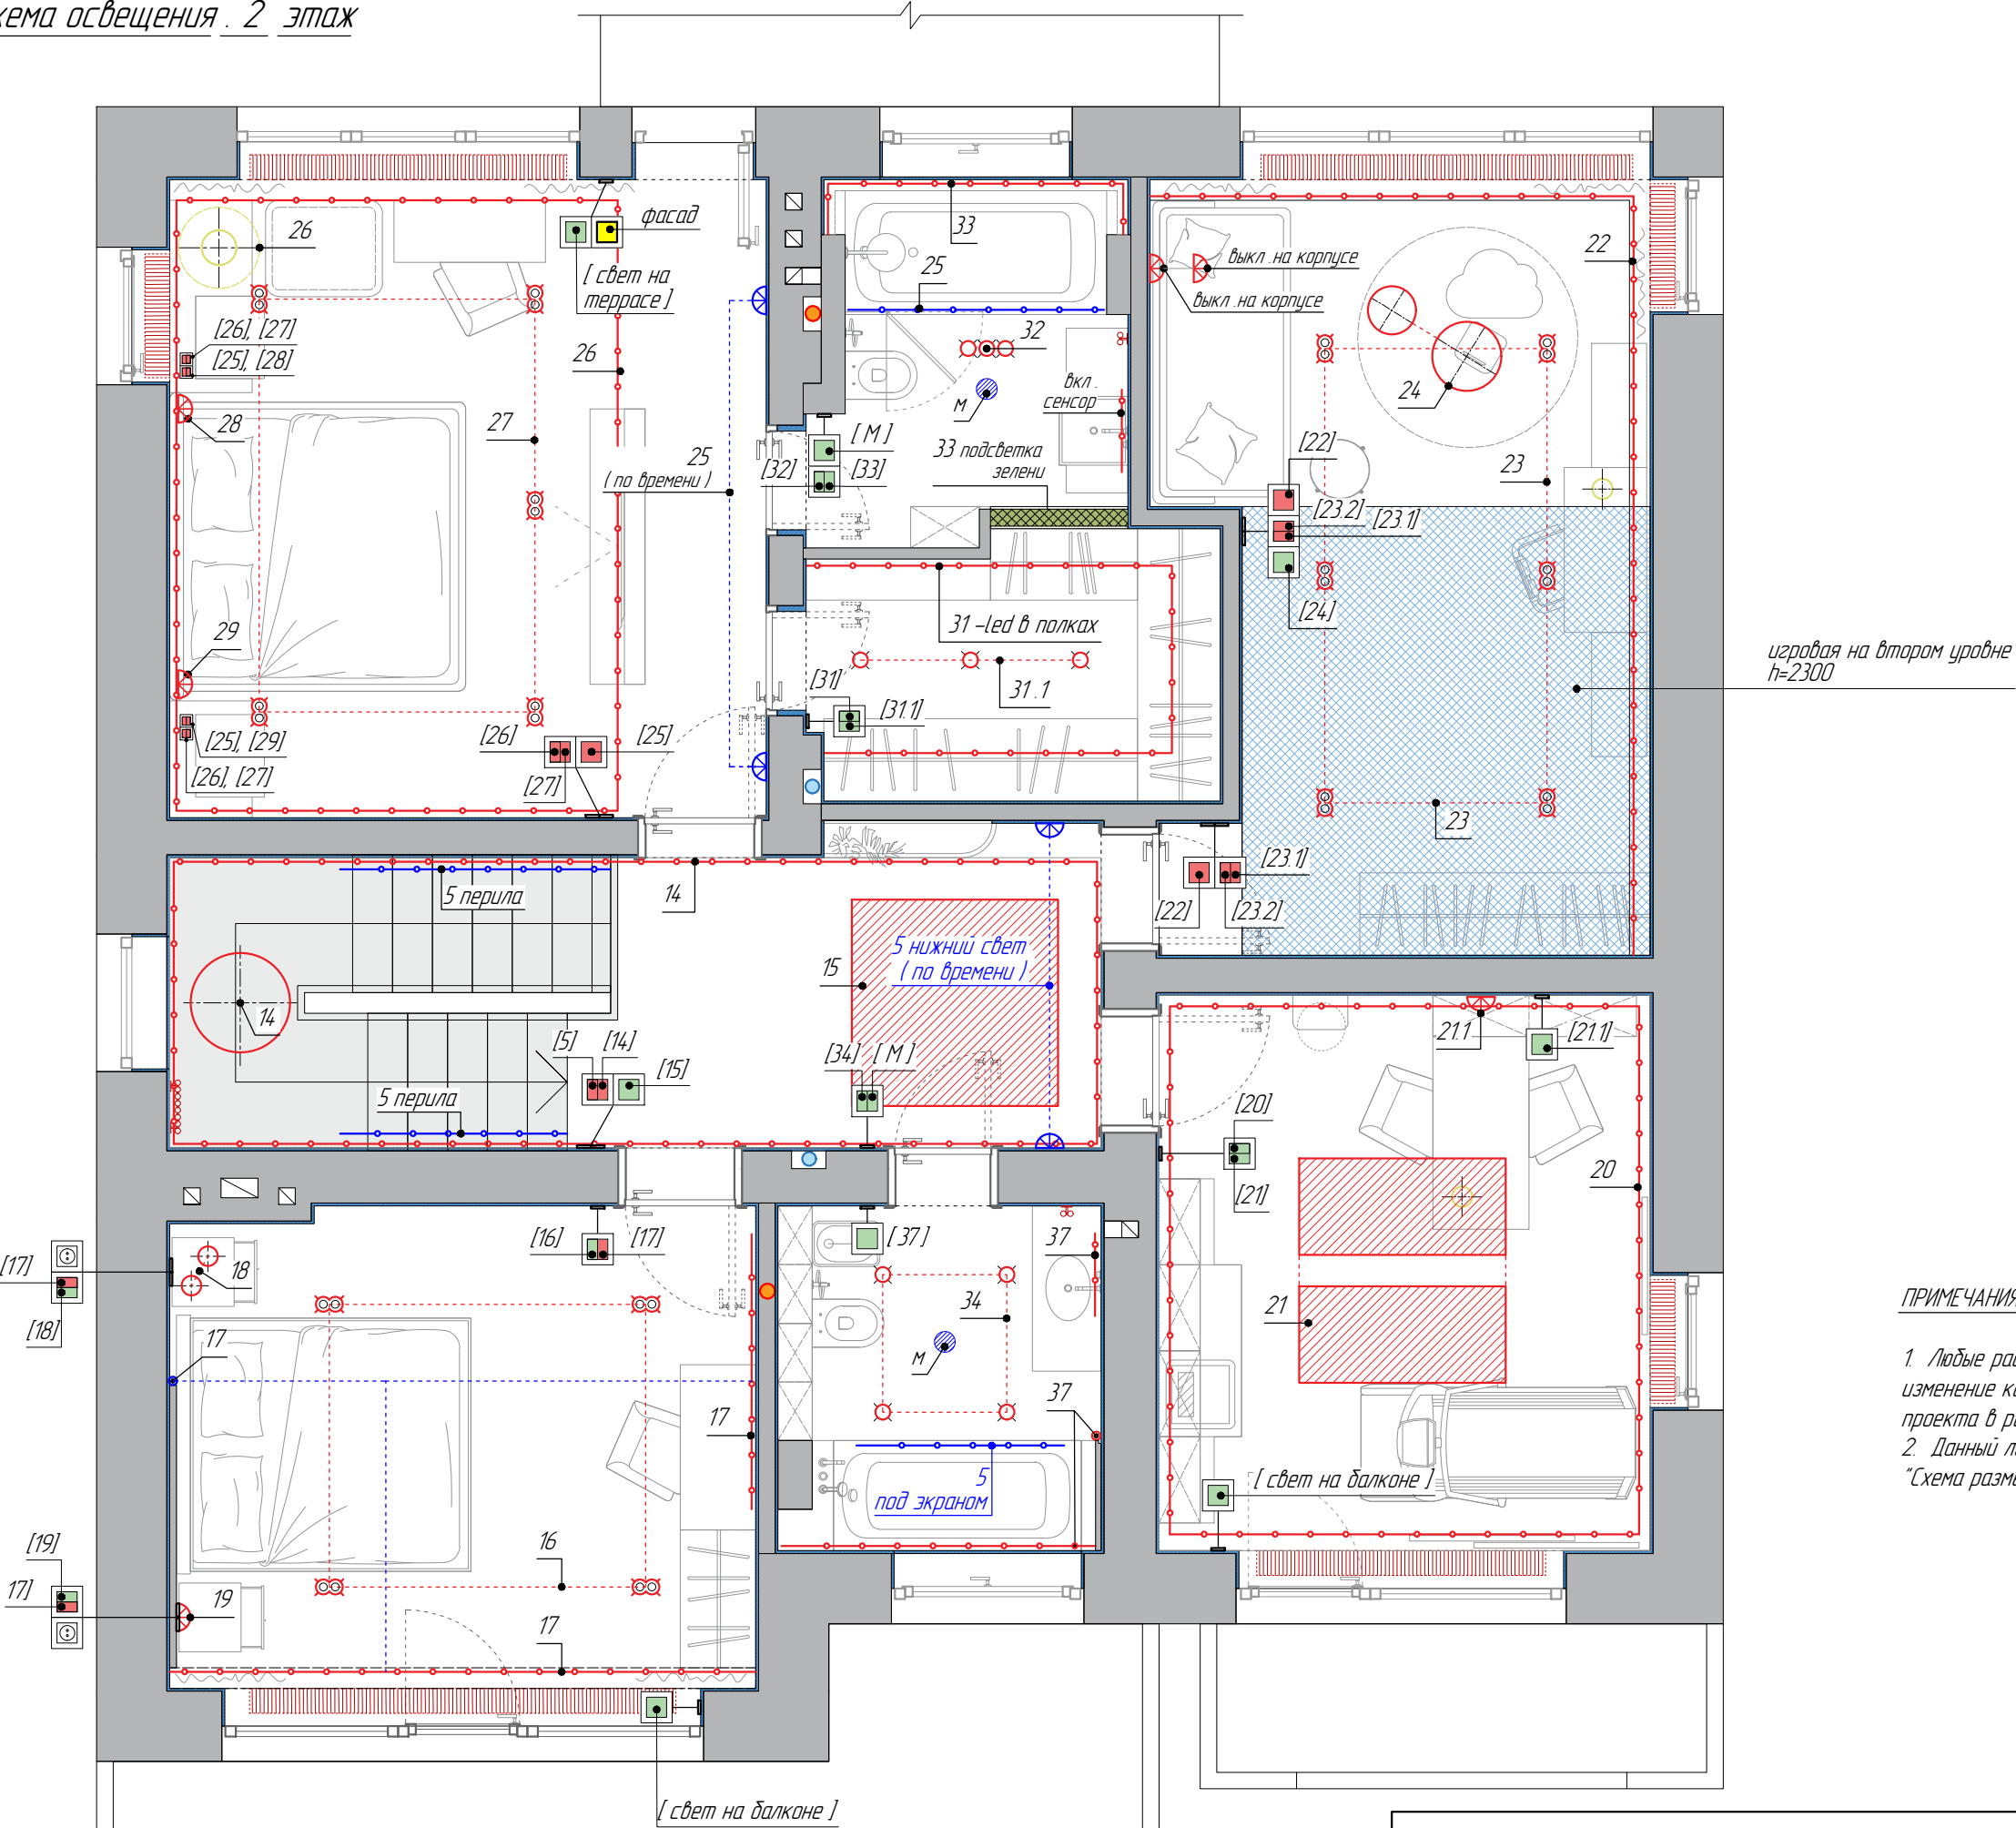


|  | УСЛОВНЫЕ ОБОЗНАЧЕНИЯ                   |
|--|----------------------------------------|
|  | электровентилятор                      |
|  | люстра/подвесной св-ник                |
|  | потолочный накладной светильник        |
|  | потолочный встраиваемый св-ник         |
|  | потолочный встраиваемый св-ник двойной |
|  | настенный светильник (бра)             |
|  | трековый светильник                    |
|  | led подсветка                          |
|  | световой потолок                       |
|  | выключатель одноклавишный              |
|  | выключатель двухклавишный              |
|  | выключатель проходной                  |
|  | выключатель проходной двухклавишный    |
|  | напольный / настольный светильник      |

ПРИМЕЧАНИЯ

- Любые расхождения проектных размеров с фактическими, нестыковки, изменение конструктивных решений и т.п., согласовывать с автором проекта в рамках авторского надзора
- Данный лист смотреть совместно с листами "Схема размещения электрооборудования" и "Схема потолка"

Схема участков водяного тёплого пола

1 этаж

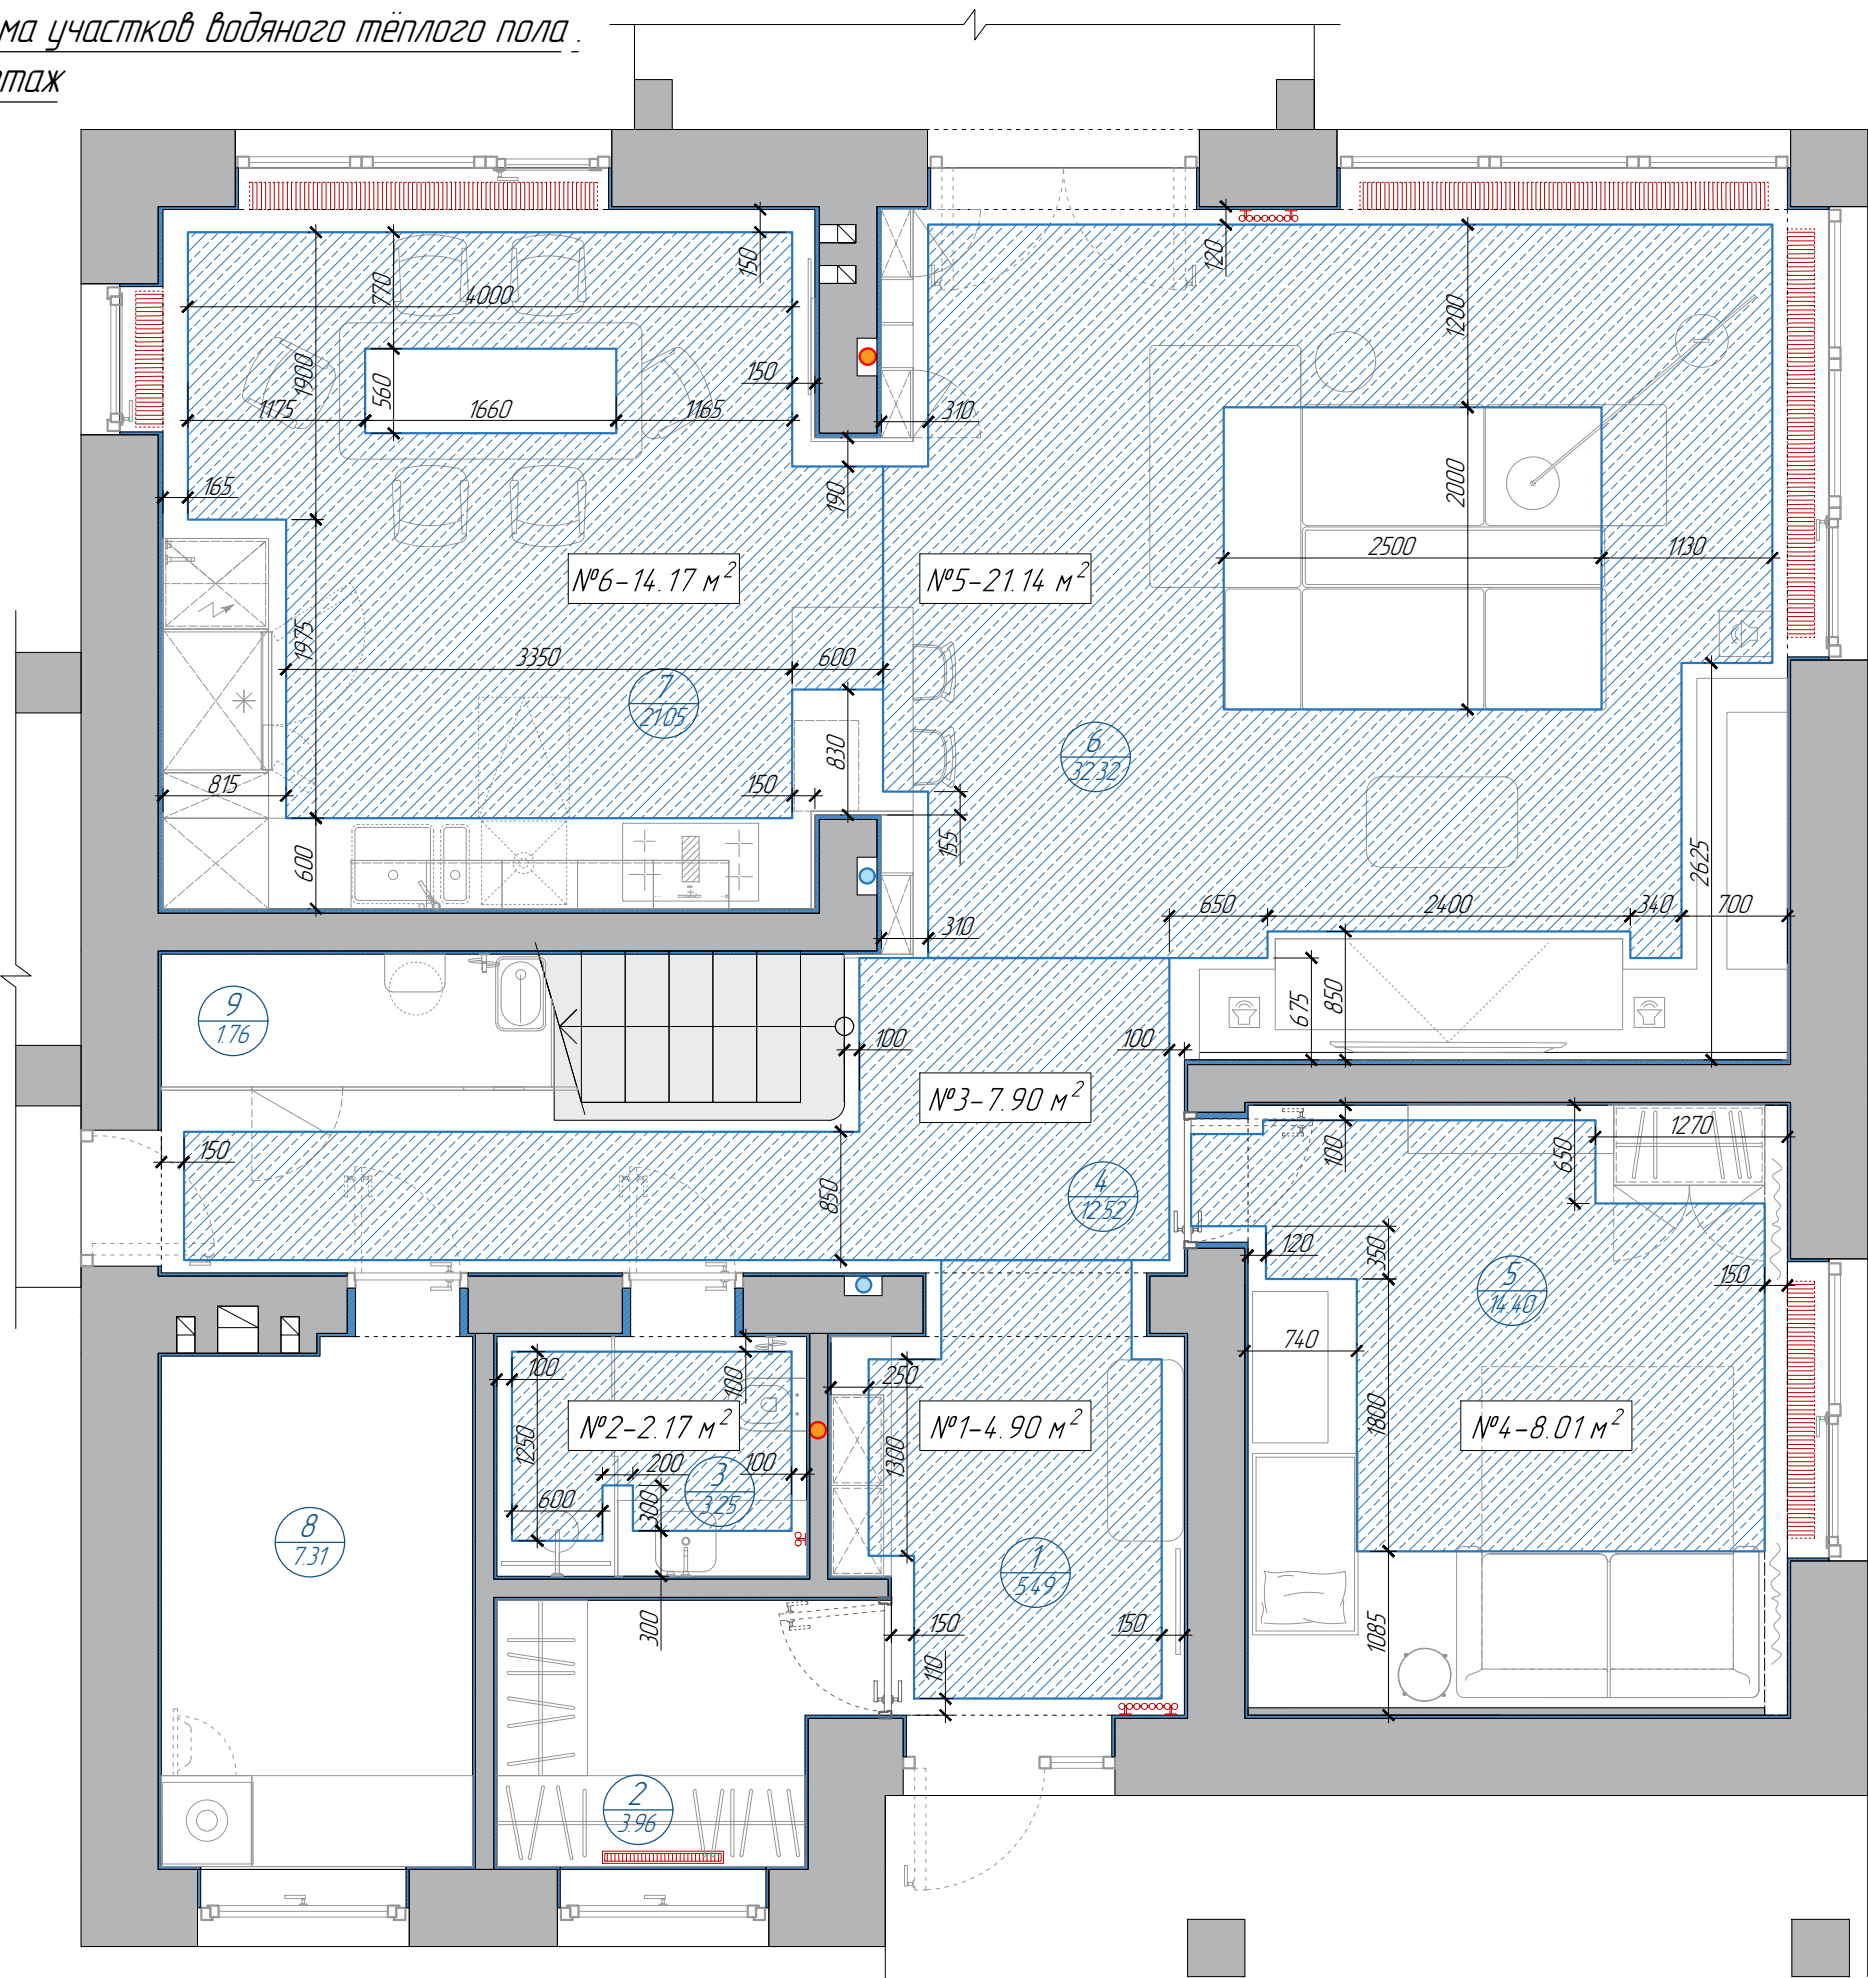

| Экспликация помещений        |        |                        |                          |        |            |
|------------------------------|--------|------------------------|--------------------------|--------|------------|
| Этаж                         | № пом. | Наименование помещения | Площадь , м <sup>2</sup> |        | Примечание |
|                              |        |                        | осн.                     | вспом. |            |
| 1                            | 1      | Прихожая               |                          | 5.49   |            |
|                              | 2      | Гардеробная            |                          | 3.96   |            |
|                              | 3      | Санузел гостей         |                          | 3.25   |            |
|                              | 4      | Лестничный холл        |                          | 12.52  |            |
|                              | 5      | Комната няни           | 14.40                    |        |            |
|                              | 6      | Гостиная               | 32.32                    |        |            |
|                              | 7      | Кухня –столовая        | 21.05                    |        |            |
|                              | 8      | Котельная              |                          | 7.31   |            |
| 2                            | 9      | Тех. помещение         |                          | 1.76   |            |
|                              | 10     | Лестничный холл        |                          | 8.33   |            |
|                              | 11     | Мастер –спальня        | 20.10                    |        |            |
|                              | 12     | Ванная комната         |                          | 5.17   |            |
|                              | 13     | Гардеробная            |                          | 5.74   |            |
|                              | 14     | Детская комната        | 18.88                    |        |            |
|                              | 15     | Кабинет                | 14.41                    |        |            |
|                              | 16     | Санузел                |                          | 5.60   |            |
|                              | 17     | Гостевая комната       | 14.80                    |        |            |
|                              |        | Итого по помещениям    | 135.96                   | 59.13  |            |
| Общая площадь помещений дома |        |                        | 195.09                   |        |            |

Технико -экономические показатели

| Вид теплого пола   | Этаж | S, м² |
|--------------------|------|-------|
| Водяной теплый пол | 1    | 58.29 |

УСЛОВНЫЕ ОБОЗНАЧЕНИЯ

- стены и перегородки из керамоблока
- стояк канализации
- стояк лифтовой канализации
- штукатурный слой
- внутрипольный конвектор
- панельный радиатор
- вертикальный трубчатый радиатор
- участок размещения водяного тёплого пола
- №6-14.17 м² номер и площадь участка

ПРИМЕЧАНИЯ


1. При монтаже теплых полов учитывать тип напольного покрытия и требования от производителя напольных покрытий к устройству теплого пола

кп РАЙТ ЭКО

|                           |  |                                                 |                       |
|---------------------------|--|-------------------------------------------------|-----------------------|
| Архитектор Овчарова Ольга |  | Схема участков<br>водяного тёплого пола. 1 этаж | ООО ЧАЛОВА<br>PROJECT |
|---------------------------|--|-------------------------------------------------|-----------------------|



Схема участков водяного тёплого пола  
2 этаж

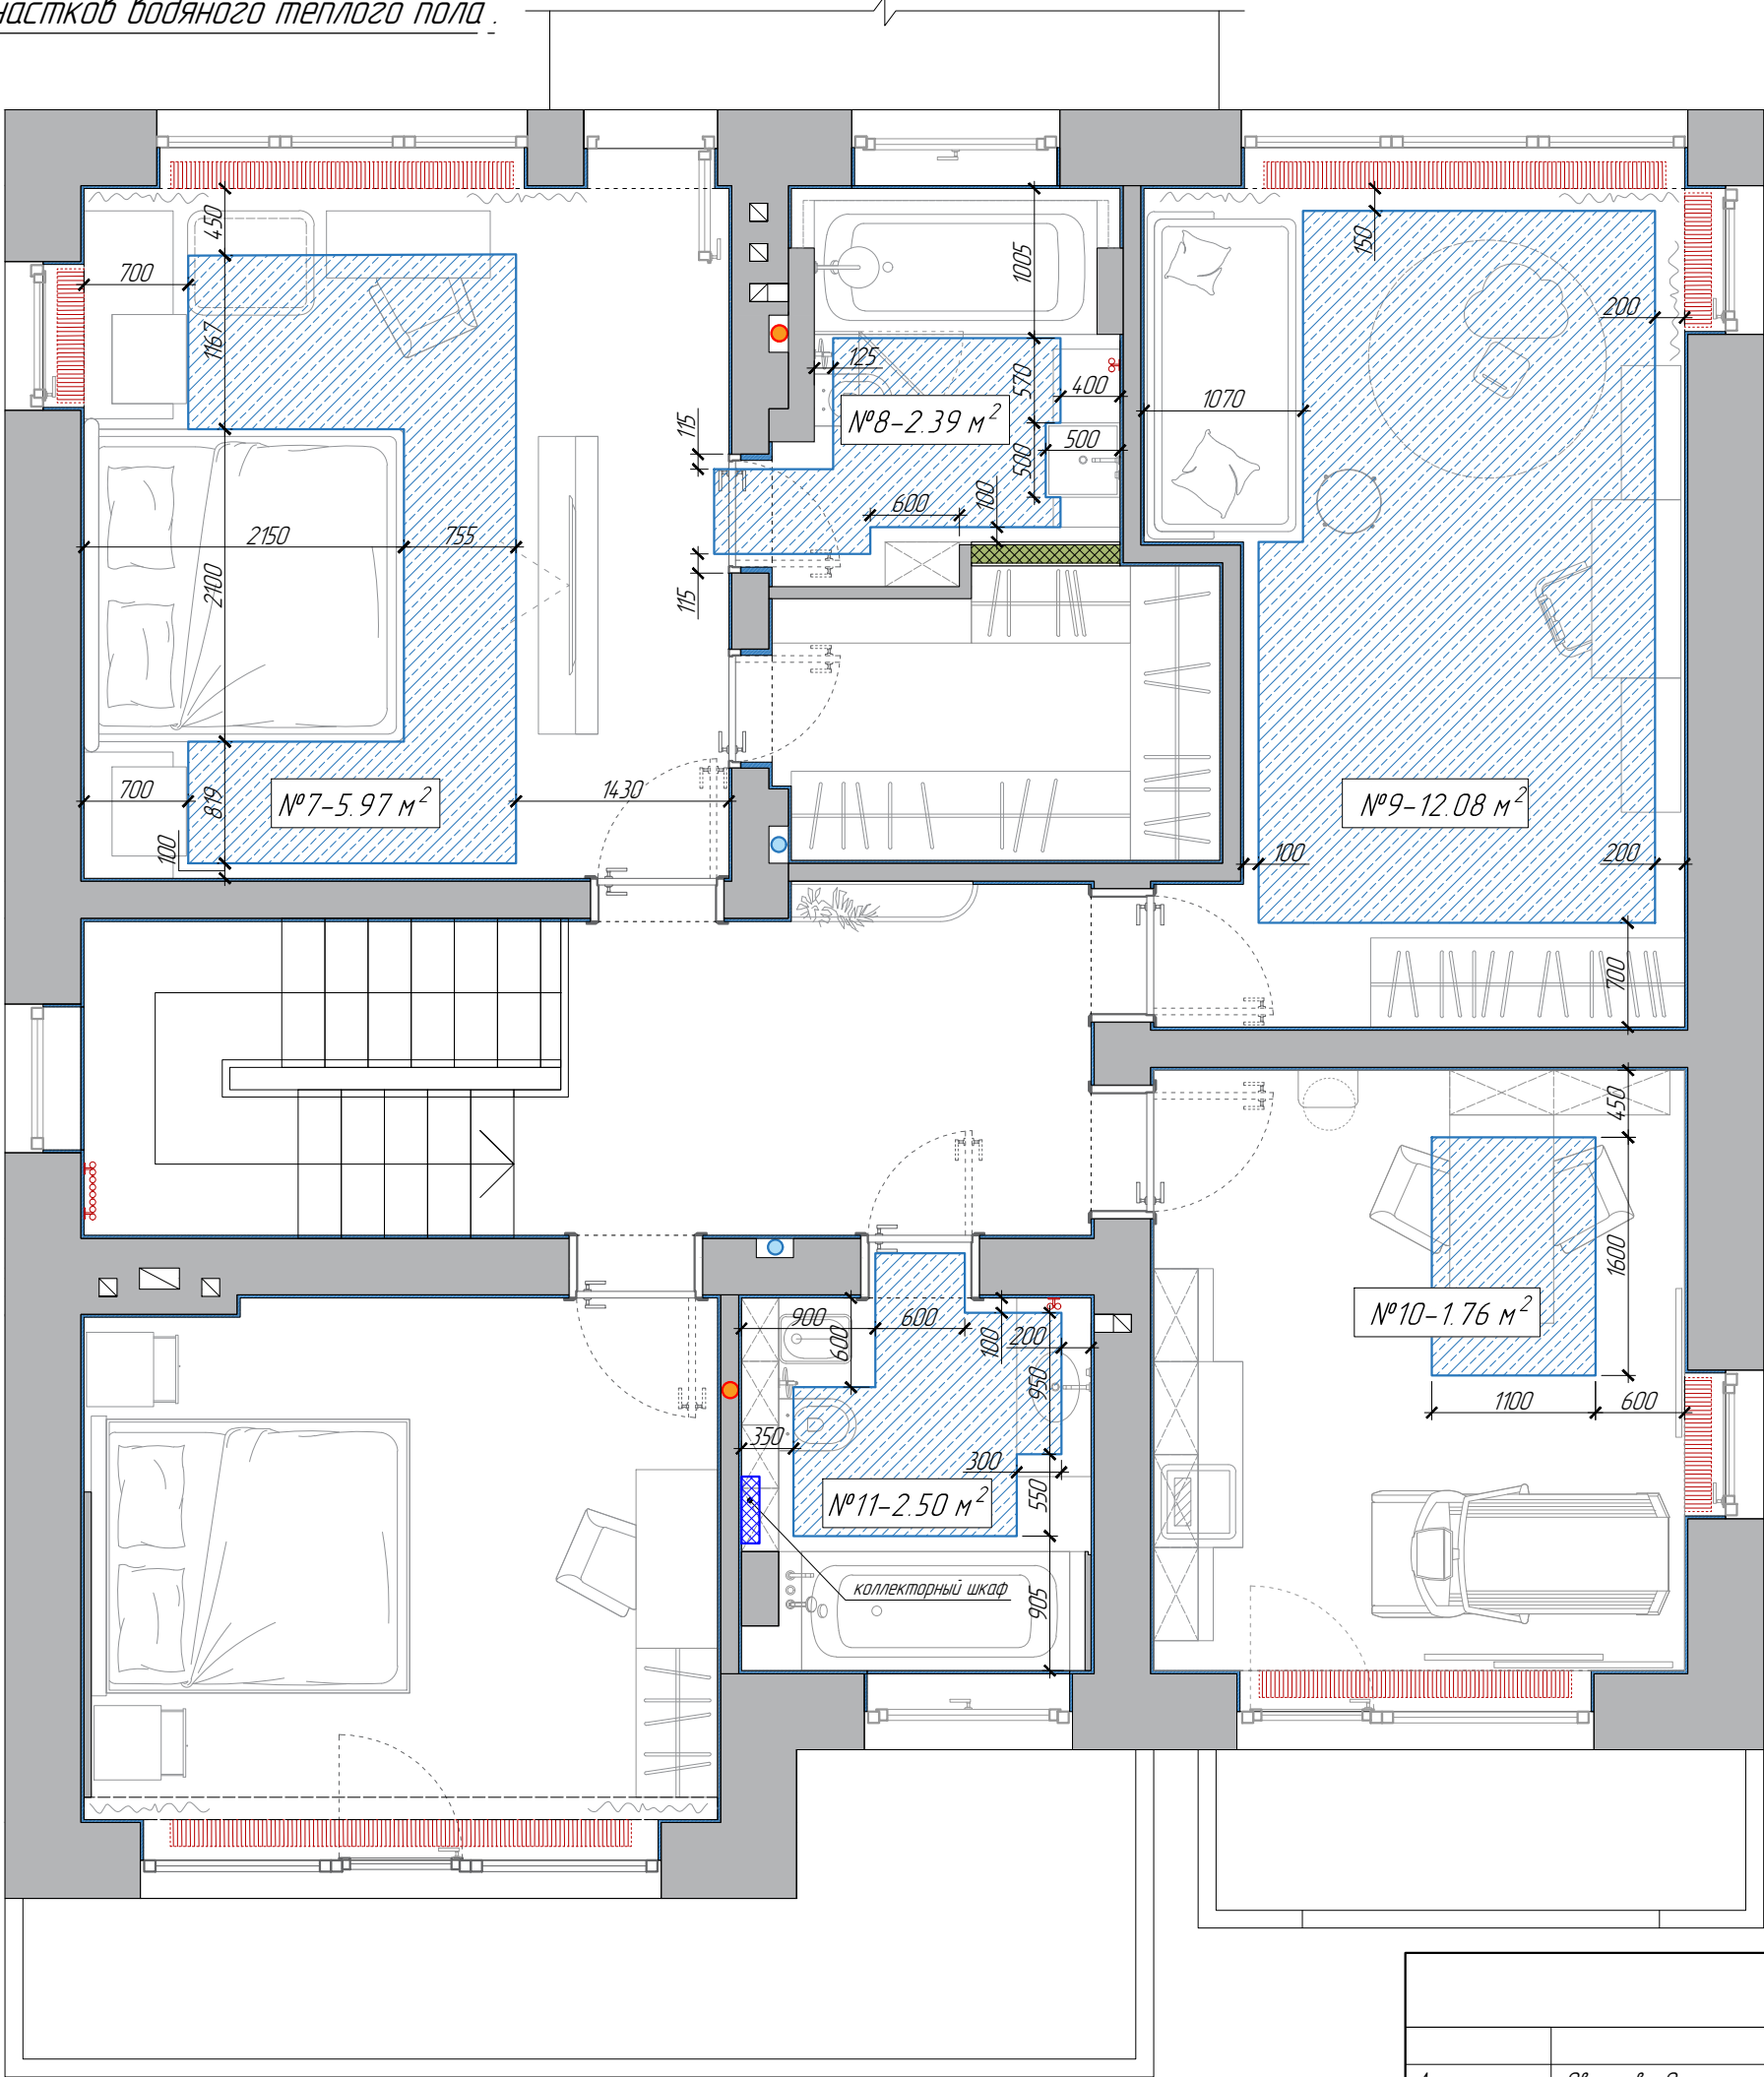

| Экспликация помещений        |        |                        |                          |        |            |
|------------------------------|--------|------------------------|--------------------------|--------|------------|
| Этаж                         | № пом. | Наименование помещения | Площадь , м <sup>2</sup> |        | Примечание |
|                              |        |                        | осн.                     | вспом. |            |
| 1                            | 1      | Прихожая               |                          | 5.49   |            |
|                              | 2      | Гардеробная            |                          | 3.96   |            |
|                              | 3      | Санузел гостевой       |                          | 3.25   |            |
|                              | 4      | Лестничный холл        |                          | 12.52  |            |
|                              | 5      | Комната няни           | 14.40                    |        |            |
|                              | 6      | Гостиная               | 32.32                    |        |            |
|                              | 7      | Кухня –столовая        | 21.05                    |        |            |
|                              | 8      | Котельная              |                          | 7.31   |            |
|                              | 9      | Тех. помещение         |                          | 1.76   |            |
| 2                            | 10     | Лестничный холл        |                          | 8.33   |            |
|                              | 11     | Мастер –спальня        | 20.10                    |        |            |
|                              | 12     | Ванная комната         |                          | 5.17   |            |
|                              | 13     | Гардеробная            |                          | 5.74   |            |
|                              | 14     | Детская комната        | 18.88                    |        |            |
|                              | 15     | Кабинет                | 14.41                    |        |            |
|                              | 16     | Санузел                |                          | 5.60   |            |
|                              | 17     | Гостевая комната       | 14.80                    |        |            |
|                              |        | Итого по помещениям    | 135.96                   | 59.13  |            |
| Общая площадь помещений дома |        |                        | 195.09                   |        |            |

Технико -экономические показатели

| Вид теплого пола   | Этаж | S, м² |
|--------------------|------|-------|
| Водяной теплый пол | 2    | 24.7  |

УСЛОВНЫЕ ОБОЗНАЧЕНИЯ


- стены и перегородки из керамоблока
- стояк канализации
- стояк лифтовой канализации
- штукатурный слой
- внутрипольный конвектор
- панельный радиатор
- вертикальный трубчатый радиатор
- участок размещения водяного тёплого пола
- №6-9.2 м² номер и площадь участка

ПРИМЕЧАНИЯ

1. При монтаже теплых полов учитывать тип напольного покрытия и требования от производителя напольных покрытий к устройству теплого пола

|             |                |                                                 |                       |
|-------------|----------------|-------------------------------------------------|-----------------------|
| кп РАЙТ ЭКО |                | Схема участков<br>водяного тёплого пола. 2 этаж | ООО ЧАЛОВА<br>PROJECT |
| Архитектор  | Овчарова Ольга |                                                 |                       |

Схема потолка. 1 эт.

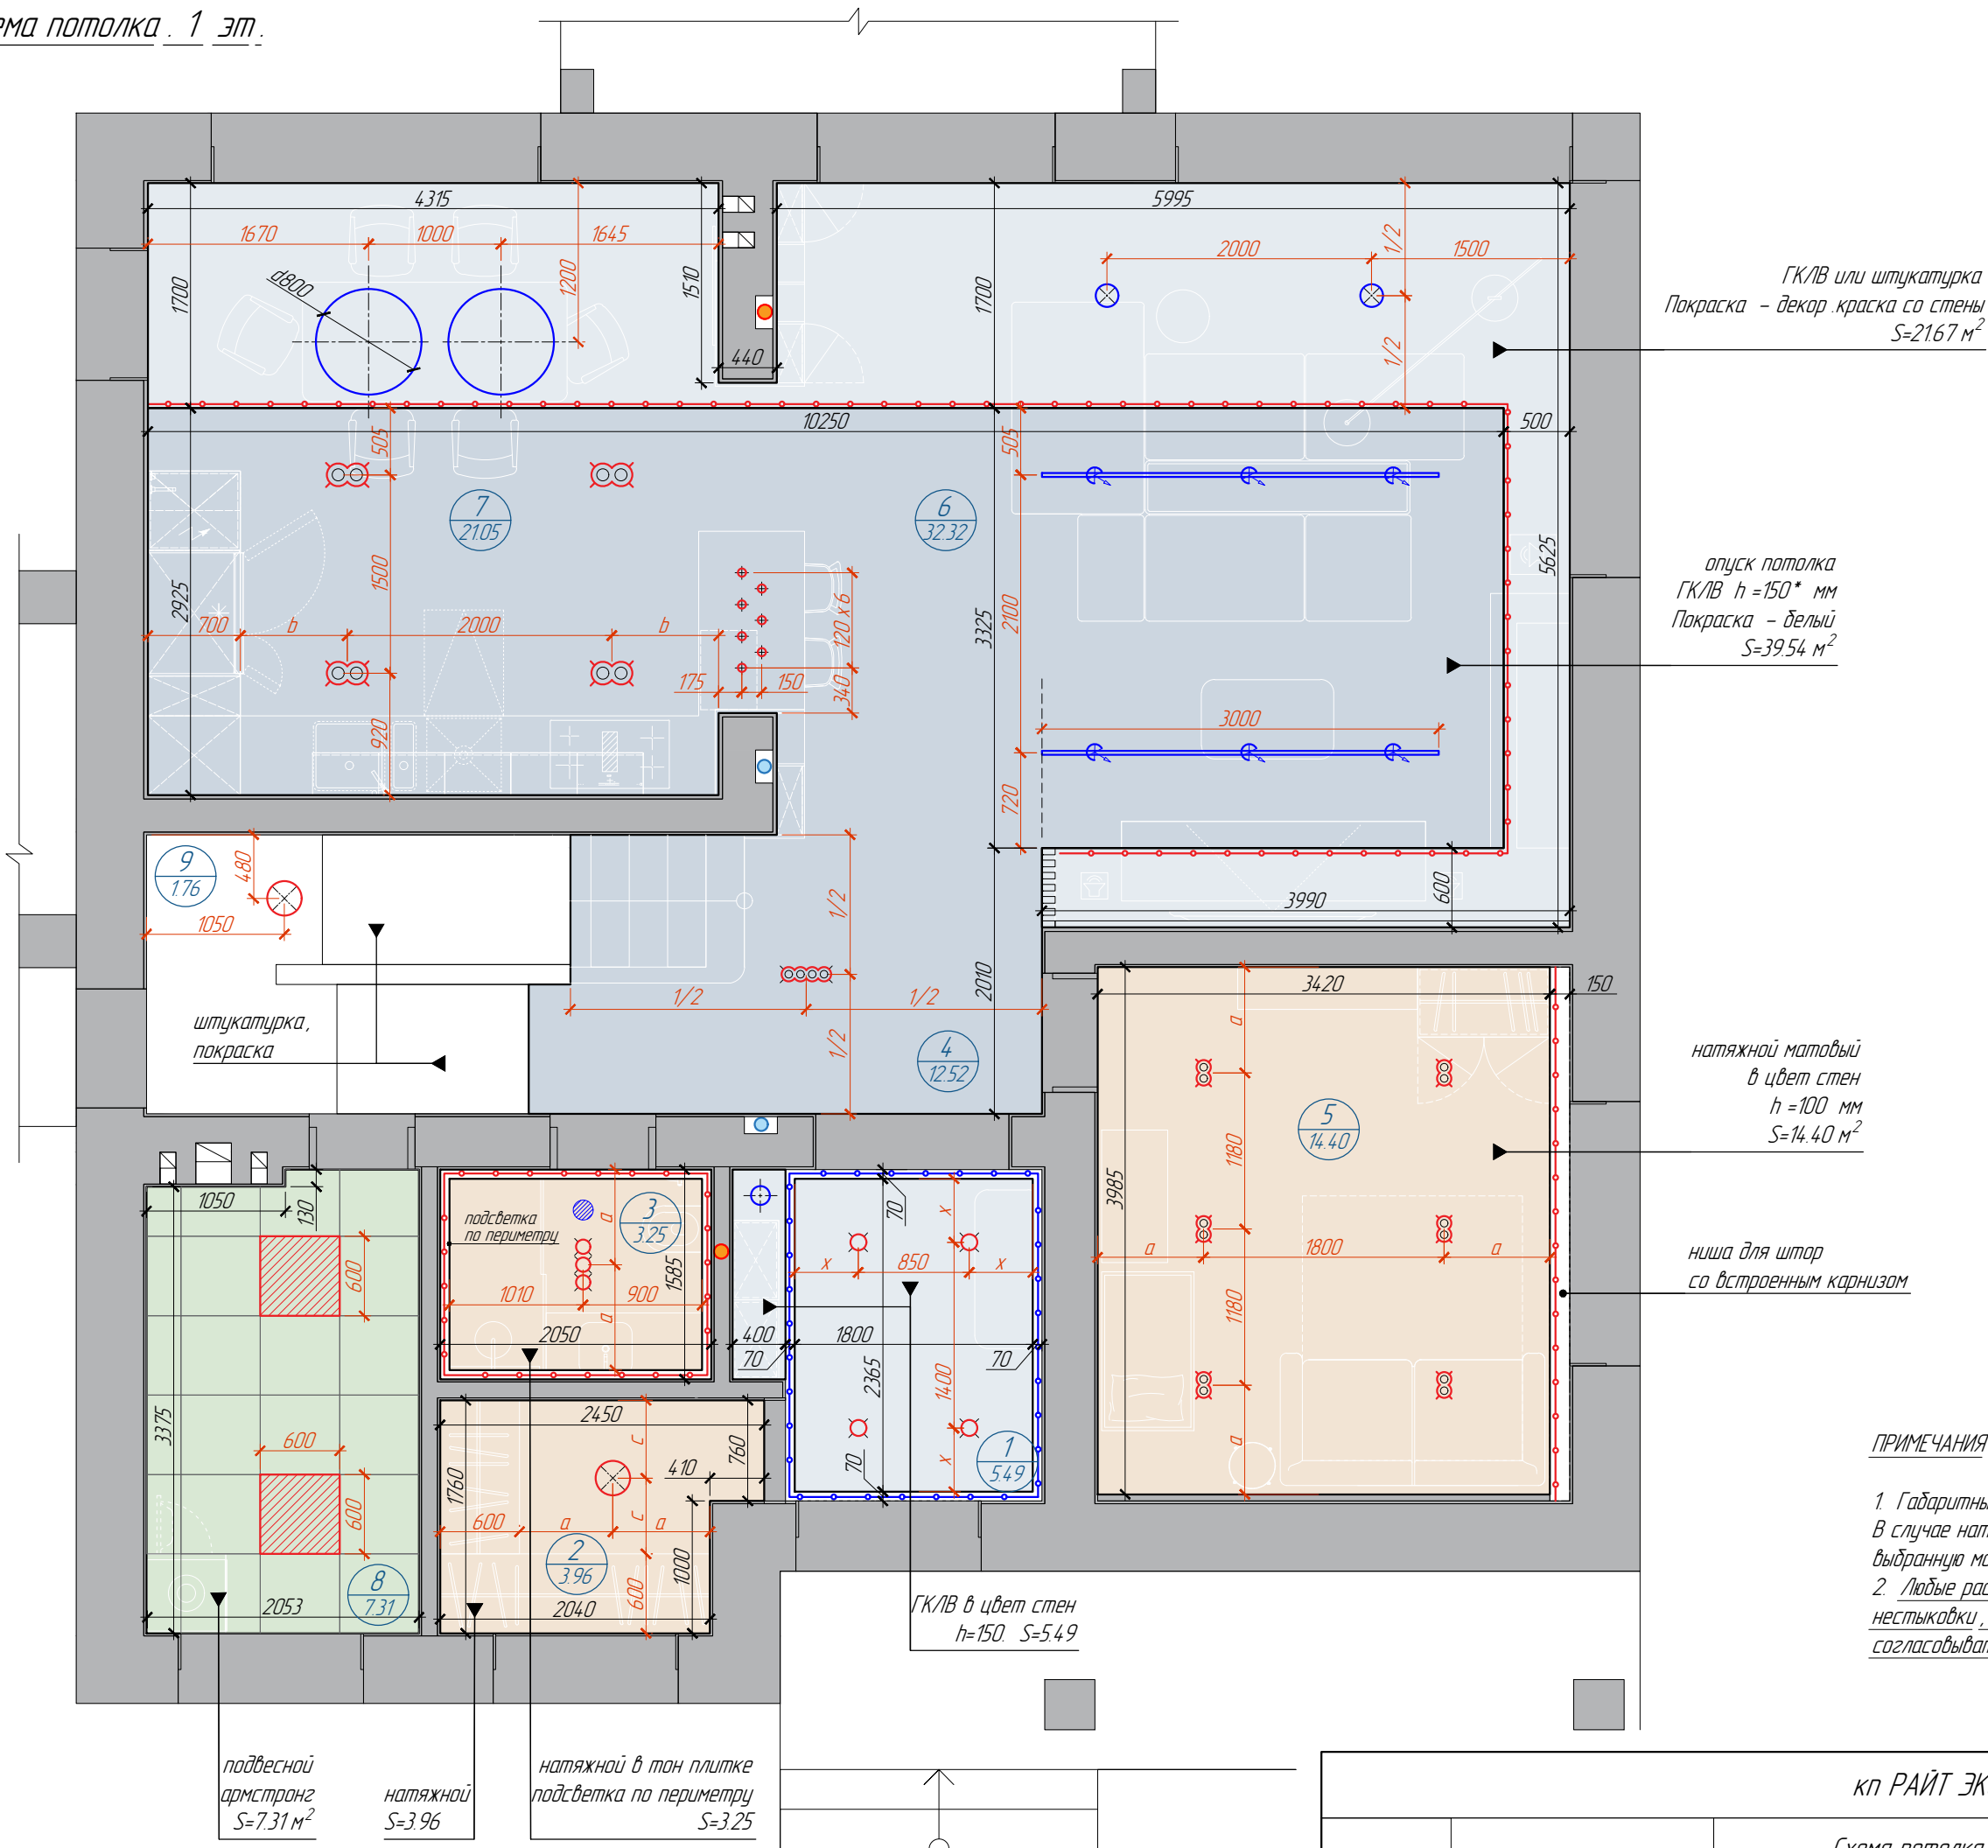

| УСЛОВНЫЕ ОБОЗНАЧЕНИЯ |                                 |
|----------------------|---------------------------------|
|                      | электровентилятор               |
|                      | люстра/подвесной св-ник         |
|                      | потолочный накладной светильник |
|                      | потолочный встраиваемый св-ник  |
|                      | потолочный встраиваемый св-ник  |
|                      | трековый светильник             |
|                      | led подсветка                   |
|                      | световой потолок                |


| УСЛОВНЫЕ ОБОЗНАЧЕНИЯ |                                    |
|----------------------|------------------------------------|
|                      | стены и перегородки из керамоблока |
|                      | стояк канализации                  |
|                      | стояк ливневой канализации         |
|                      | потолок ГК/Л                       |
|                      | натяжной потолок                   |
|                      | потолок Армстронг                  |

ПРИМЕЧАНИЯ

- Габаритные размеры ниш указаны по выступающим элементам. В случае натяжных потолков - данный размер корректируется под выбранную модель профиля
- Любые расхождения проектных размеров с фактическими, нестыковки, изменение конструктивных решений и т.п., согласовывать с автором проекта в рамках АН



Схема потолка . 2 эт.

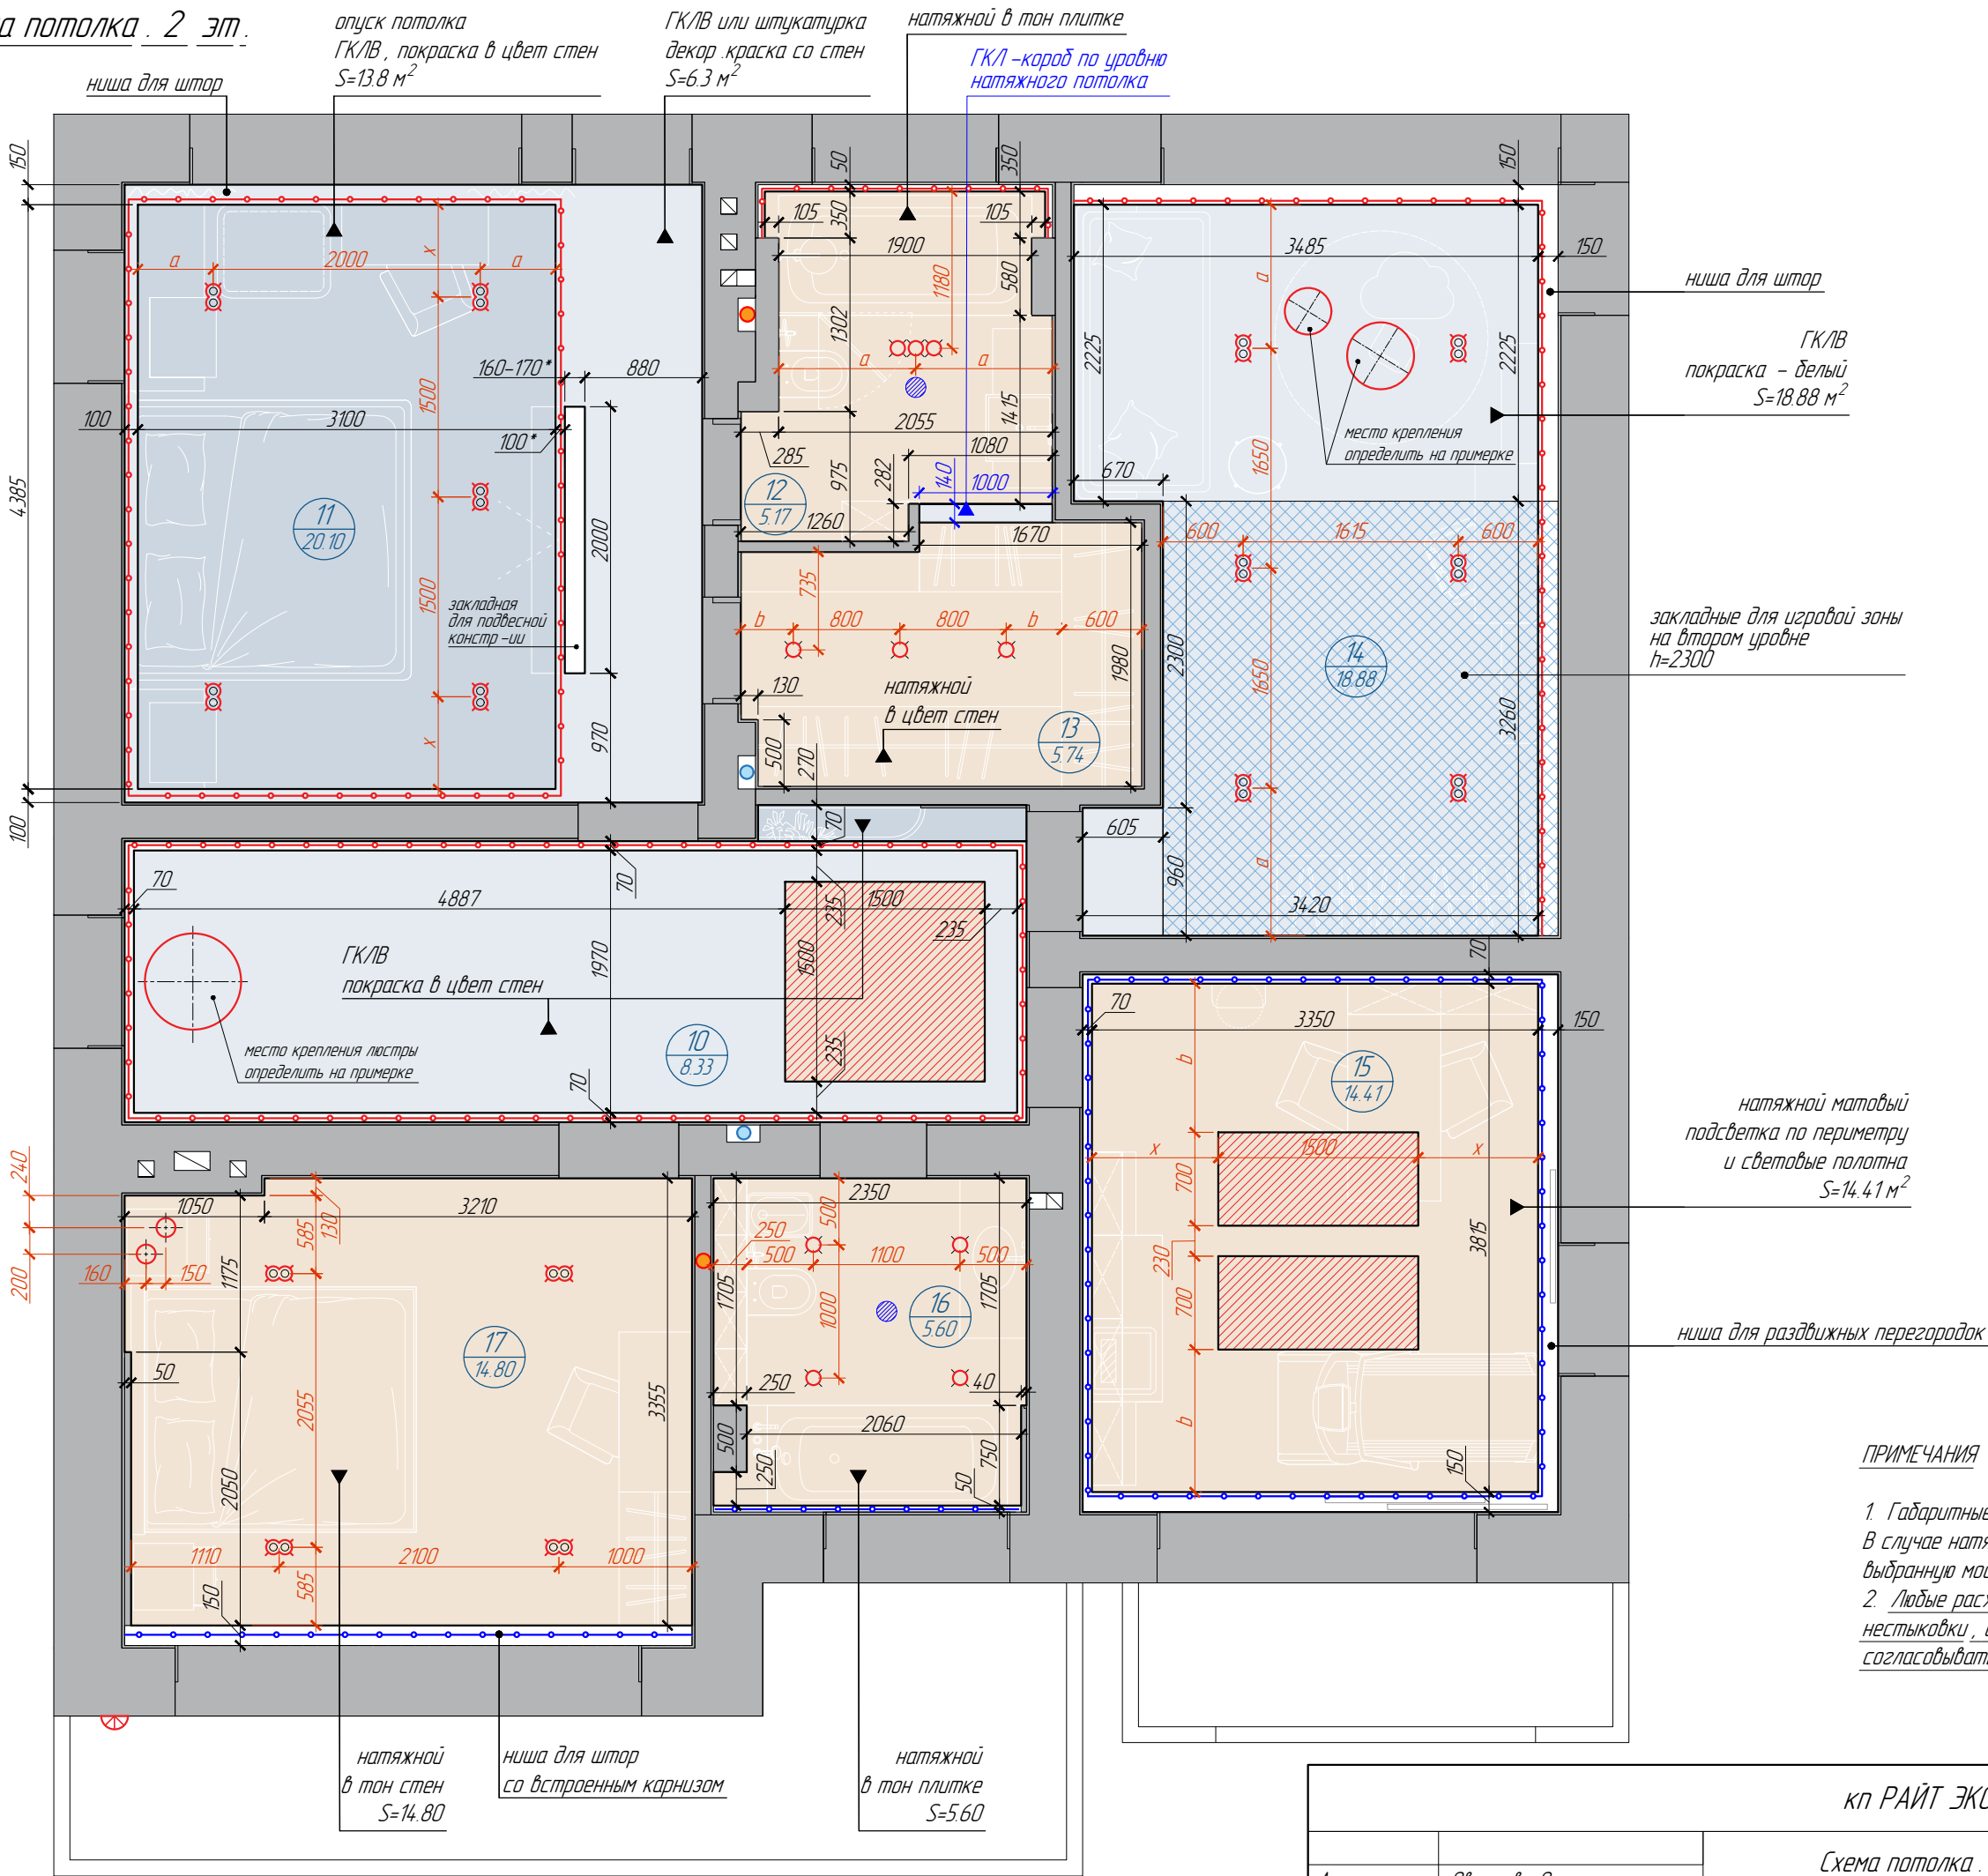

| УСЛОВНЫЕ ОБОЗНАЧЕНИЯ |                                 |
|----------------------|---------------------------------|
|                      | электровентилятор               |
|                      | люстра/подвесной св-ник         |
|                      | потолочный накладной светильник |
|                      | потолочный встраиваемый св-ник  |
|                      | потолочный встраиваемый св-ник  |
|                      | трековый светильник             |
|                      | led подсветка                   |
|                      | световой потолок                |

| УСЛОВНЫЕ ОБОЗНАЧЕНИЯ |                                    |
|----------------------|------------------------------------|
|                      | стены и перегородки из керамоблока |
|                      | стояк канализации                  |
|                      | стояк ливневой канализации         |
|                      | потолок ГКЛ                        |
|                      | натяжной потолок                   |

ПРИМЕЧАНИЯ

- Габаритные размеры ниш указаны по выступающим элементам. В случае натяжных потолков - данный размер корректируется под выбранную модель профиля
- Любые расхождения проектных размеров с фактическими, нестыковки, изменение конструктивных решений и т.п., согласовывать с автором проекта в рамках АН