

Дизайн-проект квартиры
ЖК LIFE—Кутузовский
дизайнер Ларенкова Елена




Ведомость рабочих чертежей

Ведомость рабочих чертежей		
Лист	Наименование	Примечание
01	Титульный лист	
02	Ведомость рабочих чертежей	
03	Обмерный план	
04	План расстановки мебели	
05	План демонтируемых конструкций	
06	План монтируемых конструкций	
06.1	План монтируемых конструкций. Виды 1,2	
07	План напольных покрытий	
08	План потолков с указанием уровня и материала отделки	
08.1	Этапы монтажа трековой системы Infinity Центрсвет	
09	План размещения осветительных приборов с привязкой выпусков	
10	Спецификация осветительного оборудования	
11	План размещения розеток и электрооборудования	
12	Размещение выключателей с указанием групп включения светильников	
13	План привязки сантехнического оборудования	
14	План водоподведения и водоотведения	
15	План теплых полов	
16	План размещения внутренних блоков кондиционеров	
17	Схема заполнения дверных проемов	
18	Развертка стен кухни-гостиной	
19	Развертка стен прихожей-холла	
20	Развертка стен спальни 1	
21	Развертка стен спальни 2	
22	Развертка стен санузла 1	
23	Развертка стен санузла 1	
24	Габариты мебели. Прихожая-холл	
25	Габариты мебели. Кухня-гостиная	
26	Габариты мебели. Спальня 1	
27	Габариты мебели. Спальня 2	
28	Габариты мебели. Санузел 1,2	
29	Ведомость отделочных материалов	

					Дизайнер Ларенкова Елена			
					+7(926) 135–23–40			
					foxnn2000@yandex.ru			
Изм	Лист	докум	Подп	Дата				
Разраб.	Ларенкова Елена				Дизайн– проект интерьера квартиры 91,3м.кв	Стадия	Лист	Листов
Пров.						РП	02	
Т.контр.								
					Ведомость рабочих чертежей			
Н.контр.								
Утв.								


Обмерный план

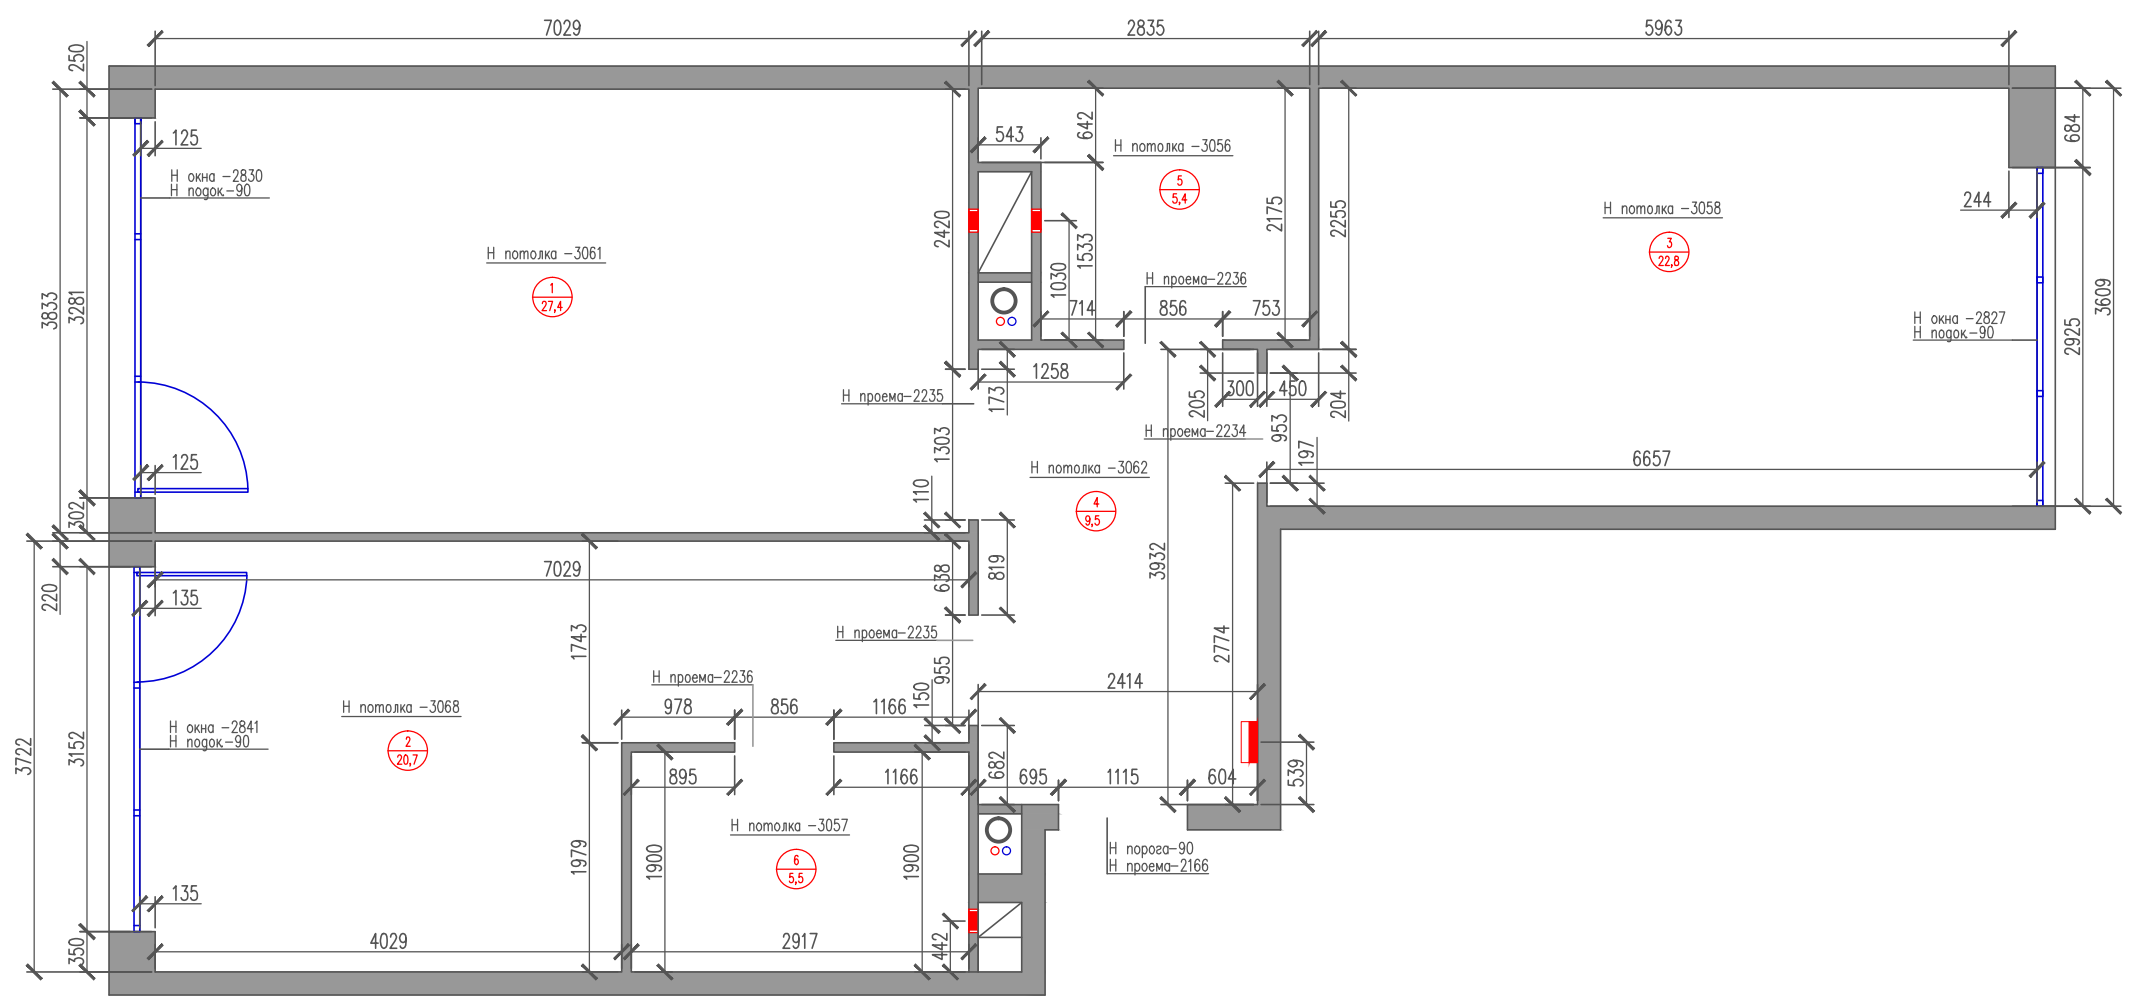

Экспликация помещений		
№пмщ	Наименование	Скв.м
1	Кухня-гостиная	27,4
2	Спальня 1	20,7
3	Спальня 2	22,8
4	Прихожая-холл	9,5
5	Санузел 1	5,4
6	Санузел 2	5,5
Общая площадь		91,3
Условные обозначения		
	существующие стены	
	сан. тех. короб	
	радиатор	
	трубы отопления	
	вентиляция	
	счетчик электр.ч.	
	предполагаемые короба	
	вент. канал	

					Дизайнер Ларенкова Елена			
					+7(926) 135–23–40			
					foxnn2000@yandex.ru			
Изм	Лист	докум	Подп	Дата	Дизайн– проект интерьера квартиры 91,3м.кв	Стадия	Лист	Листов
Разраб.	Ларенкова Елена					РП	03	
Пров.								
Т.контр.								
					Обмерный план			
Н.контр.								
Утв.								

План расстановки мебели

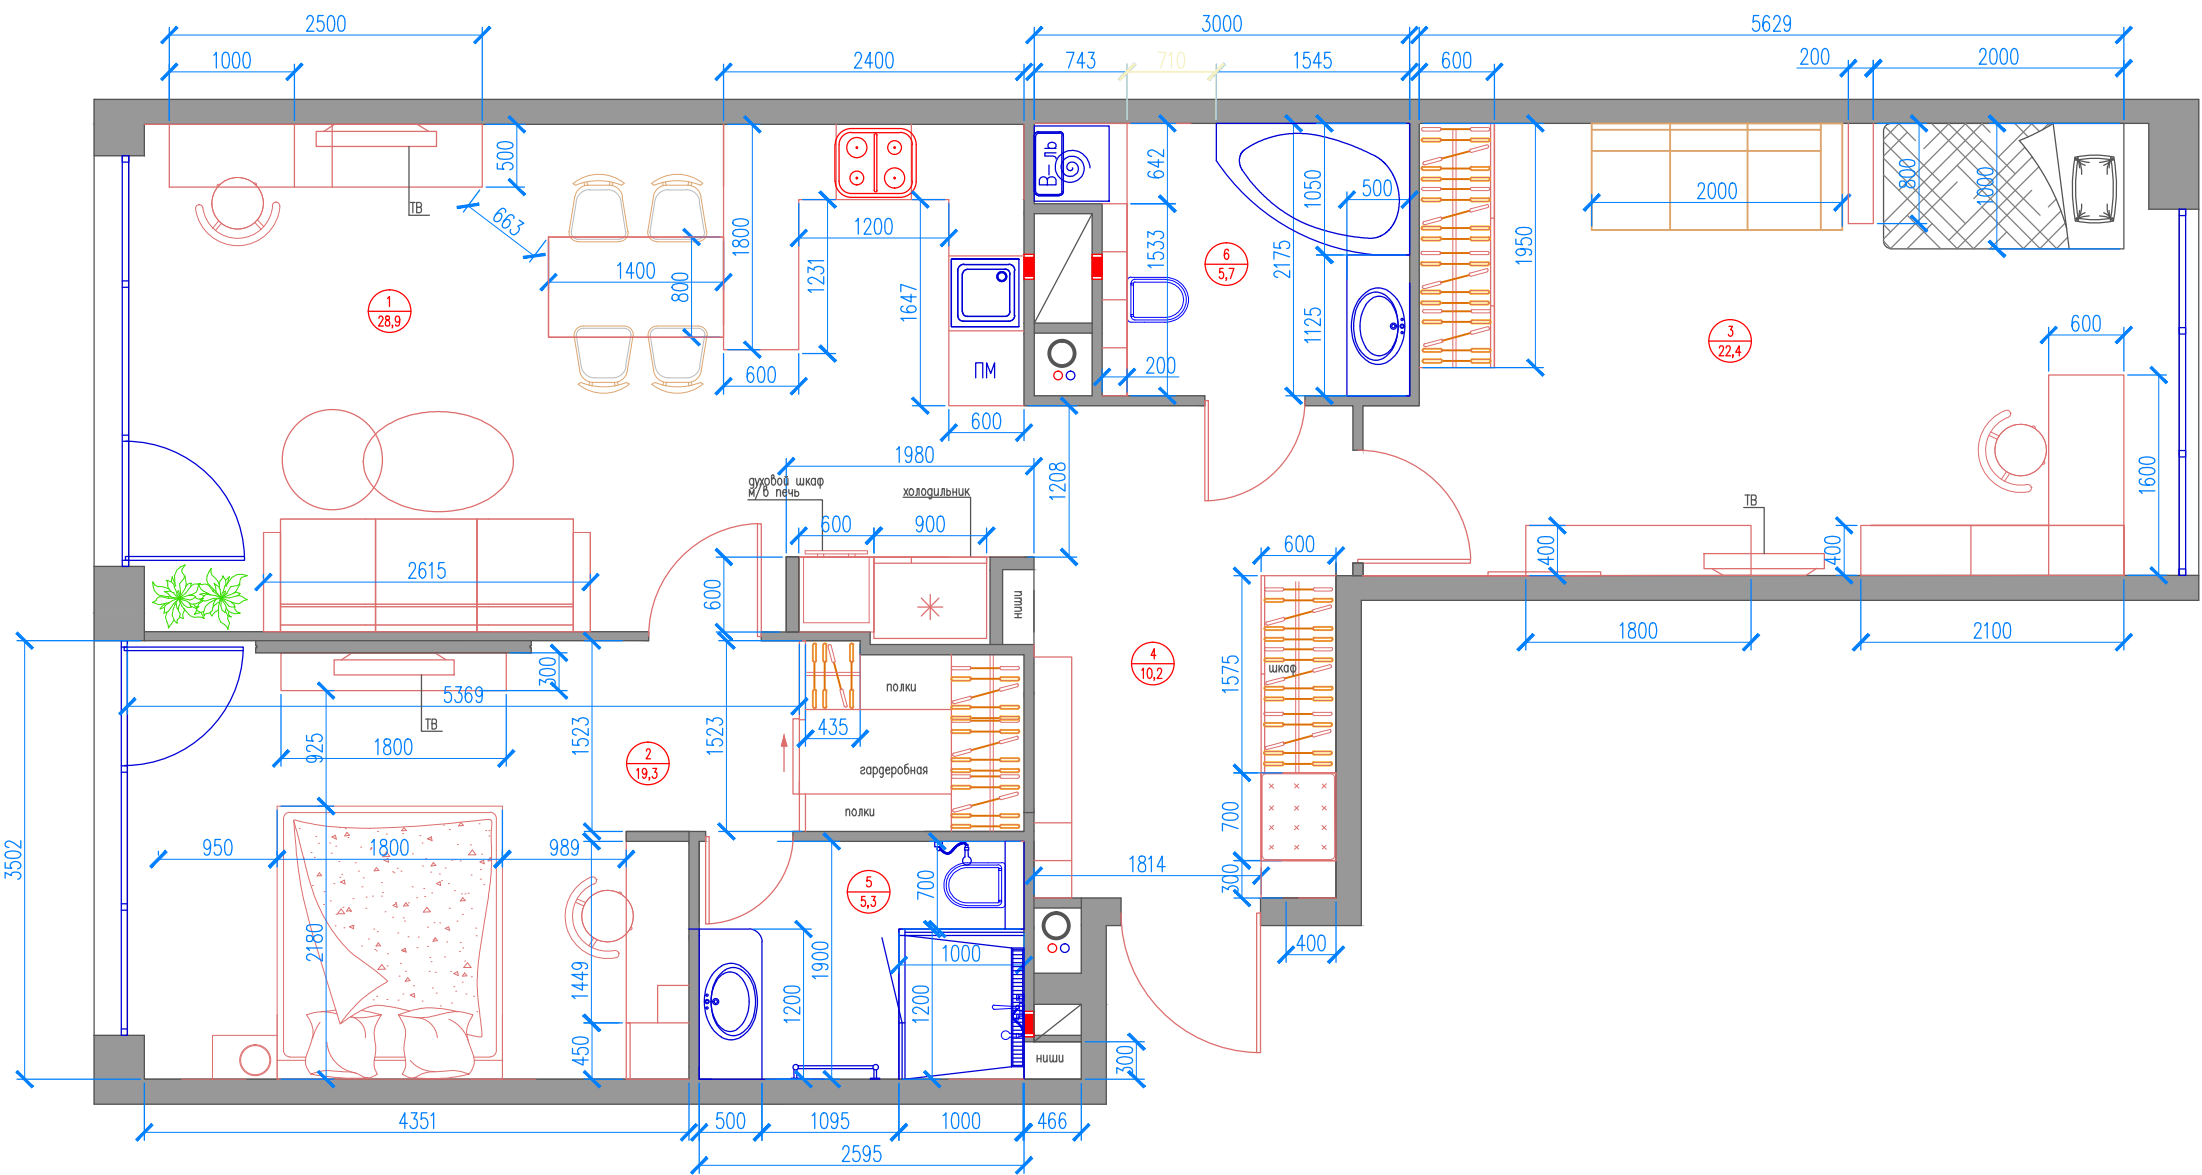

Экспликация помещений

№пмщ	Наименование	Скв. м
1	Кухня-гостиная	28,9
2	Спальня 1	19,3
3	Спальня 2	22,4
4	Прихожая-холл	10,2
5	Санузел 1	5,3
6	Санузел 2	5,7

Общая площадь 91,8

Условные обозначения


	существующие стены
○ ○ ○	сан. тех. короб
○○	радиатор трубы отопления
■	вентиляция
—	счетчик электр.ч.
▨	предполагаемые короба
▧	вент. канал

Перегородки

№поз.	Обозначение	Наименование	Кол-во
1	▨	Алюминиевый перегородочный блок из всп. пены	

Дизайнер Ларенкова Елена				
+7(926) 135-23-40				
foxnn2000@yandex.ru				
Изм.	Лист	докум.	Подп.	Дата
Разраб.	Ларенкова Елена			
Пров.				
Т.контр.				
Н.контр.				
Умв.				
Дизайн-проект интерьера квартиры 91,3м.кв			Стадия	Лист
			РП	04
План расстановки мебели				


План демонтируемых конструкций

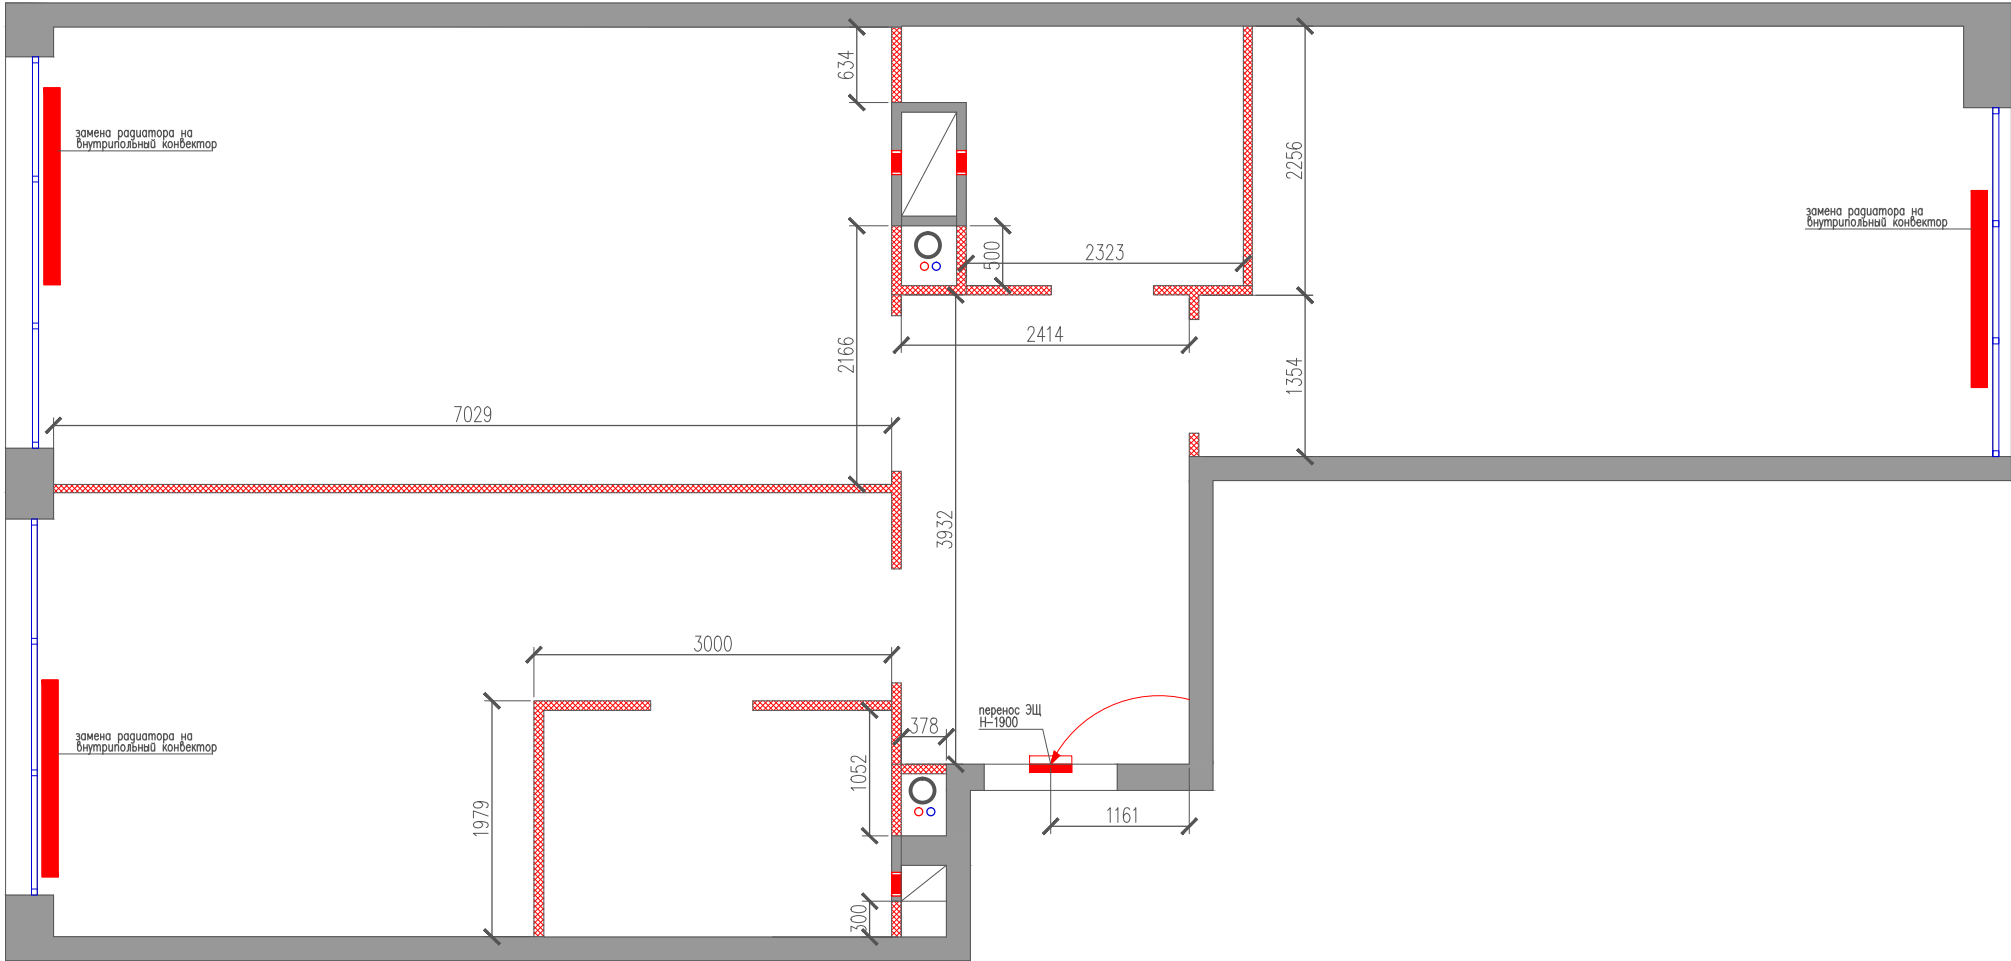

Экспликация помещений		
№пмщ	Наименование	Скв. м
1	Кухня-гостиная	28,9
2	Спальня 1	19,3
3	Спальня 2	22,4
4	Прихожая-холл	10,2
5	Санузел 1	5,3
6	Санузел 2	5,7
Общая площадь		91,8
Условные обозначения		
	существующие стены	
○ ○ ○	сан. тех. короб	
○○	радиатор	
—	трубы отопления	
—	вентиляция	
—	счетчик электрич.	
▨	предполагаемые короба	
▧	вент. канал	

					Дизайнер Ларенкова Елена			
					+7(926) 135–23–40			
					foxnn2000@yandex.ru			
Изм	Лист	докум	Подп	Дата	Дизайн– проект интерьера квартиры 91,3м.кв	Стадия	Лист	Листов
Разраб.	Ларенкова Елена					РП	05	
Пров.								
Т.контр.								
					План демонтируемых конструкций			
Н.контр.								
Умв.								

План монтируемых конструкций

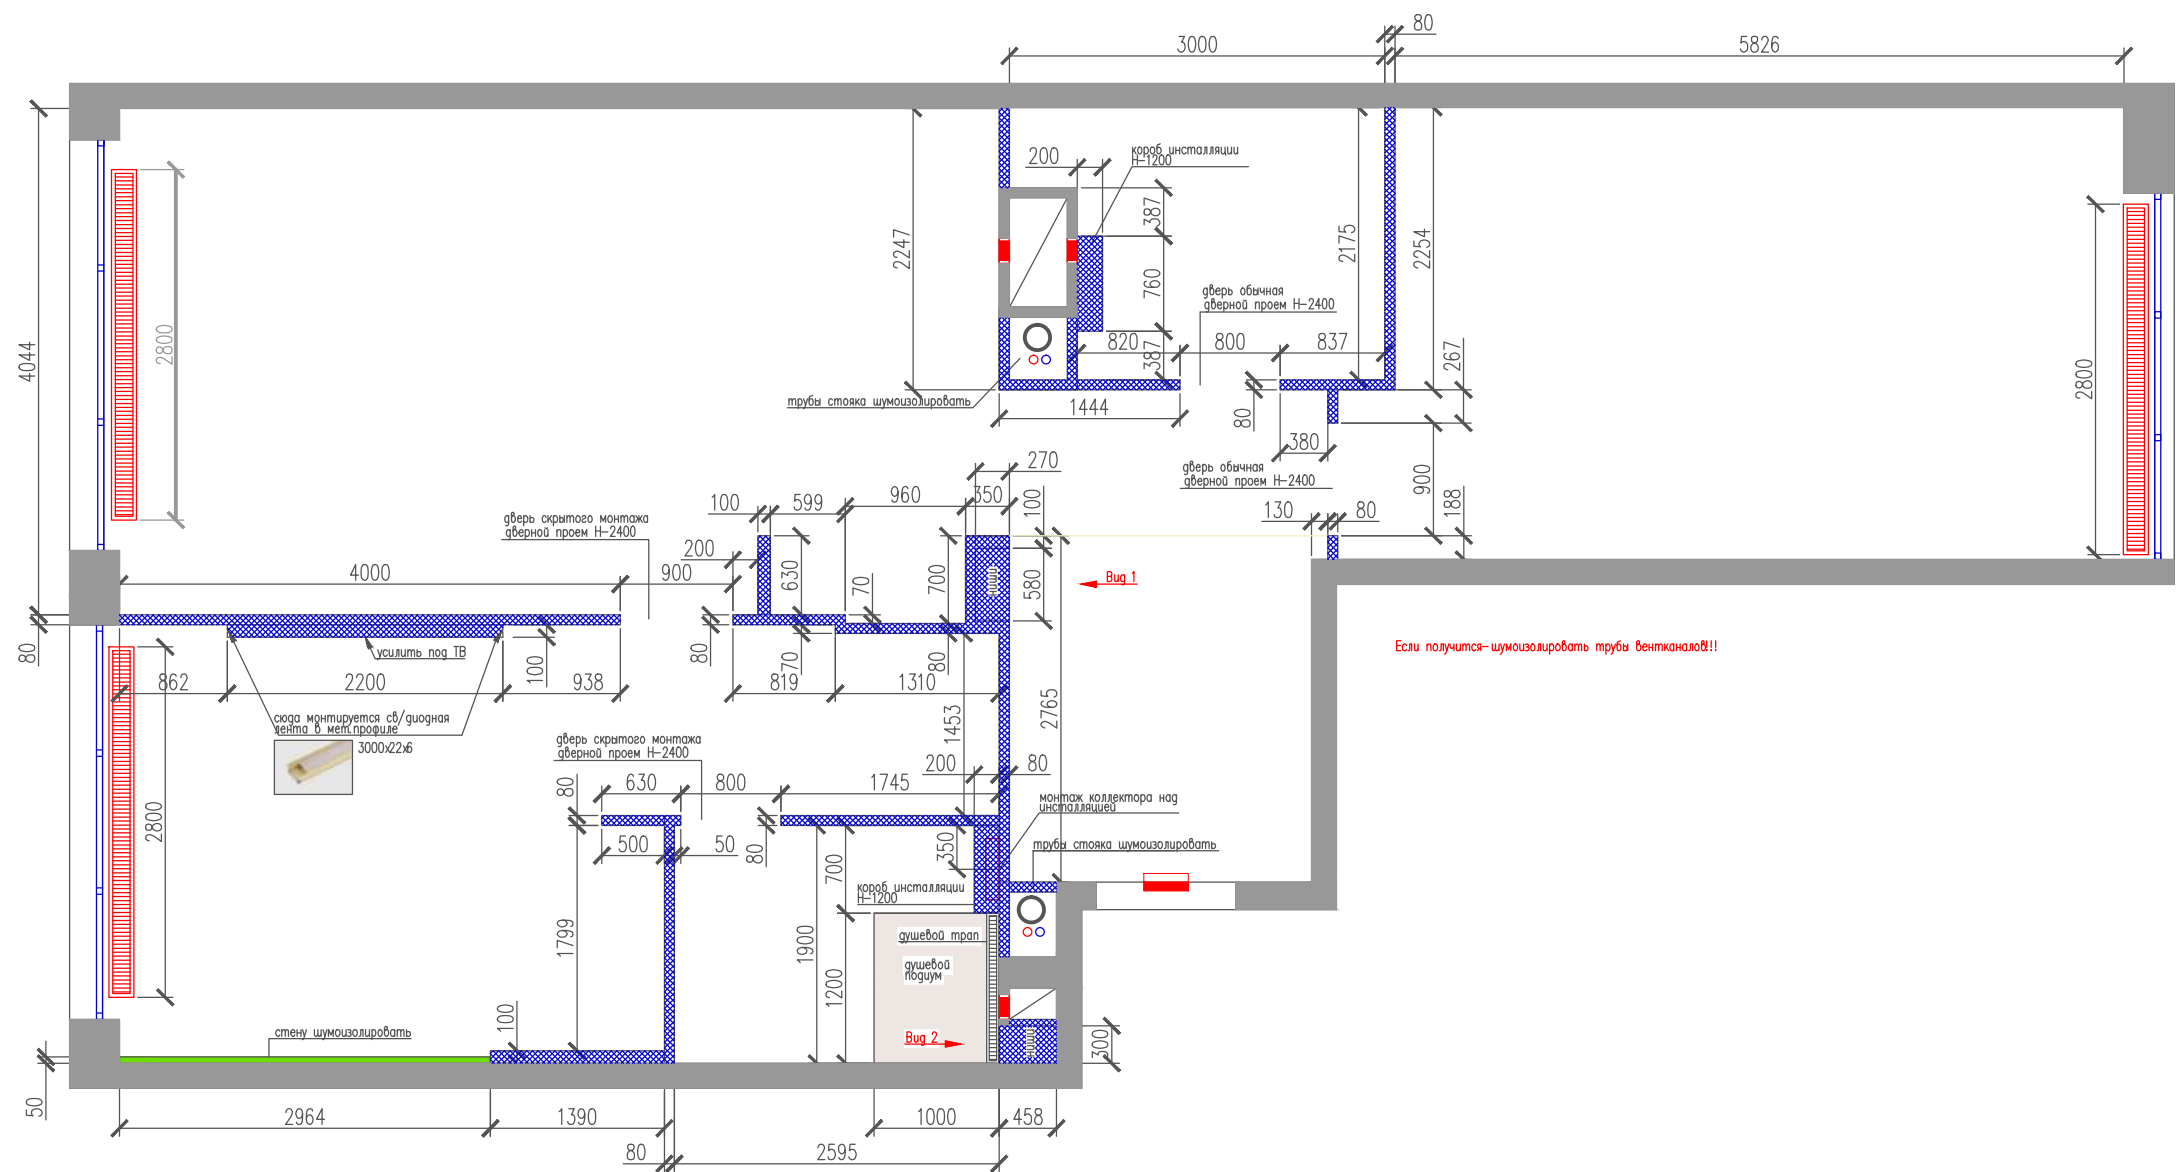

Экспликация помещений

№пмщ	Наименование	Скв. м
1	Кухня-гостиная	28,9
2	Спальня 1	19,3
3	Спальня 2	22,4
4	Прихожая-холл	10,2
5	Санузел 1	5,3
6	Санузел 2	5,7

Общая площадь 91,8

Условные обозначения

	существующие стены
○ ○ ○	сан. тех. короб
○ ○	радиатор
—	трубы отопления
—	вентиляция
—	счетчик электр.ч.
▨	предполагаемые короба
▨	вент. канал

Перегородки

№поз.	Обозначение	Наименование	Кол-во
1	▨	вентиляционный канал	1

Дизайнер Ларенкова Елена
+7(926) 135-23-40
foxnn2000@yandex.ru

Изм.	Лист	докум.	Подп.	Дата
Разраб.	Ларенкова Елена			
Пров.				
Т.контр.				
Н.контр.				
Умб.				



Дизайн-проект интерьера
квартиры 91,3м.кв

Стадия	Лист	Листов
РП	06	

План монтируемых конструкций

План монтируемых конструкций

Виды 1,2

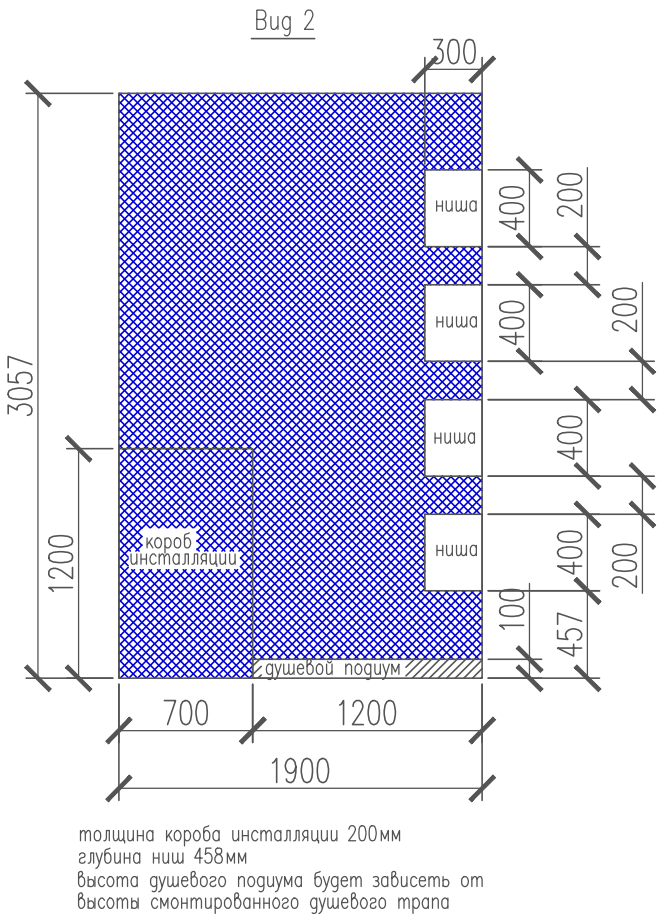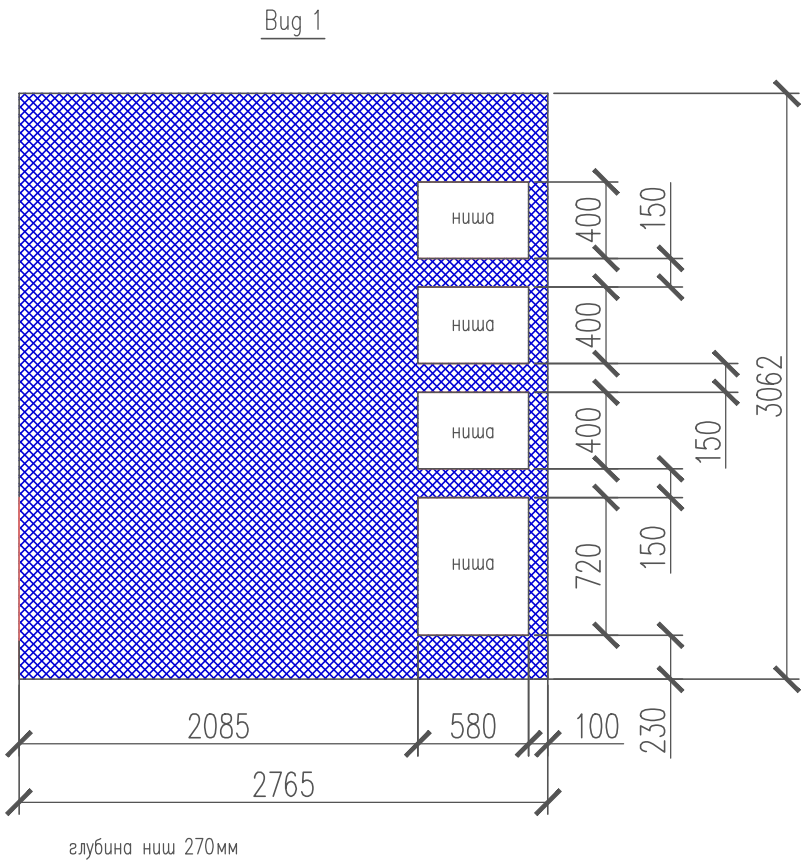

Экспликация помещений

№пмщ	Наименование	Скв.м
1	Кухня-гостиная	28,9
2	Спальня 1	19,3
3	Спальня 2	22,4
4	Прихожая-холл	10,2
5	Санузел 1	5,3
6	Санузел 2	5,7

Общая площадь 91,8

Условные обозначения

	существующие стены
	сан. тех. короб
	радиатор
	трубы отопления
	вентиляция
	счетчик электр.ч.
	предполагаемые короба
	вент. канал

Перегородки

№поз.	Обозначение	Наименование	Кол-во
1		высотостойкий перегородочный блок на всю высоту помещения	

					Дизайнер Ларенкова Елена			
					+7(926) 135–23–40			
					foxnn2000@yandex.ru			
Изм	Лист	докум	Подп	Дата	Дизайн– проект интерьера квартиры 91,3м.кв	Стадия	Лист	Листов
Разраб.	Ларенкова Елена					РП	06.1	
Пров.								
Т.контр.								
					План монтируемых конструкций. Виды 1,2			
Н.контр.								
Умв.								

План напольных покрытий



*** Переход между керамогранитом и паркетной доской выполнить с помощью стыковочного профиля (цвет согласовать с заказчиком!!)
*** Отметки верха напольного покрытия во всей квартире должны быть выполнены в одном уровне (без перепадов)
*** Укладка паркетной доски хаотичная со сдвигом 30%
*** Стыки различных напольных покрытий выполнять со смещением в сторону открывания двери, с выравниванием по линии полотна

Полы			
№поз.	Обозн.	Наименование	Кол-во
1		паркетная доска Galathea американский орех селект лак Select (5650р/м2) или Polarwood Дуб Сирис Премиум масло однополосный Oak Premium Select (4765р/м2) или Hago Series 4000(5G) 529976 американский орех однополосный (22930р/м2)	66,6м.кв+5%запас
2		керамогранит 600x600 Supertova Stoun Atlas Concord толщина 10мм	12,4м.кв+5%запас
3		керамогранит 1200x600 Rex Reyes de Rex Choco Glossy Rett толщина 10мм	5м.кв+5%запас
		керамогранит 600x600 Ризальто Керама Марацци SG634202R толщина 11мм	5,8м.кв+5%запас
4		начало раскладки	

Экспликация помещений

№пмщ.	Наименование	Скв. м
1	Кухня-гостиная	28,9
2	Спальня 1	19,3
3	Спальня 2	22,4
4	Прихожая-холл	10,2
5	Санузел 1	5,3
6	Санузел 2	5,7

Общая площадь 91,8

Условные обозначения

	существующие стены
○ ○ ○	сан. тех. короб
○ ○	радиатор
—	трубы отопления
□	вентиляция
—	счетчик электр.ч.
▨	предполагаемые короба
▧	вент. канал

Перегородки

№поз.	Обозначение	Наименование	Кол-во
1		высотостойкий газобетонный блок на всю высоту помещения	

Дизайнер Ларенкова Елена
+7(926) 135-23-40
foxnn2000@yandex.ru


Изм.	Лист	докум.	Подп.	Дата
Разраб.	Ларенкова Елена			
Пров.				
Т.контр.				
Н.контр.				
Умв.				

Дизайн-проект интерьера
квартиры 91,3м.кв

Стадия	Лист	Листов
РП	07	


План напольных покрытий

План потолков с указанием уровня и материала отделки

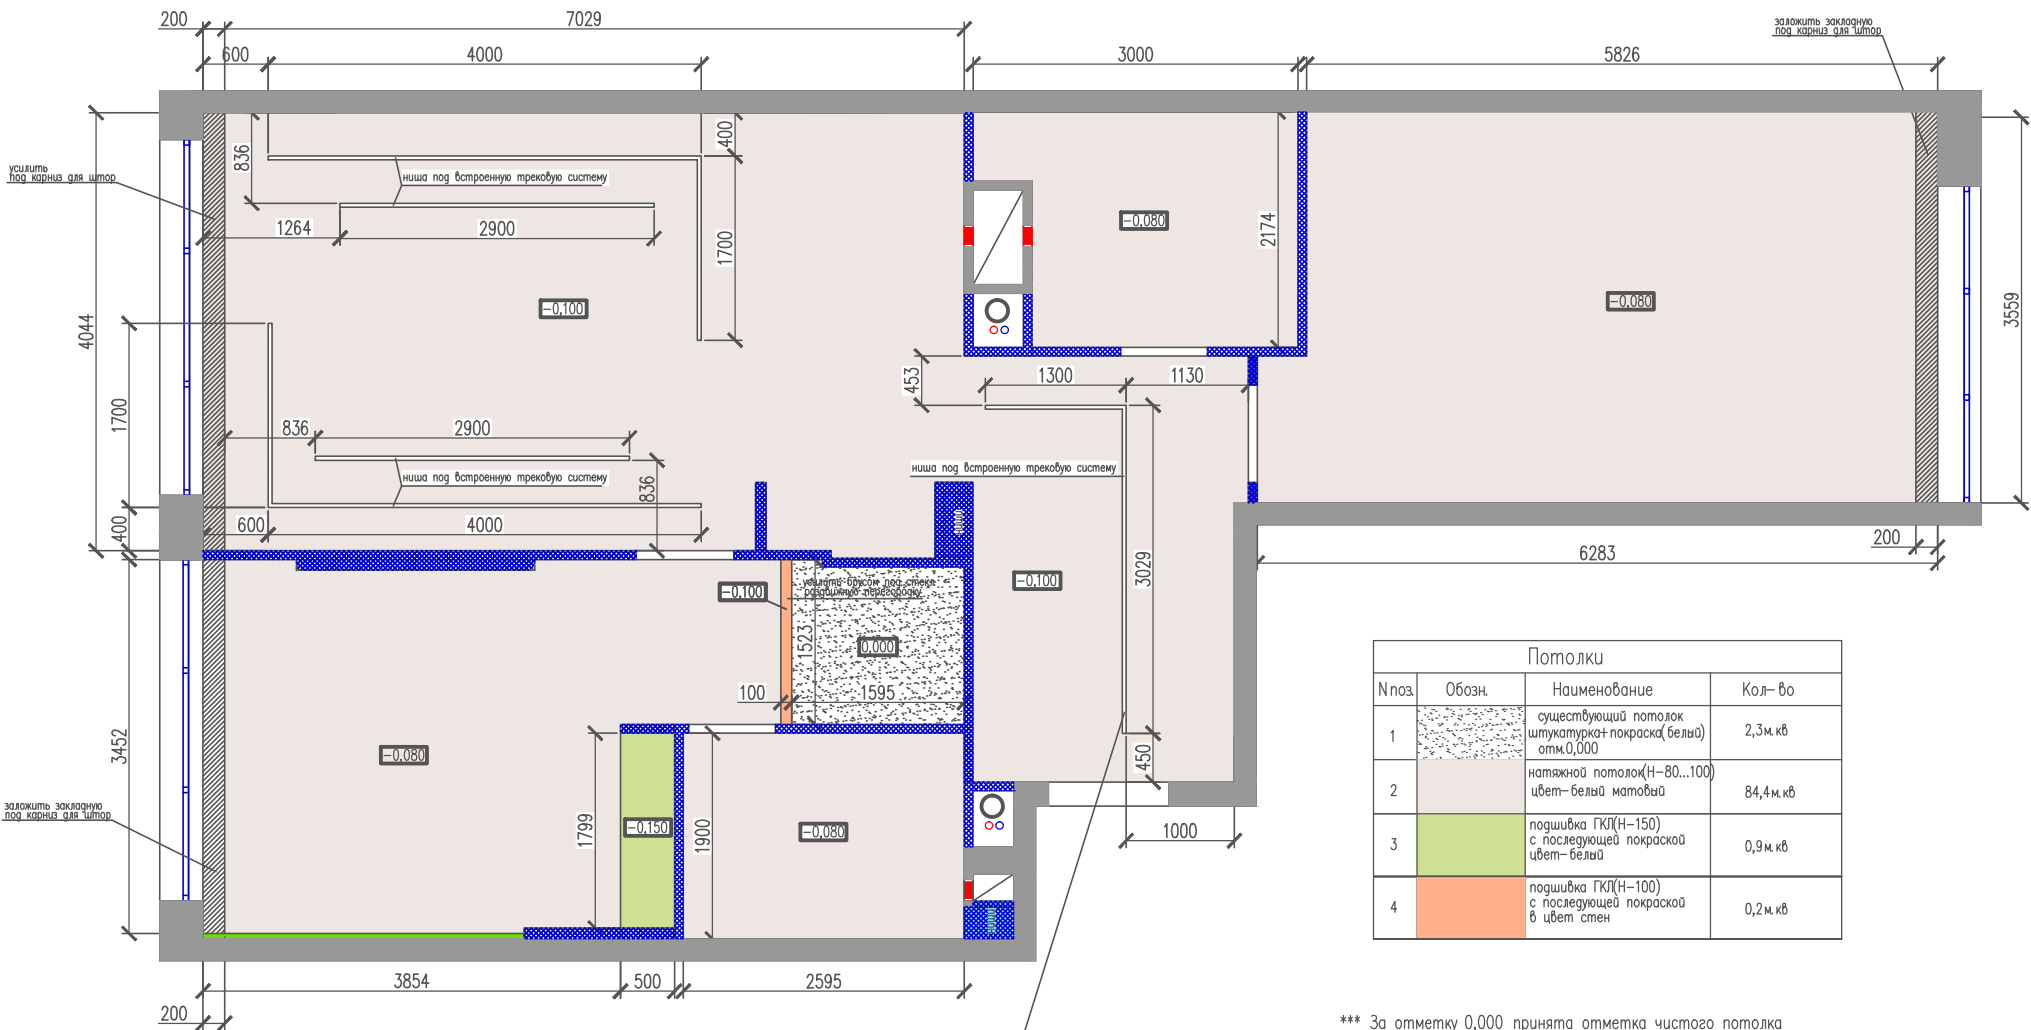

Потолки			
№поз.	Обозн.	Наименование	Кол-во
1		существующий потолок штукатурка+покраска(белый) отм.0,000	2,3м.кв
2		натяжной потолок(Н-80...100) цвет-белый матовый	84,4м.кв
3		подшивка ГКЛ(Н-150) с последующей покраской цвет-белый	0,9м.кв
4		подшивка ГКЛ(Н-100) с последующей покраской в цвет стен	0,2м.кв

*** За отметку 0,000 принята отметка чистого потолка
*** Трансформаторы светодиодной ленты монтируются в боксе для групп автоматов или в ближайших шкафах
*** Ширина ниши под трековую систему зависит от размера трека. В проекте вставлена трековая система INFINITY ЦЕНТРСВЕТ для натяжных потолков

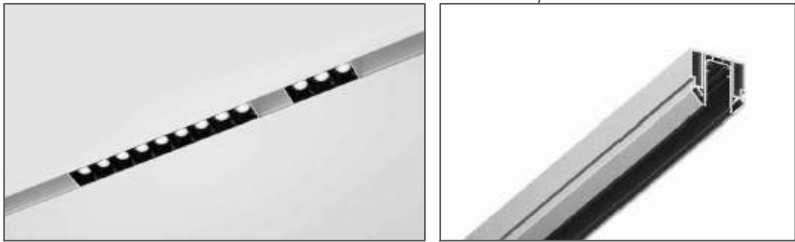

*** Этапы монтажа встроенной трековой системы см. на Инструкции по монтажу (прилагается к проекту в конце альбома)

Экспликация помещений

№пмщ.	Наименование	Скв. м
1	Кухня-гостиная	28,9
2	Спальня 1	19,3
3	Спальня 2	22,4
4	Прихожая-холл	10,2
5	Санузел 1	5,3
6	Санузел 2	5,7

Общая площадь 91,8

Условные обозначения

	существующие стены
○ ○ ○	сан. тех. короб
○ ○	радиатор
—	трубы отопления
—	вентиляция
—	счетчик электр.ч.
	предполагаемые короба
▤	вент. канал

Перегородки

№поз.	Обозначение	Наименование	Кол-во
1		массивный газобетонный блок на всю высоту помещения	

Дизайнер Ларенкова Елена
+7(926) 135-23-40
foxnn2000@yandex.ru


Изм.	Лист	докум.	Подп.	Дата
Разраб.	Ларенкова Елена			
Пров.				
Т.контр.				
Н.контр.				
Умв.				

Дизайн-проект интерьера
квартиры 91,3м.кв

Стадия	Лист	Листов
РП	08	

План потолков с указанием уровня и материала отделки

План размещения осветительных приборов с привязкой выпусков

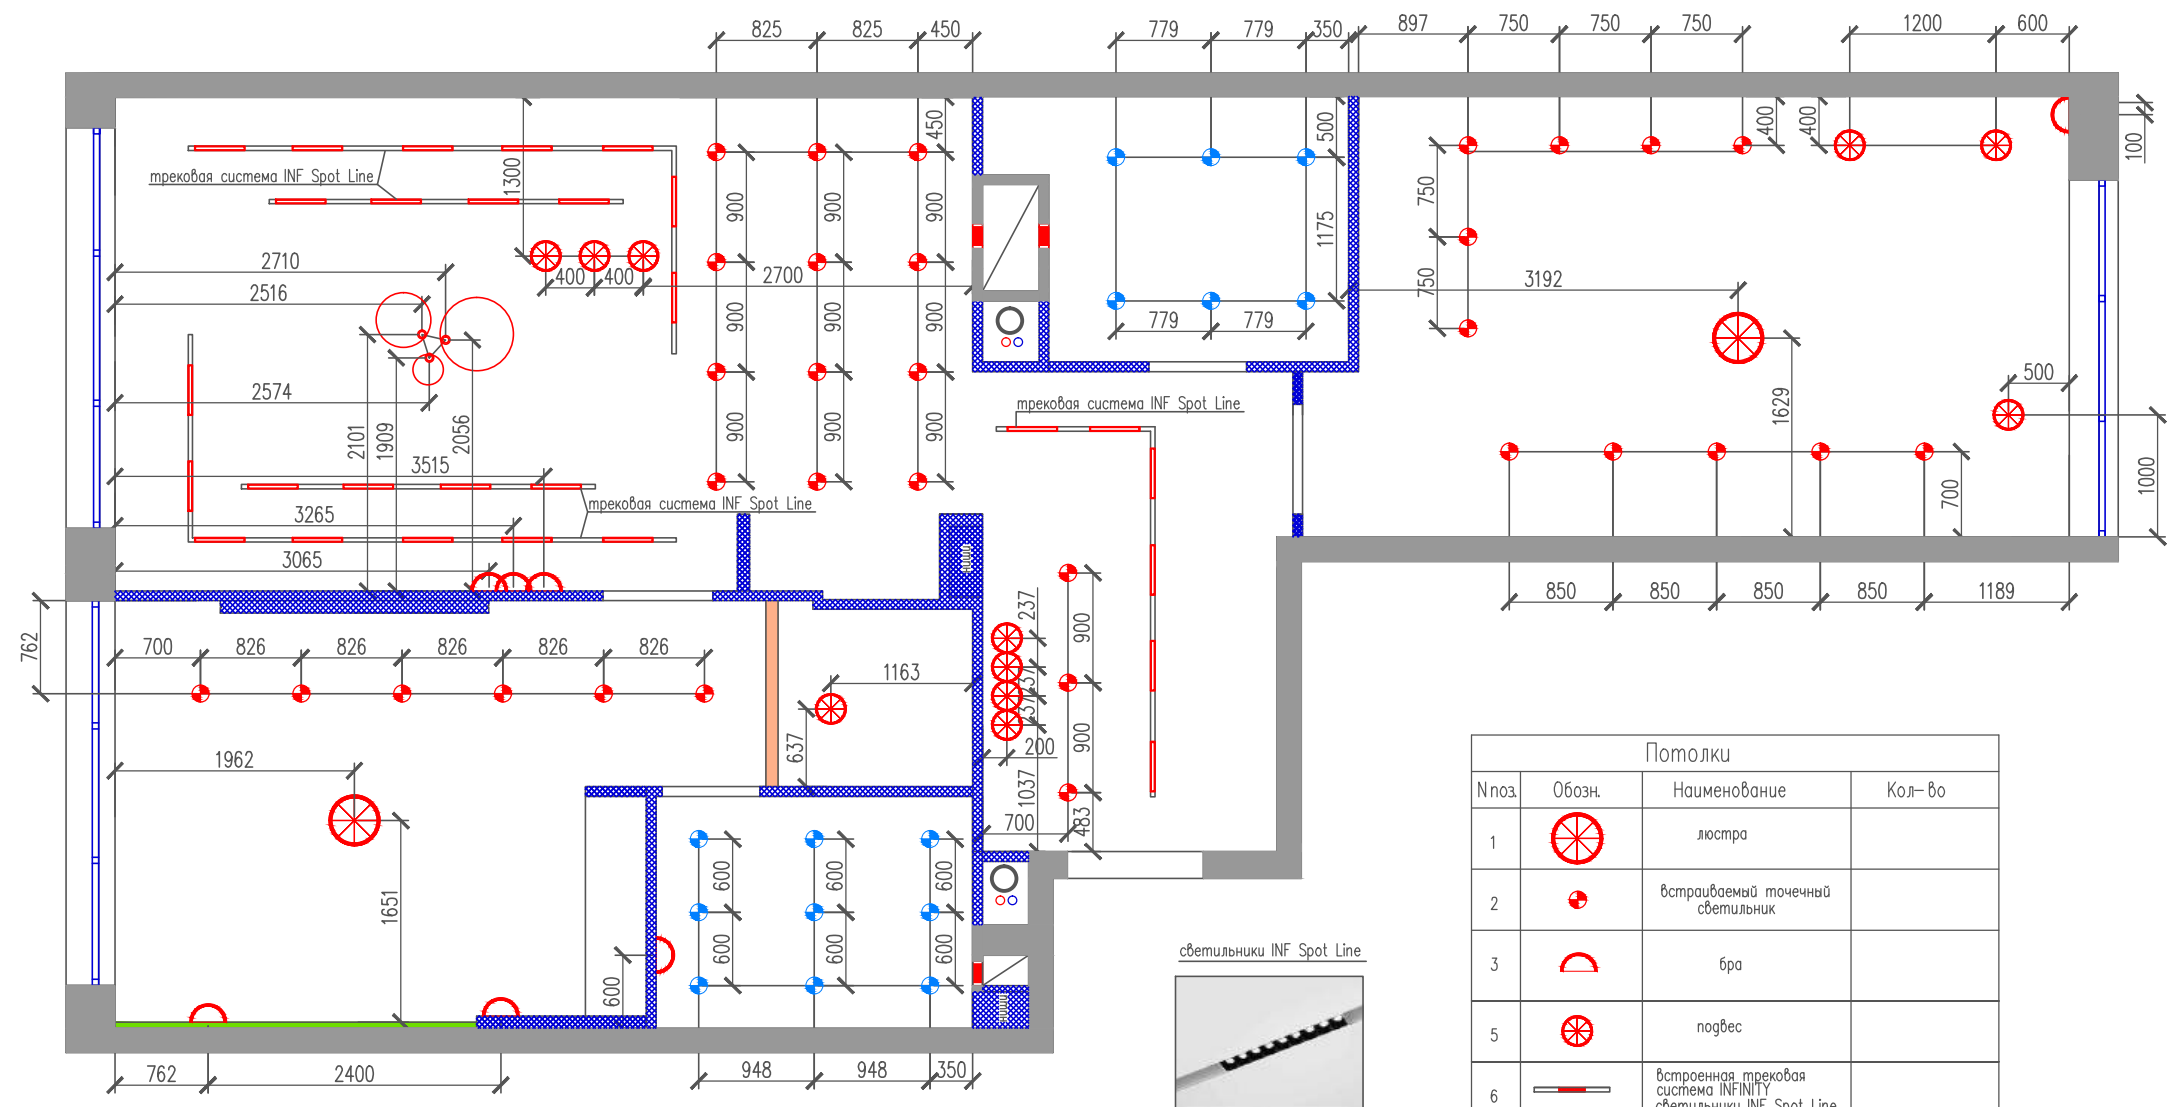

*** Все выпуски, указанные на чертеже, оставить длиной не менее 1м

Экспликация помещений

№пмщ	Наименование	Скв. м
1	Кухня-гостиная	28,9
2	Спальня 1	19,3
3	Спальня 2	22,4
4	Прихожая-холл	10,2
5	Санузел 1	5,3
6	Санузел 2	5,7

Общая площадь 91,8

Условные обозначения

	существующие стены
○ ○ ○	сан. тех. короб
○ ○	радиатор
—	трубы отопления
—	вентиляция
—	счетчик электр.
▨	предполагаемые короба
▨	вент. канал


Перегородки

№поз.	Обозначение	Наименование	Кол-во
1	▨	влагостойкий перегородочный блок на всю высоту помещения	

Потолки			
№поз.	Обозн.	Наименование	Кол-во
1	⊗	люстра	
2	●	встраиваемый точечный светильник	
3	⌒	бра	
5	⊗	подвес	
6	—	встроенная трековая система INFINITY светильники INF Spot Line	
7	⊕	встраиваемый точечный светильник влагостойкий	

Дизайнер Ларенкова Елена				
+7(926) 135-23-40				
foxnn2000@yandex.ru				
Изм.	Лист	докум	Подп.	Дата
Разраб.	Ларенкова Елена			
Пров.				
Т.контр.				
Н.контр.				
Умв.				
Дизайн-проект интерьера			Стадия	Лист
квартиры 91,3м.кв			РП	09
План размещения осветительных приборов с привязкой				
выпусков				

Спецификация осветительного оборудования

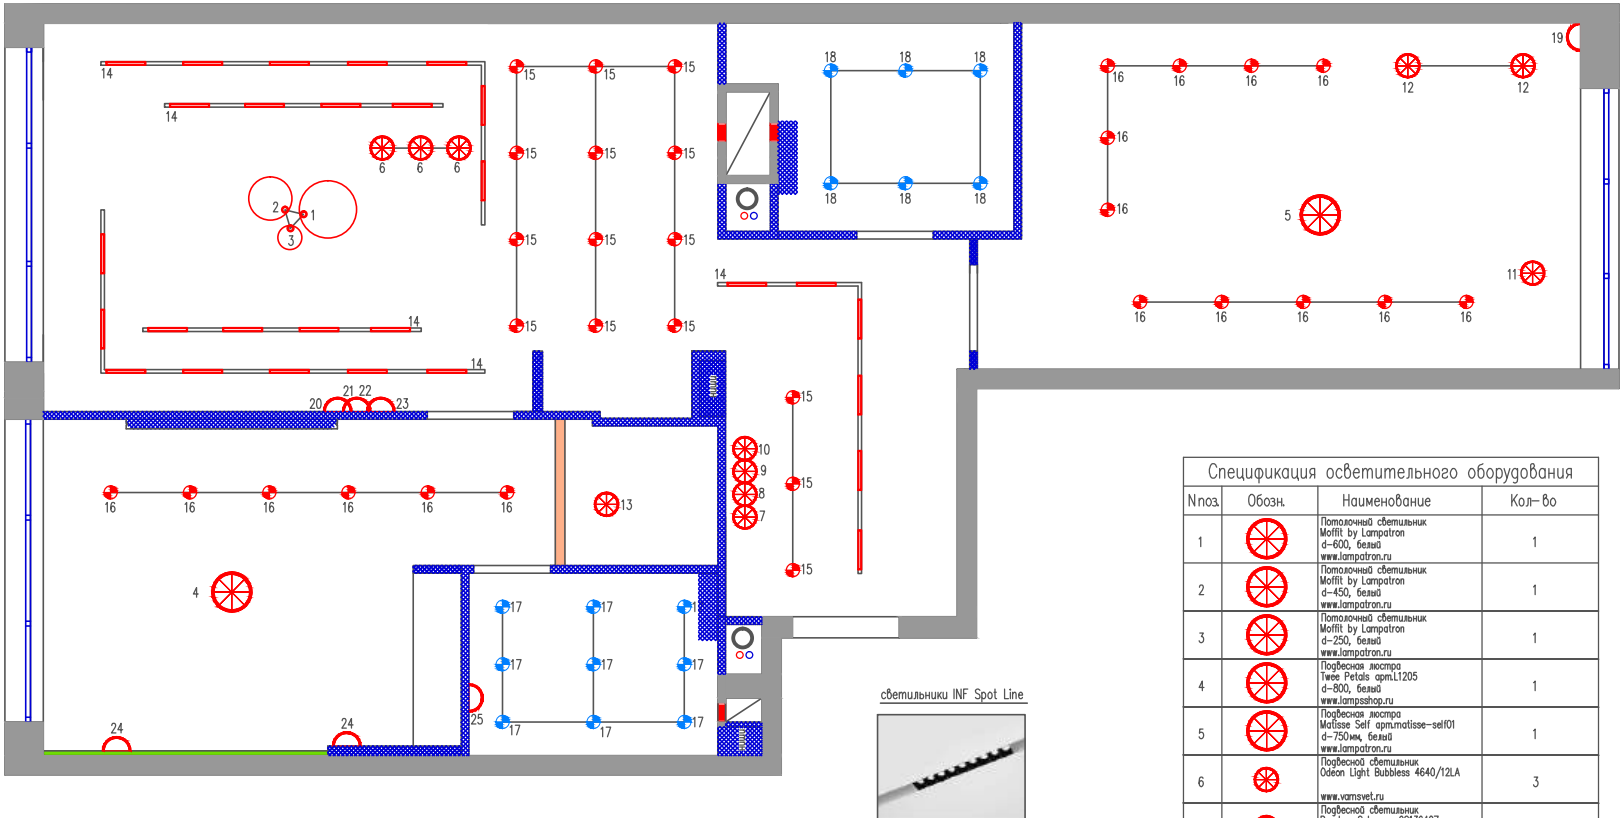

*** Тип, способ установки, назначение и категории светильников уточнить при выборе у поставщика



Спецификация осветительного оборудования			
№поз	Обозн.	Наименование	Кол-во
1		Потолочный светильник Mofitt by Lamptron d=600, белый www.lampatron.ru	1
2		Потолочный светильник Mofitt by Lamptron d=450, белый www.lampatron.ru	1
3		Потолочный светильник Mofitt by Lamptron d=250, белый www.lampatron.ru	1
4		Погребная люстра Three Petals арт.L1205 d=800, белый www.lampshor.ru	1
5		Погребная люстра Mofisse Self арт.mofisse-self01 d=750мм, белый www.lampatron.ru	1
6		Погребная люстра Odson Light Bubble 4640/12LA www.vamsvet.ru	3
7		Погребная люстра Random Solo арт.25136427 d=280мм, прозрачное золото www.zshades.ru	1
8		Погребная люстра Random Solo арт.25136401 d=180мм, хромированный www.zshades.ru	1
9		Погребная люстра Random Solo арт.25136398 d=180мм, прозрачная www.zshades.ru	1
10		Погребная люстра Random Solo арт.25136375 d=120мм, белый www.zshades.ru	1
11		Погребная люстра Cloud Grade арт.L1536g для точечного света, золото www.lampshor.ru	1
12		Потолочный светильник Mofisse C Self d=255мм, белый www.playlighting.ru	2
13		Потолочный светильник Alakon B арт.PL3063 d=250, белый www.lampshor.ru	1

Спецификация осветительного оборудования			
№поз	Обозн.	Наименование	Кол-во
14		Встроенная трековая система INFINITY светильники INF Spot Line	сб-к L205мм-28шт/трек- 21,7п/м, соединитель-3шт
15		Встраиваемый светильник Lightstar Cardano 214010 белый www.vamsvet.ru	15
16		Встраиваемый светильник Montre Basico Set C0045 белый www.vamsvet.ru	17
17		Встраиваемый светильник Roudron Premium 99741 золотой www.vamsvet.ru	9(3компл*3шт)
18		Встраиваемый светильник Lightstar Leddy 212185 белый www.vamsvet.ru	6
19		Бра Maykon Technical Stem C035ML-L3M3K золотой матовый www.vamsvet.ru	1
20		Бра Lift by Lamptron d=200, белый-латунь www.lampatron.ru	1
21		Бра Lift by Lamptron d=400, белый-латунь www.lampatron.ru	1
22		Бра Lift by Lamptron d=250, белый-латунь www.lampatron.ru	1
23		Бра Lift by Lamptron d=300, белый-латунь www.lampatron.ru	1
24		Бра Three Petals арт.B4243b белый www.lampshor.ru	2
25		Погребная люстра Azzardo Davinci 48 AZ2650 золотой www.vamsvet.ru	1

Экспликация помещений

№пмщ	Наименование	Скв.м
1	Кухня-гостиная	28,9
2	Спальня 1	19,3
3	Спальня 2	22,4
4	Прихожая-холл	10,2
5	Санузел 1	5,3
6	Санузел 2	5,7

Общая площадь 91,8

Условные обозначения

	существующие стены
	сан.тех.короб
	радиатор
	трубы отопления
	вентиляция
	счетчик электр.
	предполагаемые коробки
	вент.канал

Перегородки

№поз	Обозначение	Наименование	Кол-во
1		Алюминиевый перегородочный блок на всю высоту помещения	1

Дизайнер Ларенкова Елена
+7(926) 135-23-40
foxnn2000@yandex.ru


Изм.	Лист	докум	Подп	Дата
Разраб.	Ларенкова Елена			
Пров.				
Т.контр.				
Н.контр.				
Умв.				

Дизайн-проект интерьера
квартиры 91,3м.кв

Стадия	Лист	Листов
РП	10	

Спецификация осветительного оборудования

План размещения розеток и электрооборудования

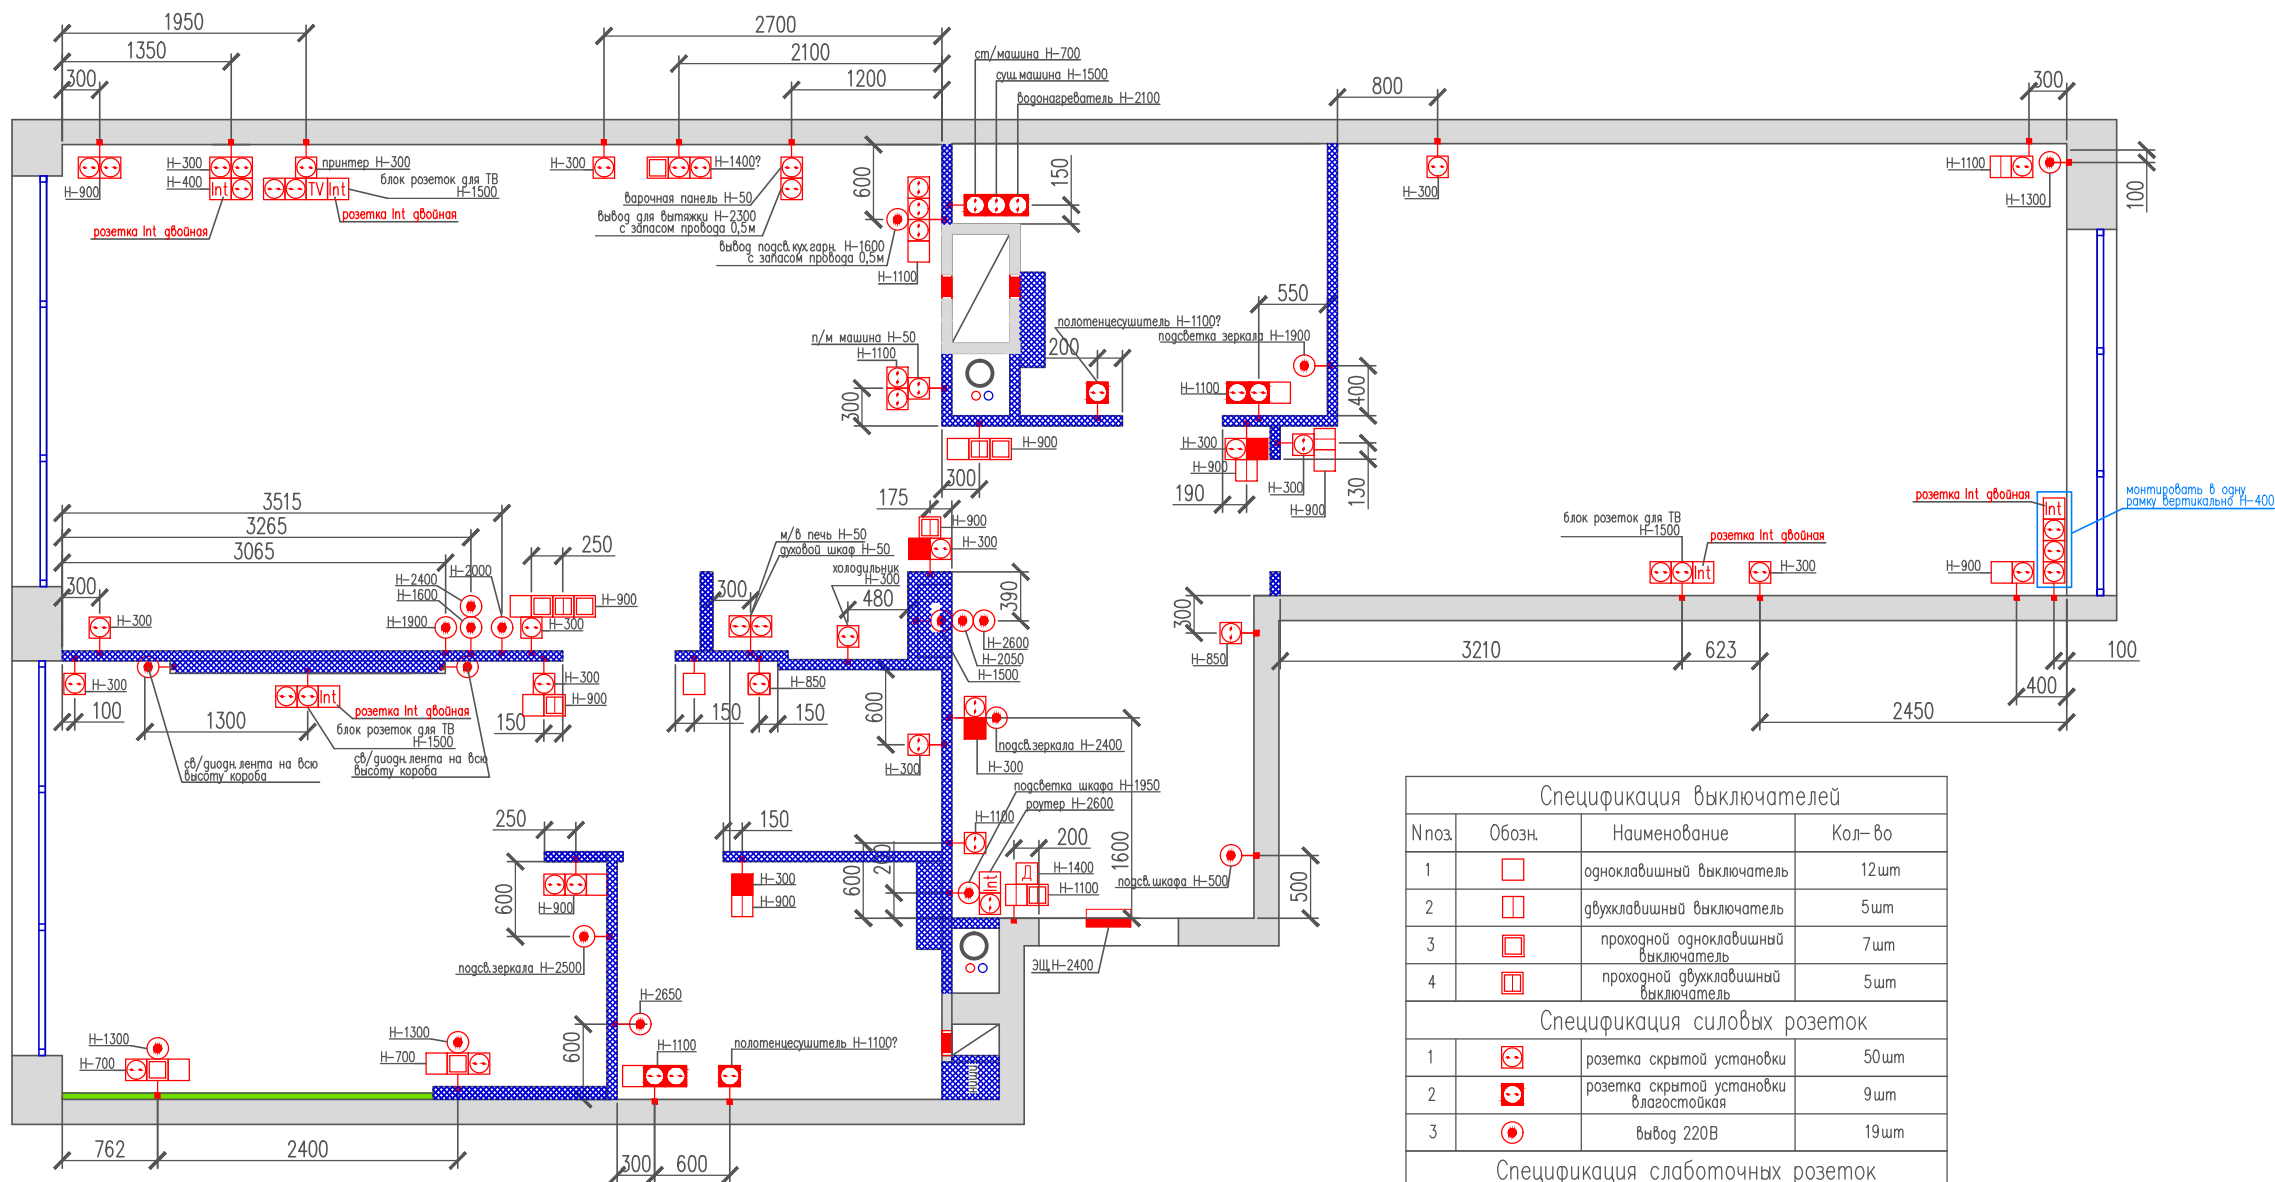

*** Высота установки розеток Н-300мм от уровня чистого пола (кроме обозначенных на чертеже)
*** Высота установки выключателей Н-900мм от уровня чистого пола (кроме обозначенных на чертеже)
*** Привязки выводов и розеток в месте установки кухни выполнить согласно техусловиям, предоставляемым поставщиком. Привязку и высоту уточнить после выбора оборудования
*** Все высотные отметки даны от уровня чистого пола до центра группы
*** Все объединенные группы розеток и выключателей монтировать в одну рамку
*** Трансформаторы светодиодной ленты монтируются в боксе для групп автоматов или в ближайших шкафах

Спецификация выключателей			
№поз	Обозн.	Наименование	Кол-во
1		одноклавишный выключатель	12шт
2		двухклавишный выключатель	5шт
3		проходной одноклавишный выключатель	7шт
4		проходной двухклавишный выключатель	5шт
Спецификация силовых розеток			
1		розетка скрытой установки	50шт
2		розетка скрытой установки влагостойкая	9шт
3		вывод 220В	19шт
Спецификация слаботочных розеток			
1		ТВ	1шт
2		интернет	5шт—двойных 1шт—одинарная
3		домофон	1шт
4		телефон	—
5		audio вывод	—
		силовой щит электрический	1шт
		регулятор теплого пола	4шт
Спецификация рамок			
1		рамка одинарная	28шт
2		рамка двойная	14шт
3		рамка тройная	9шт
4		рамка четверная	4шт

Экспликация помещений

№пмщ	Наименование	Скв. м
1	Кухня-гостиная	28,9
2	Спальня 1	19,3
3	Спальня 2	22,4
4	Прихожая-холл	10,2
5	Санузел 1	5,3
6	Санузел 2	5,7

Общая площадь 91,8


Условные обозначения

	существующие стены
	сан. тех. короб
	радиатор
	трубы отопления
	вентиляция
	счетчик электр.
	предполагаемые короба
	вент. канал

Перегородки

№поз	Обозначение	Наименование	Кол-во
1		негорючий перегородочный блок на всю высоту помещения	

Размещение выключателей с указанием групп включения светильников

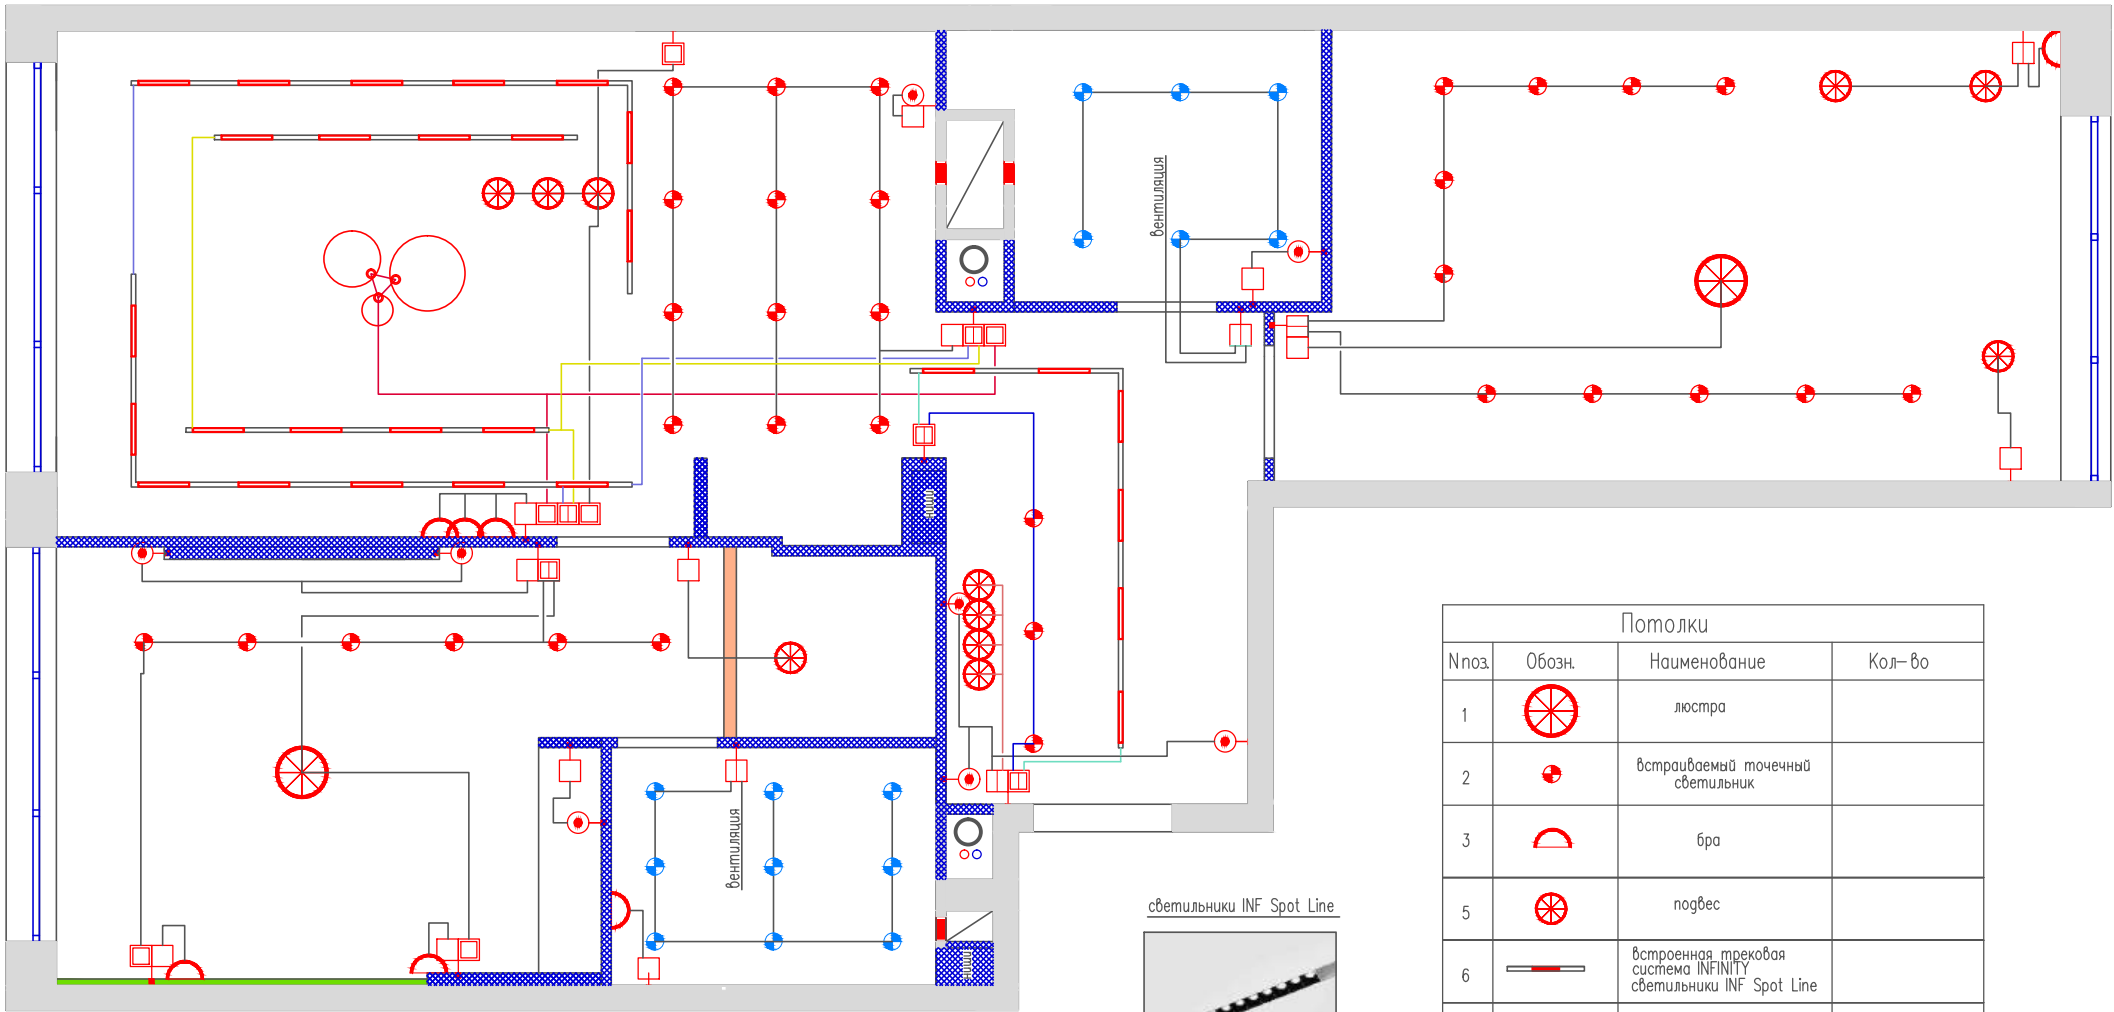

светильники INF Spot Line



Потолки			
№поз.	Обозн.	Наименование	Кол-во
1		люстра	
2		встраиваемый точечный светильник	
3		бра	
5		подвес	
6		встроенная трековая система INFINITY светильники INF Spot Line	
7		встраиваемый точечный светильник влагостойкий	
Спецификация выключателей			
№поз.	Обозн.	Наименование	Кол-во
1		одноклавишный выключатель	12шт
2		двухклавишный выключатель	5шт
3		проходной одноклавишный выключатель	7шт
4		проходной двухклавишный выключатель	5шт

Экспликация помещений

№пмщ.	Наименование	Скв. м
1	Кухня-гостиная	28,9
2	Спальня 1	19,3
3	Спальня 2	22,4
4	Прихожая-холл	10,2
5	Санузел 1	5,3
6	Санузел 2	5,7

Общая площадь 91,8

Условные обозначения


	существующие стены
	сан. тех. короб
	радиатор
	трубы отопления
	вентиляция
	счетчик электр.ч.
	предполагаемые коробки
	вент. канал

Перегородки

№поз.	Обозначение	Наименование	Кол-во
1		влагостойкий перегородочный блок на всю высоту помещения	

					Дизайнер Ларенкова Елена		
					+7(926) 135-23-40		
					foxnn2000@yandex.ru		
Изм.	Лист	докум.	Подп.	Дата	Дизайн-проект интерьера квартиры 91,3м.кв	Стадия	Лист
Разраб.	Ларенкова Елена					РП	12
Пров.							
Т.контр.					Размещение выключателей с указанием групп включения светильников		
Н.контр.							
Умв.							

План привязки сантехнического оборудования

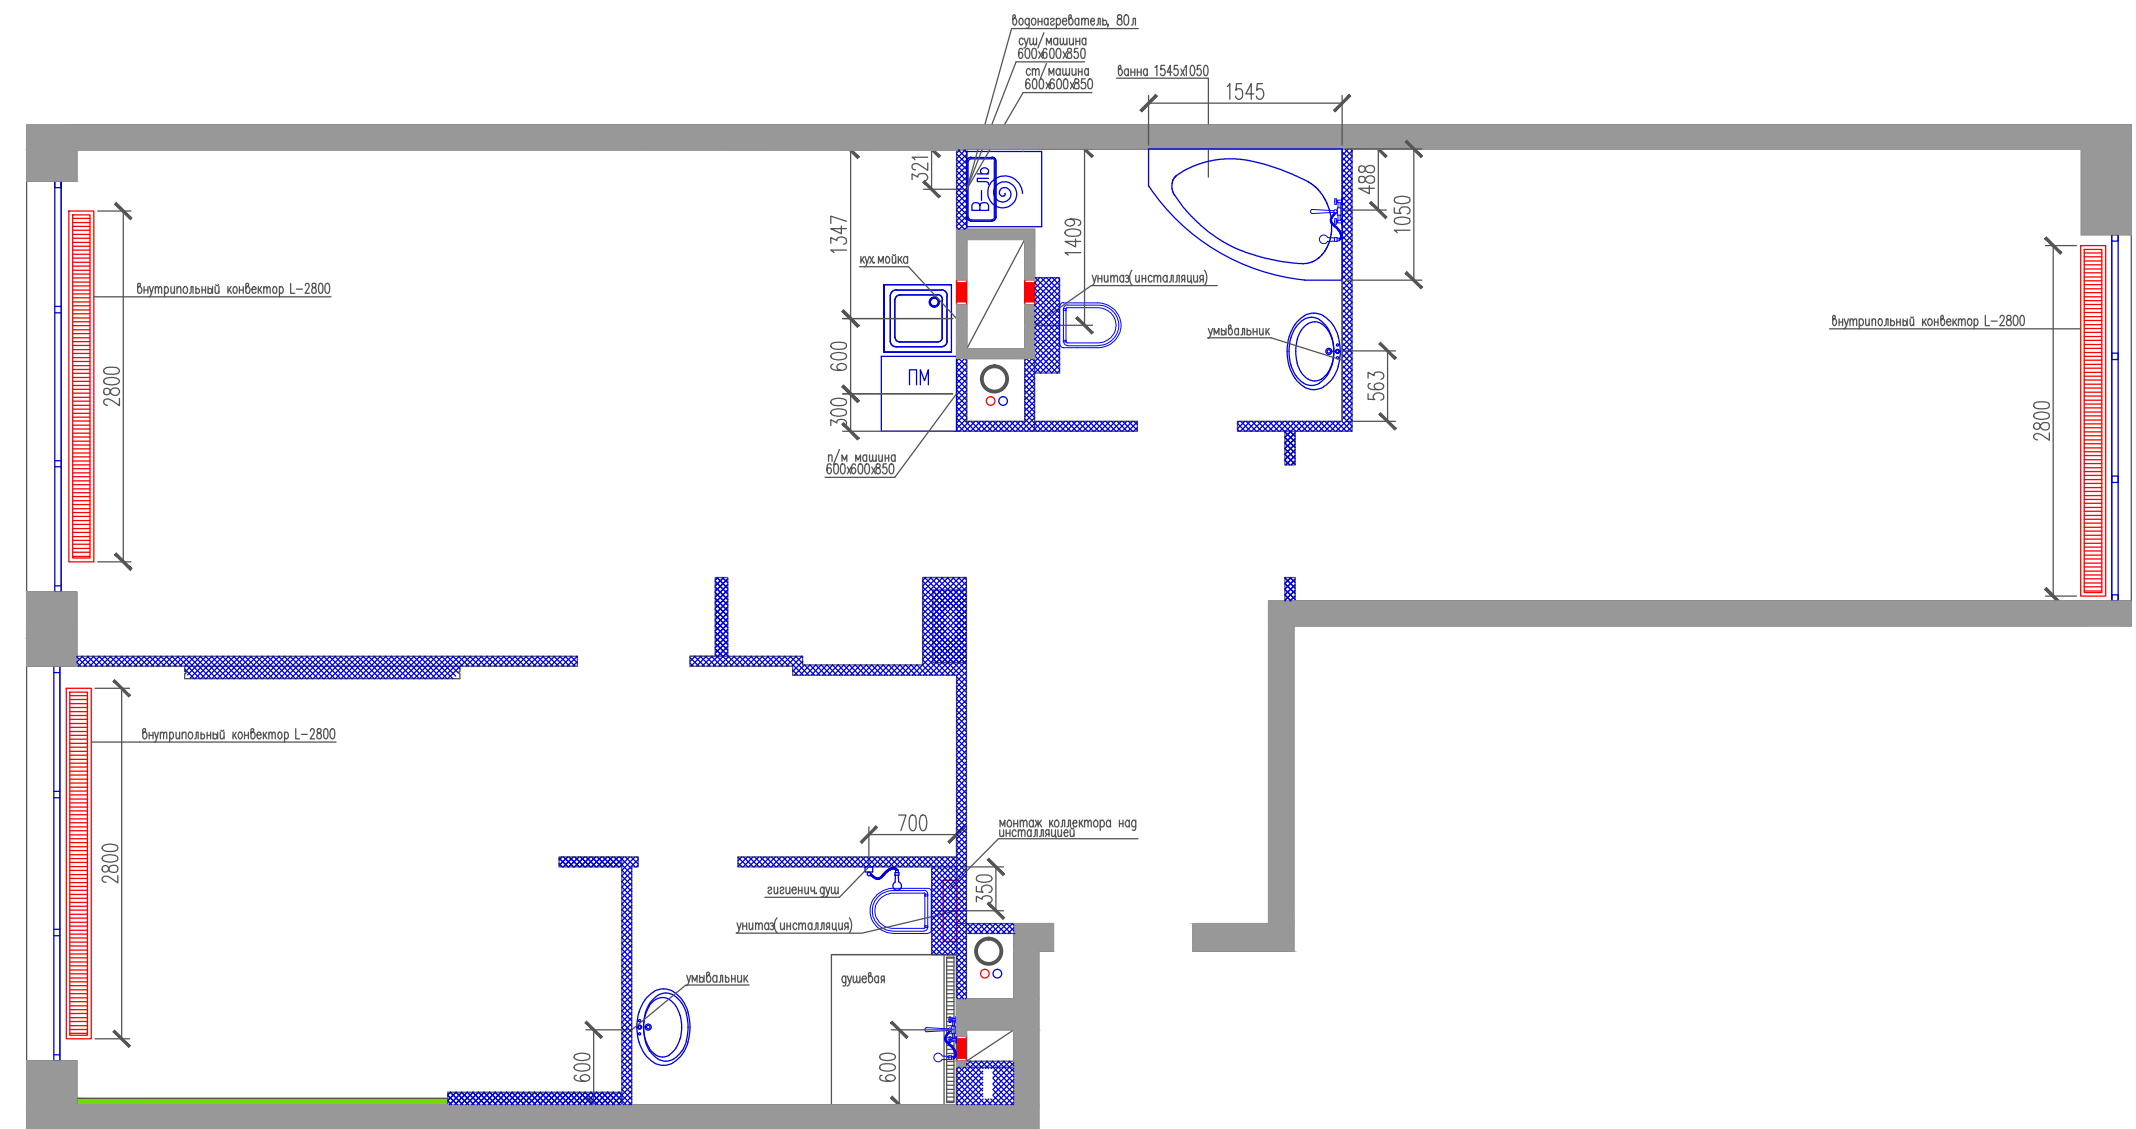


*** Все размеры, площади, привязки предварительные, требуют уточнения после проведения монтажных работ и работ по выравниванию стен
*** Все размеры даны от чистых стен до центра вывода
*** Выводы смотреть на сантехнических картах поставщика


Экспликация помещений			
№пмщ.	Наименование	Скв. м	
1	Кухня-гостиная	28,9	
2	Спальня 1	19,3	
3	Спальня 2	22,4	
4	Прихожая-холл	10,2	
5	Санузел 1	5,3	
6	Санузел 2	5,7	
Общая площадь		91,8	
Условные обозначения			
	существующие стены		
	сан. тех. короб		
	радиатор трубы отопления		
	вентиляция		
	счетчик электрич.		
	предполагаемые короба		
	вент. канал		
Перегородки			
№поз.	Обозначение	Наименование	Кол-во
1		Возвратный пазогребневый блок на всю высоту помещения	

Дизайнер Ларенкова Елена				
+7(926) 135-23-40				
foxnn2000@yandex.ru				
Изм.	Лист	докум	Подп.	Дата
Разраб.	Ларенкова Елена		Дизайн-проект интерьера	
Пров.			квартиры 91,3м.кв	
Т.контр.			Стадия	Лист
			РП	13
Н.контр.			Листов	
Умв.			План привязки сантехнического оборудования	

План водоподведения и водоотведения

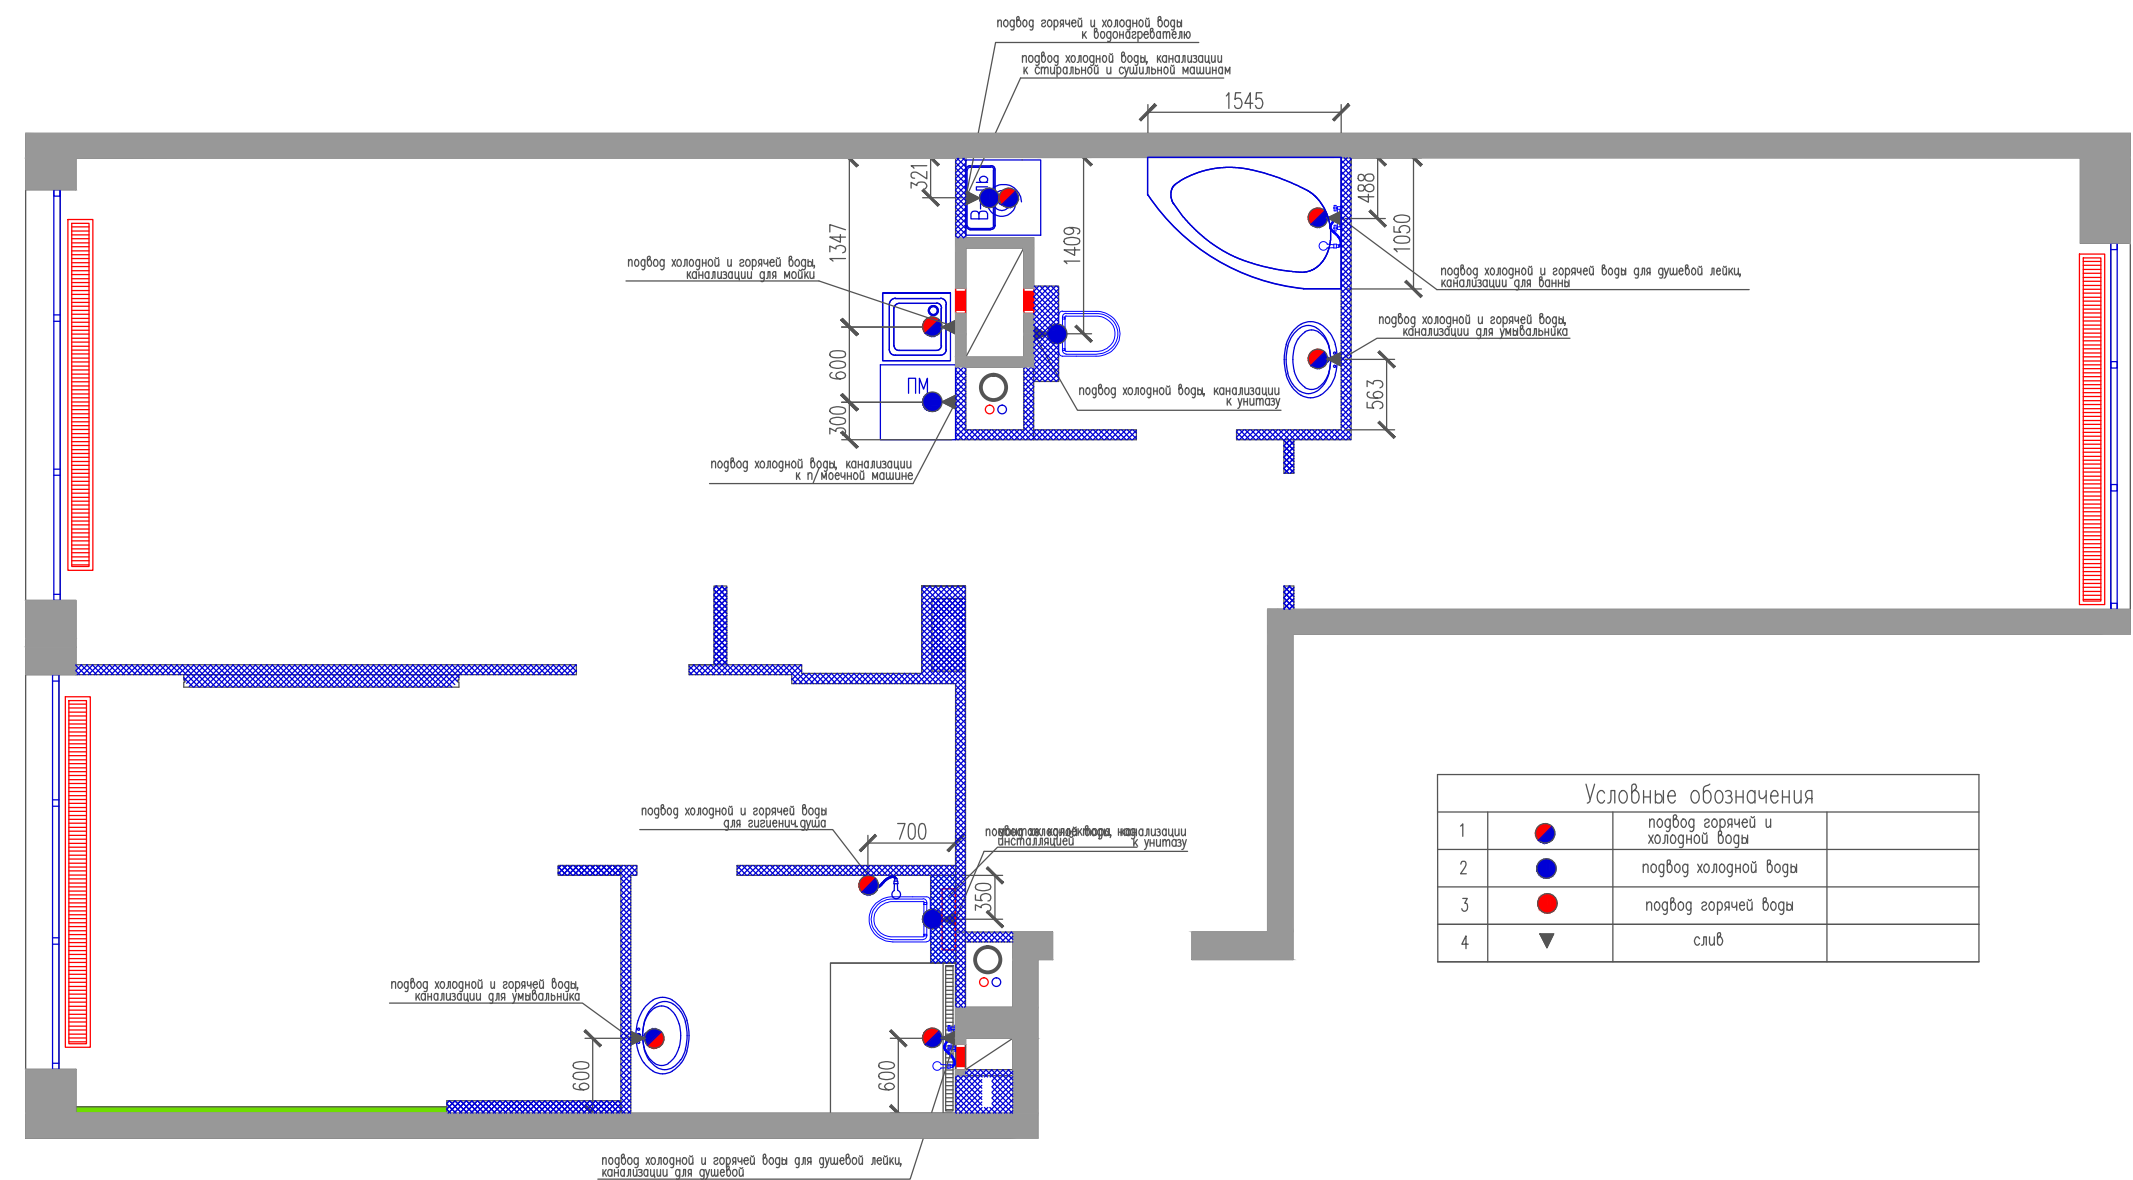


*** Привязки инженерного оборудования уточнить после выбора моделей по тех.паспортам
*** Привязки воды и канализации по кухне уточнить у поставщиков

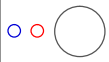Экспликация помещений			
№пмщ.	Наименование	Скв. м	
1	Кухня-гостиная	28,9	
2	Спальня 1	19,3	
3	Спальня 2	22,4	
4	Прихожая-холл	10,2	
5	Санузел 1	5,3	
6	Санузел 2	5,7	
Общая площадь		91,8	
Условные обозначения			
	существующие стены		
	сан. тех. короб		
	радиатор трубы отопления		
	вентиляция		
	счетчик электрич.		
	предполагаемые короба		
	вент. канал		
Перегородки			
№поз.	Обозначение	Наименование	Кол-во
1		Возвратный газосварочный блок на всю высоту помещения	

					Дизайнер Ларенкова Елена			
					+7(926) 135–23–40			
					foxnn2000@yandex.ru			
Изм	Лист	докум	Подп	Дата	Дизайн– проект интерьера квартиры 91,3м.кв	Стадия	Лист	Листов
Разраб.	Ларенкова Елена					РП	14	
Пров.								
Т.контр.								
					План водоподведения и водоотведения			
Н.контр.								
Утв.								

План теплых полов

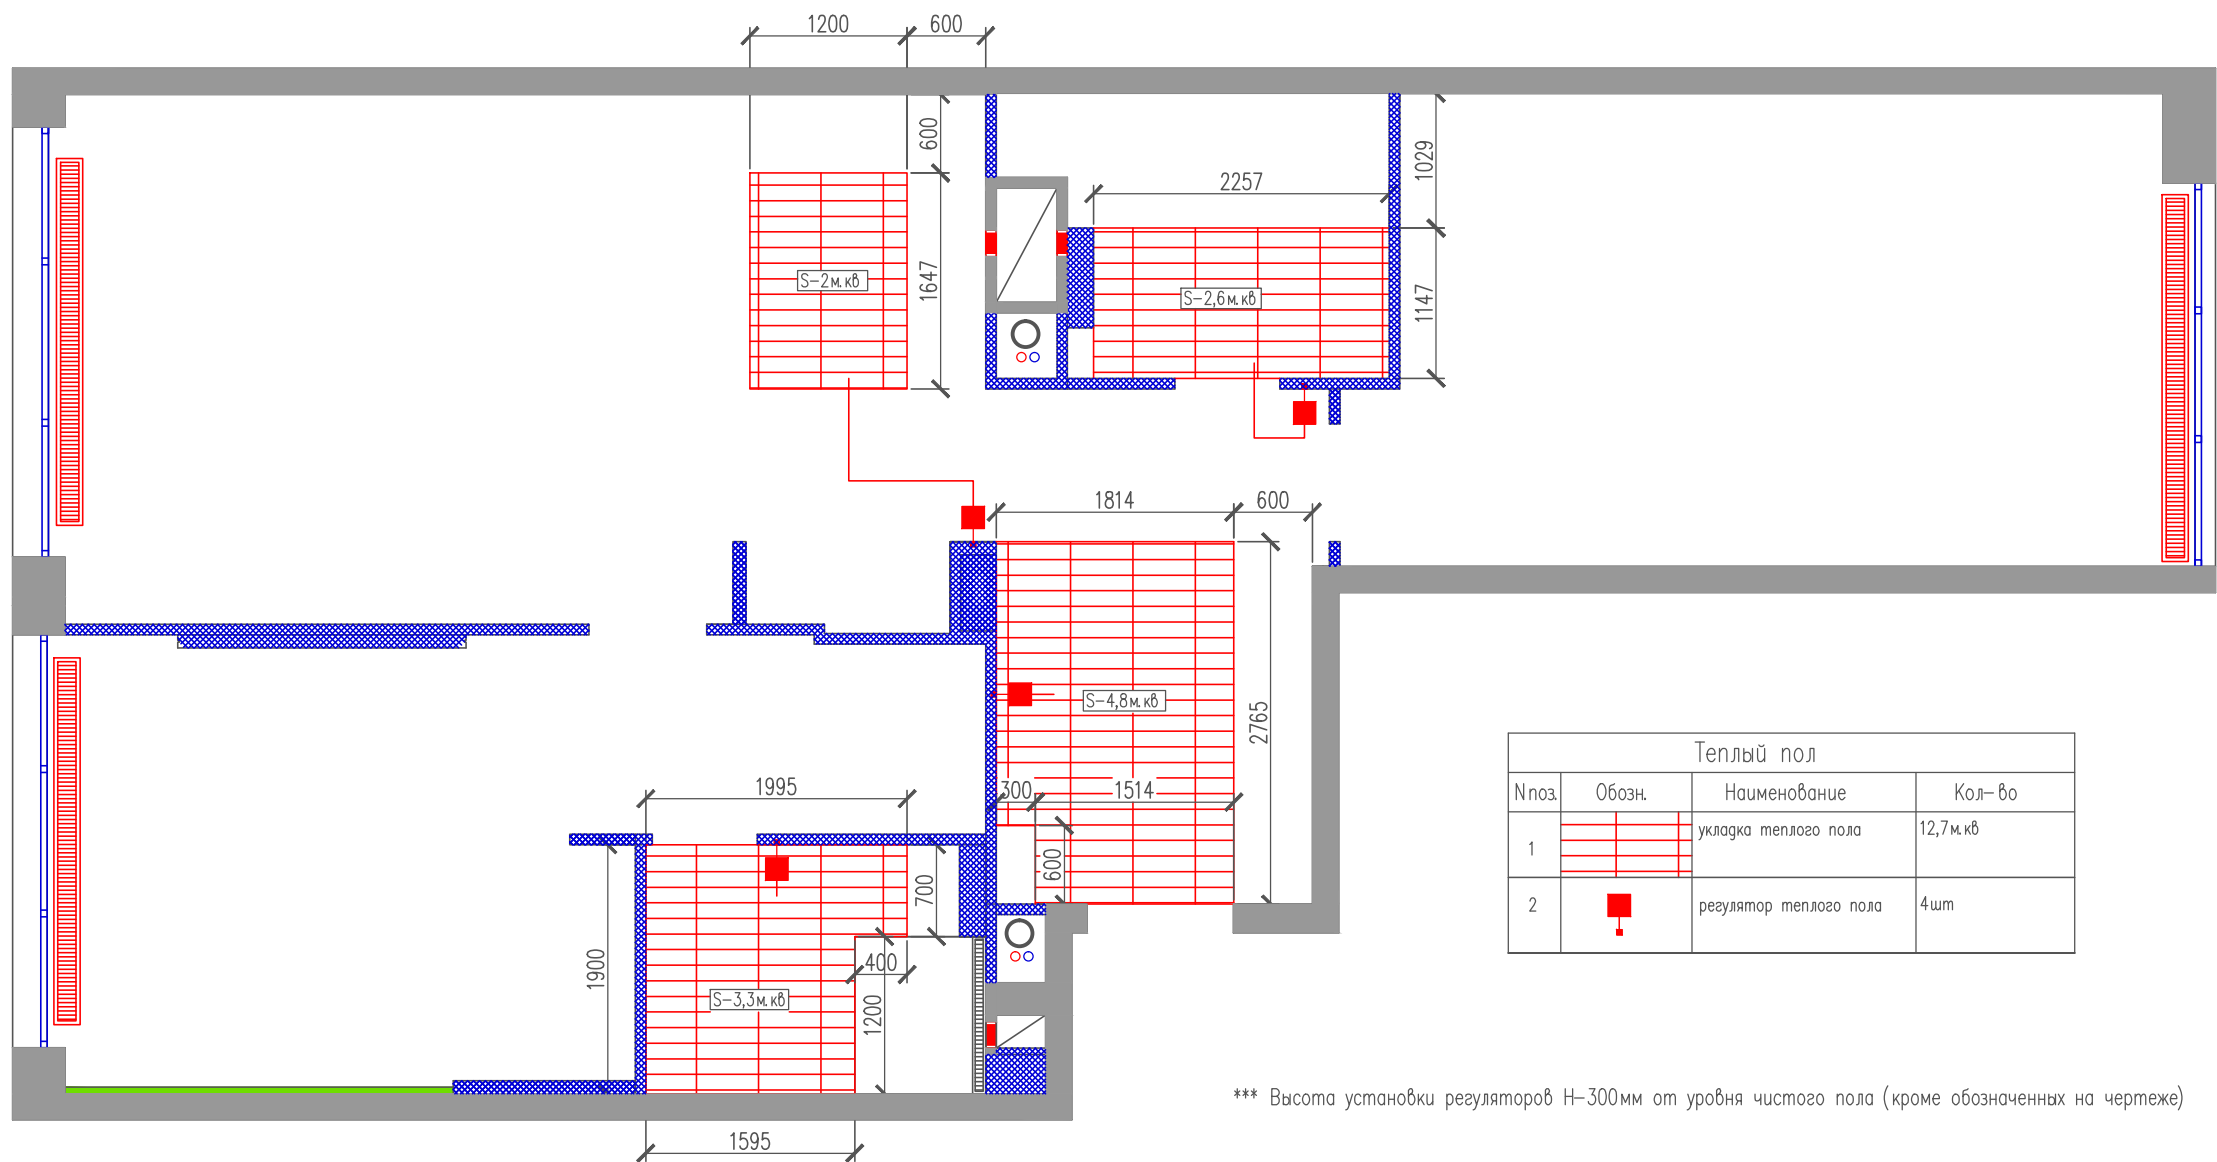

Экспликация помещений

№пмщ	Наименование	Скв.м
1	Кухня-гостиная	28,9
2	Спальня 1	19,3
3	Спальня 2	22,4
4	Прихожая-холл	10,2
5	Санузел 1	5,3
6	Санузел 2	5,7

Общая площадь 91,8

Условные обозначения

	существующие стены
	сан. тех. короб
	радиатор
	трубы отопления
	вентиляция
	счетчик электр.ч.
	предполагаемые короба
	вент. канал

Перегородки


№поз.	Обозначение	Наименование	Кол-во
1		высотный перегородочный блок на всю высоту помещения	

Теплый пол			
№поз.	Обозн.	Наименование	Кол-во
1		укладка теплого пола	12,7 м.кв
2		регулятор теплого пола	4 шт

*** Высота установки регуляторов Н=300мм от уровня чистого пола (кроме обозначенных на чертеже)

					Дизайнер Ларенкова Елена +7(926) 135–23–40 foxnn2000@yandex.ru			
Изм	Лист	докум	Подп	Дата				
Разраб.	Ларенкова Елена				Дизайн– проект интерьера квартиры 91,3м.кв	Стадия	Лист	Листов
Пров.						РП	15	
Т. контр.								
					План теплых полов			
Н. контр.								
Умв.								

План размещения внутреннего блока кондиционера

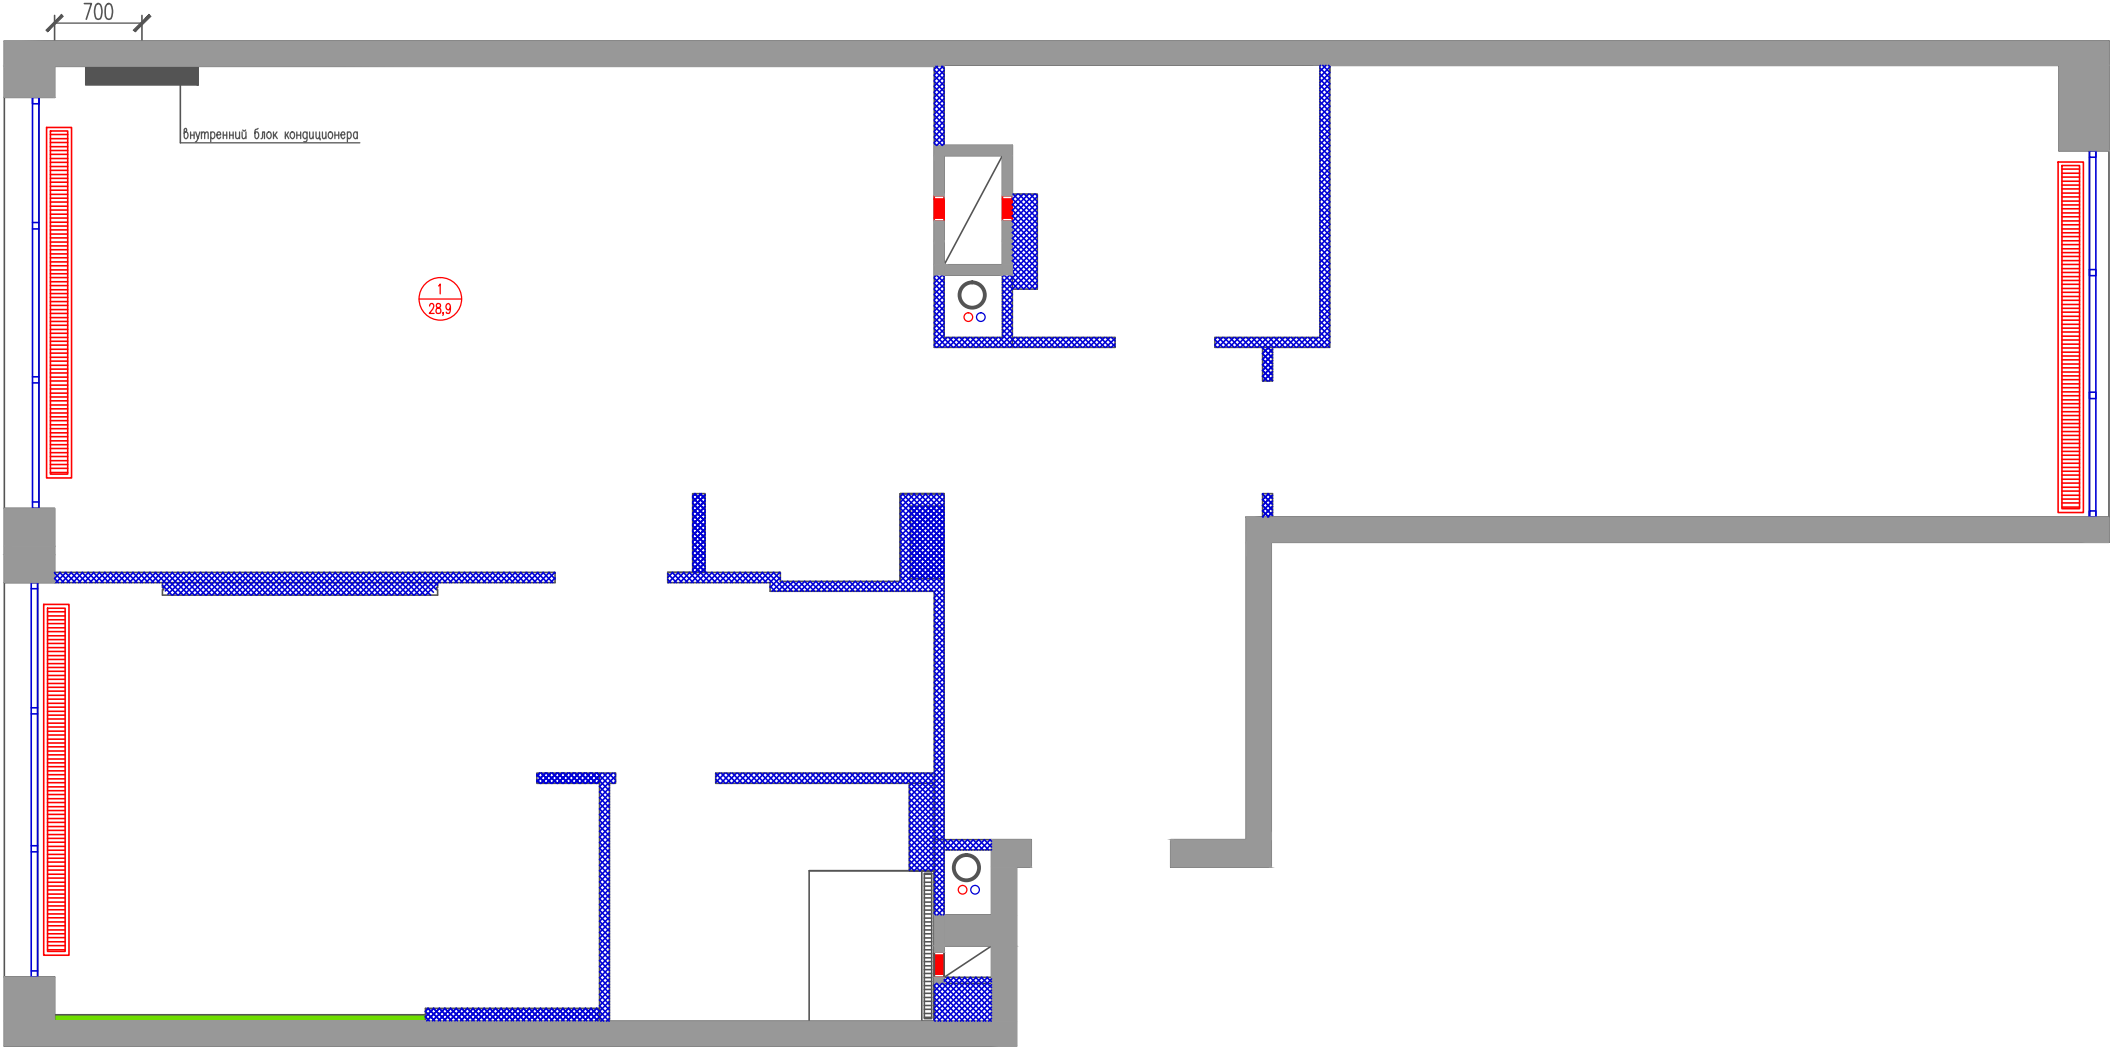

Экспликация помещений

№пмщ	Наименование	Скв. м
1	Кухня-гостиная	28,9
2	Спальня 1	19,3
3	Спальня 2	22,4
4	Прихожая-холл	10,2
5	Санузел 1	5,3
6	Санузел 2	5,7

Общая площадь 91,8

Условные обозначения


	существующие стены
○ ○ ○	сан. тех. короб
○○	радиатор трубы отопления
■	вентиляция
—	счетчик электр.ч.
▨	предполагаемые короба
▤	вент. канал

Перегородки

№поз.	Обозначение	Наименование	Кол-во
1	▨	влагостойкий перегородочный блок из всп. пены	1

					Дизайнер Ларенкова Елена
					+7(926) 135-23-40
					foxnn2000@yandex.ru
Изм.	Лист	докум	Подп.	Дата	Дизайн-проект интерьера
Разраб.	Ларенкова Елена				квартиры 91,3м.кв
Пров.					Стация РП
Т.контр.					Лист 16
					Листов
Н.контр.					План размещения внутреннего блока кондиционера
Утв.					

Схема заполнения дверных проемов

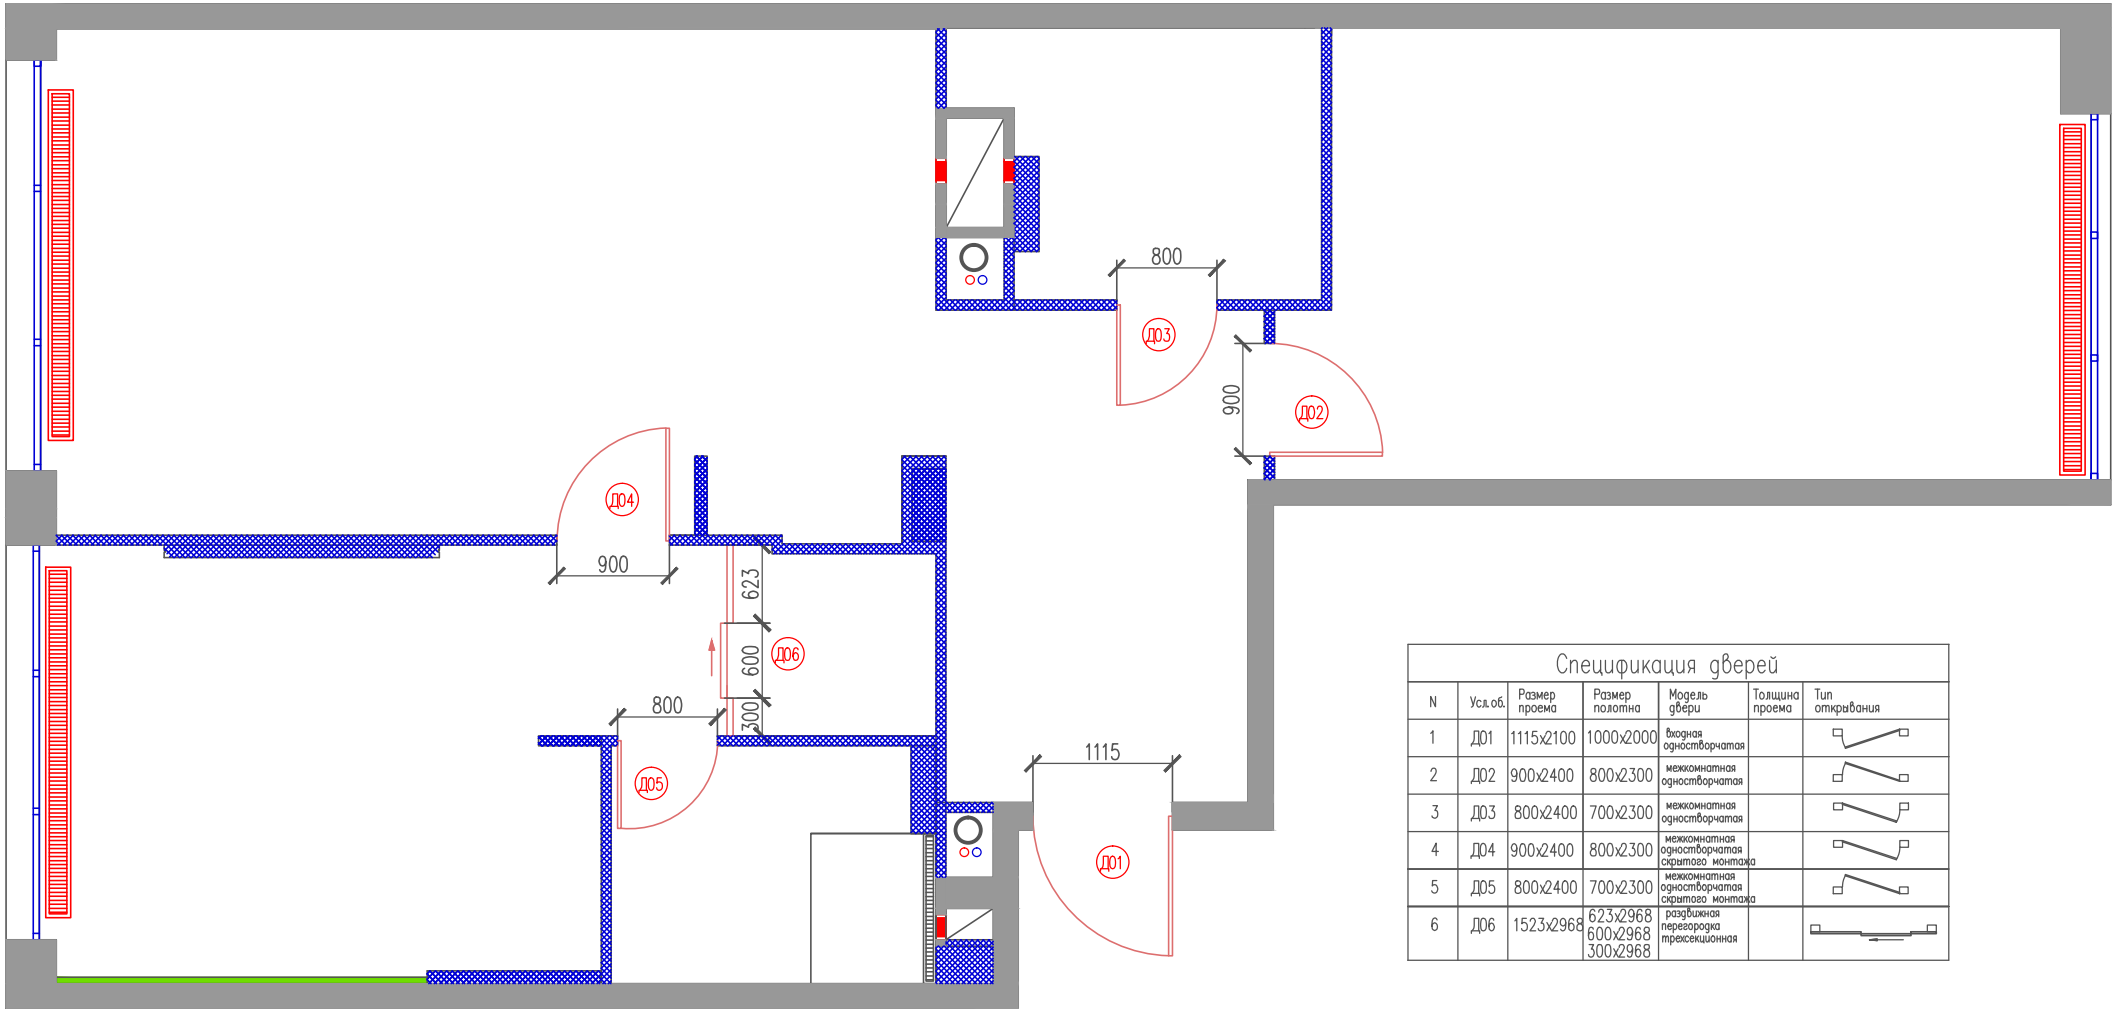

Спецификация дверей						
N	Усл.об.	Размер проема	Размер полотна	Модель двери	Толщина проема	Тип открывания
1	Д01	1115x2100	1000x2000	двухстворчатая		
2	Д02	900x2400	800x2300	межкомнатная одностворчатая		
3	Д03	800x2400	700x2300	межкомнатная одностворчатая		
4	Д04	900x2400	800x2300	межкомнатная одностворчатая скрытого монтажа		
5	Д05	800x2400	700x2300	межкомнатная одностворчатая скрытого монтажа		
6	Д06	1523x2968	623x2968 600x2968 300x2968	раздвижная перегородка трансекционная		

*** Уточнить размер проема и толщину стен с учетом чистовой отделки перед заказом дверей !!!

Экспликация помещений

№пмщ.	Наименование	Скв. м
1	Кухня-гостиная	28,9
2	Спальня 1	19,3
3	Спальня 2	22,4
4	Прихожая-холл	10,2
5	Санузел 1	5,3
6	Санузел 2	5,7

Общая площадь 91,8

Условные обозначения






	существующие стены
○ ○ ○	сан. тех. короб
○○	радиатор
▬	трубы отопления
▬	вентиляция
▬	счетчик электр.ч.
▨	предполагаемые короба
▧	вент. канал

Перегородки

№поз.	Обозначение	Наименование	Кол-во
1	▨	высотный перегородочный блок на всю высоту помещения	

					Дизайнер Ларенкова Елена			
					+7(926) 135–23–40			
					foxnn2000@yandex.ru			
Изм	Лист	докум	Подп	Дата	Дизайн– проект интерьера квартиры 91,3м.кв	Стадия	Лист	Листов
Разраб.	Ларенкова Елена			РП		17		
Пров.								
Т. контр.								
					Схема заполнения дверных проемов			
Н. контр.								
Утв.								

Развертка стен кухни-гостиной

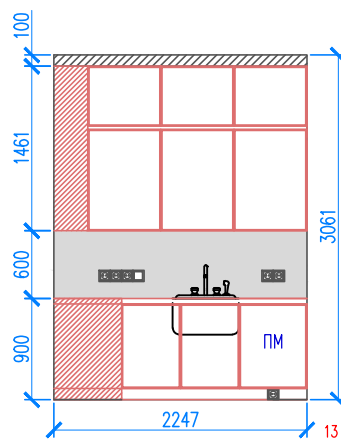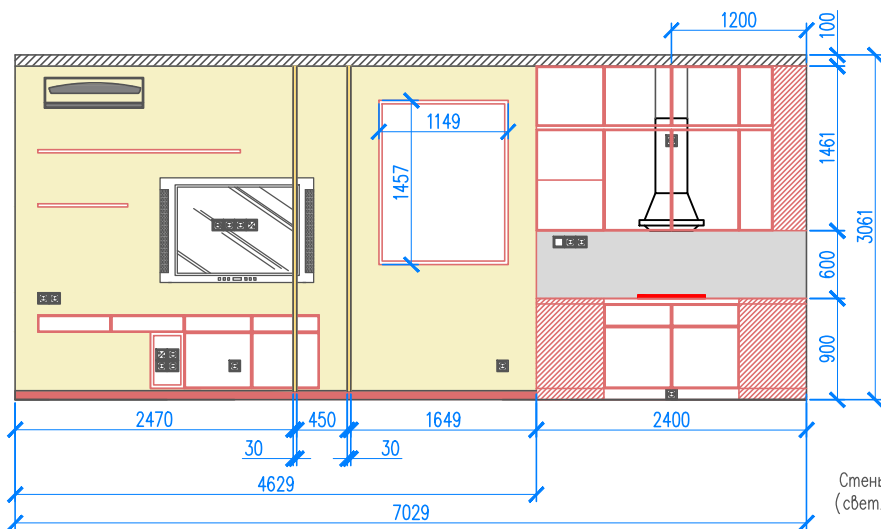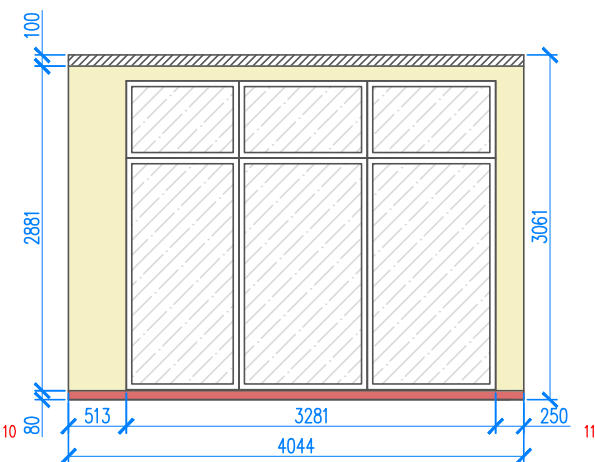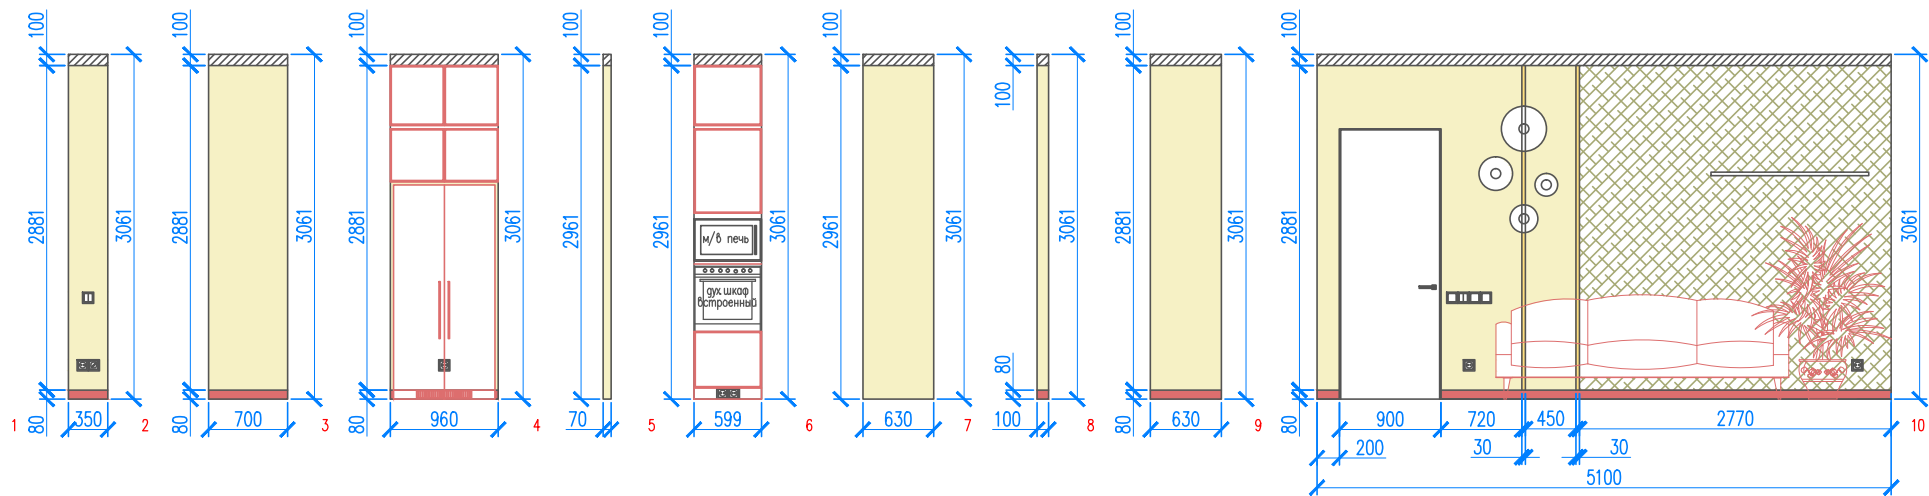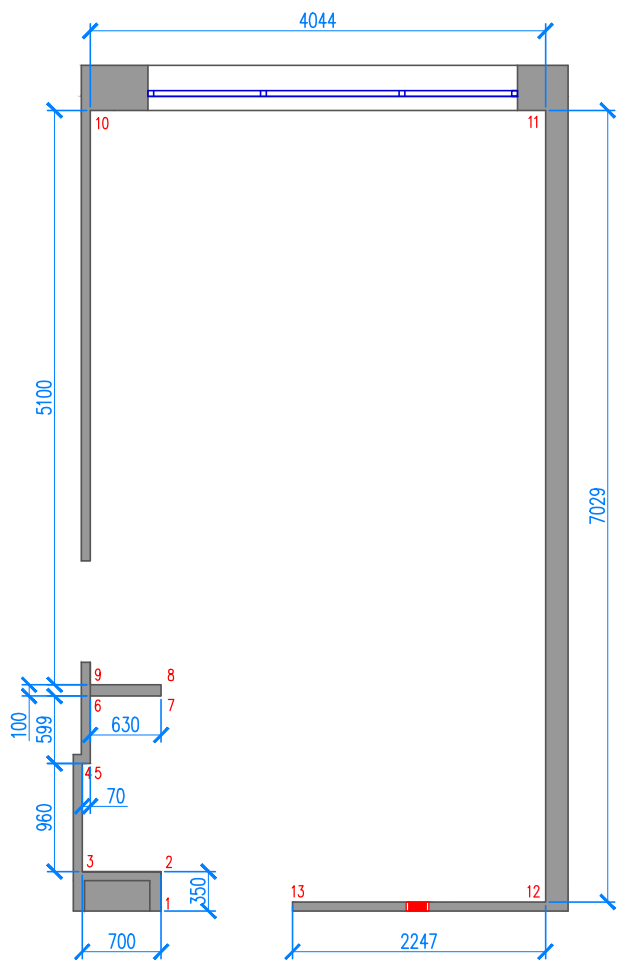


Стены за кухонным гарнитуром- под покраску
(сбелю/бежевый цвет арт. SW7563 Restful White)

Ведомость отделки стен			
№поз.	Обозн.	Наименование	Кол-во
1		под покраску Sherwin-Williams арт. SW7563 Restful White	S-47,4м.кв
2		плинтус полиуретановый 2000х60х19 арт. SX195 Orac Decor (под покраску в цвет дверной обивки)	15,6м/п
3		фреска Re-Space Affresco арт. JK-43 col.1 2770х2961	S-8,2м.кв
4		искусственный камень? на фартук арт. (этот же материал идет на столешницу)	S-2,82м.кв
5		латунный молдинг (монтируется вровень со стеной) ширина 30мм	12м/п

Материалы посчитаны без запаса и округления


					Дизайнер Ларенкова Елена +7(926) 135–23–40 foxnn2000@yandex.ru			
Изм	Лист	докум	Подп	Дата	Дизайн– проект интерьера квартиры 91,3м.кв	Стадия	Лист	Листов
Разраб.	Ларенкова Елена					РП	18	
Пров.								
Т. контр.								
					Развертка стен кухни– гостиной			
Н. контр.								
Умв.								

Развертка стен прихожей–холла

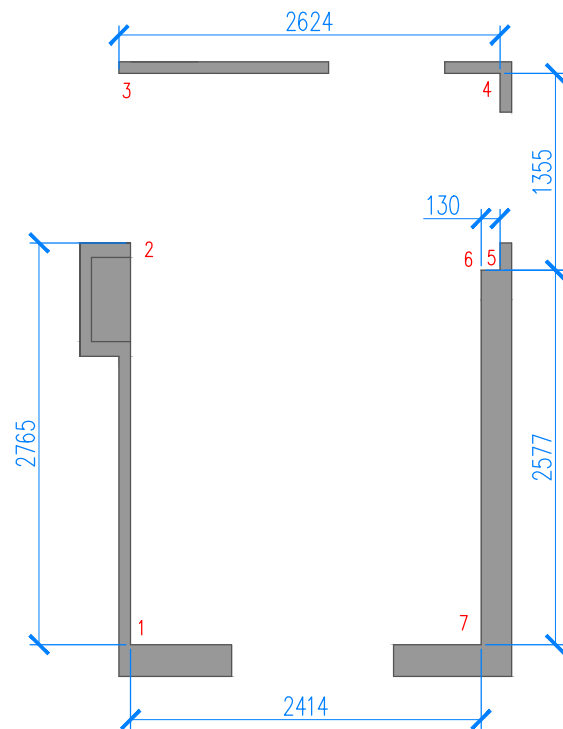


Ведомость отделки стен			
№поз.	Обозн.	Наименование	Кол-во
1		под покраску Sherwin-Williams apm.SW7563 Restfull White	S-29,5м.кв
2		плинтус полиуретановый 2000x80x19 apm.SX195 Orac Decor (под покраску в цвет дверной обналочки)	6,8м/п

Материалы посчитаны без запаса и округления

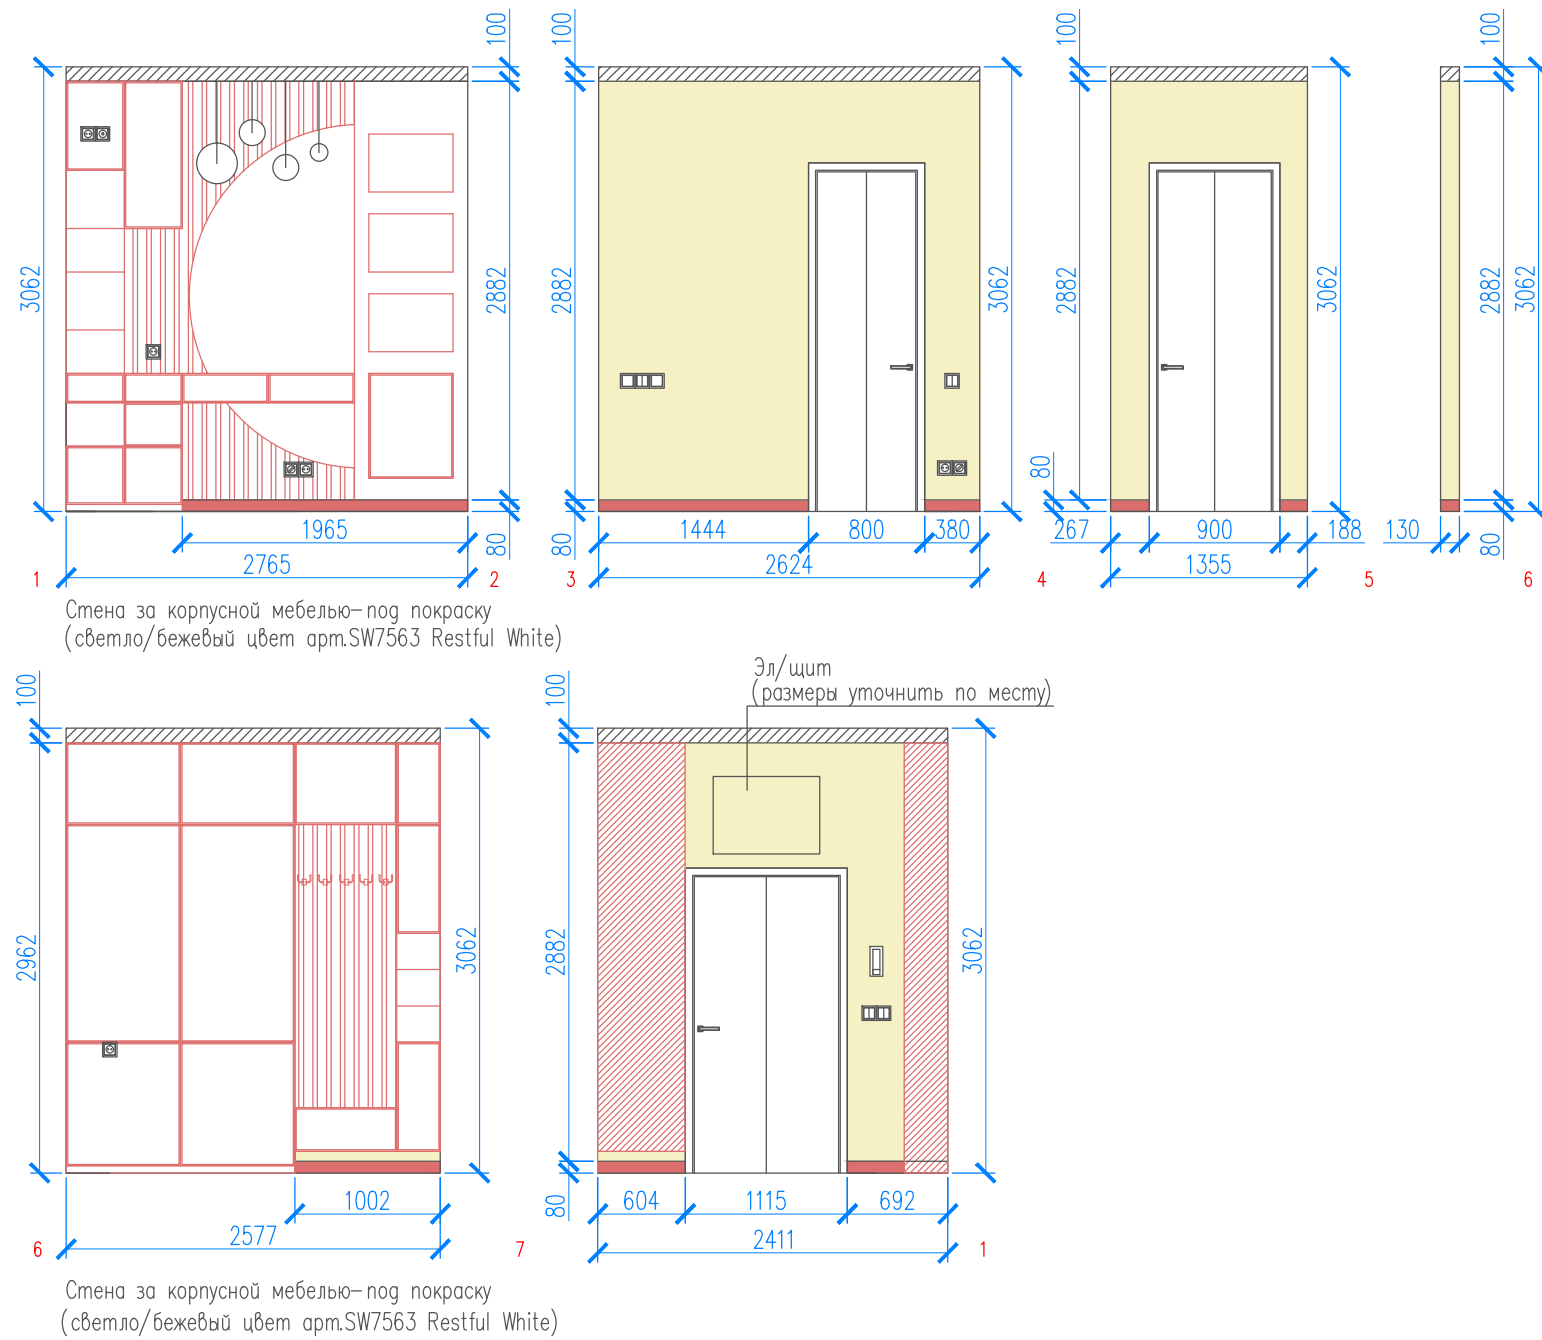


					Дизайнер Ларенкова Елена +7(926) 135–23–40 foxnn2000@yandex.ru			
Изм	Лист	докум	Подп	Дата				
Разраб.	Ларенкова Елена				Дизайн– проект интерьера квартиры 91,3м.кв	Стация	Лист	Листов
Пров.						РП	19	
Т. контр.								
					Развертка стен прихожей–холла			
Н. контр.								
Утв.								

Развертка стен спальни 1

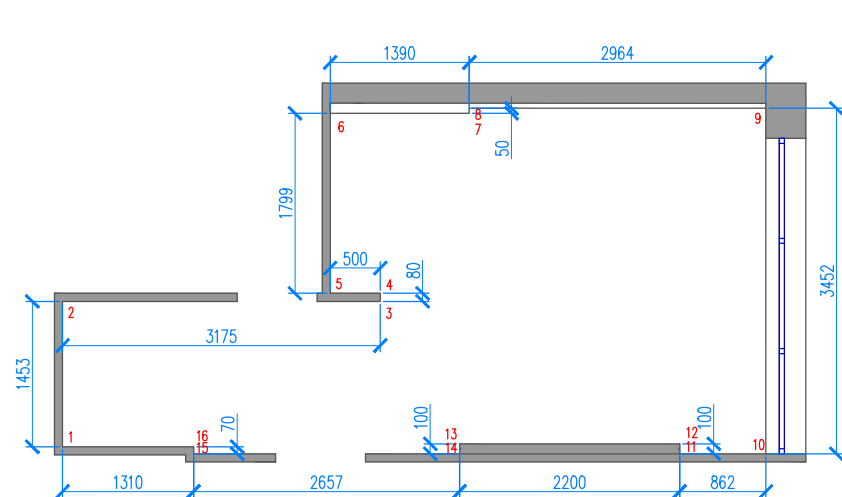


Ведомость отделки стен			
№поз.	Обозн.	Наименование	Кол-во
1		под покраску Sherwin-Williams арт.SW8917 Shell White	S-31,8м.кв
2		плитка полиуретановая 2000x80x9 арт.SX195 Orac Decor (под покраску в цвет дверной обивки)	15,4м/п
3		фотообои Wall-street арт.24376 fezzalst 2964x2988	S-8,9м.кв
4		под покраску Sherwin-Williams арт.SW6359 Sociable	S-2,82м.кв
5		светодиодная лента в мет.профиле L-3000 цвет профиля- латунь	2штх3м

Материалы посчитаны без запаса

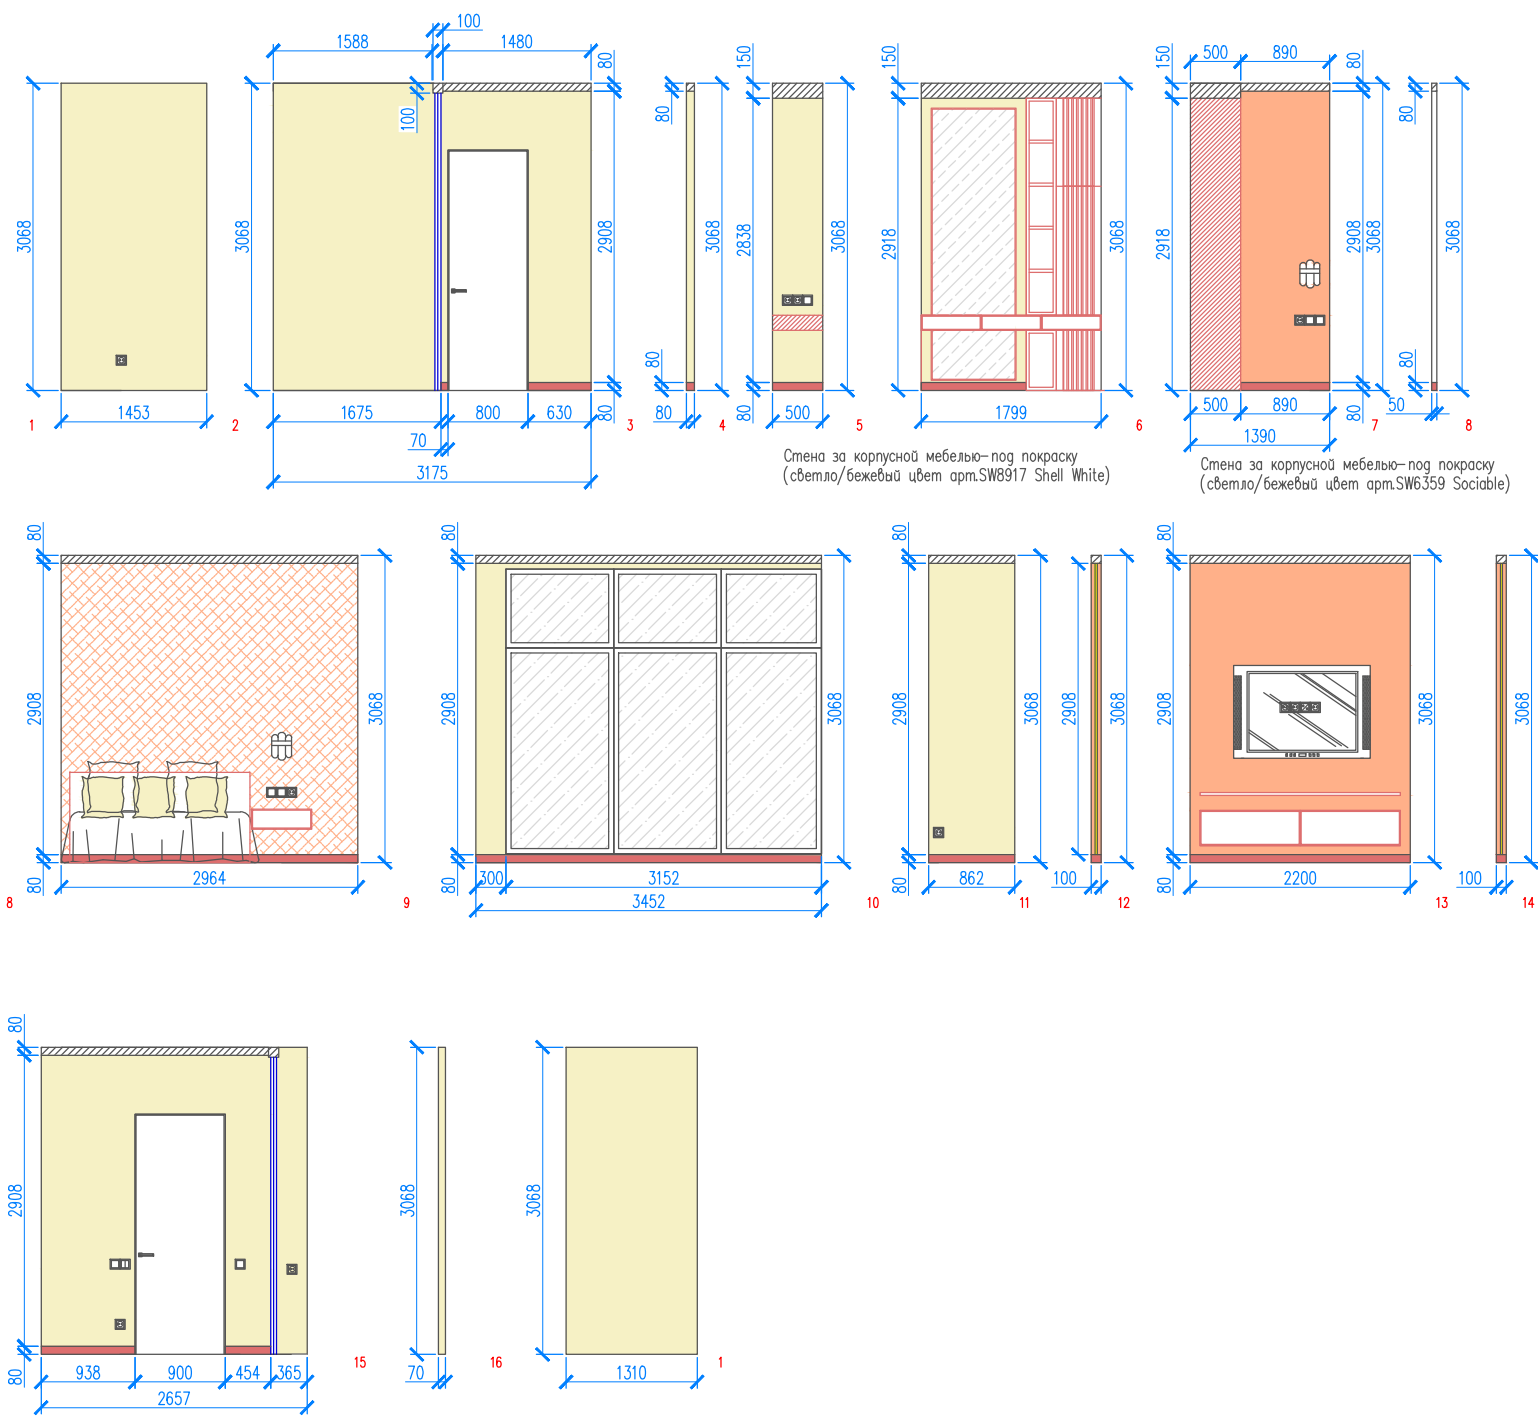



					Дизайнер Ларенкова Елена			
					+7(926) 135–23–40			
					foxnn2000@yandex.ru			
Изм	Лист	докум	Подп	Дата	Дизайн– проект интерьера квартиры 91,3м.кв	Стадия	Лист	Листов
Разраб.	Ларенкова Елена					РП	20	
Пров.								
Т. контр.								
					Развертка стен спальни 1			
Н. контр.								
Умв.								

Развертка стен спальни 2

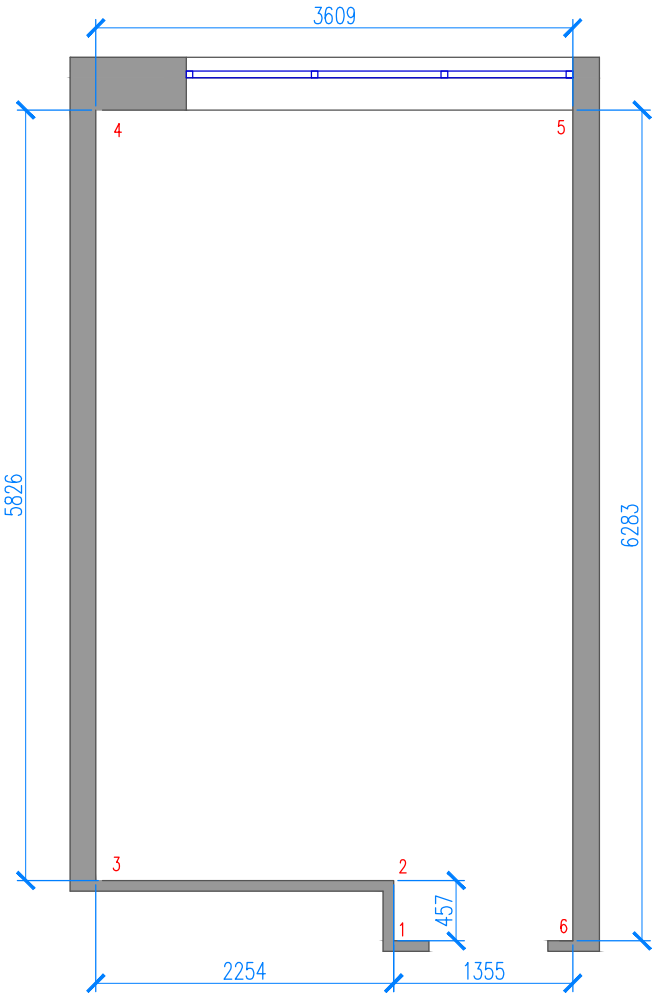



Ведомость отделки стен			
№поз.	Обозн.	Наименование	Кол-во
1		под покраску Sherwin-Williams арт.SW6056 Polite White	S-32,5 м.кв
2		плинтус полиуретановый 2000x80x19 арт.SX195 Orac Decor (под покраску в цвет дверной обналочки)	14,2 м/п
3		фотопечать на обоях 2400x2978	S-7,2 м.кв
4		роспись стены 2826x2978	S-8,4 м.кв

Материалы посчитаны без запаса

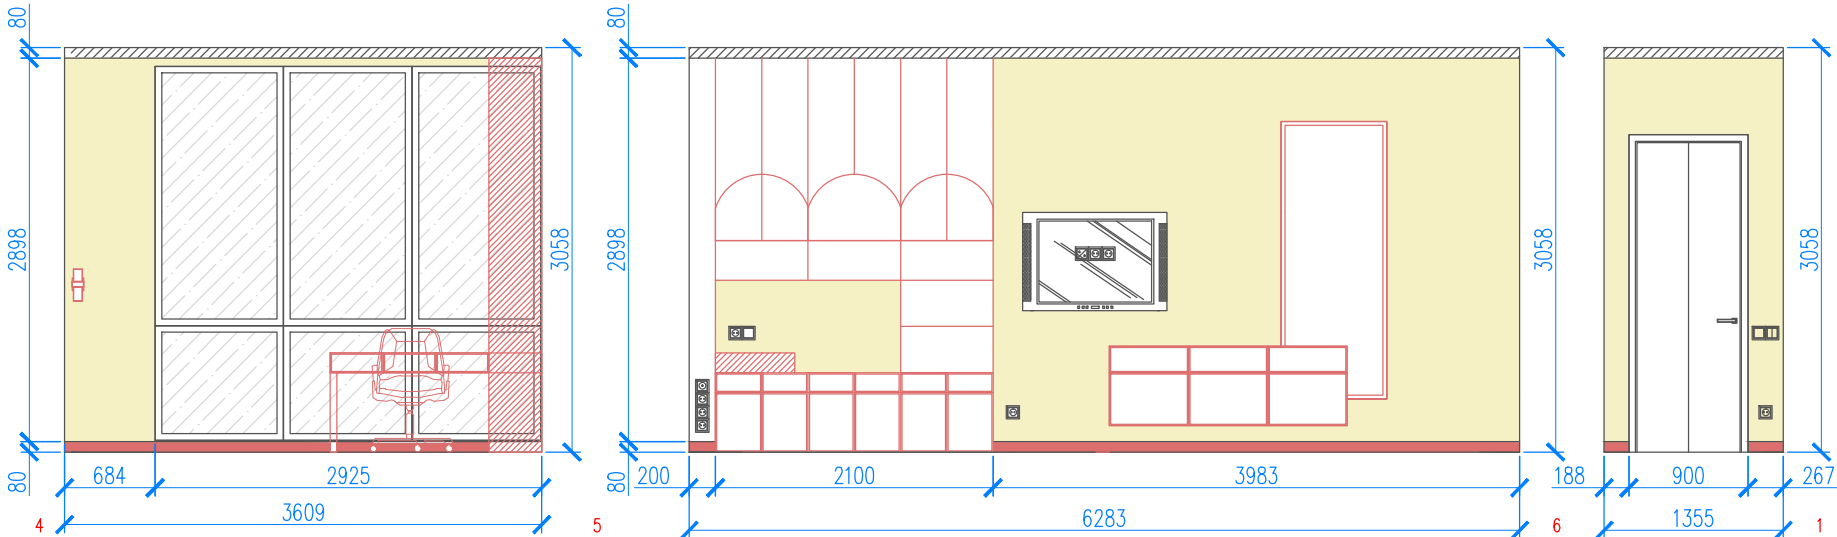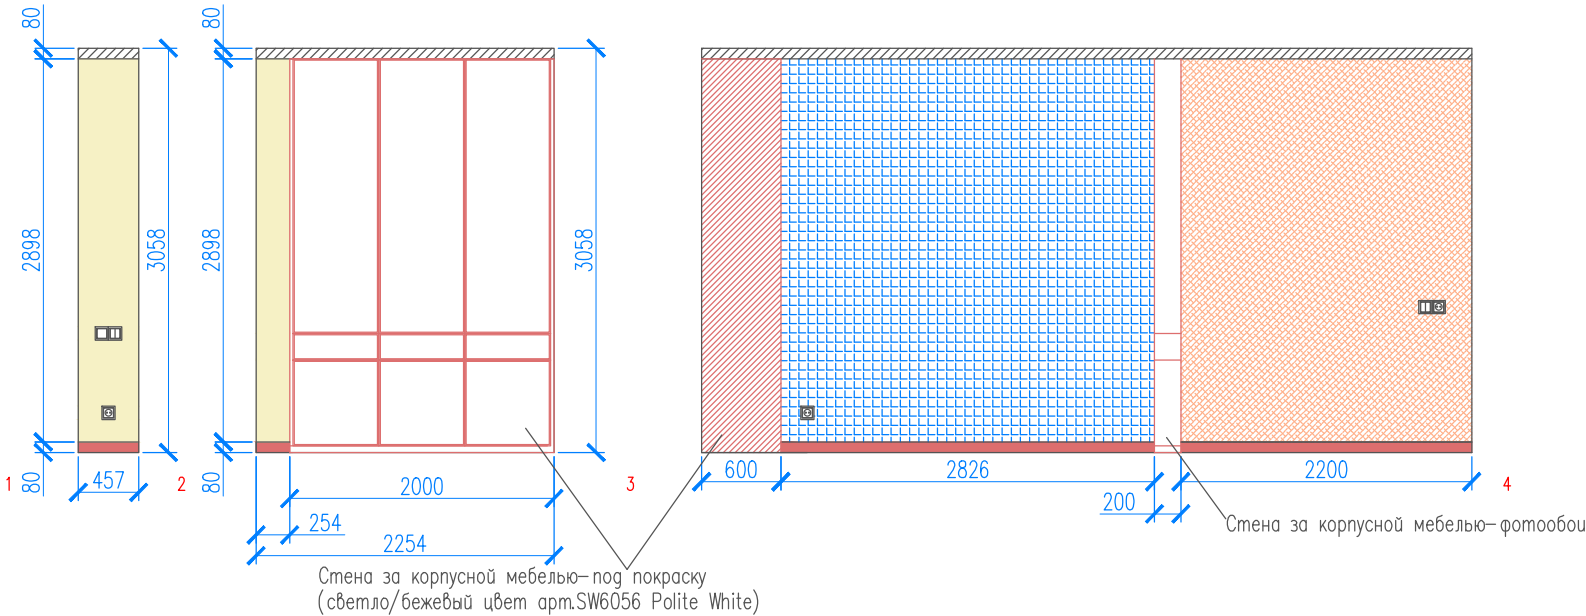


					Дизайнер Ларенкова Елена			
					+7(926) 135–23–40			
					foxnn2000@yandex.ru			
Изм	Лист	докум	Подп	Дата	Дизайн– проект интерьера квартиры 91,3м.кв	Стадия	Лист	Листов
Разраб.	Ларенкова Елена					РП	21	
Пров.								
Т. контр.								
					Развертка стен спальни 2			
Н. контр.								
Умв.								



Развертка стен санузла 1

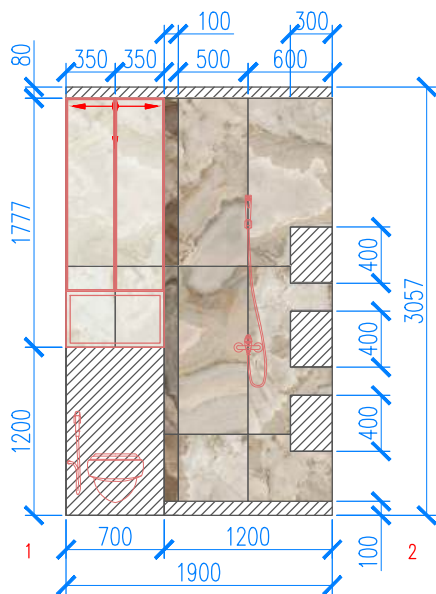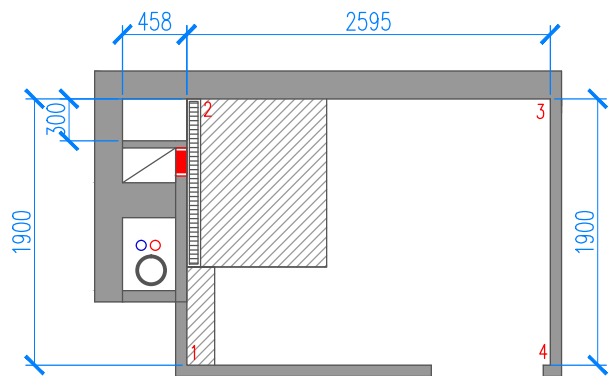

Развертка короба
инсталляции


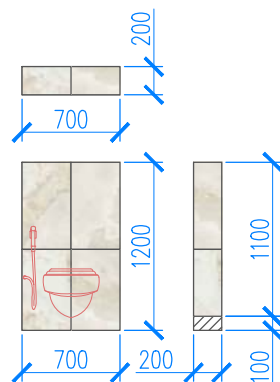


Развертка ниш
(3 штуки)

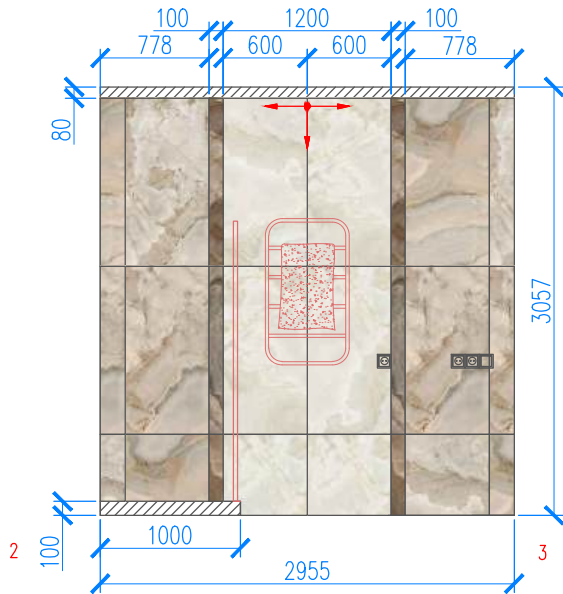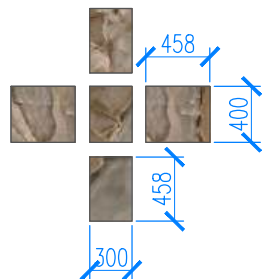


Ведомость отделки стен			
№поз.	Обозн.	Наименование	Кол-во
1		керамогранит 1200x600 Rex Reves de Rex Perle Glossy толщина 10мм www.artreal.ru	31шт
2		керамогранит 1200x600 Rex Reves de Rex Noisette Glossy толщина 10мм	22шт
3		керамогранит 1200x600 Rex Reves de Rex Choco Glossy толщина 10мм нарезка на полосы шириной 100мм	2шт
4		начало раскладки	

Ширина шва 1мм

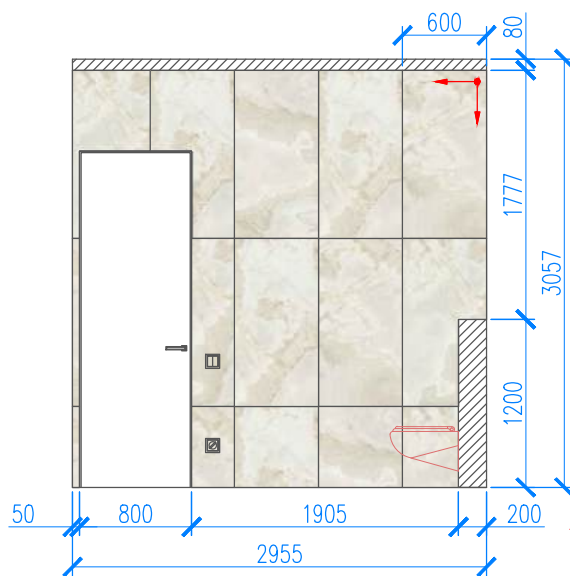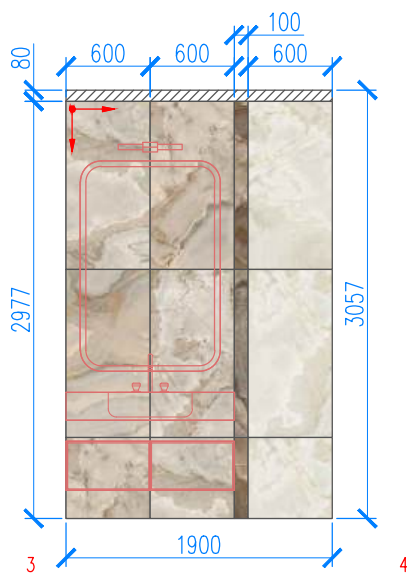

					Дизайнер Ларенкова Елена			
					+7(926) 135-23-40			
					foxnn2000@yandex.ru			
Изм	Лист	докум	Подп	Дата	Дизайн- проект интерьера квартиры 91,3м.кв	Стадия	Лист	Листов
Разраб.	Ларенкова Елена					РП	22	
Пров.								
Т. контр.								
					Развертка стен санузла 1			
Н. контр.								
Умв.								

Развертка стен санузла 2

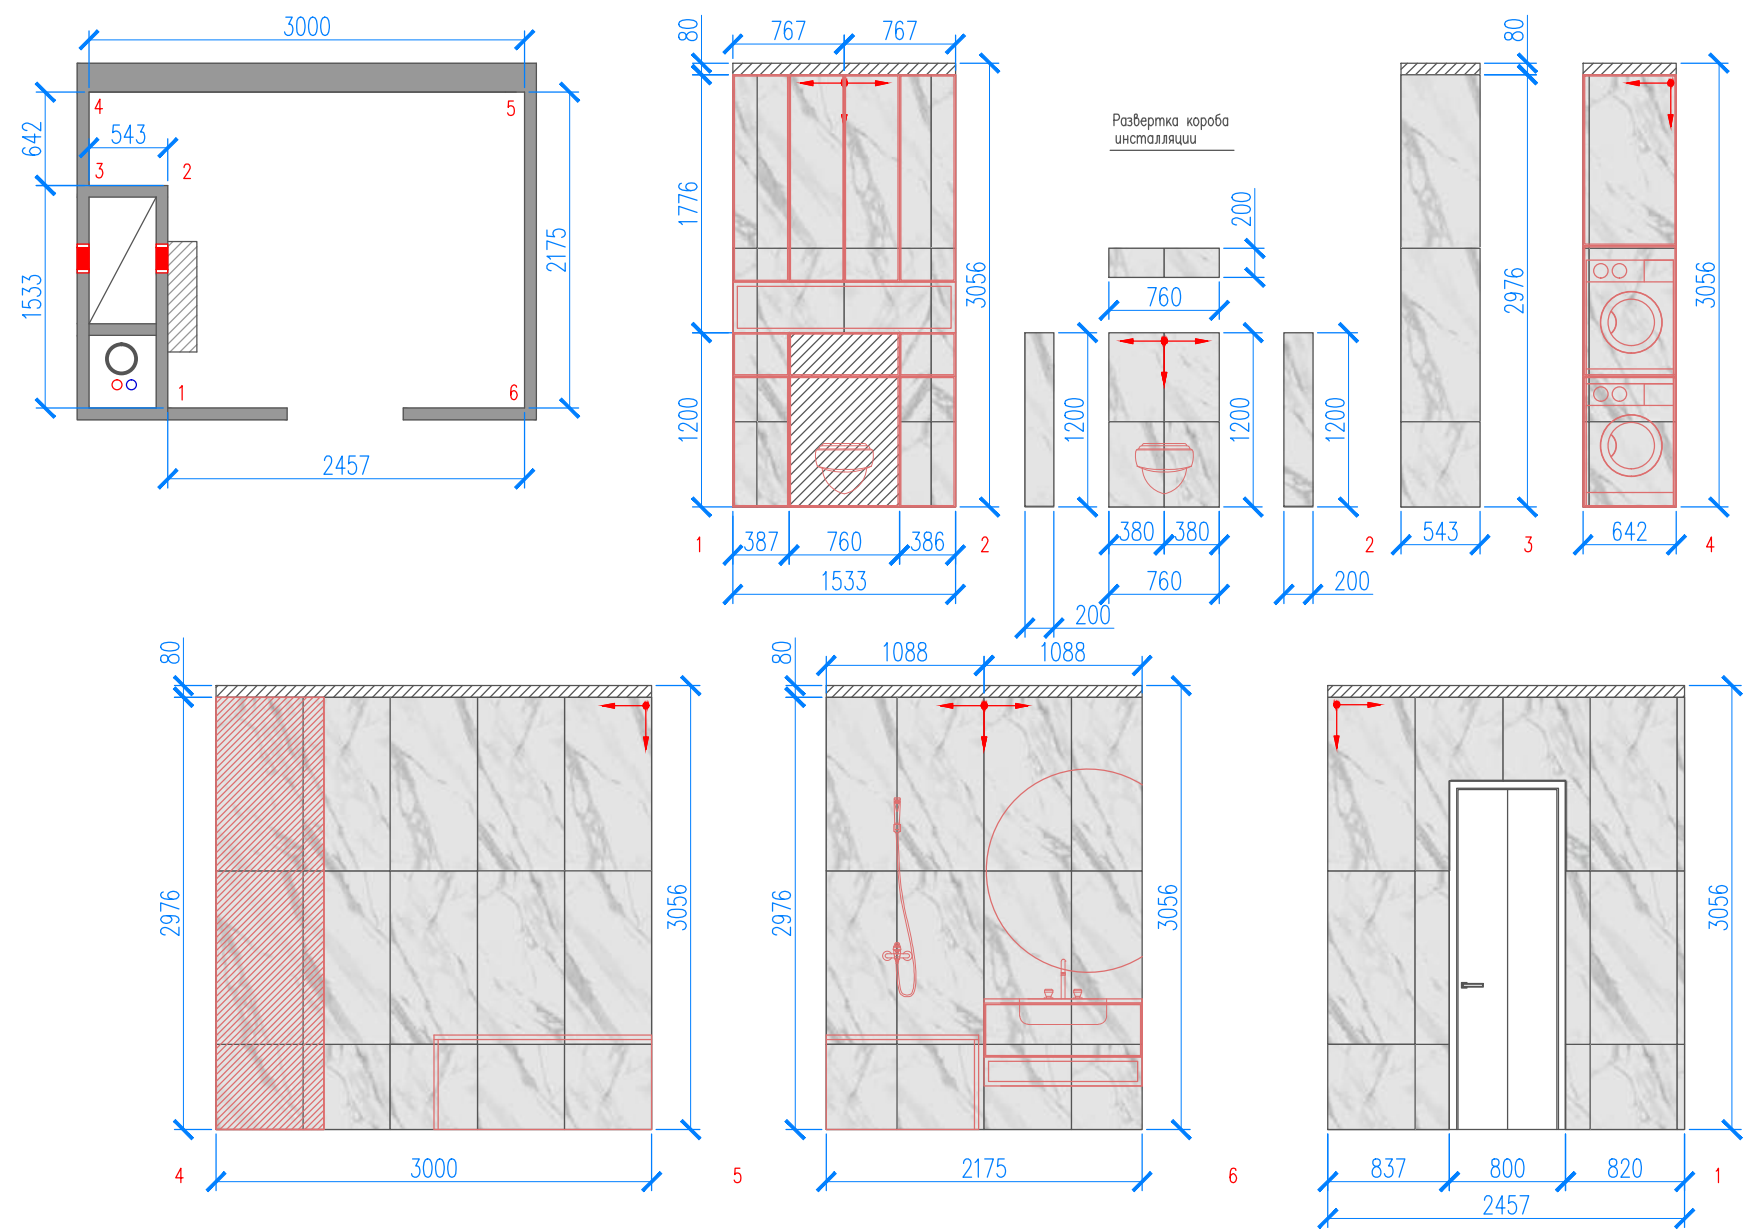


Ведомость отделки стен			
№поз	Обозн.	Наименование	Кол-во
1		керамогранит 1195x600 Монте тиберио, Керама Марацци арт.SG507102R лаппатированный обрезной толщина 11мм	29,5 м. кв+5%запас
4		начало раскладки	

Ширина шва 1мм


Изм.	Лист	докум	Подп	Дата	Дизайнер Ларенкова Елена +7(926) 135-23-40 foxnn2000@yandex.ru			
Разраб.	Ларенкова Елена							
Пров.					Дизайн- проект интерьера квартиры 91,3м.кв			
Т.контр.								
Н.контр.					Развертка стен санузла 2			
Умв.								
					Стадия	Лист	Листов	
					РП	23		

Габариты мебели. Прихожая—холл

Мебель в прихожей-холле

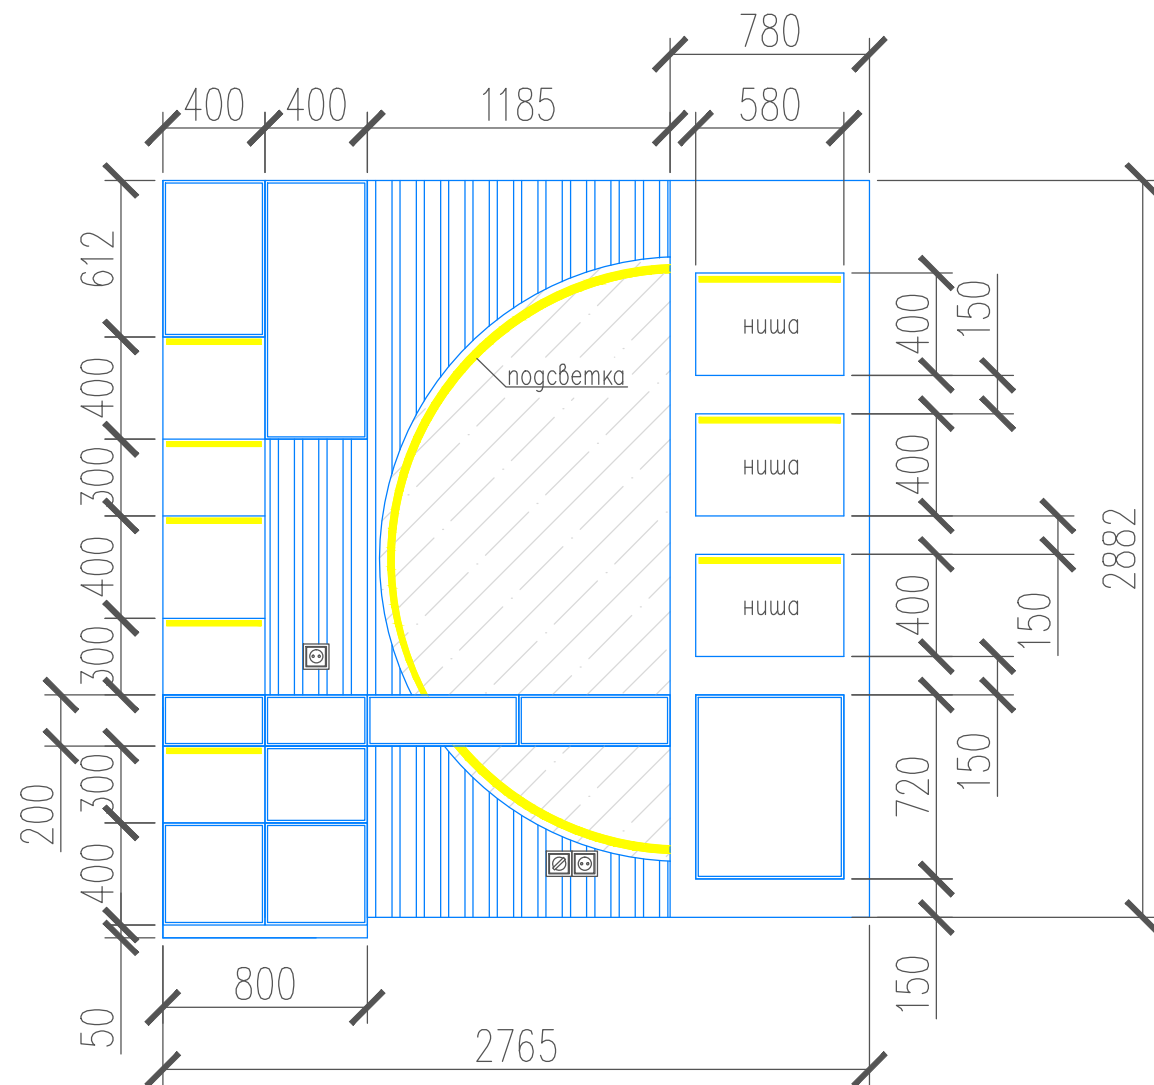

Глубина стеллажа и консоли—300мм
Глубина встроенного шкафчика и ниш—250мм

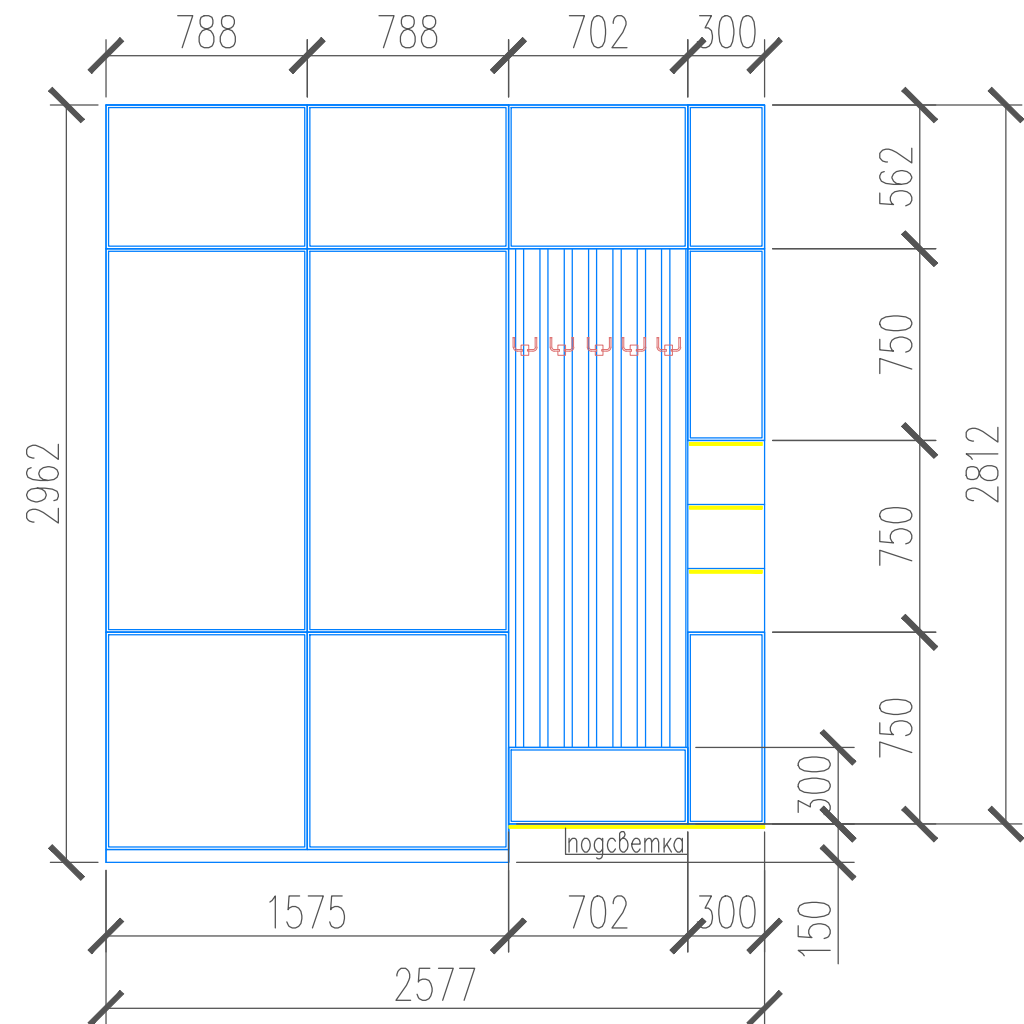


Глубина всех секций – 600мм


					Дизайнер Ларенкова Елена +7(926) 135–23–40 foxnn2000@yandex.ru			
Изм	Лист	докум	Подп	Дата				
Разраб.	Ларенкова Елена				Дизайн– проект интерьера квартиры 91,3м.кв	Стация	Лист	Листов
Пров.						РП	24	
Т. контр.								
					Габариты мебели. Прихожая–холл			
Н. контр.								
Умб								

Габариты мебели. Кухня– гостиная

Кухонный гарнитур

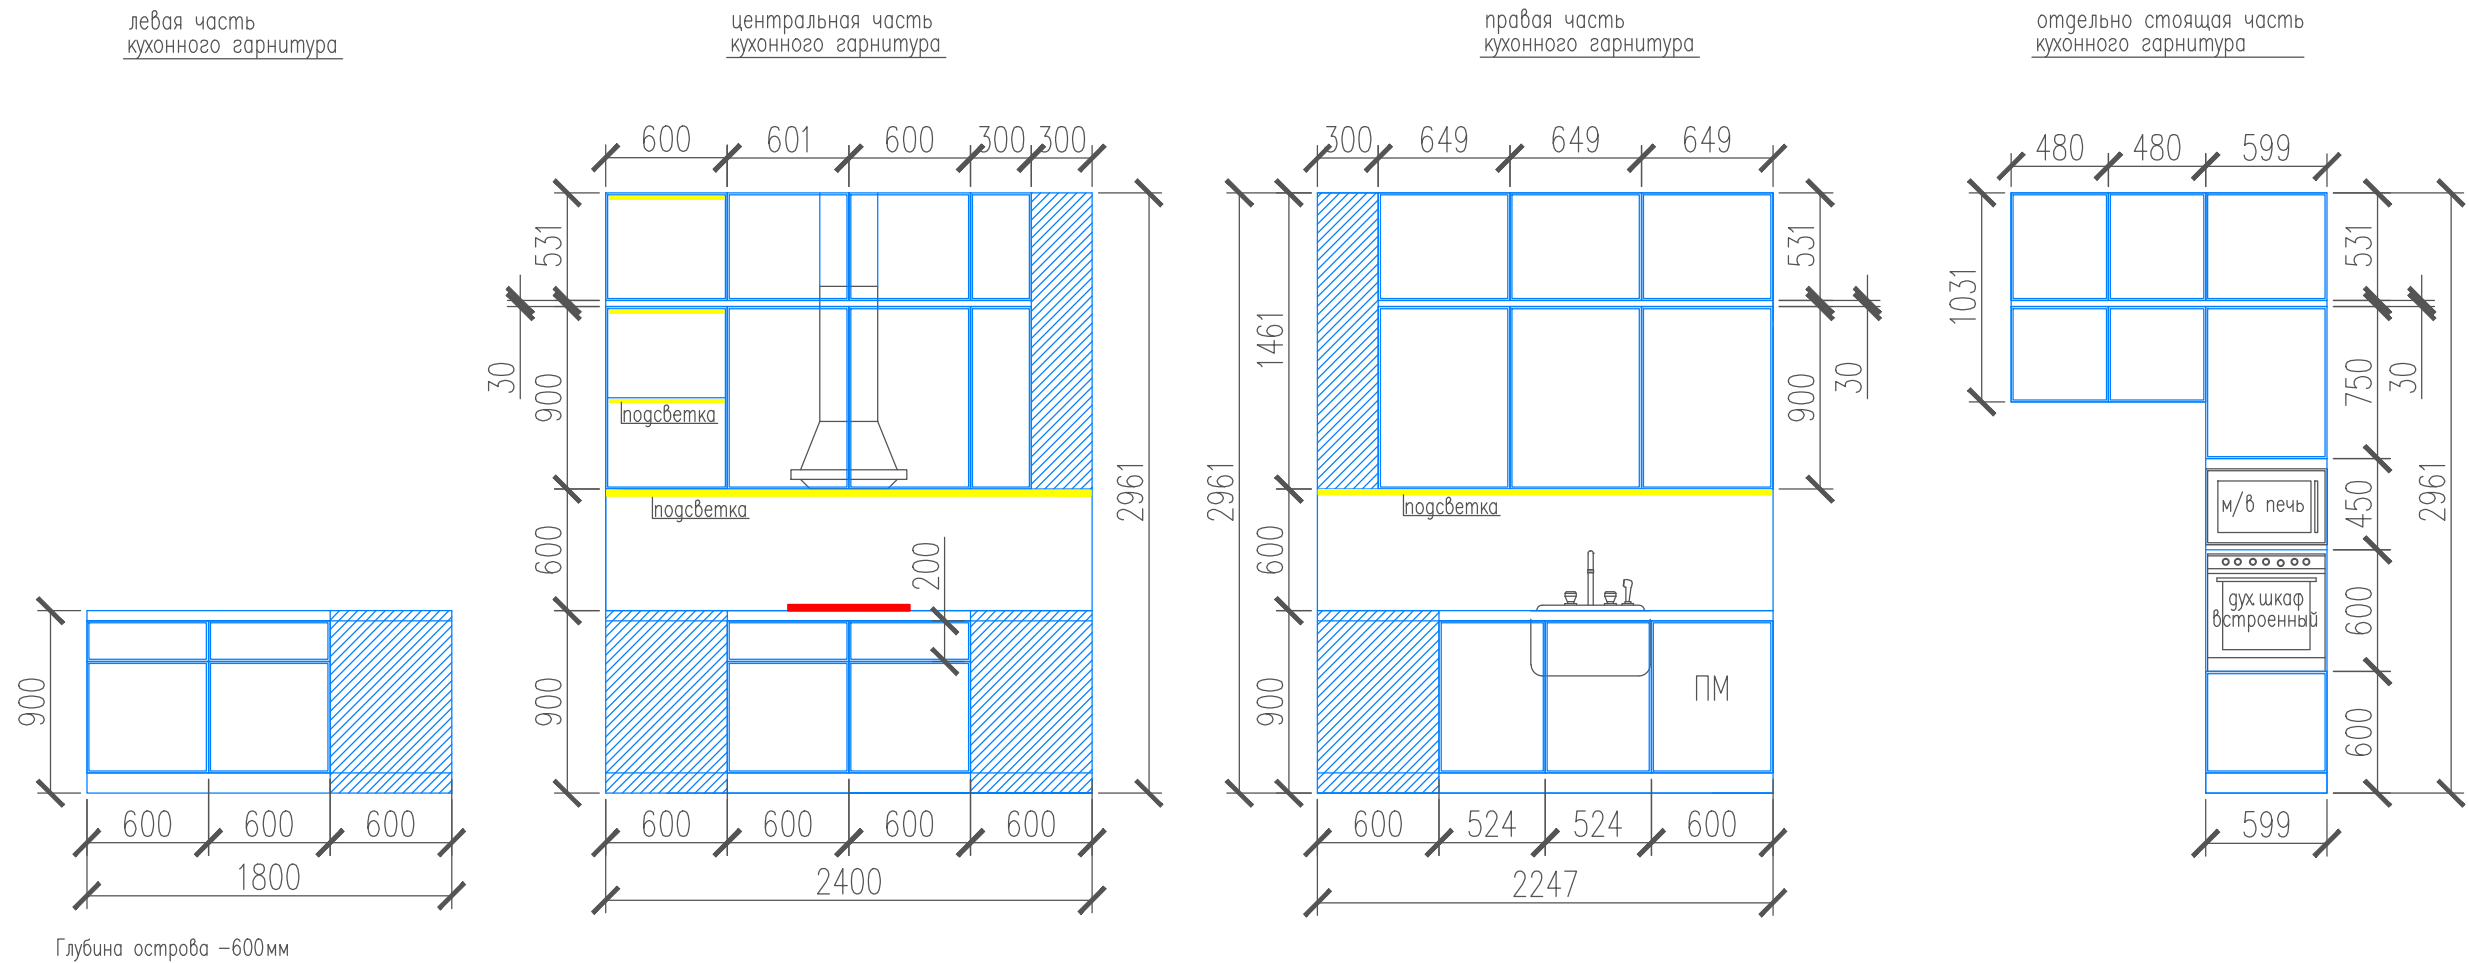

Зона ТВ в гостиной

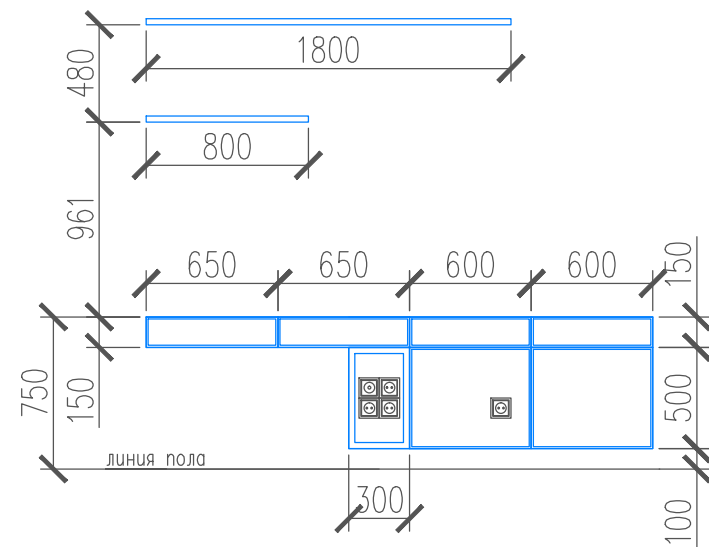





Полка над диваном



Ширина полки-200...250мм


Изм.	Лист	докум	Подп	Дата	Дизайнер Ларенкова Елена			
Разраб.	Ларенкова Елена				+7(926) 135-23-40			
Пров.					foxnn2000@yandex.ru			
Т.контр.					Дизайн- проект интерьера квартиры 91,3м.кв		Стадия	Лист
							РП	25
Н.контр.					Габариты мебели. Кухня– гостиная			
Умв.								

Габариты мебели. Спальня 1

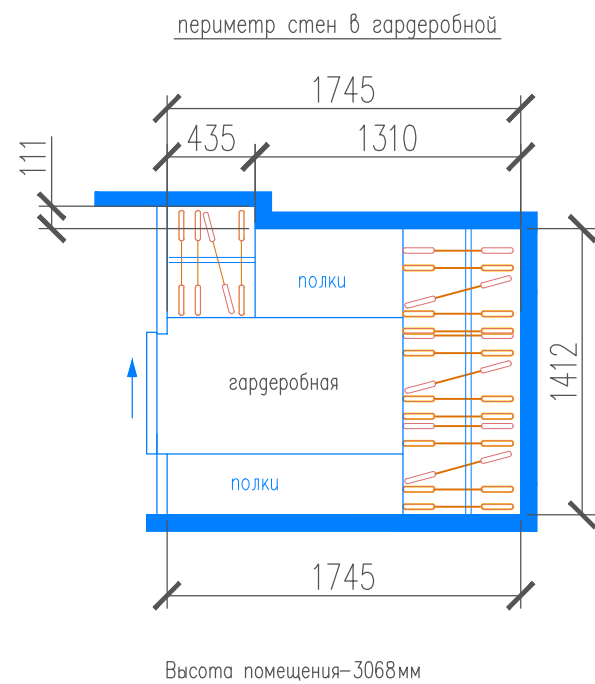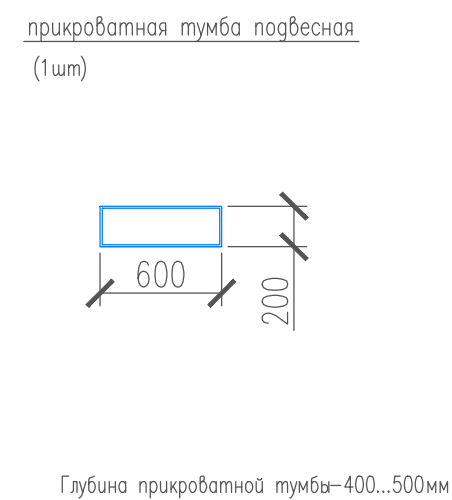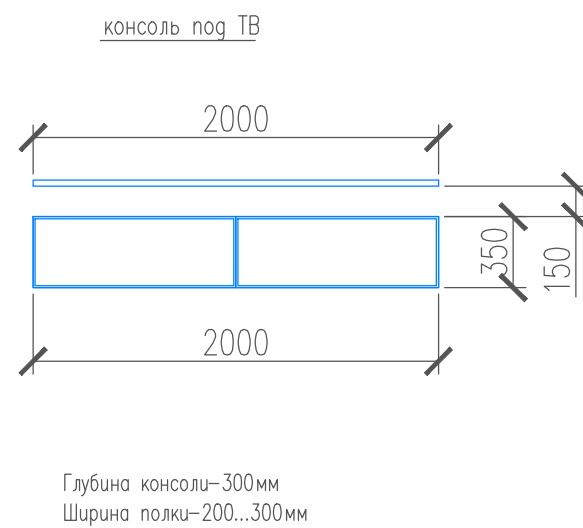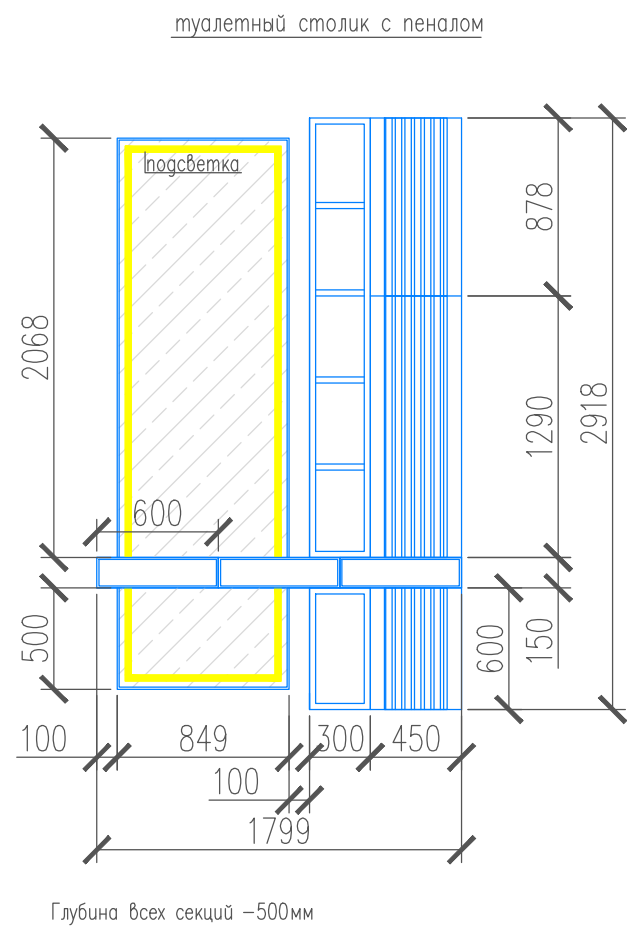


					Дизайнер Ларенкова Елена +7(926) 135–23–40 foxnn2000@yandex.ru			
Изм	Лист	докум	Подп	Дата				
Разраб.	Ларенкова Елена				Дизайн– проект интерьера квартиры 91,3м.кв	Стадия	Лист	Листов
Пров.						РП	26	
Т.контр.								
					Габариты мебели. Спальня 1			
Н.контр.								
Утв.								


Габариты мебели. Спальня 2

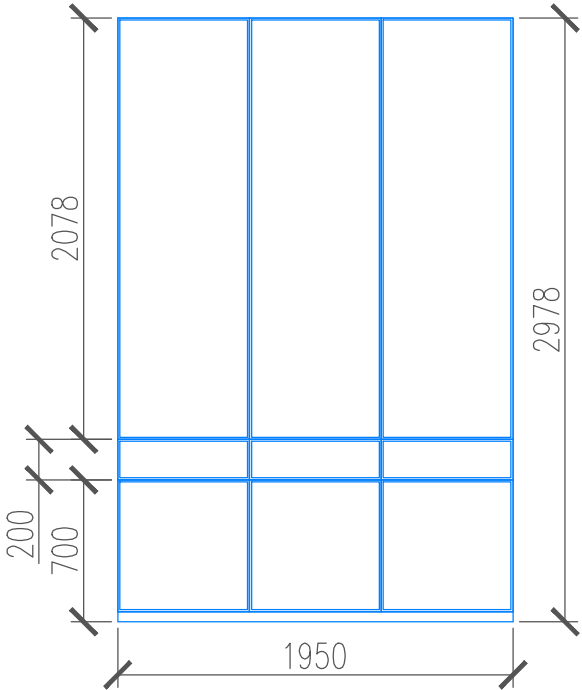


Глубина шкафа –600мм

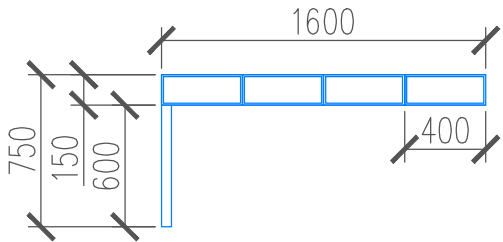


Ширина стола –600мм

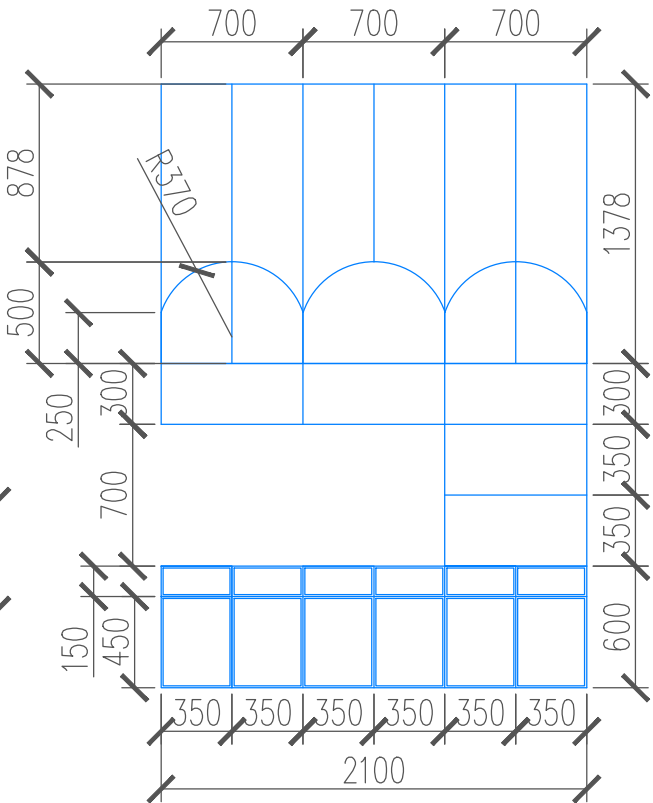

Глубина всех секций –400мм

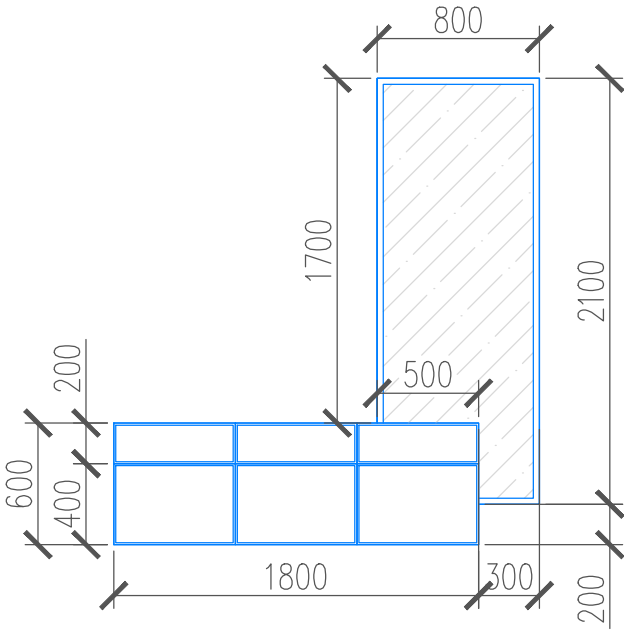


Глубина подвесной консоли –400мм

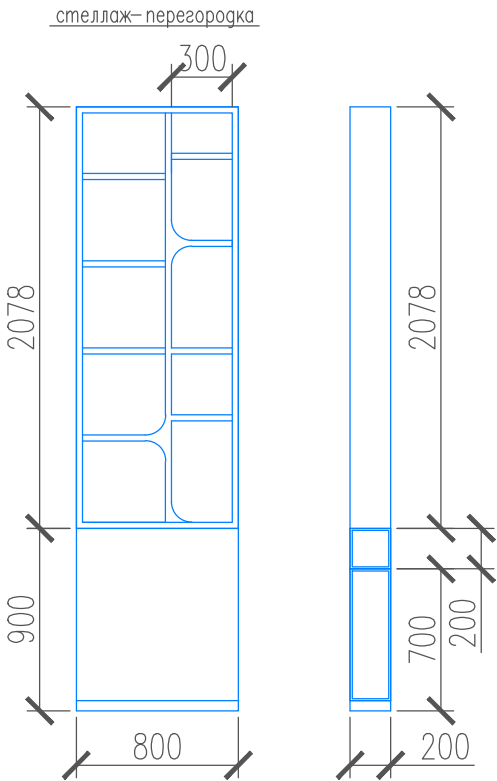


Изм.	Лист	докум	Подп	Дата	Дизайнер Ларенкова Елена			
Разраб.	Ларенкова Елена				+7(926) 135-23-40			
Пров.					foxnn2000@yandex.ru			
Т.контр.					Дизайн- проект интерьера			
Н.контр.					квартиры 91,3м.кв			
Утв.					Габариты мебели. Спальня 2			
					Стадия	Лист	Листов	
					РП	27		

Габариты мебели. Санузел 1,2

Санузел 1

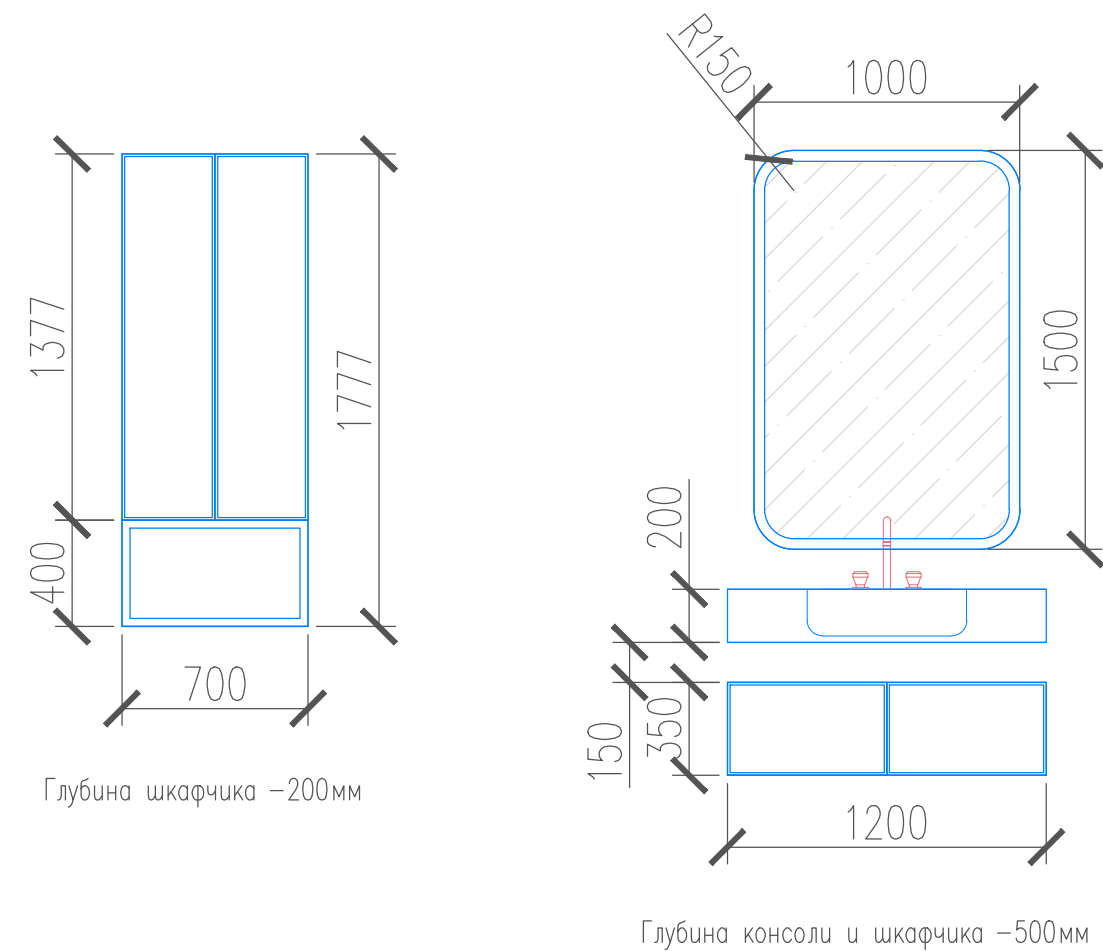

Санузел 2

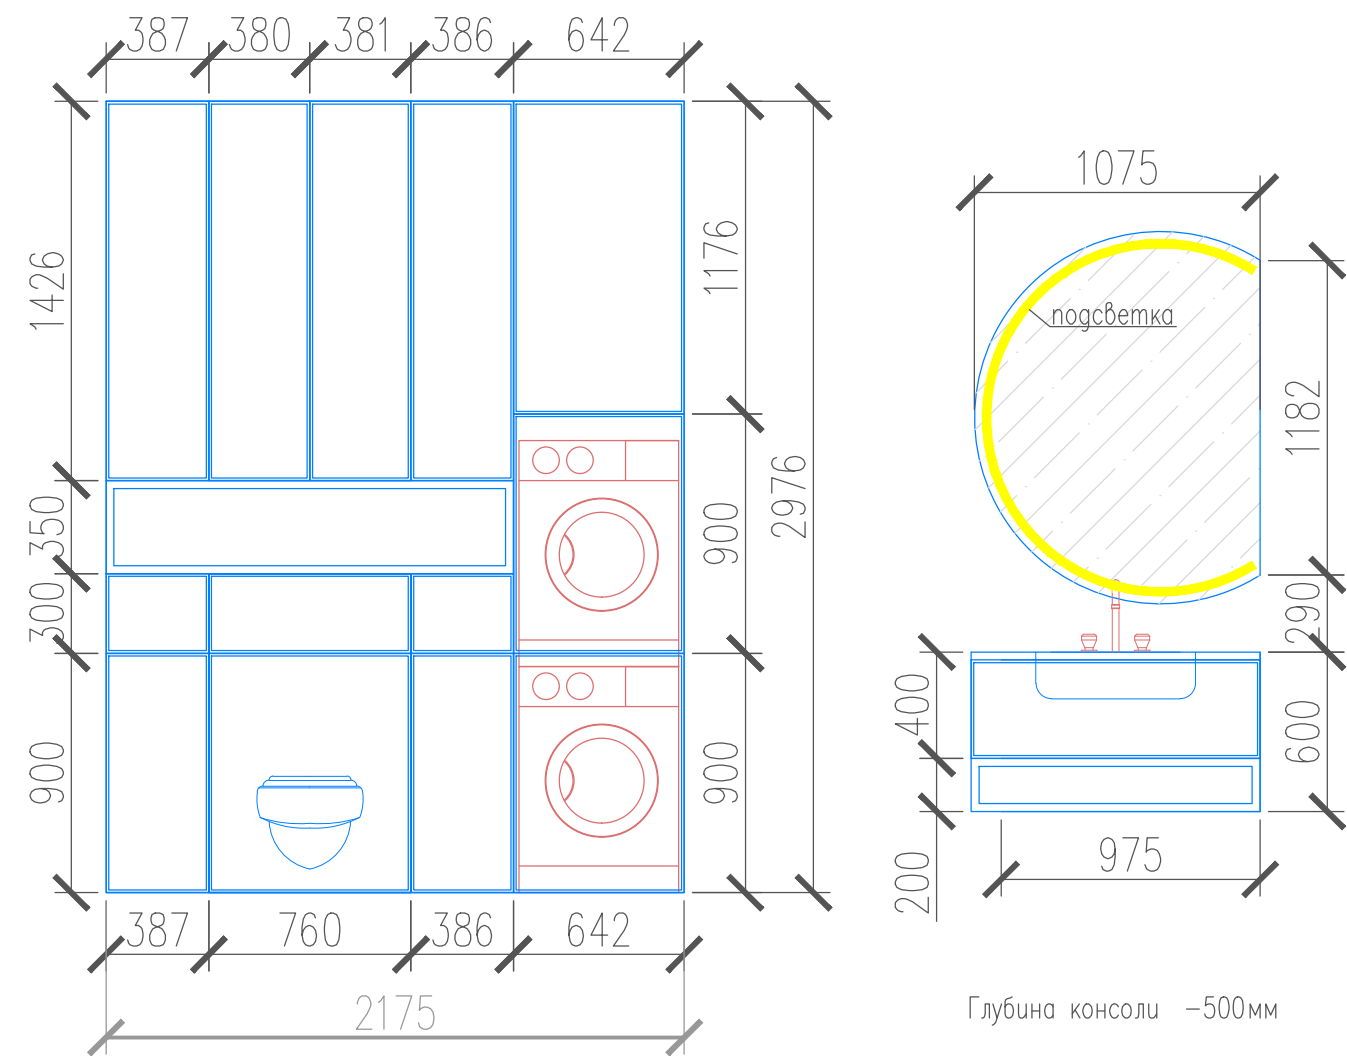



Глубина секции со ст. и суш.машинами -743мм
Глубина секций с инсталляцией -200мм

					Дизайнер Ларенкова Елена			
					+7(926) 135-23-40			
					foxnn2000@yandex.ru			
Изм.	Лист	докум	Подп.	Дата	Дизайн- проект интерьера квартиры 91,3м.кв		Стадия	Лист
Разраб.	Ларенкова Елена						РП	28
Пров.								
Т.контр.								
Н.контр.					Габариты мебели. Санузел 1,2			
Умв.								



Ведомость отделочных материалов


Ведомость отделочных материалов							
Помещение	Пол		Потолок		Стены		Примечание
	Наименование	Кол-во	Наименование	Кол-во	Наименование	Кол-во	
Прихожая-холл	Керамогранит	7,1 м.кв	ГКЛ+ покраска	10,2 м.кв	Под покраску	29,5 м.кв	
	Supernova Stoun Atlas Concord				Sherwin-Williams		
	Паркетная доска	3,5 м.кв			apm.SW7563 Restfull White		
	Galathea американский орех селект лак Select				Плинтус полиуретановый	6,8 пог/м	
Кухня-гостиная	Керамогранит	5,4 м.кв	ГКЛ+ покраска	27,4 м.кв	Под покраску	47,4 м.кв	
	Supernova Stoun Atlas Concord				Sherwin-Williams		
	Паркетная доска	21,4 м.кв			apm.SW7563 Restfull White		
	Galathea американский орех селект лак Select				Плинтус полиуретановый	15,6 пог/м	
					apm.SX195 Orac Decor		
					Фреска		
					Re-Space Affresco apm.JK-43 col.1	8,2 м.кв	
					Латунный молдинг (ширина 30мм)	12 пог/м	
Спальня 1	Паркетная доска	19,3 м.кв	ГКЛ+ покраска	1,1 м.кв	Под покраску	31,8 м.кв	
	Galathea американский орех селект лак Select		Существующий потолок (штукатурка+ покраска)	2,4 м.кв	Sherwin-Williams		
			Натяжной потолок (белый матовый)	15,8 м.кв	apm.SW8917 Shell White		
					Плинтус полиуретановый	15,4 пог/м	
					apm.SX195 Orac Decor		
					Фотообои	8,9 м.кв	
					Wall-street apm.24376 fezalis1		
					Под покраску	2,82 м.кв	
Спальня 2	Паркетная доска	22,4 м.кв	Натяжной потолок (белый матовый)	21,3 м.кв	Sherwin-Williams		
	Galathea американский орех селект лак Select				apm.SW6359 Sociable		
					Монтаж св/диодной ленты в стену	6 пог/м	
					Под покраску	32,5 м.кв	
Санузел 1	Керамогранит	5 м.кв	Натяжной потолок (белый матовый)	4,9 м.кв	Sherwin-Williams		
	Rex Reves de Rex Choco Glossy Rett				apm.SW6056 Polite White		
					Плинтус полиуретановый	14,2 пог/м	
					apm.SX195 Orac Decor		
Санузел 2	Керамогранит	5,8 м.кв	Натяжной потолок (белый матовый)	5,6 м.кв	Фотопечать на обоях	7,2 м.кв	
	Риальто Керама Марацци				Художественная роспись	8,4 м.кв	
	apm.SG634202R				Керамогранит	39,6 м.кв	
					Rex Reves de Rex		
					Perle Glossy		
					Noisette Glossy		
					Choco Glossy		
					Керамогранит	29,5 м.кв	
					Монте тиберио, Керама Марацци		
					apm.SG507102R лаппатированный		
					обрезной		

					Дизайнер Ларенкова Елена			
					+7(926) 135–23–40			
					foxnn2000@yandex.ru			
Изм	Лист	докум	Подп	Дата				
Разраб.	Ларенкова Елена				Дизайн– проект интерьера квартиры 91,3м.кв	Стадия	Лист	Листов
Пров.						РП	29	
Т.контр.								
					Ведомость отделочных материалов			
Н.контр.								
Умв.								

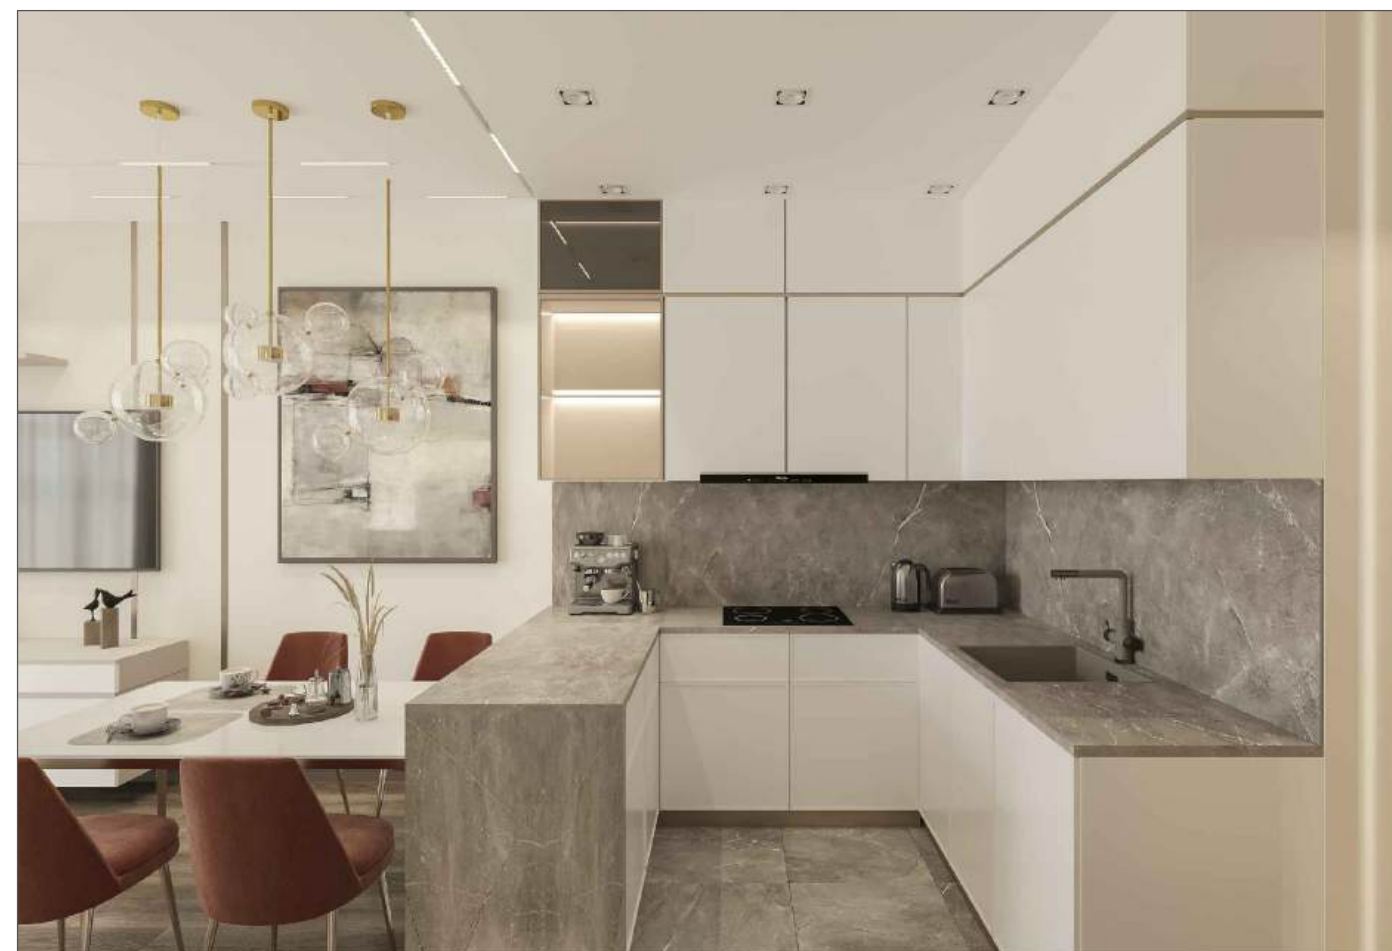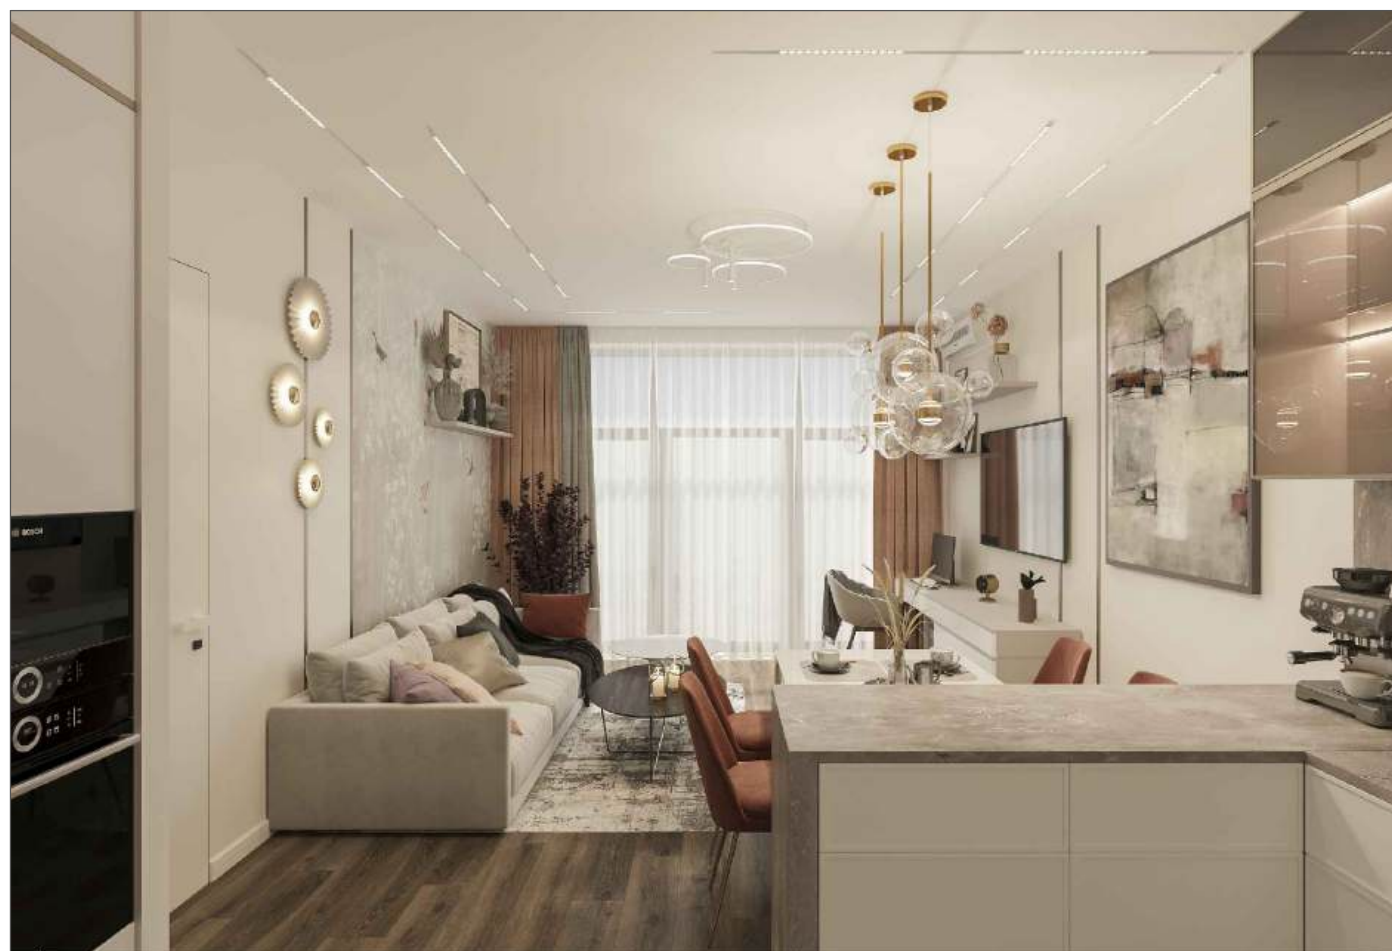





КУХНЯ—ГОСТИНАЯ

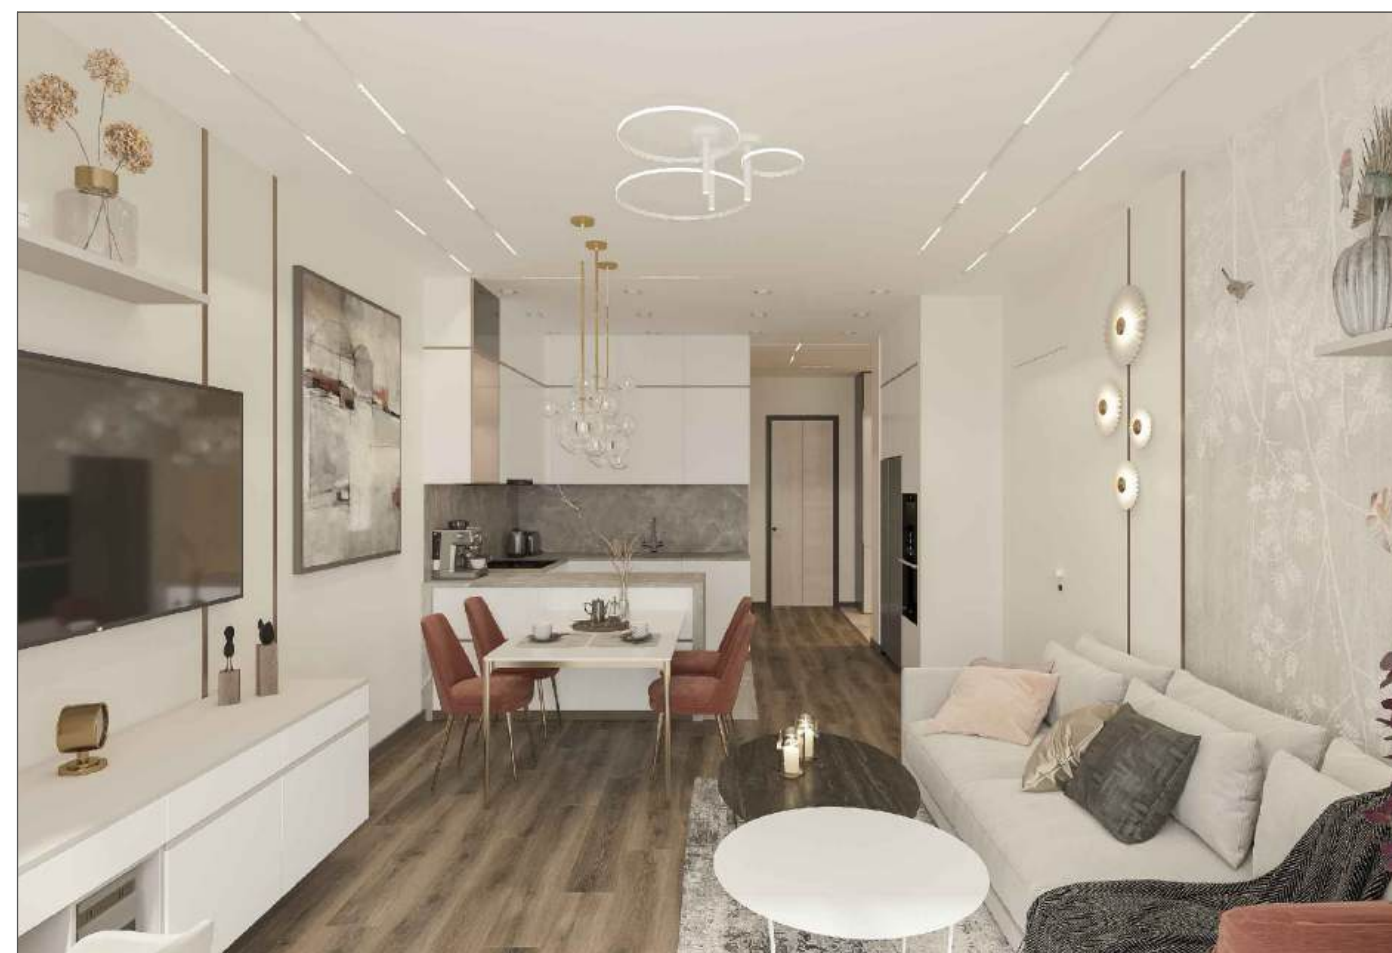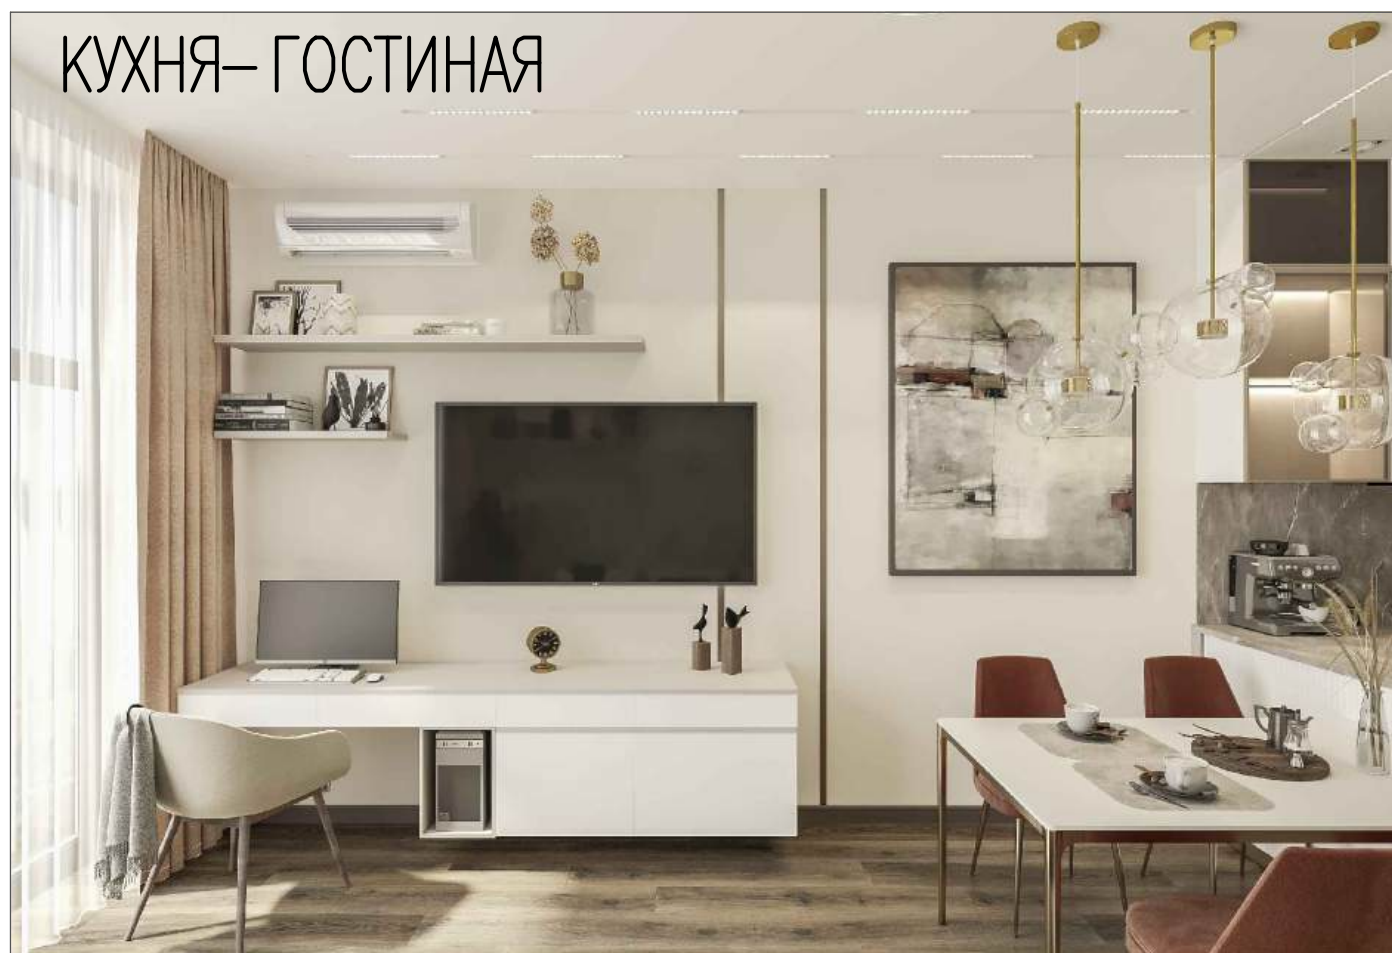

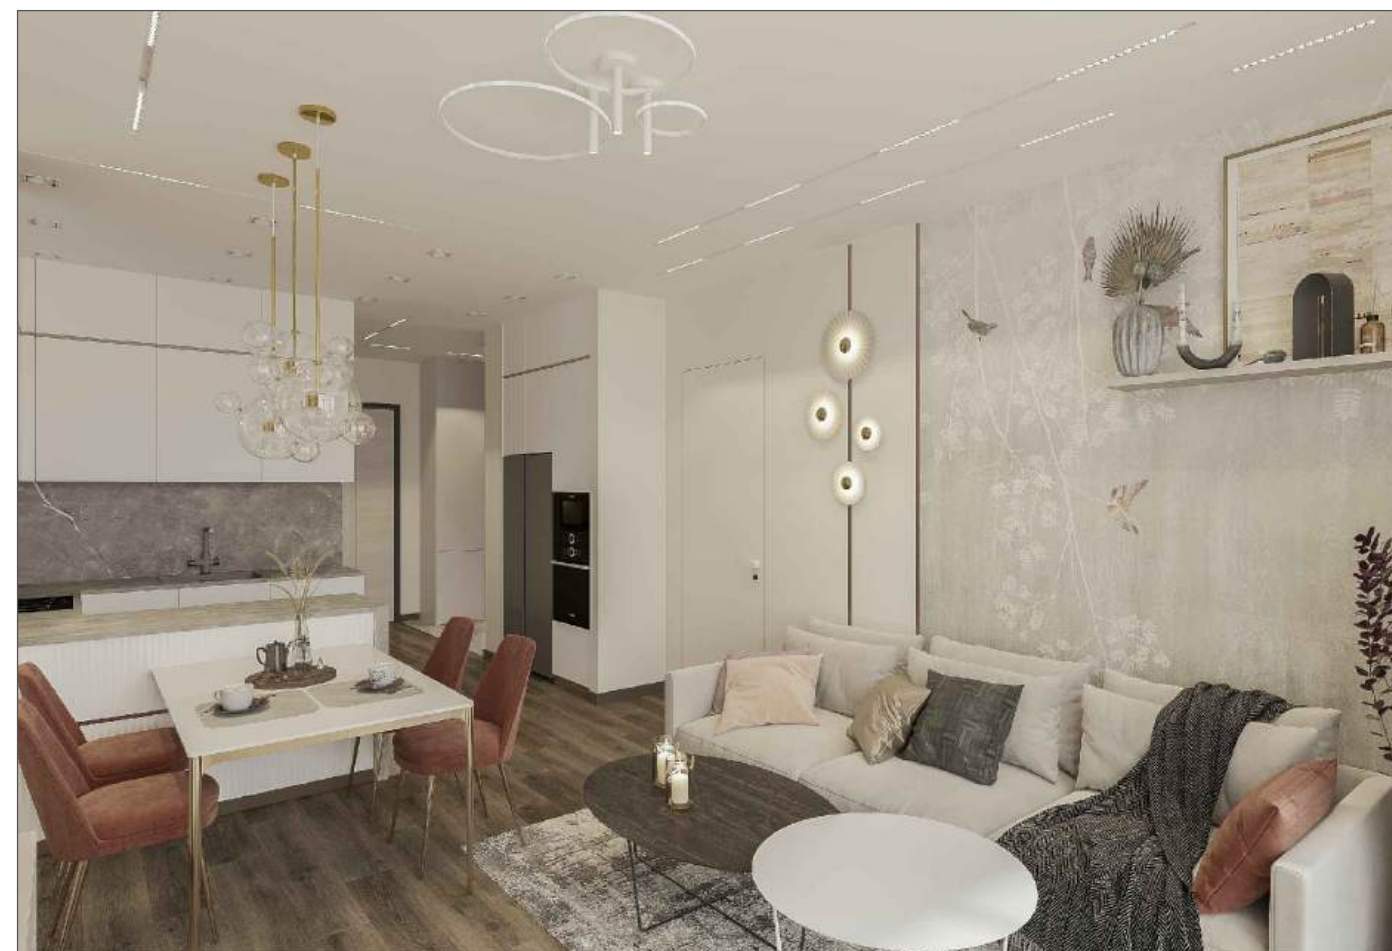




КУХНЯ—ГОСТИНАЯ



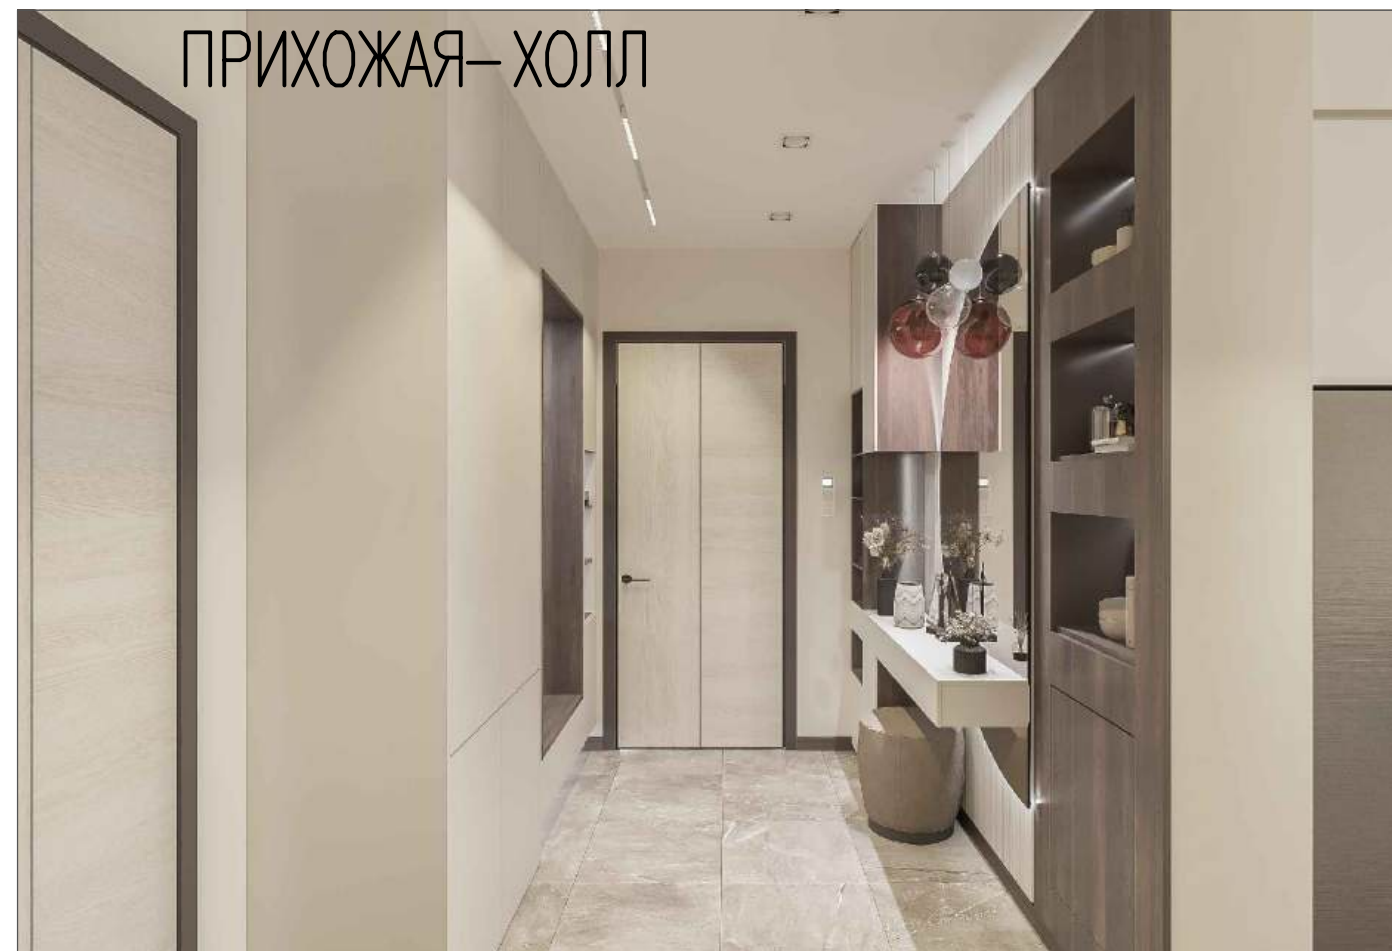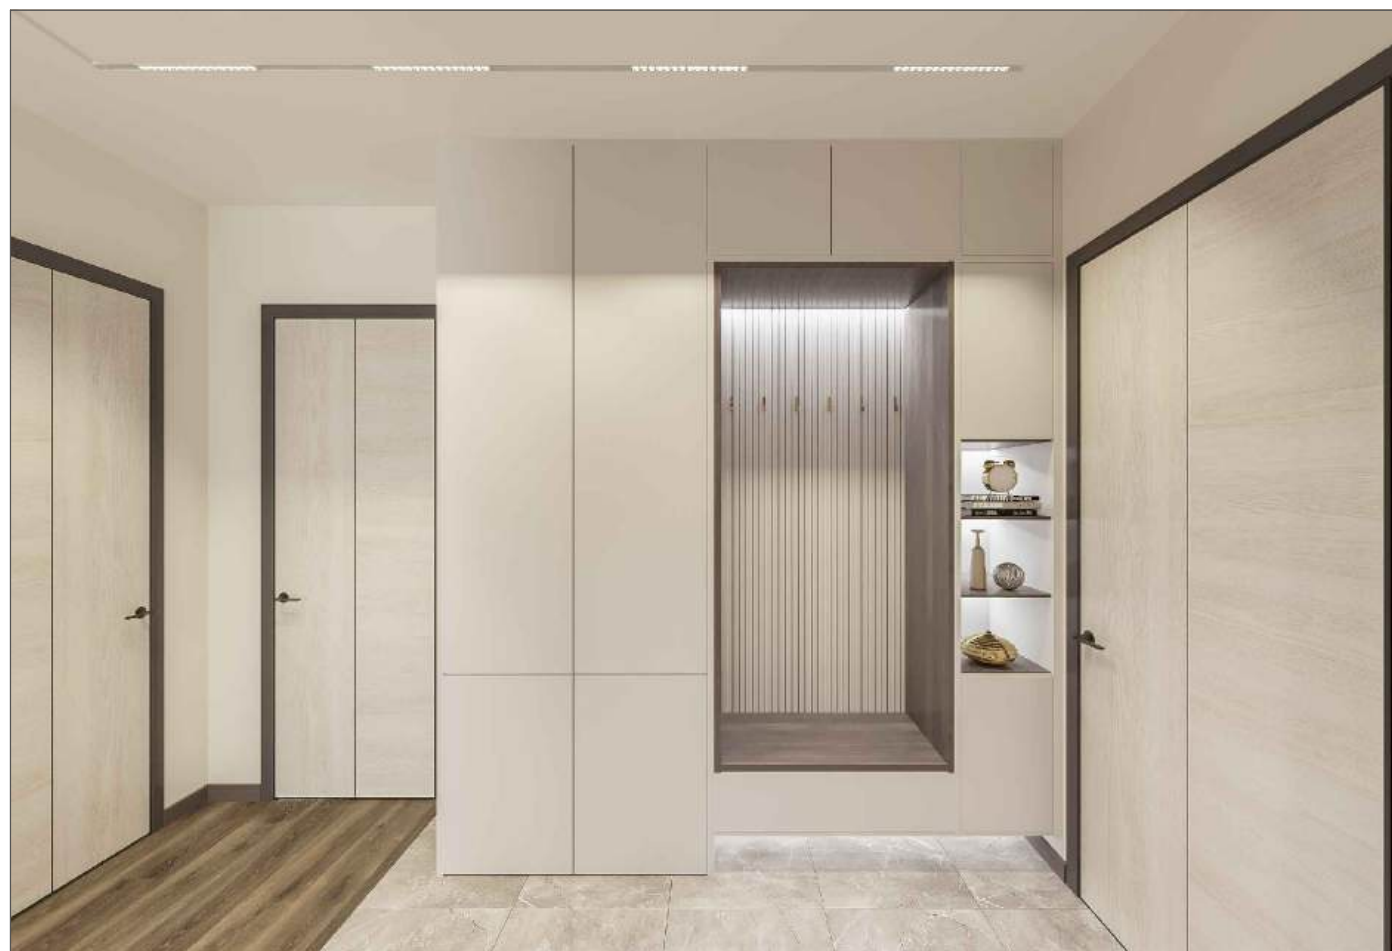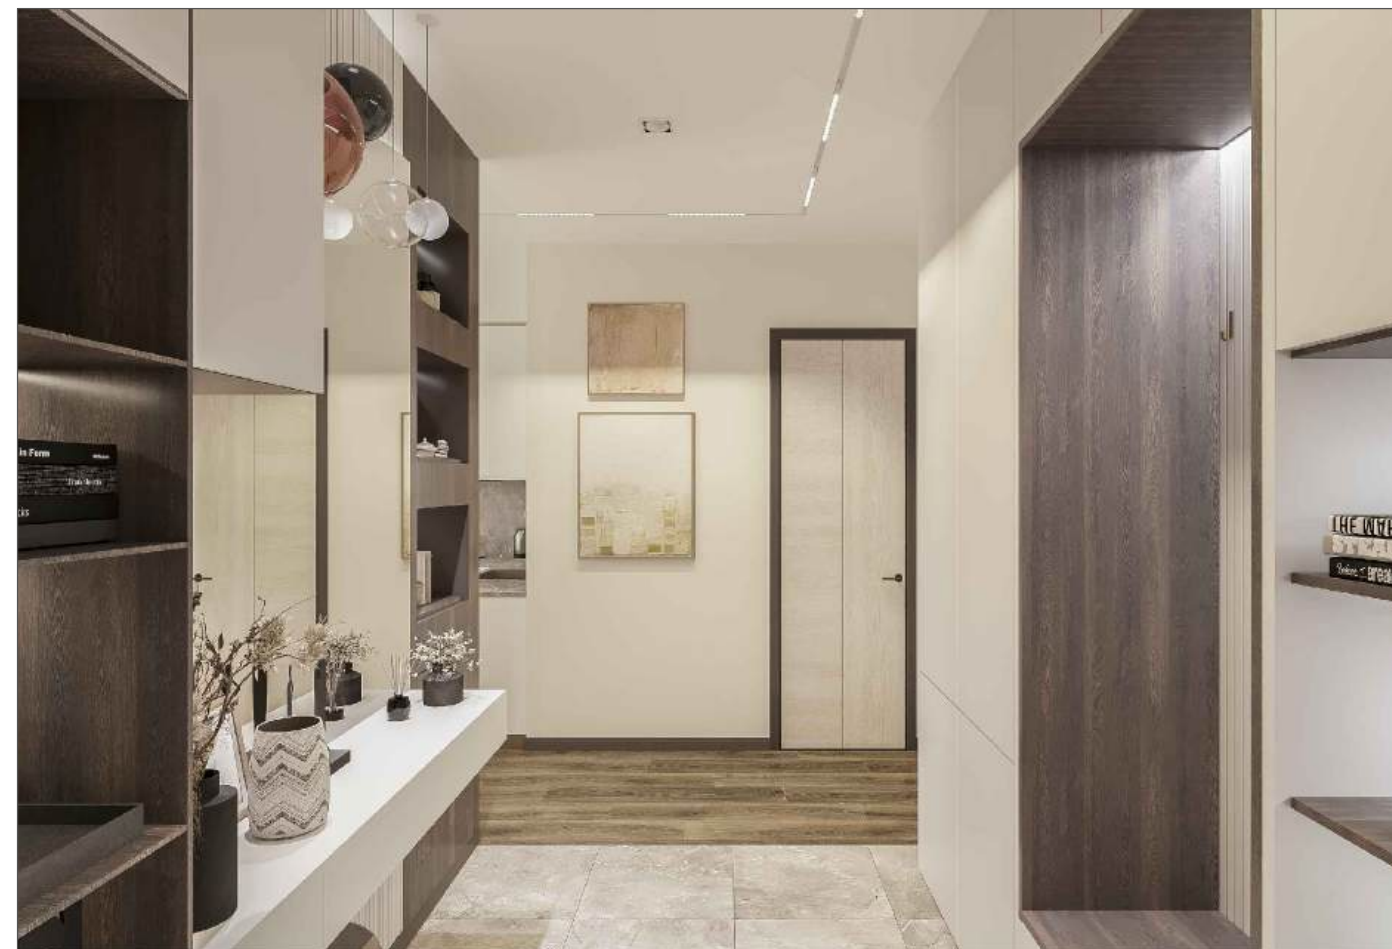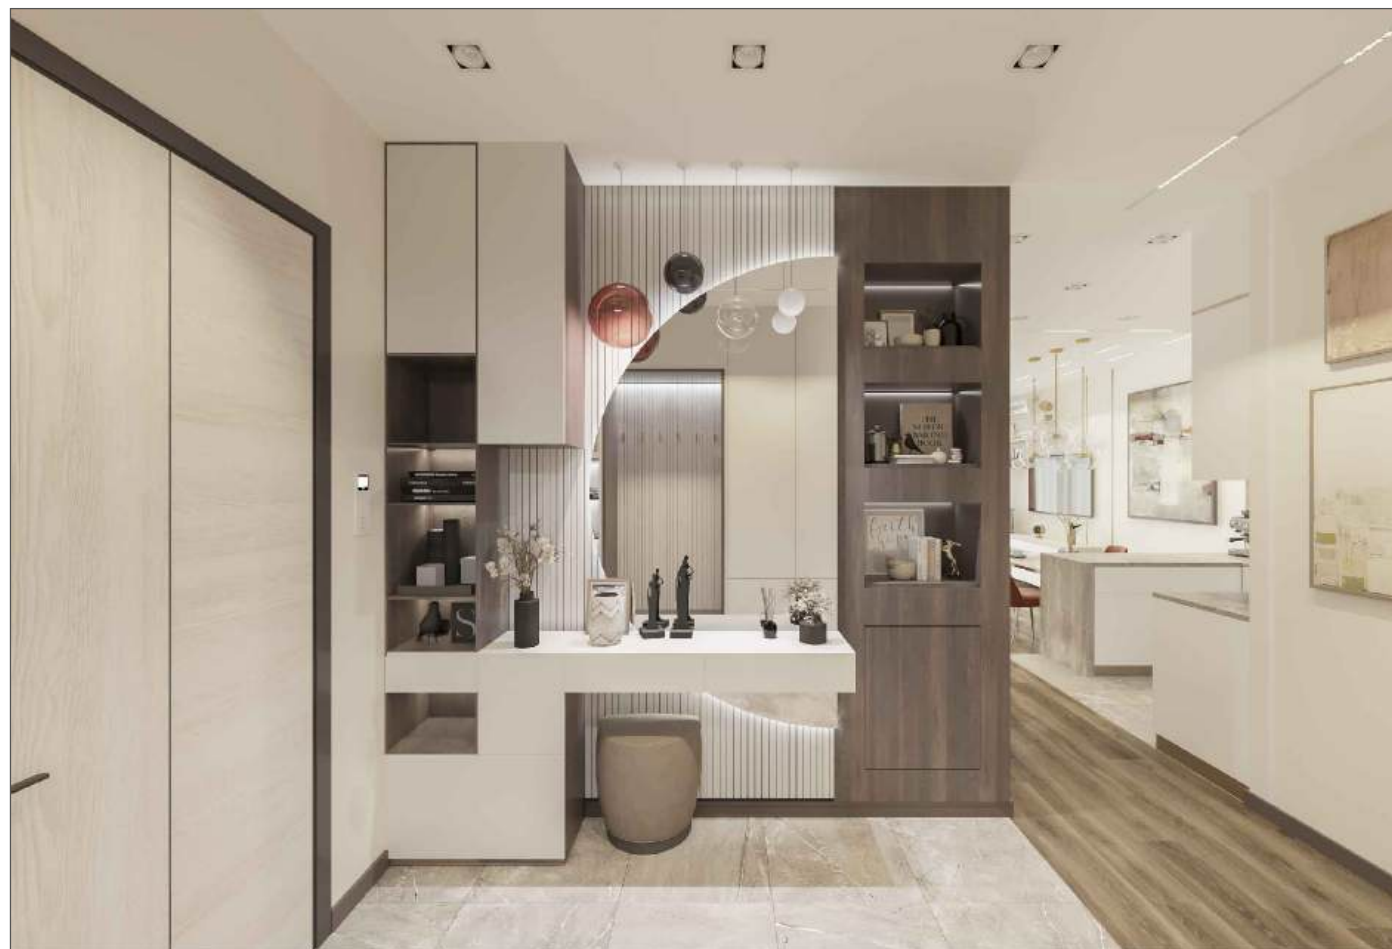



ПРИХОЖАЯ-ХОЛЛ

СПАЛЬНЯ 1

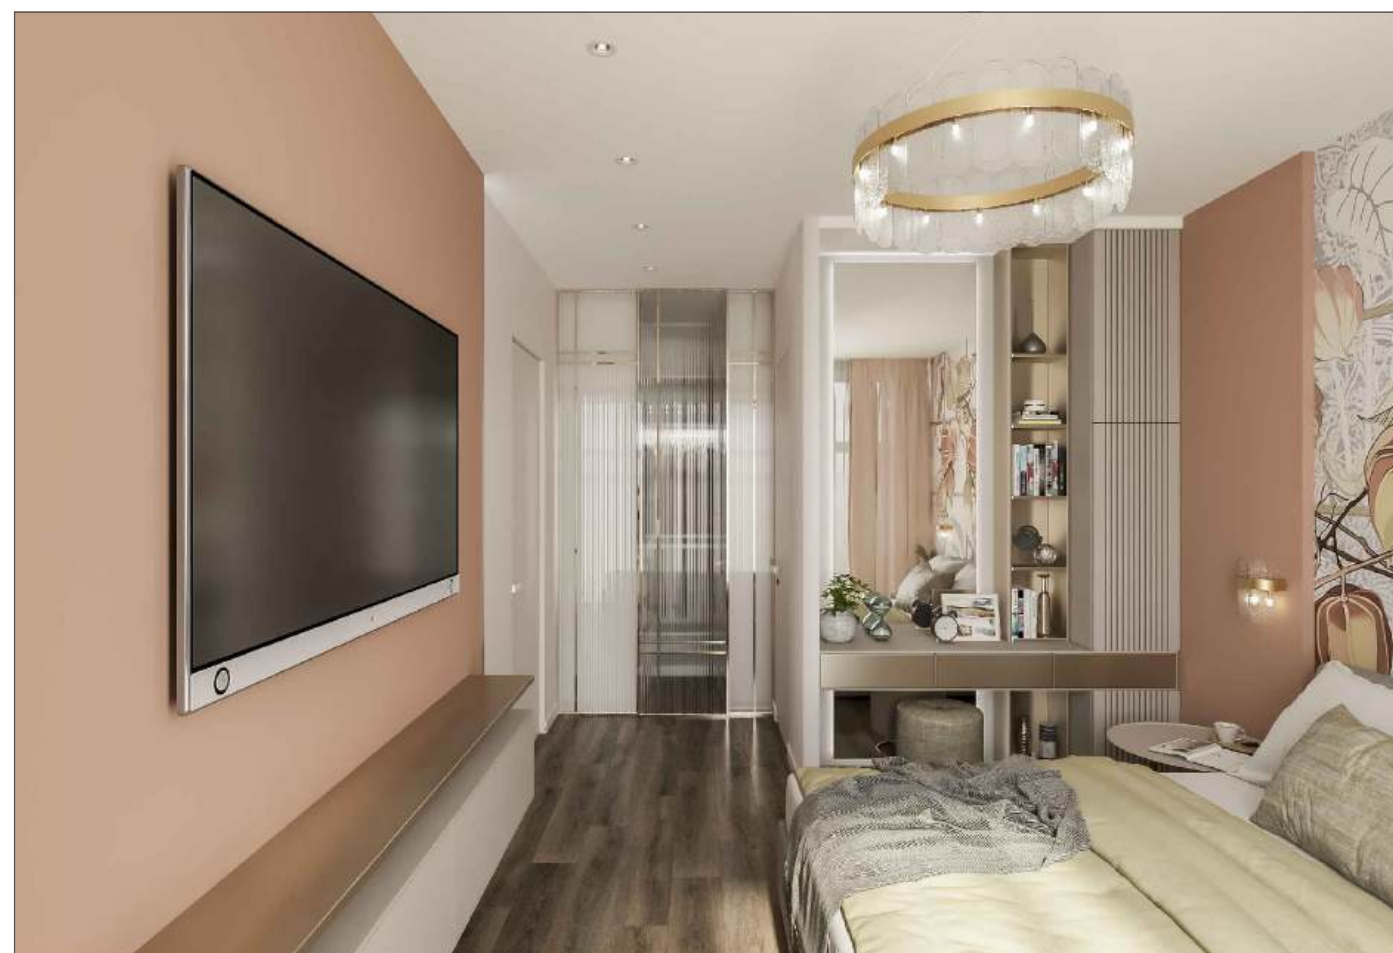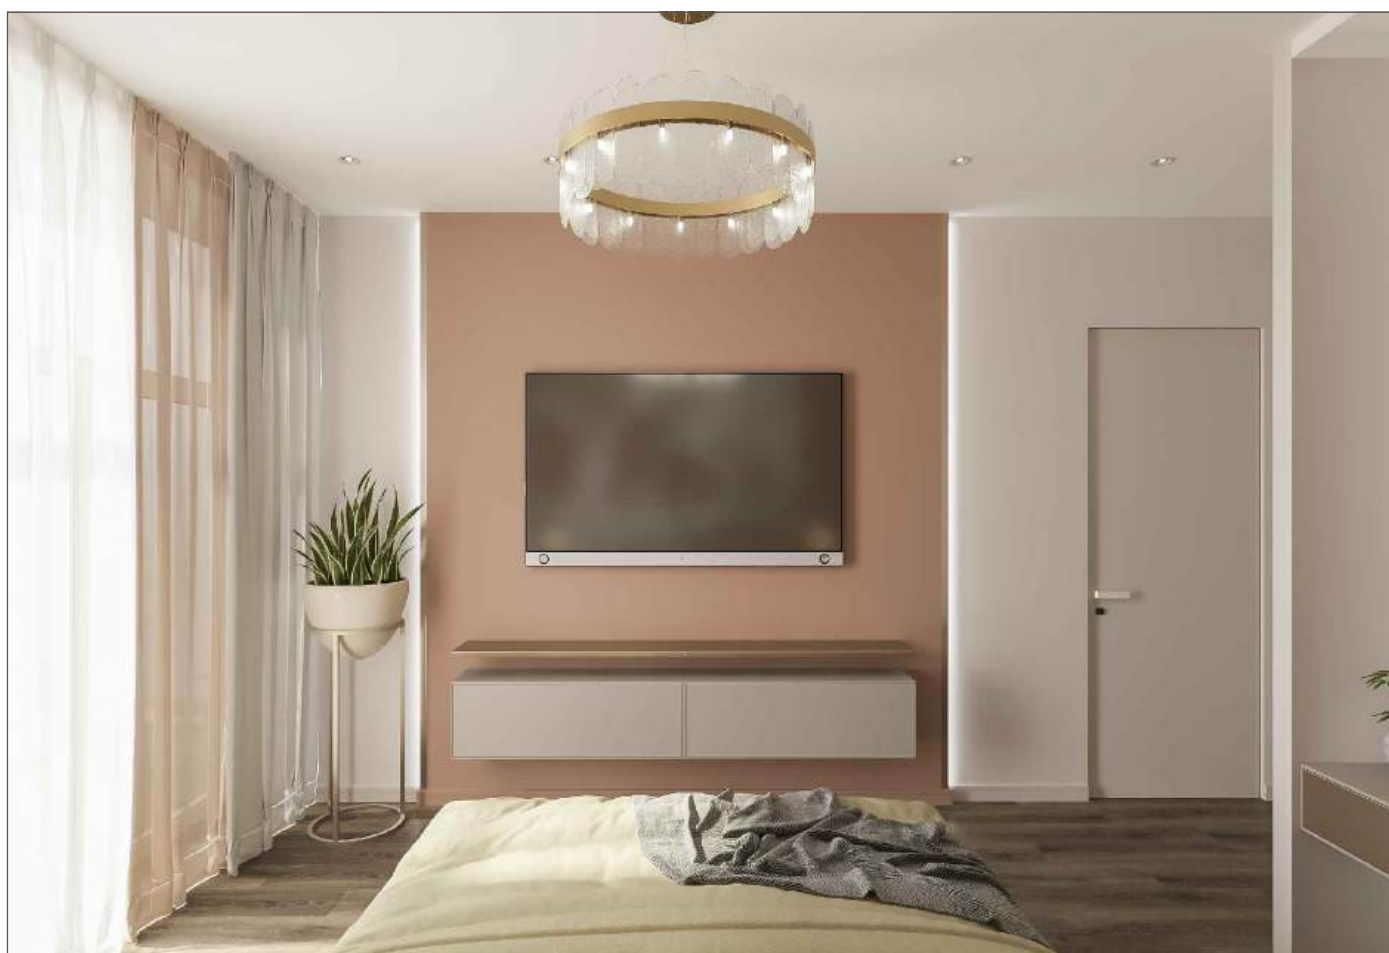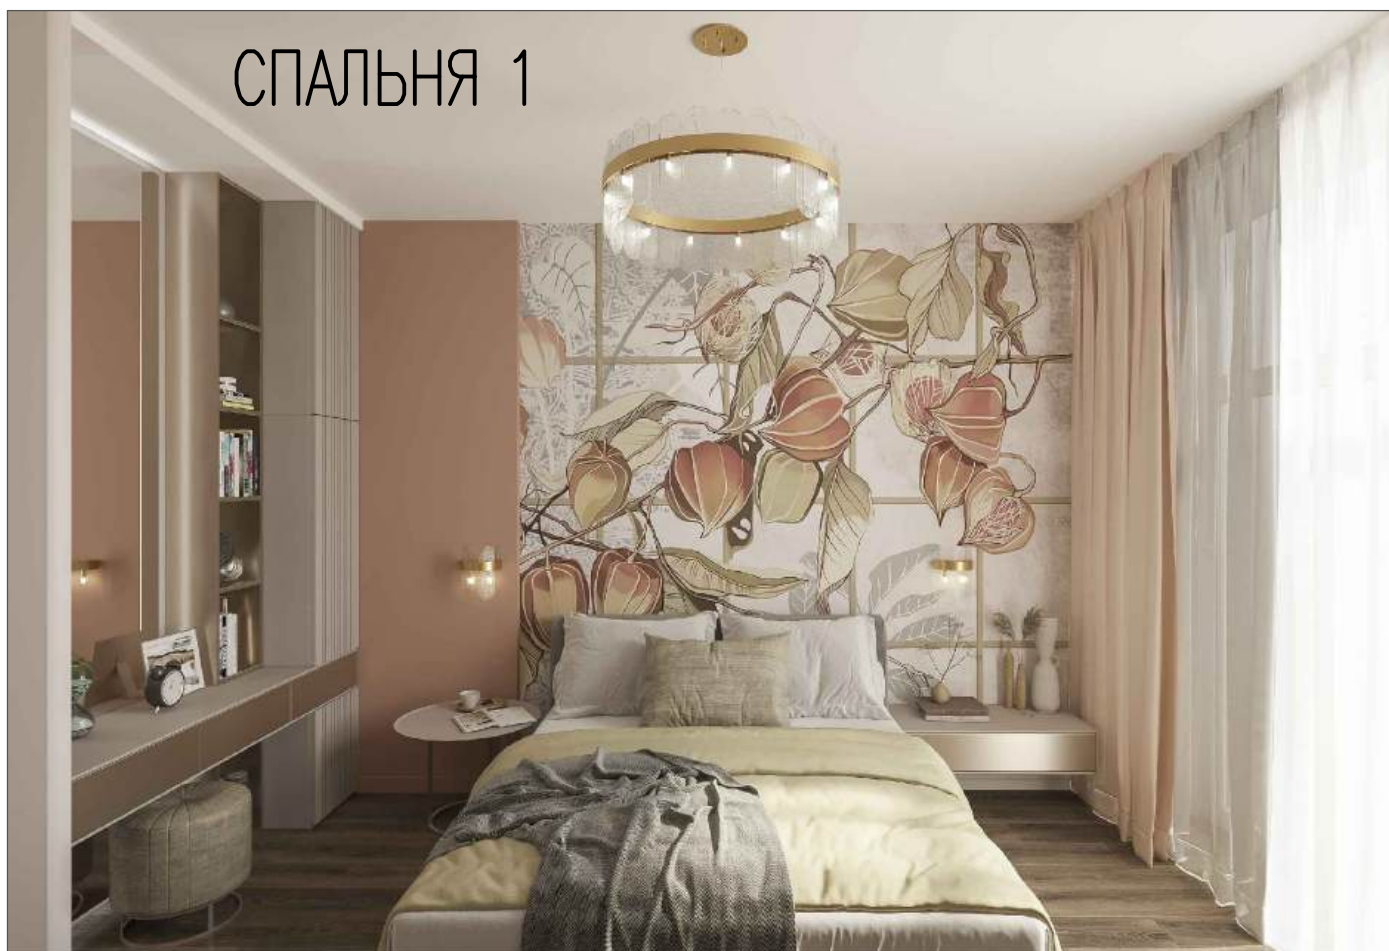






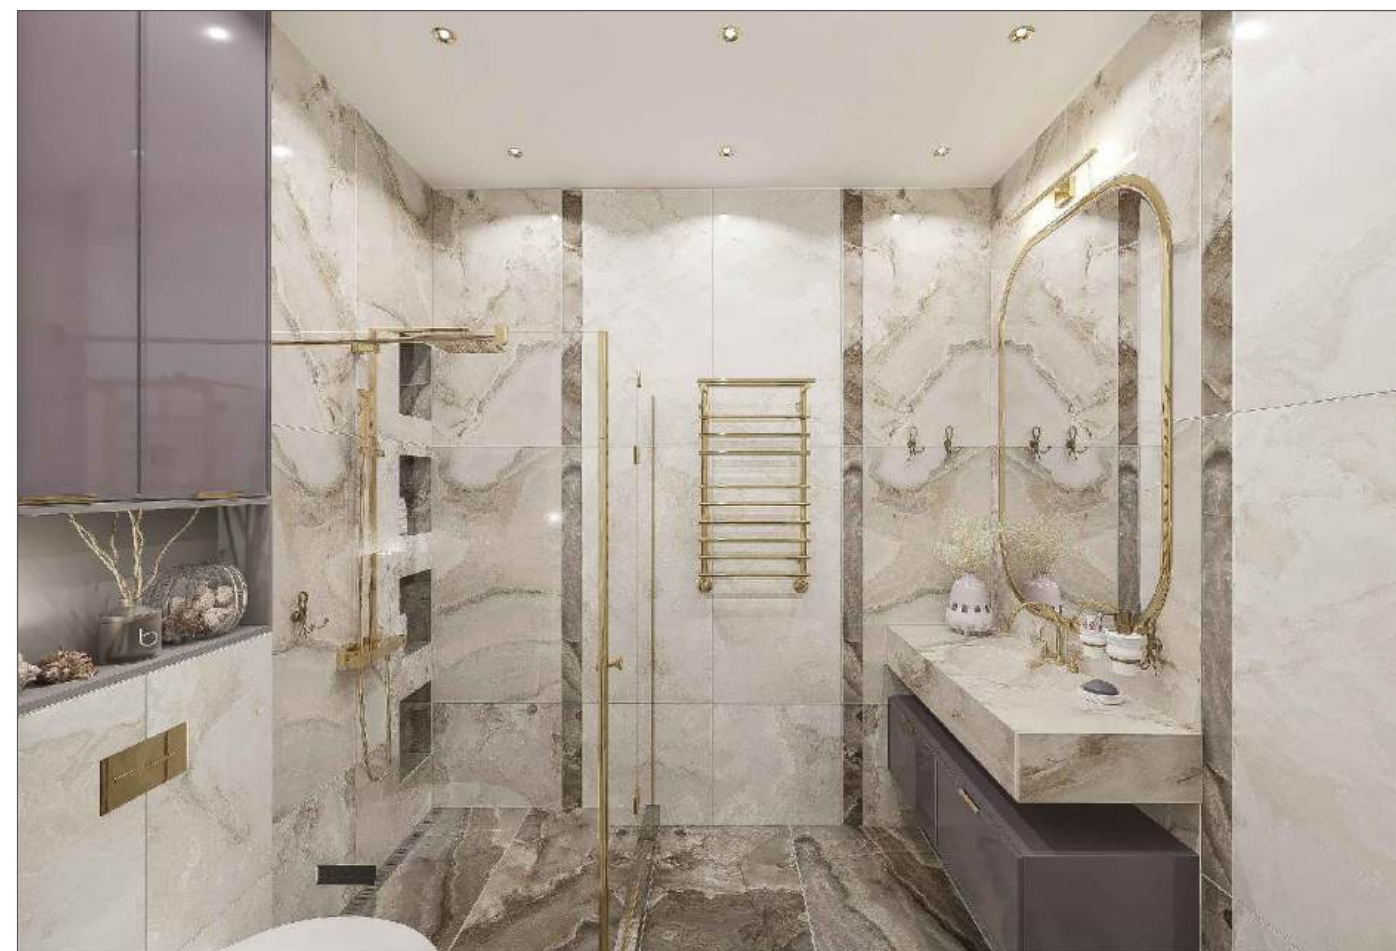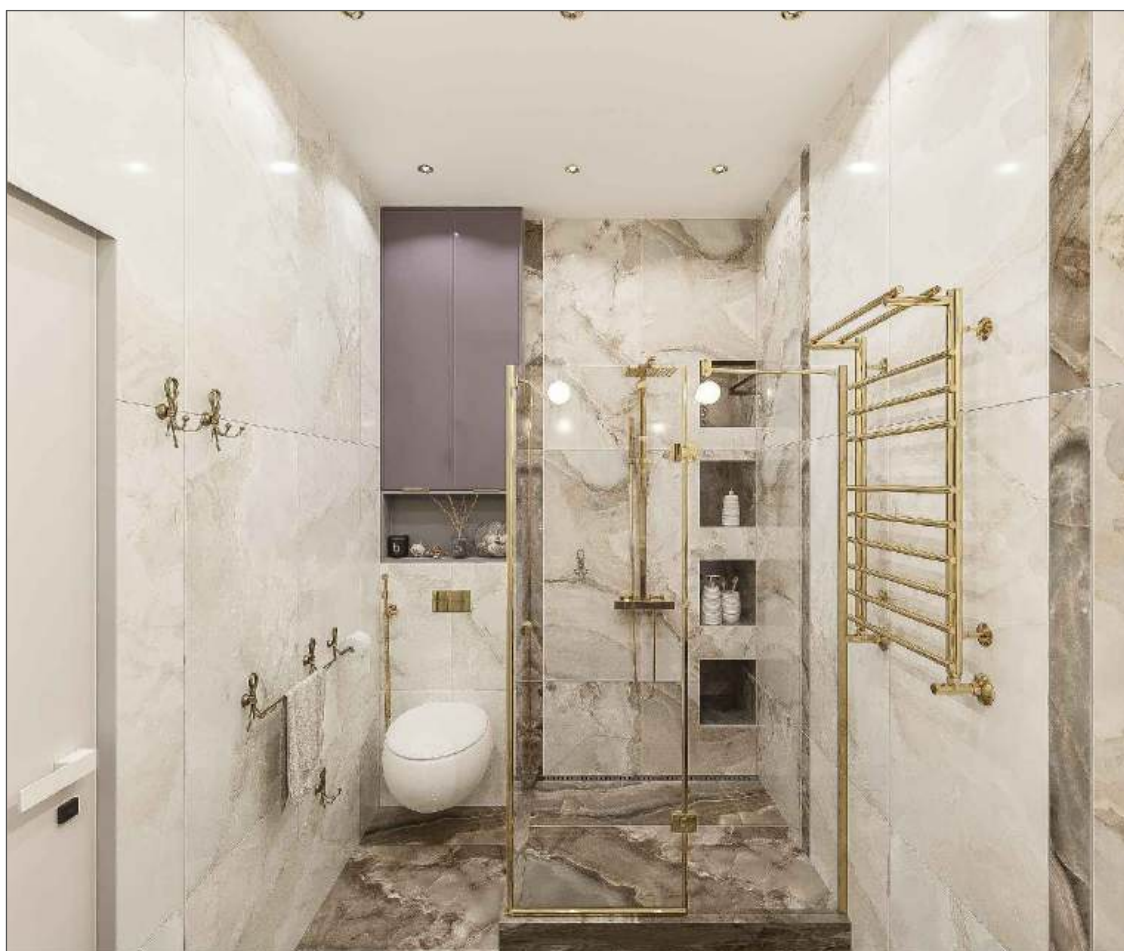

САНУЗЕЛ 1

САМУЗЕЛ 1

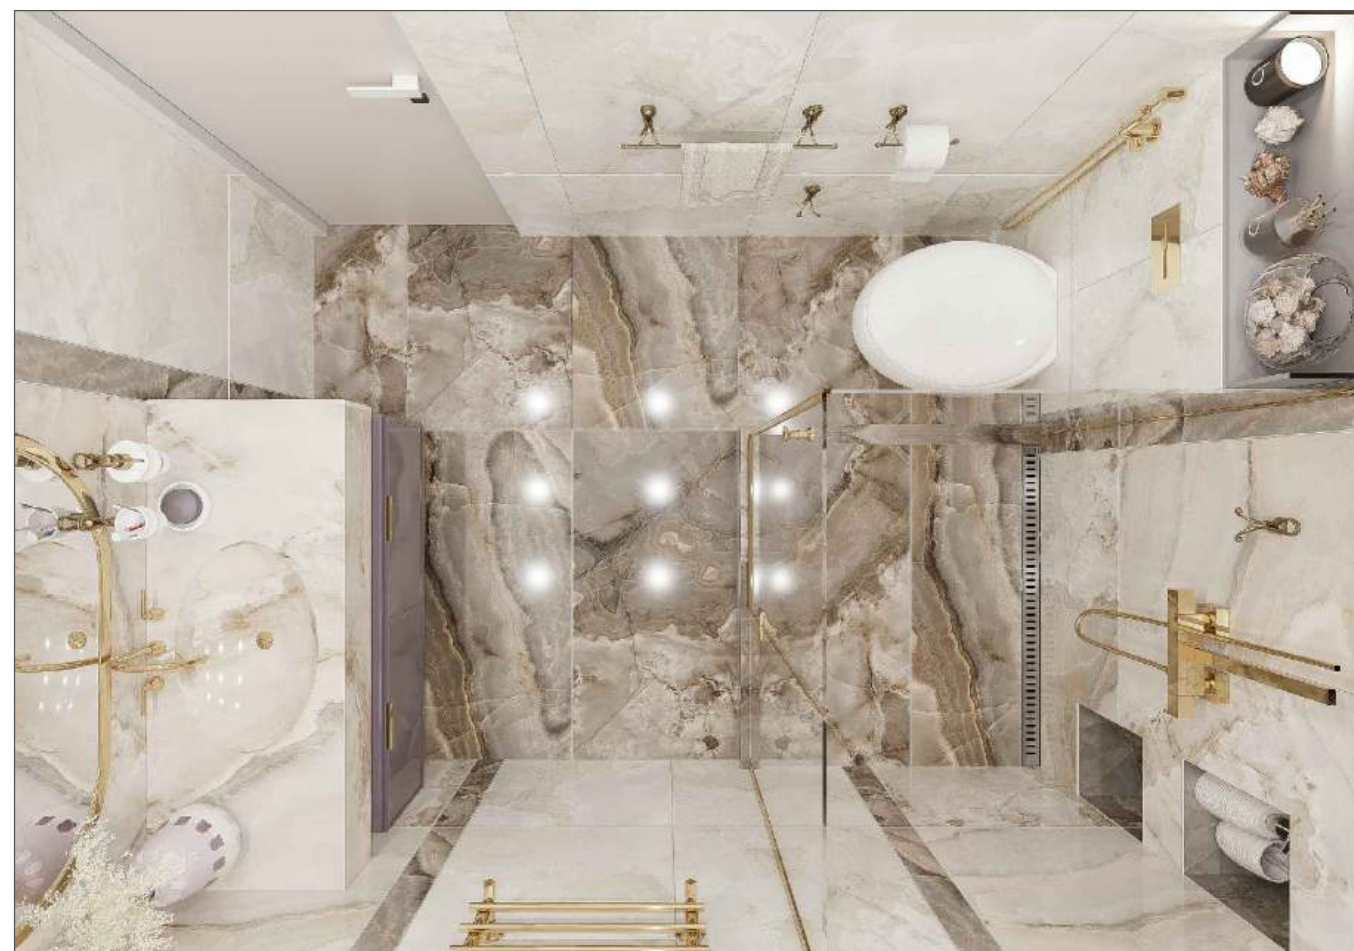

САМУЗЕЛ 2



